



EXISTING BLOCK PLAN

SCALE 1:200

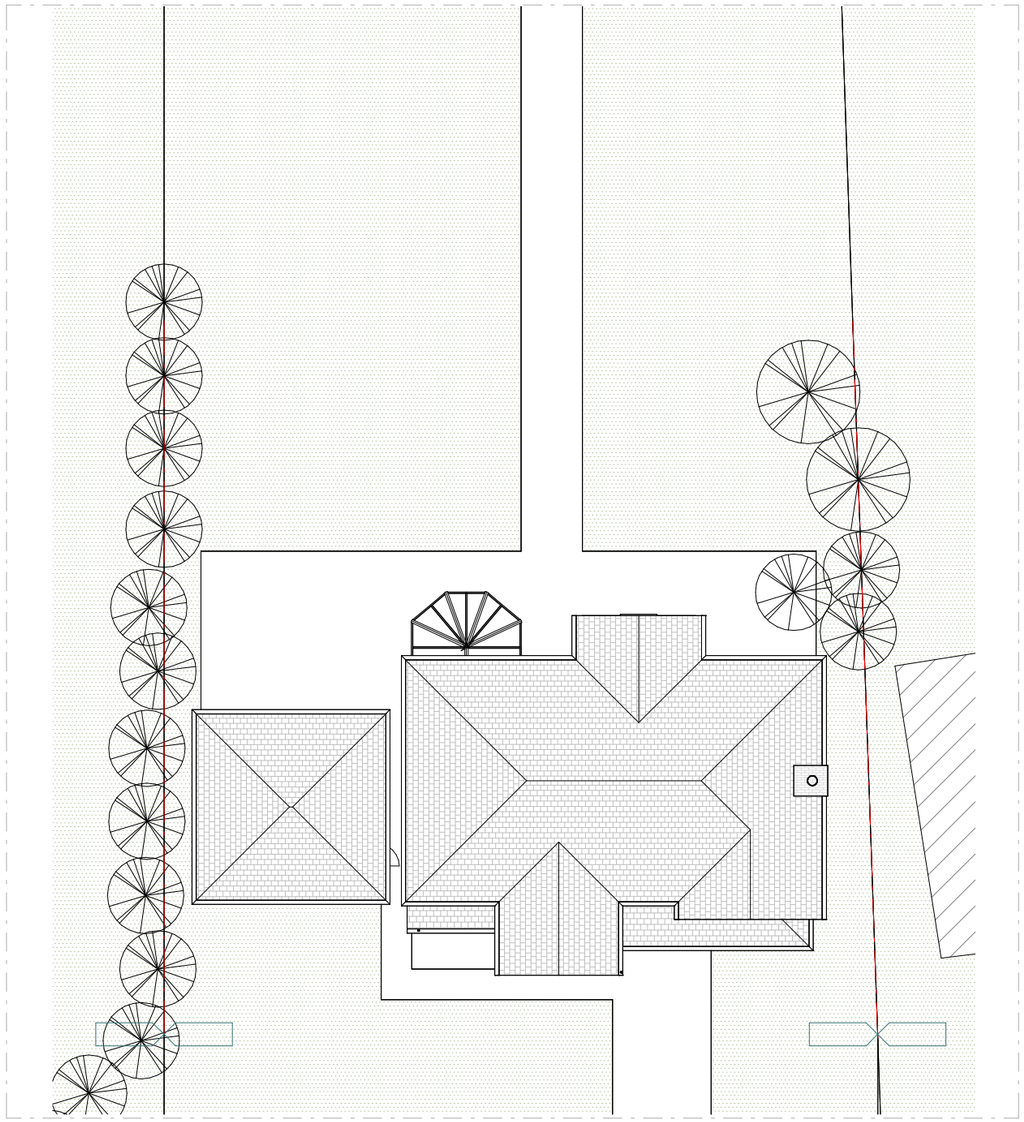

3D EXISTING

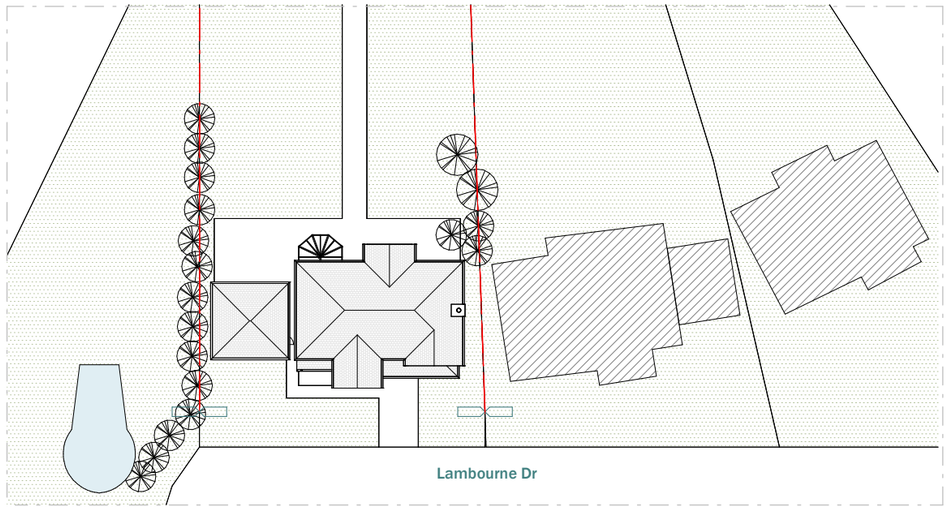

EXISTING SITE PLAN

SCALE 1:500

LEGEND:

- EXISTING
- PROPOSED
- BOUNDARY

Scale 1:500 @A3

10m 50m

Scale 1:1250 @A3

25m 125m

extension architecture


3 River Reach, Gartons Way,
Battersea
London SW11 3SX
Tel (0208) 288 8950 Fax (0871) 918 2798
www.extensionarchitecture.co.uk

This drawing is prepared solely for design and planning submission purposes. It is not intended or suitable for either building regulations or construction purposes and should not be used for such. All dimension shall be check and confirmed with site rep. and any discrepancies between the drawings and site shall be reported to PM. This drawing to be read in conjunction with engineers specification and details. For construction information please refer to all drawings and specification of works.

For any structural steelworks details please refer to structural engineer's drawings & calculations.

The copyright of the drawing and designs remains with Extension Architecture. All copies are only for information about the application, they may not be used for any other purpose without the express written permission of Extension Architecture.

CLIENT: Vik Barodia	NOTES			SCALE: As indicated	DATE: 16.02.2024
PROJECT: 1 Lambourne Drive, KT11 3LB	VERSION	DESCRIPTION	DATE	DRAWN: SF	VERSION
TITLE: Site & Block Plan				SHEET REF. NO: 1LB -PL-REVB -00	

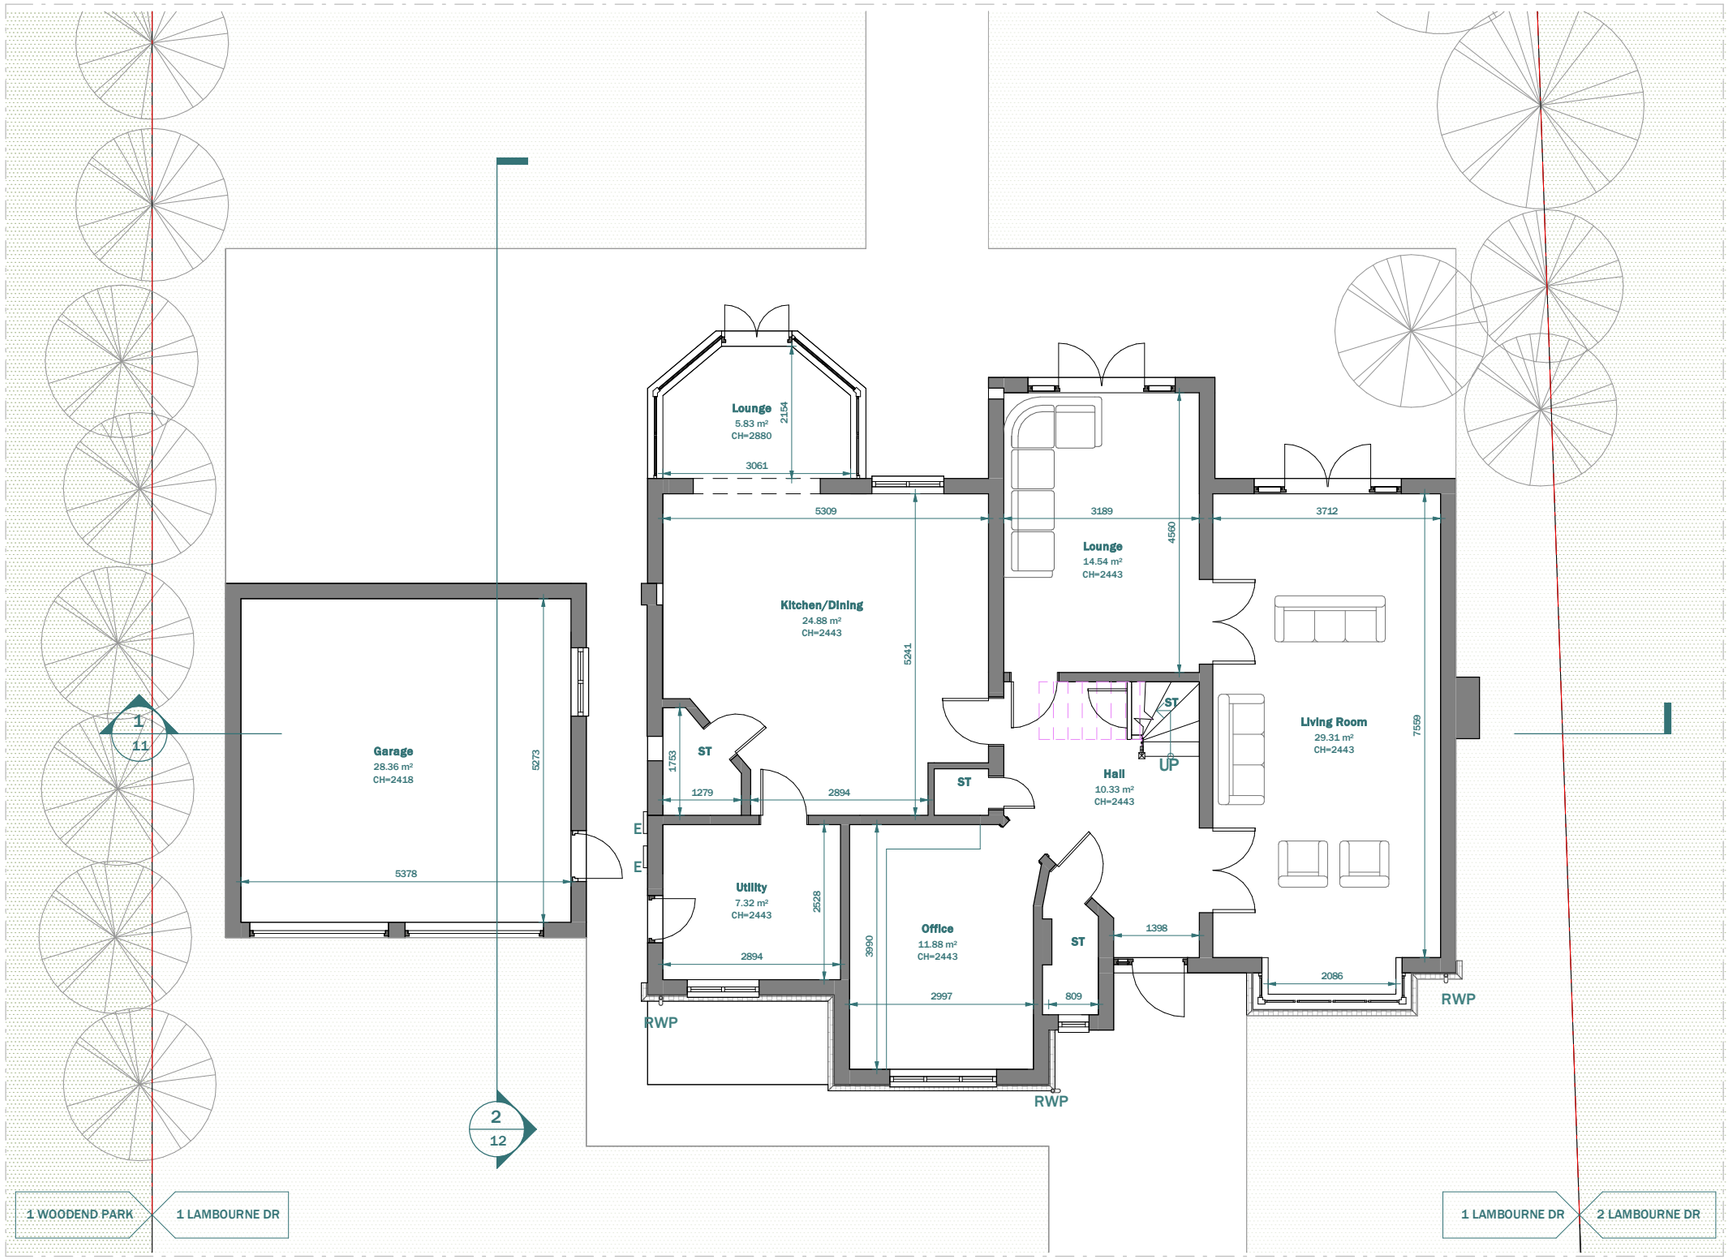

EXISTING GROUND FLOOR

LEGEND:

- EXISTING WALL
- PROPOSED WALL
- DEMOLISHED LINE
- INVISIBLE LINE

Scale 1:100 @A3 — 0 1 2 3 4 5m
Scale 1:50 @A3 — 0 0.5 1 1.5 2 2.5m
Scale 1:20 @A3 — 0 20 40 60 80 100m


extension architecture
3 River Reach, Gartons Way,
Battersea
London SW11 3SX
Tel (0208) 288 8950 Fax (0871) 918 2798
www.extensionarchitecture.co.uk

This drawing is prepared solely for design and planning submission purposes. It is not intended or suitable for either building regulations or construction purposes and should not be used for such. All dimension shall be check and confirmed with site rep. and any discrepancies between the drawings and site shall be reported to PM. This drawing to be read in conjunction with engineers specification and details. For construction information please refer to all drawings and specification of works.

For any structural steelworks details please refer to structural engineer's drawings & calculations.

The copyright of the drawing and designs remains with Extension Architecture. All copies are only for information about the application, they may not be used for any other purpose without the express written permission of Extension Architecture.

CLIENT: Vik Barodia	NOTES			SCALE: 1 : 100	DATE: 16.02.2024
PROJECT: 1 Lambourne Drive, KT11 3LB	VERSION	DESCRIPTION	DATE	DRAWN: SF	VERSION
TITLE: Existing Ground Floor				SHEET REF. NO: 1LB -PL-REVB -01	

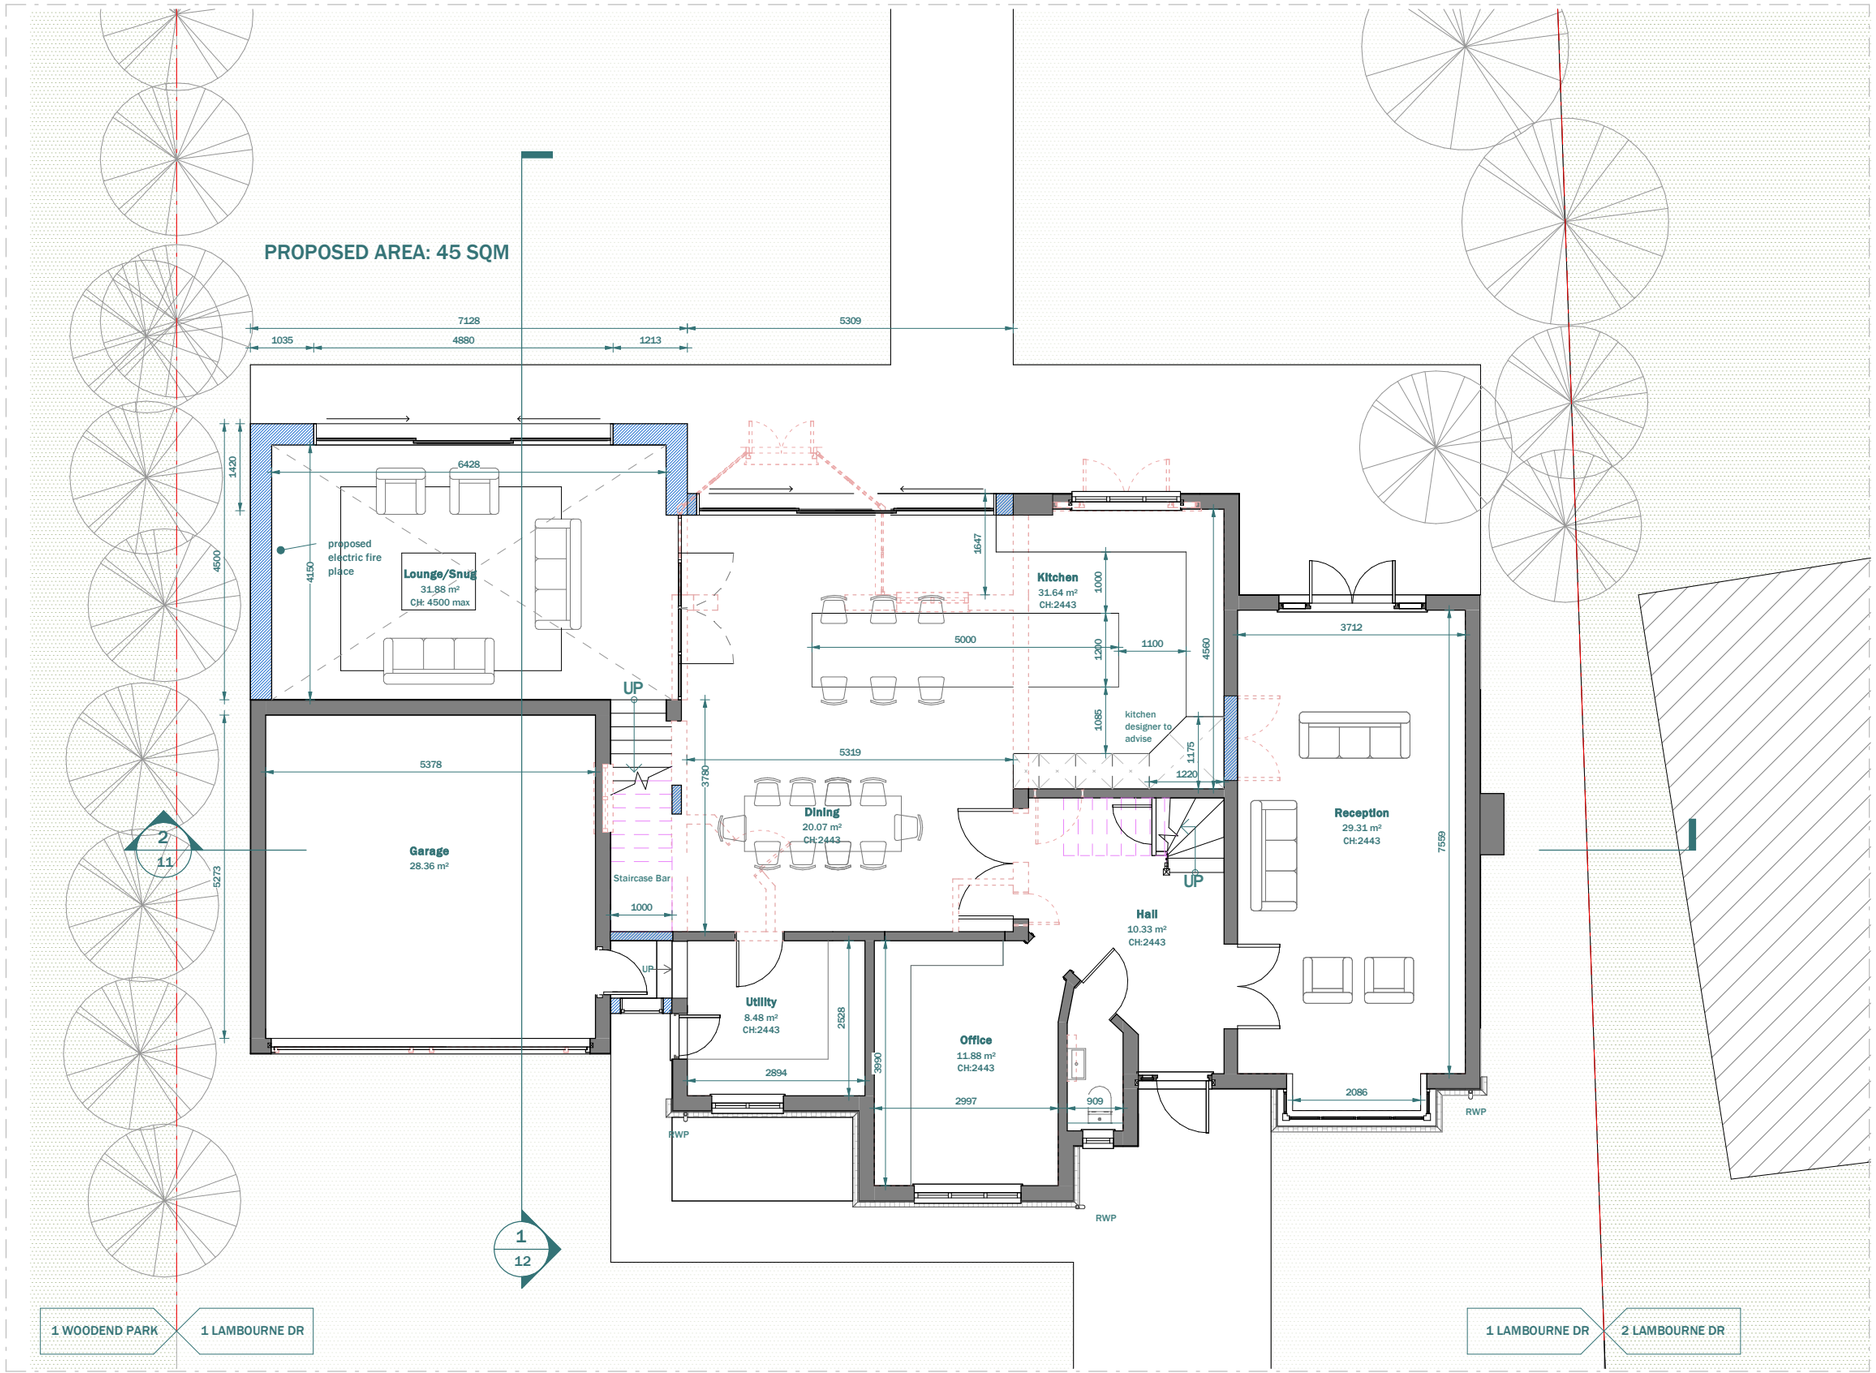

PROPOSED GROUND FLOOR

LEGEND:

- EXISTING WALL
- PROPOSED WALL
- DEMOLISHED LINE
- INVISIBLE LINE

Scale 1:100 @A3 — 0 1 2 3 4 5m

Scale 1:50 @A3 — 0 0.5 1 1.5 2 2.5m

Scale 1:20 @A3 — 0 20 40 60 80 100m


extension architecture
3 River Reach, Gartons Way,
Battersea
London SW11 3SX
Tel (0208) 288 8950 Fax (0871) 918 2798
www.extensionarchitecture.co.uk

This drawing is prepared solely for design and planning submission purposes. It is not intended or suitable for either building regulations or construction purposes and should not be used for such. All dimension shall be check and confirmed with site rep. and any discrepancies between the drawings and site shall be reported to PM. This drawing to be read in conjunction with engineers specification and details. For construction information please refer to all drawings and specification of works.

For any structural steelworks details please refer to structural engineer's drawings & calculations.

The copyright of the drawing and designs remains with Extension Architecture. All copies are only for information about the application, they may not be used for any other purpose without the express written permission of Extension Architecture.

CLIENT: Vik Barodia	NOTES			SCALE: 1 : 100	DATE: 16.02.2024
PROJECT: 1 Lambourne Drive, KT11 3LB	VERSION	DESCRIPTION	DATE	DRAWN: SF	VERSION
TITLE: Proposed Ground Floor				SHEET REF. NO: 1LB -PL-REVB -02	

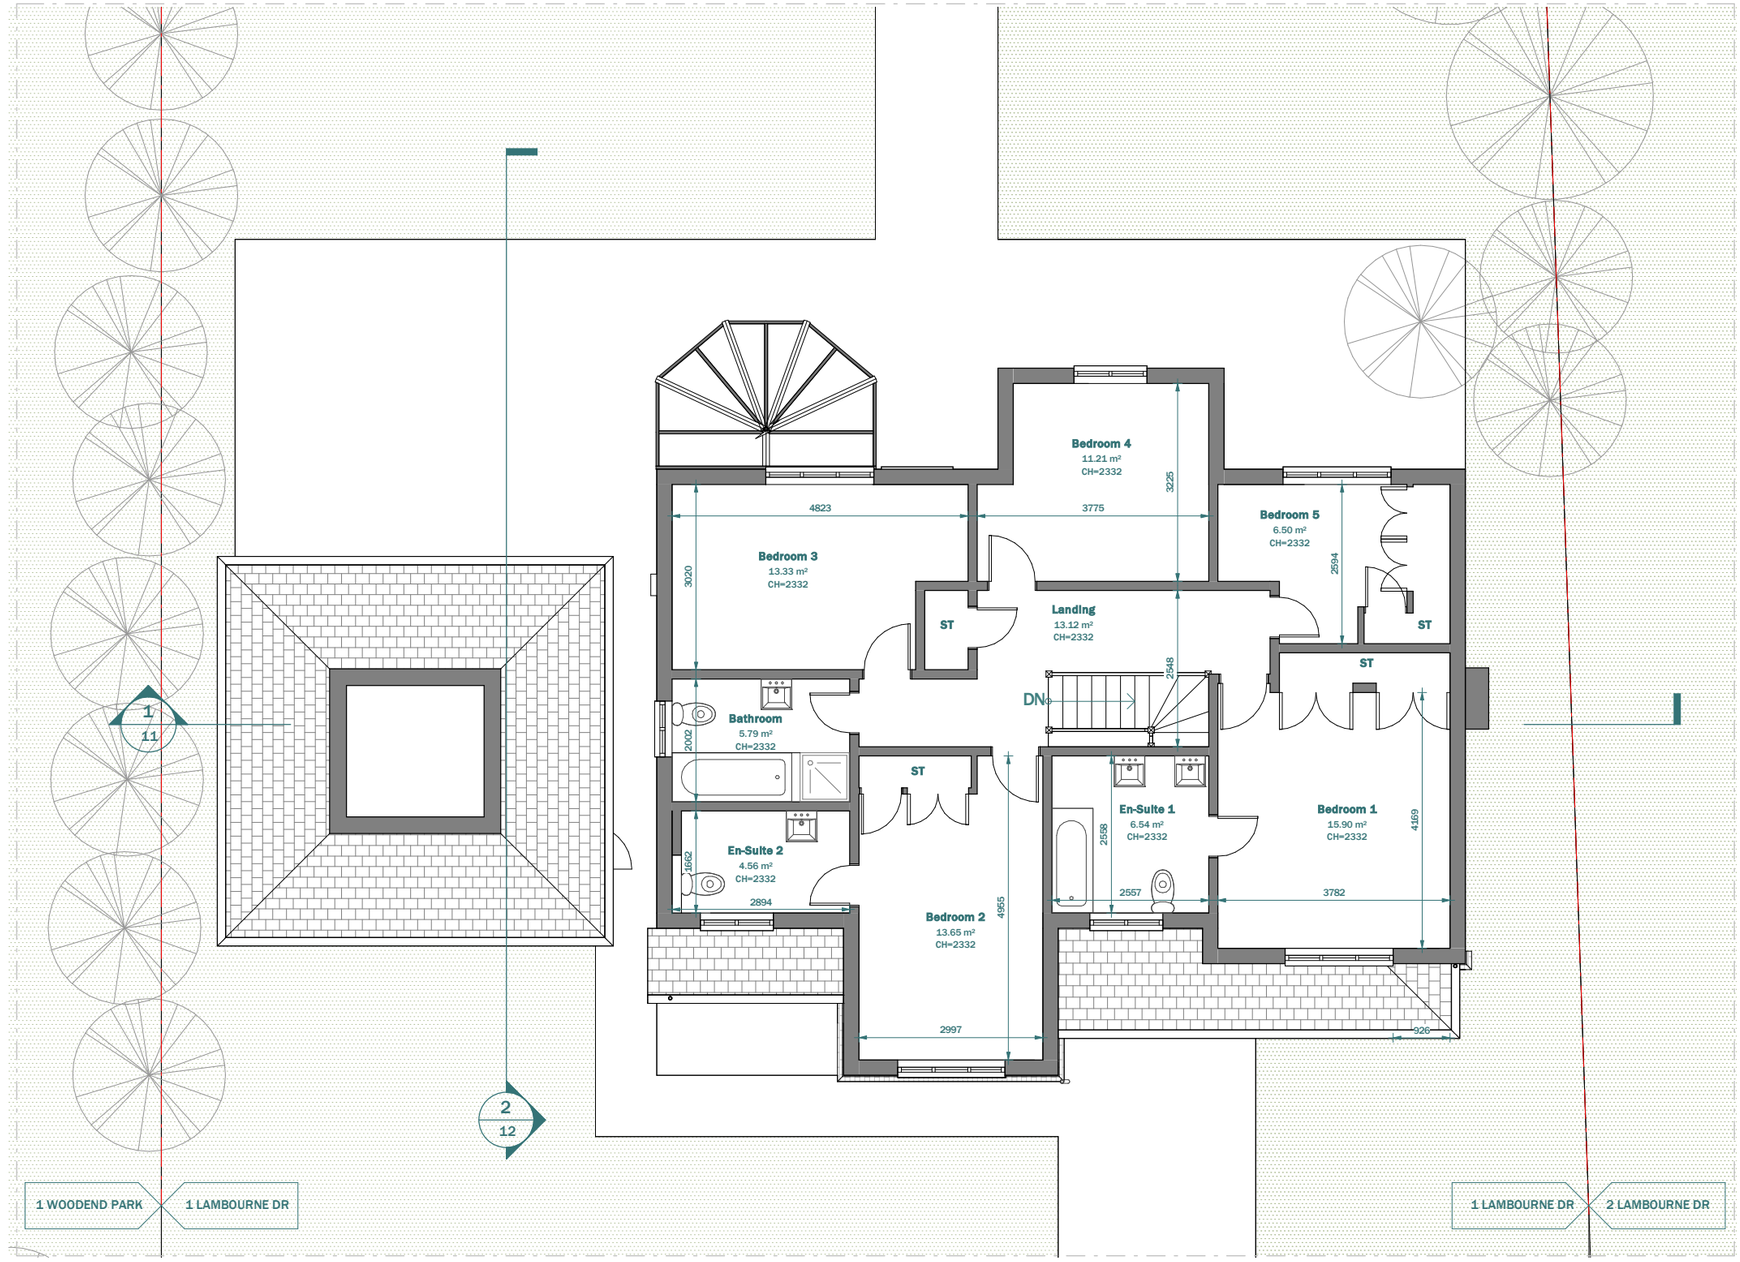

EXISTING FIRST FLOOR

N

LEGEND:

- EXISTING WALL
- PROPOSED WALL
- DEMOLISHED LINE
- INVISIBLE LINE

Scale 1:100 @A3 0 1 2 3 4 5m

Scale 1:50 @A3 0 0.5 1 1.5 2 2.5m

Scale 1:20 @A3 0 20 40 60 80 100m


extension architecture
3 River Reach, Gartons Way,
Battersea
London SW11 3SX
Tel (0208) 288 8950 Fax (0871) 918 2798
www.extensionarchitecture.co.uk

This drawing is prepared solely for design and planning submission purposes. It is not intended or suitable for either building regulations or construction purposes and should not be used for such. All dimension shall be check and confirmed with site rep. and any discrepancies between the drawings and site shall be reported to PM. This drawing to be read in conjunction with engineers specification and details. For construction information please refer to all drawings and specification of works.

For any structural steelworks details please refer to structural engineer's drawings & calculations.

The copyright of the drawing and designs remains with Extension Architecture. All copies are only for information about the application, they may not be used for any other purpose without the express written permission of Extension Architecture.

CLIENT: Vik Barodia	NOTES			SCALE: 1 : 100	DATE: 16.02.2024
PROJECT: 1 Lambourne Drive, KT11 3LB	VERSION	DESCRIPTION	DATE	DRAWN: SF	VERSION
TITLE: Existing First Floor				SHEET REF. NO: 1LB -PL-REVB -03	

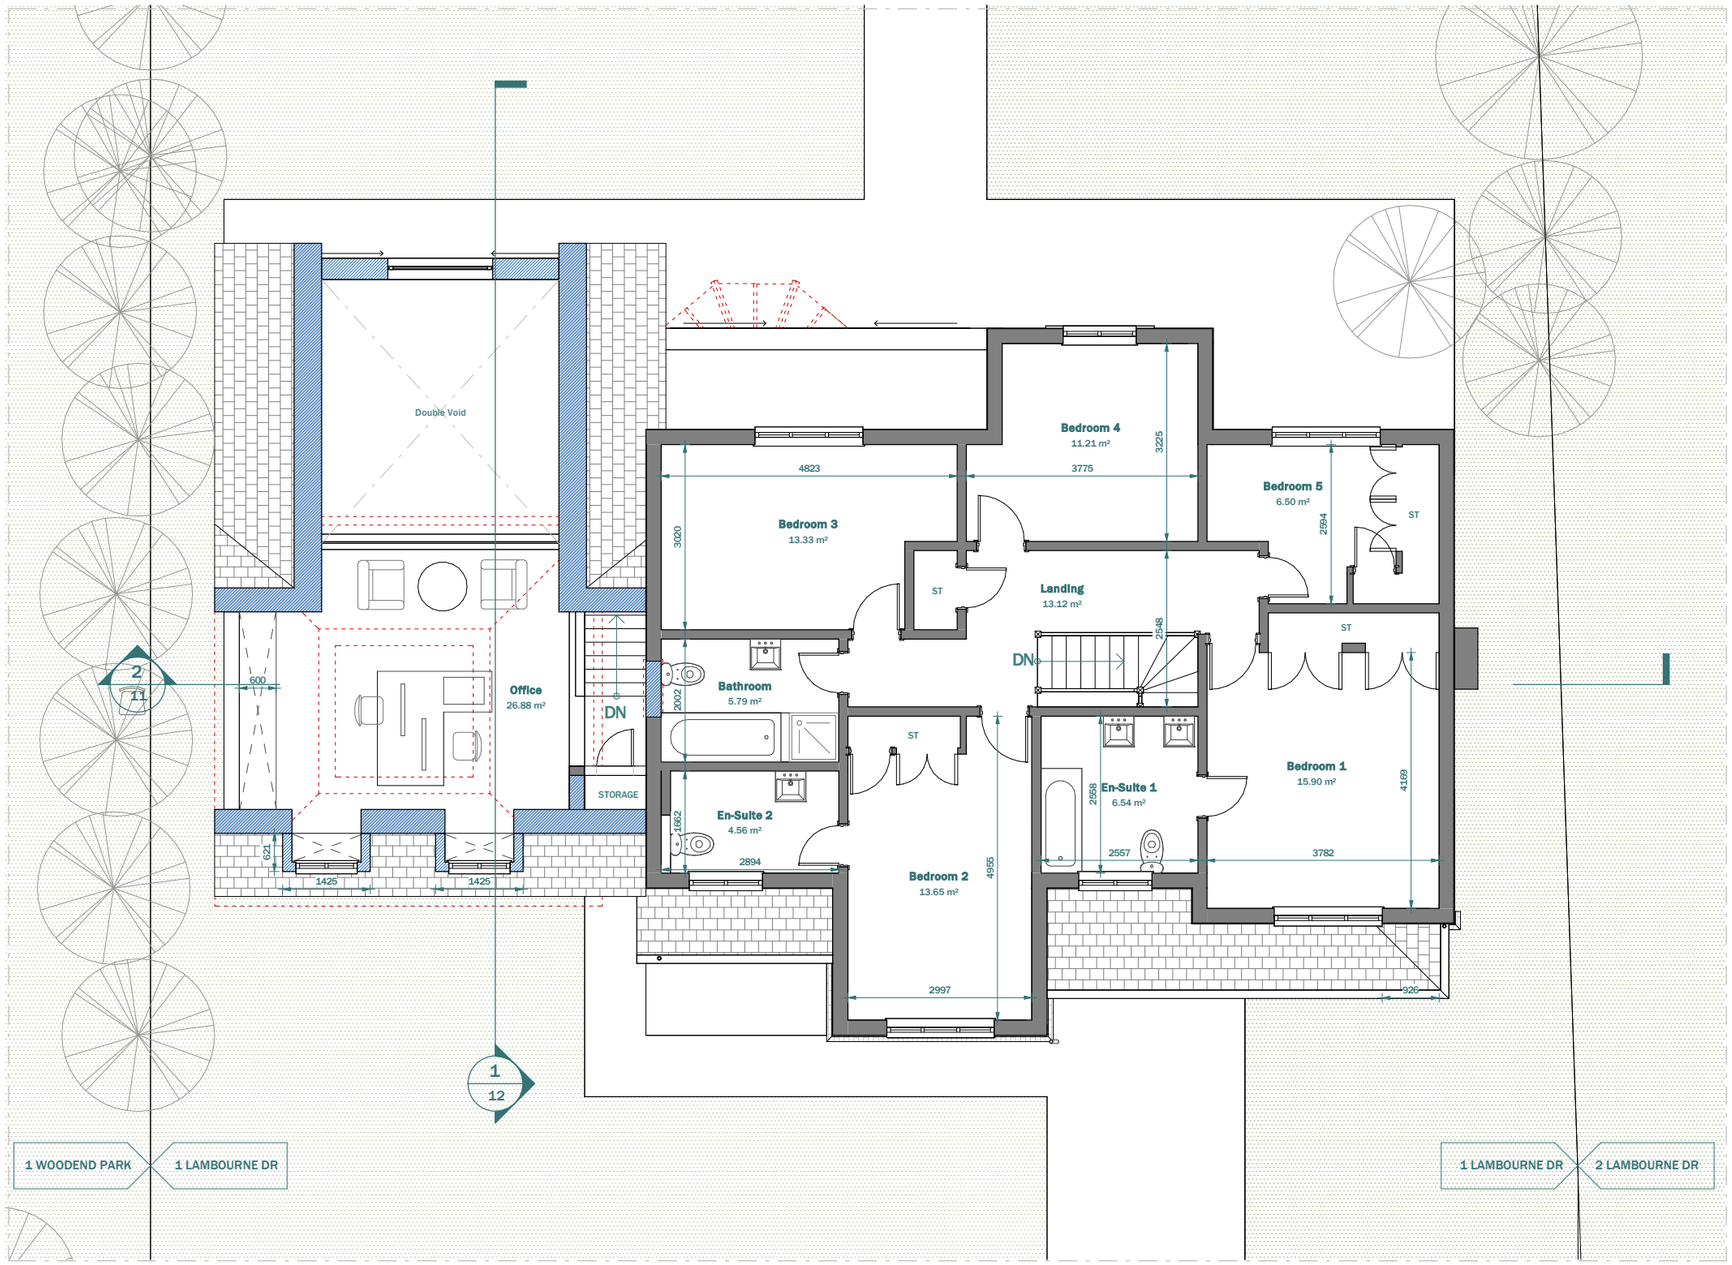

EXISTING FIRST FLOOR

N

LEGEND:

- EXISTING WALL
- PROPOSED WALL
- DEMOLISHED LINE
- INVISIBLE LINE

Scale 1:100 @A3 0 1 2 3 4 5m

Scale 1:50 @A3 0 0.5 1 1.5 2 2.5m

Scale 1:20 @A3 0 20 40 60 80 100m


extension architecture
3 River Reach, Gartons Way,
Battersea
London SW11 3SX
Tel (0208) 288 8950 Fax (0871) 918 2798
www.extensionarchitecture.co.uk

This drawing is prepared solely for design and planning submission purposes. It is not intended or suitable for either building regulations or construction purposes and should not be used for such. All dimension shall be check and confirmed with site rep. and any discrepancies between the drawings and site shall be reported to PM. This drawing to be read in conjunction with engineers specification and details. For construction information please refer to all drawings and specification of works.

For any structural steelworks details please refer to structural engineer's drawings & calculations.

The copyright of the drawing and designs remains with Extension Architecture. All copies are only for information about the application, they may not be used for any other purpose without the express written permission of Extension Architecture.

CLIENT: Vik Barodia	NOTES			SCALE: 1 : 100	DATE: 16.02.2024
PROJECT: 1 Lambourne Drive, KT11 3LB	VERSION	DESCRIPTION	DATE	DRAWN: SF	VERSION
TITLE: Proposed First Floor				SHEET REF. NO: 1LB -PL-REVB -04	

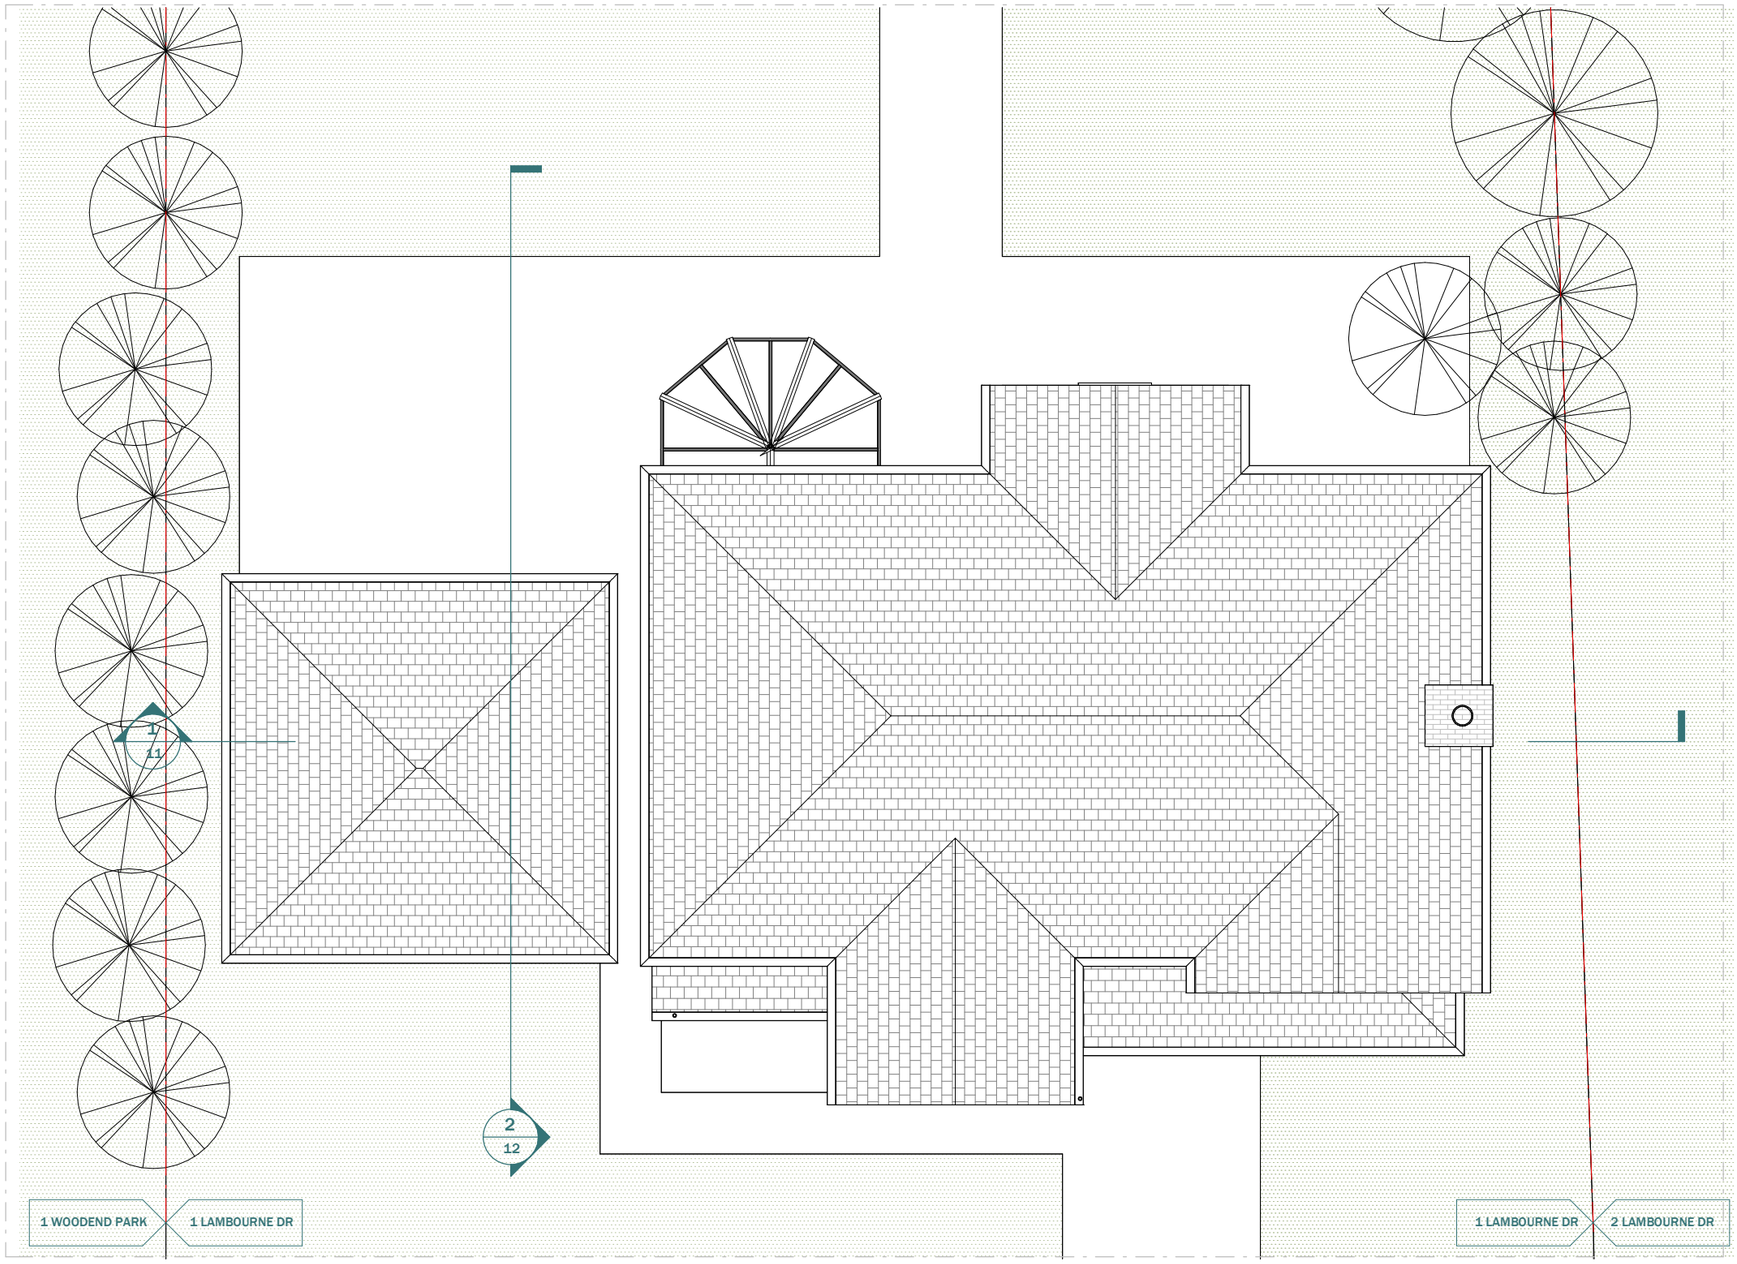

EXISTING ROOF FLOOR

LEGEND:

- EXISTING WALL
- PROPOSED WALL
- DEMOLISHED LINE
- INVISIBLE LINE

Scale 1:100 @A3 — 0 1 2 3 4 5m

Scale 1:50 @A3 — 0 0.5 1 1.5 2 2.5m

Scale 1:20 @A3 — 0 20 40 60 80 100m


extension architecture
3 River Reach, Gartons Way,
Battersea
London SW11 3SX
Tel (0208) 288 8950 Fax (0871) 918 2798
www.extensionarchitecture.co.uk

This drawing is prepared solely for design and planning submission purposes. It is not intended or suitable for either building regulations or construction purposes and should not be used for such. All dimension shall be check and confirmed with site rep. and any discrepancies between the drawings and site shall be reported to PM. This drawing to be read in conjunction with engineers specification and details. For construction information please refer to all drawings and specification of works.

For any structural steelworks details please refer to structural engineer's drawings & calculations.

The copyright of the drawing and designs remains with Extension Architecture. All copies are only for information about the application, they may not be used for any other purpose without the express written permission of Extension Architecture.

CLIENT: Vik Barodia	NOTES			SCALE: 1 : 100	DATE: 16.02.2024
PROJECT: 1 Lambourne Drive, KT11 3LB	VERSION	DESCRIPTION	DATE	DRAWN: SF	VERSION
TITLE: Existing Roof Plan				SHEET REF. NO: 1LB -PL-REVB -05	

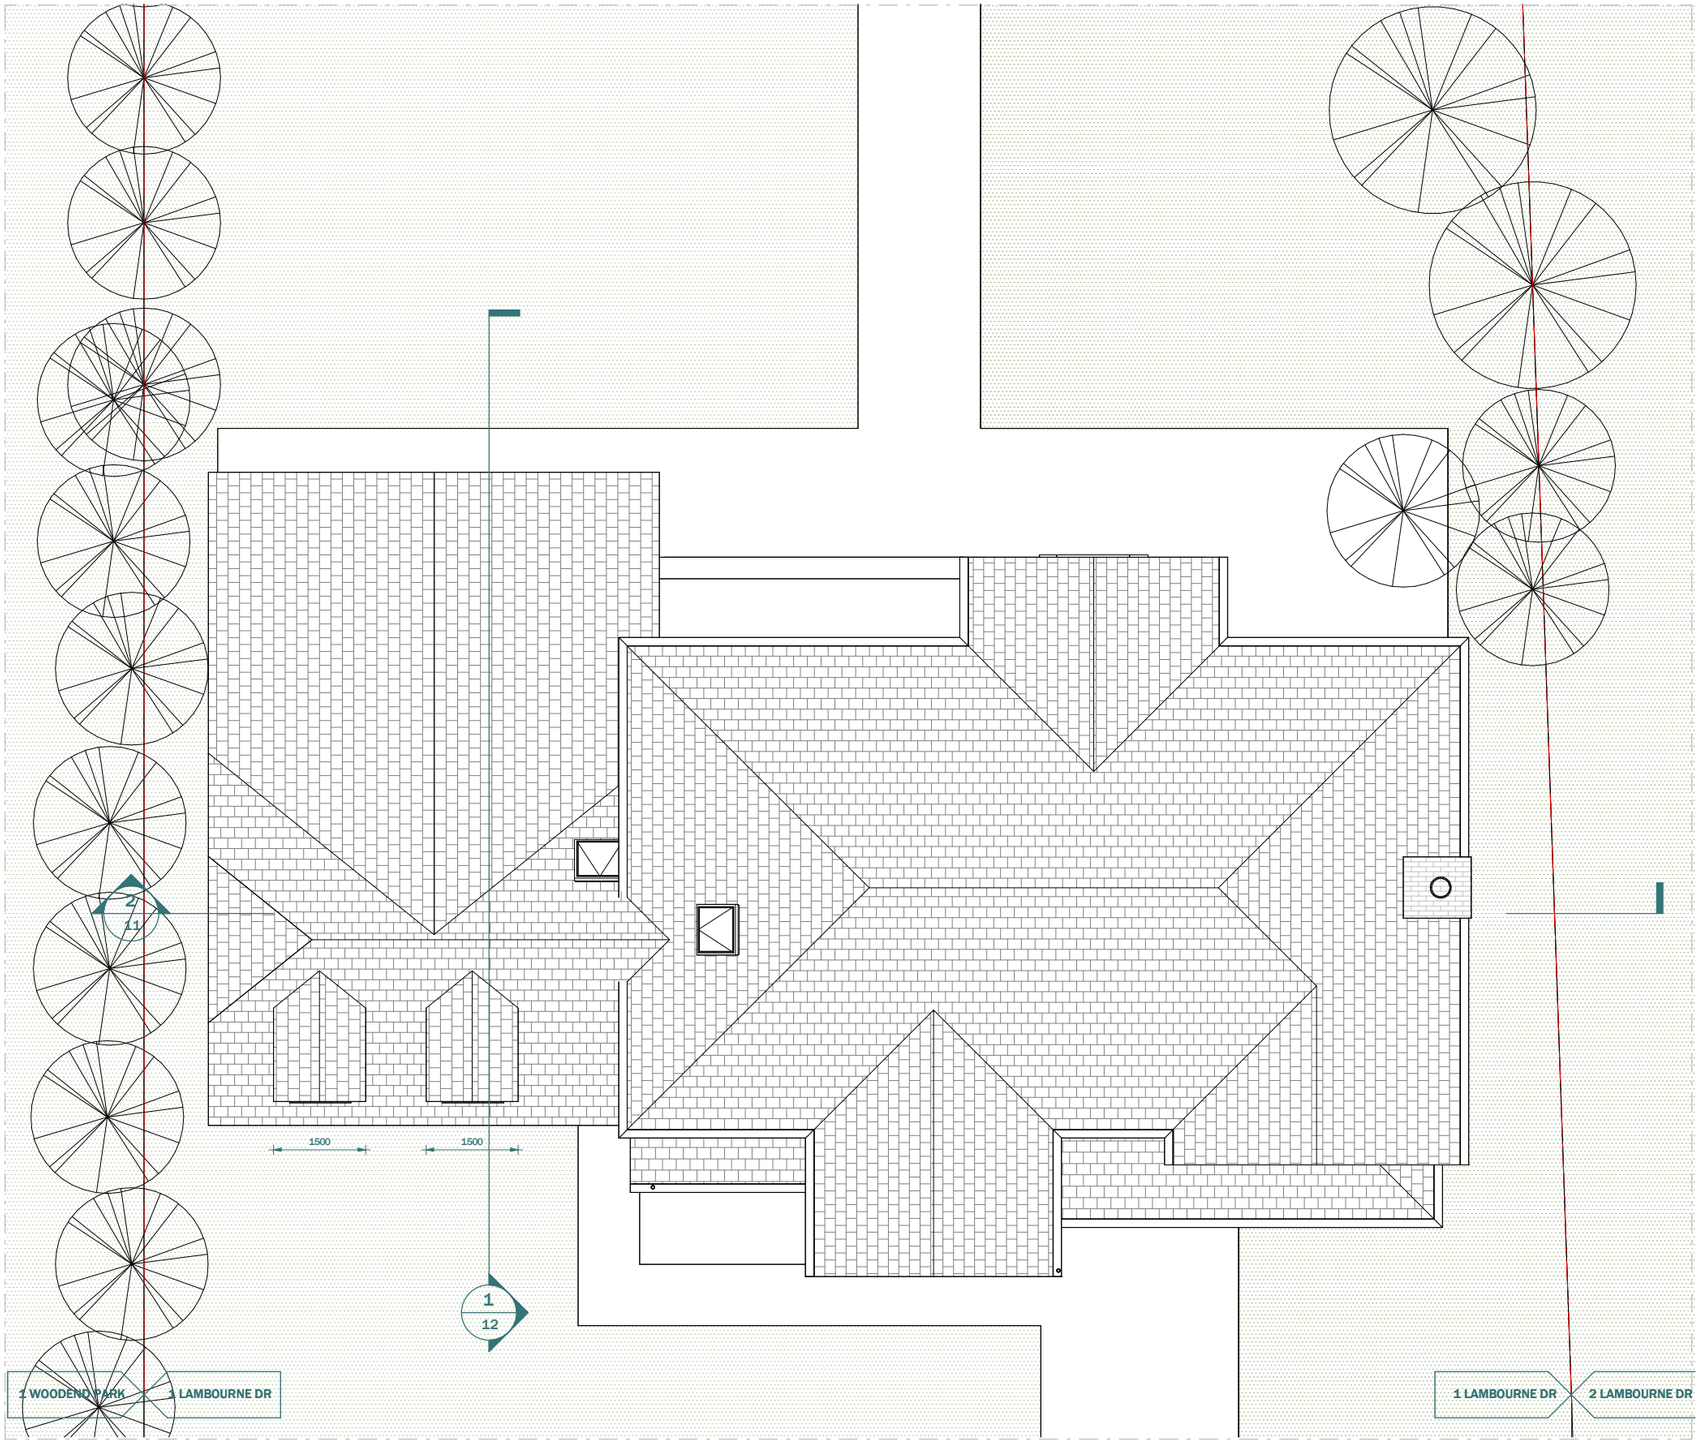

LEGEND:

- EXISTING WALL
- PROPOSED WALL
- DEMOLISHED LINE
- INVISIBLE LINE

Scale 1:100 @A3 — 0 1 2 3 4 5m

Scale 1:50 @A3 — 0 0.5 1 1.5 2 2.5m

Scale 1:20 @A3 — 0 20 40 60 80 100m

extension architecture

3 River Reach, Gartons Way,
Battersea
London SW11 3SX
Tel (0208) 288 8950 Fax (0871) 918 2798
www.extensionarchitecture.co.uk

This drawing is prepared solely for design and planning submission purposes. It is not intended or suitable for either building regulations or construction purposes and should not be used for such. All dimension shall be check and confirmed with site rep. and any discrepancies between the drawings and site shall be reported to PM. This drawing to be read in conjunction with engineers specification and details. For construction information please refer to all drawings and specification of works.

For any structural steelworks details please refer to structural engineer's drawings & calculations.

The copyright of the drawing and designs remains with Extension Architecture. All copies are only for information about the application, they may not be used for any other purpose without the express written permission of Extension Architecture.

CLIENT: Vik Barodia	NOTES			SCALE: 1 : 100	DATE: 16.02.2024
PROJECT: 1 Lambourne Drive, KT11 3LB	VERSION	DESCRIPTION	DATE	DRAWN: SF	VERSION
TITLE: Proposed Roof Plan				SHEET REF. NO: 1LB -PL-REVB -06	



EXISTING FRONT ELEVATION



PROPOSED FRONT ELEVATION

Scale 1:100 @A3 0 1 2 3 4 5m
Scale 1:50 @A3 0 0.5 1 1.5 2 2.5m
Scale 1:20 @A3 0 20 40 60 80 100m

extension architecture
3 River Reach, Gartons Way,
Battersea
London SW11 3SX
Tel (0208) 288 8950 Fax (0871) 918 2798
www.extensionarchitecture.co.uk

This drawing is prepared solely for design and planning submission purposes. It is not intended or suitable for either building regulations or construction purposes and should not be used for such. All dimension shall be check and confirmed with site rep. and any discrepancies between the drawings and site shall be reported to PM. This drawing to be read in conjunction with engineers specification and details. For construction information please refer to all drawings and specification of works.

For any structural steelworks details please refer to structural engineer's drawings & calculations.

The copyright of the drawing and designs remains with Extension Architecture. All copies are only for information about the application, they may not be used for any other purpose without the express written permission of Extension Architecture.

CLIENT: Vik Barodia

PROJECT: 1 Lambourne Drive, KT11 3LB

TITLE: Existing & Proposed Front Elevation

NOTES

VERSION	DESCRIPTION	DATE

SCALE: 1 : 100

DATE: 16.02.2024

DRAWN: SF

VERSION:

SHEET REF. NO: 1LB -PL-REVB -07



EXISTING REAR ELEVATION



PROPOSED REAR ELEVATION

Scale 1:100 @A3 0 1 2 3 4 5m

Scale 1:50 @A3 0 0.5 1 1.5 2 2.5m

Scale 1:20 @A3 0 20 40 60 80 100m

extension architecture

3 River Reach, Gartons Way,
Battersea
London SW11 3SX
Tel (0208) 288 8950 Fax (0871) 918 2798
www.extensionarchitecture.co.uk

This drawing is prepared solely for design and planning submission purposes. It is not intended or suitable for either building regulations or construction purposes and should not be used for such. All dimension shall be check and confirmed with site rep. and any discrepancies between the drawings and site shall be reported to PM. This drawing to be read in conjunction with engineers specification and details. For construction information please refer to all drawings and specification of works.


For any structural steelworks details please refer to structural engineer's drawings & calculations.

The copyright of the drawing and designs remains with Extension Architecture. All copies are only for information about the application, they may not be used for any other purpose without the express written permission of Extension Architecture.

CLIENT: Vik Barodia	NOTES			SCALE: 1 : 100	DATE: 16.02.2024
PROJECT: 1 Lambourne Drive, KT11 3LB	VERSION	DESCRIPTION	DATE	DRAWN: SF	VERSION
TITLE: Existing & Proposed Rear Elevation				SHEET REF. NO: 1LB -PL-REVB -08	



EXISTING LEFT ELEVATION

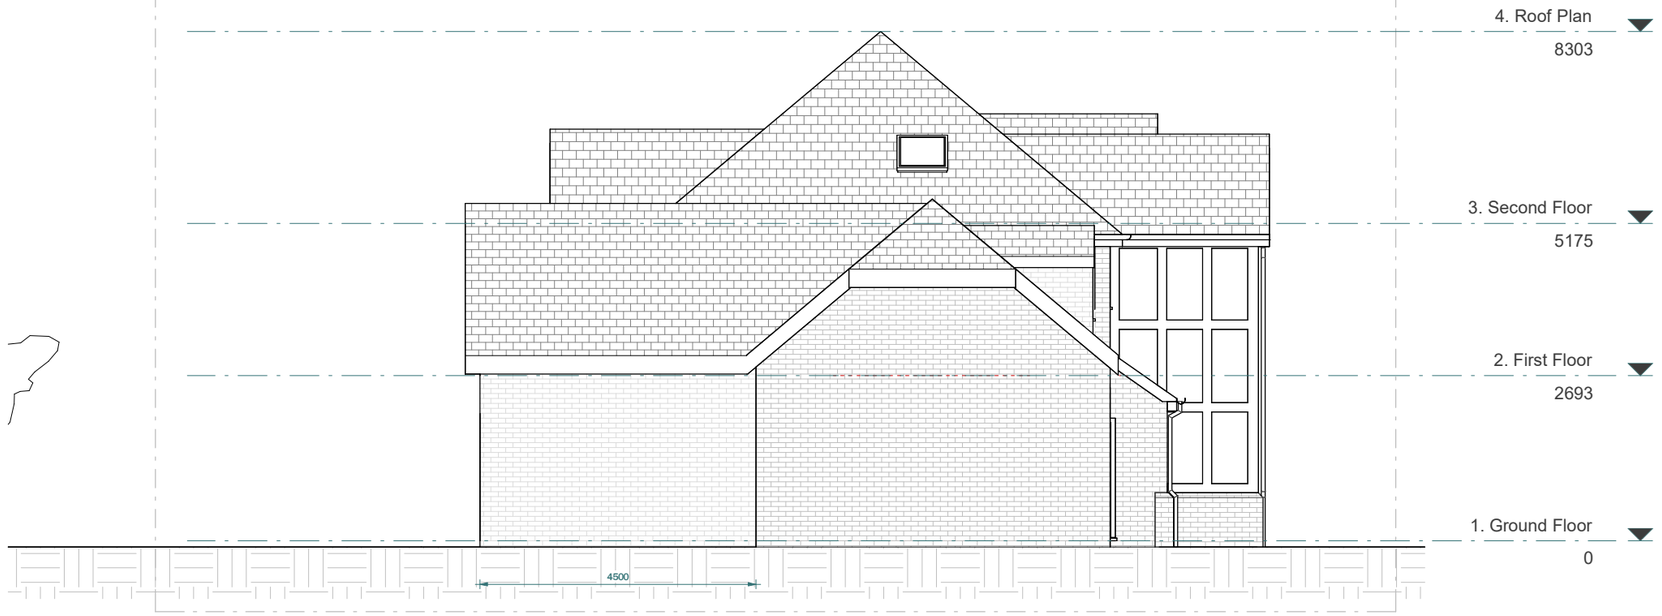

PROPOSED LEFT ELEVATION

Scale 1:100 @A3 0 1 2 3 4 5m

Scale 1:50 @A3 0 0.5 1 1.5 2 2.5m

Scale 1:20 @A3 0 20 40 60 80 100m

extension architecture


3 River Reach, Gartons Way,
Battersea
London SW11 3SX
Tel (0208) 288 8950 Fax (0871) 918 2798
www.extensionarchitecture.co.uk

This drawing is prepared solely for design and planning submission purposes. It is not intended or suitable for either building regulations or construction purposes and should not be used for such. All dimension shall be check and confirmed with site rep. and any discrepancies between the drawings and site shall be reported to PM. This drawing to be read in conjunction with engineers specification and details. For construction information please refer to all drawings and specification of works.


For any structural steelworks details please refer to structural engineer's drawings & calculations.

The copyright of the drawing and designs remains with Extension Architecture. All copies are only for information about the application, they may not be used for any other purpose without the express written permission of Extension Architecture.

CLIENT: Vik Barodia	NOTES			SCALE: 1 : 100	DATE: 16.02.2024
PROJECT: 1 Lambourne Drive, KT11 3LB	VERSION	DESCRIPTION	DATE	DRAWN: SF	VERSION
TITLE: Existing & Proposed Left Elevation				SHEET REF. NO: 1LB -PL-REVB -09	

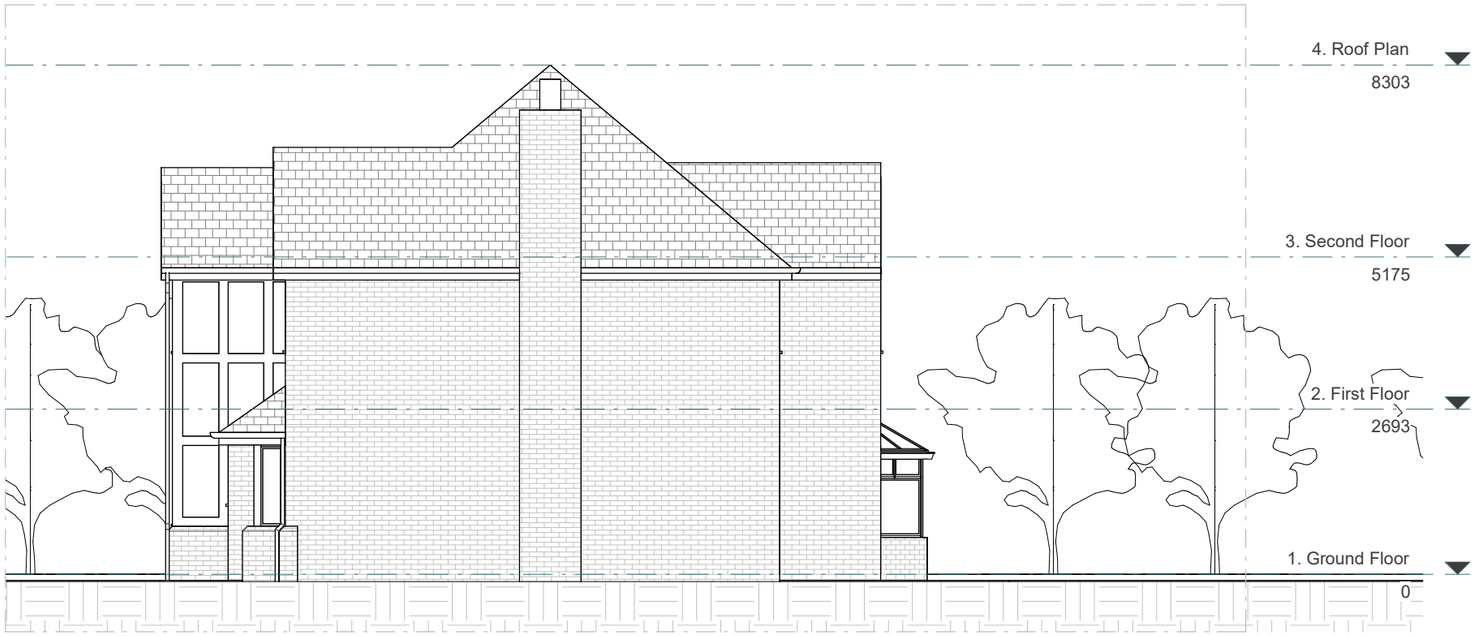

EXISTING RIGHT ELEVATION

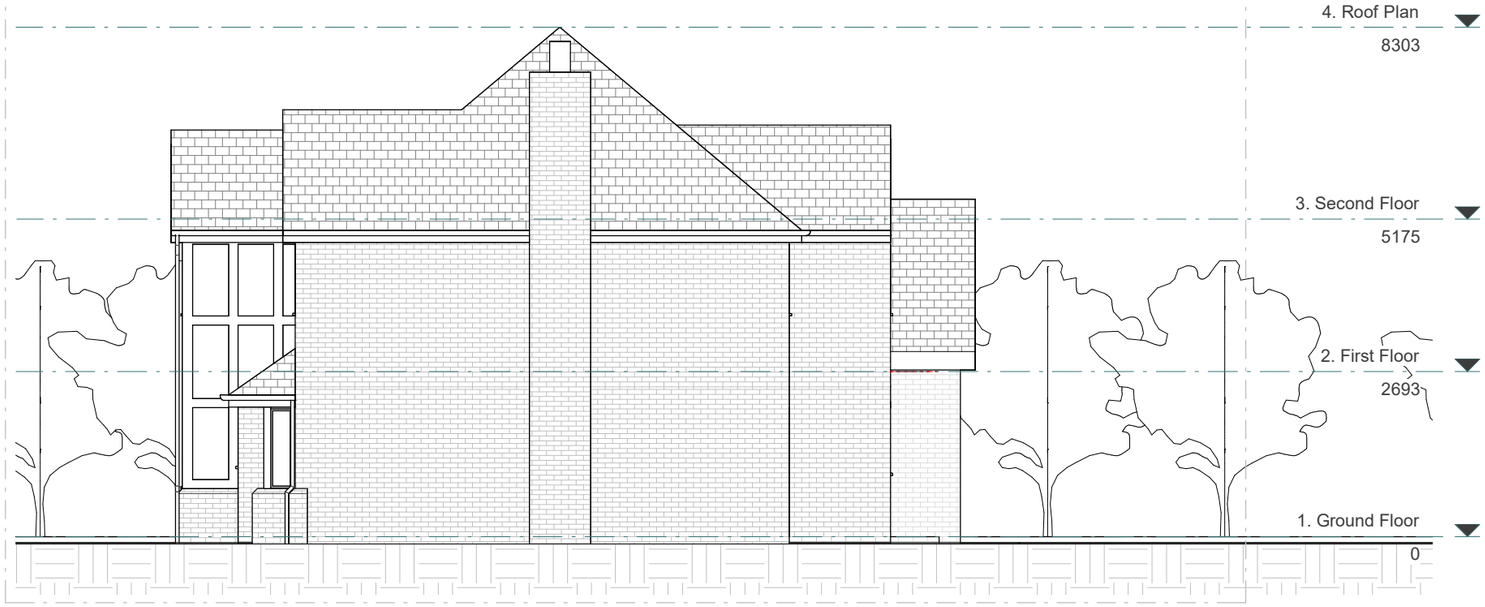

PROPOSED RIGHT ELEVATION

Scale 1:100 @A3 0 1 2 3 4 5m

Scale 1:50 @A3 0 0.5 1 1.5 2 2.5m

Scale 1:20 @A3 0 20 40 60 80 100m

extension architecture


3 River Reach, Gartons Way,
Battersea
London SW11 3SX
Tel (0208) 288 8950 Fax (0871) 918 2798
www.extensionarchitecture.co.uk

This drawing is prepared solely for design and planning submission purposes. It is not intended or suitable for either building regulations or construction purposes and should not be used for such. All dimension shall be check and confirmed with site rep. and any discrepancies between the drawings and site shall be reported to PM. This drawing to be read in conjunction with engineers specification and details. For construction information please refer to all drawings and specification of works.


For any structural steelworks details please refer to structural engineer's drawings & calculations.

The copyright of the drawing and designs remains with Extension Architecture. All copies are only for information about the application, they may not be used for any other purpose without the express written permission of Extension Architecture.

CLIENT: Vik Barodia	NOTES			SCALE: 1 : 100	DATE: 16.02.2024
PROJECT: 1 Lambourne Drive, KT11 3LB	VERSION	DESCRIPTION	DATE	DRAWN: SF	VERSION
TITLE: Existing & Proposed Right Elevation				SHEET REF. NO: 1LB -PL-REVB -10	

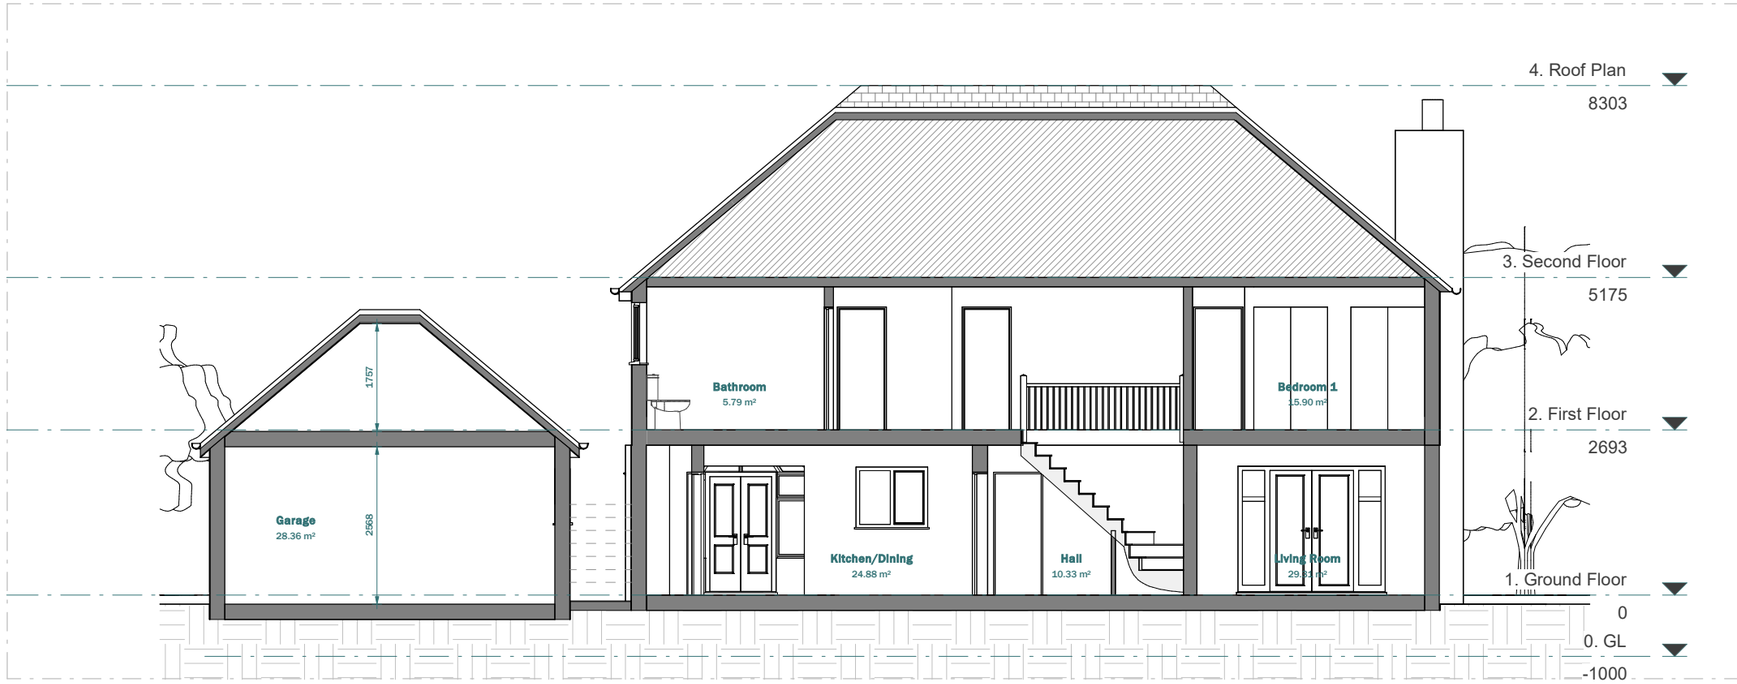

EXISTING SECTION A-A

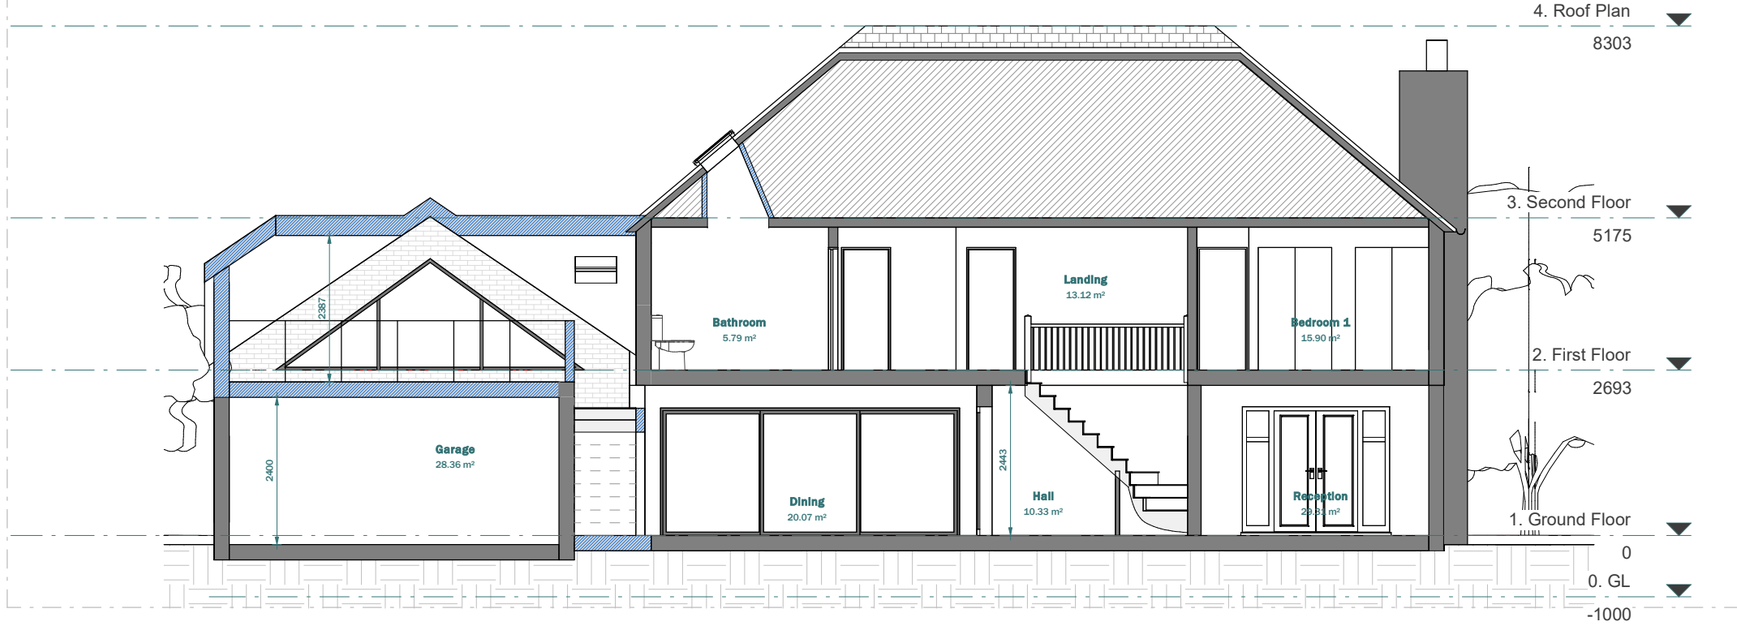

PROPOSED SECTION A-A

Scale 1:100 @A3 0 1 2 3 4 5m

Scale 1:50 @A3 0 0.5 1 1.5 2 2.5m

Scale 1:20 @A3 0 20 40 60 80 100m

extension architecture

3 River Reach, Gartons Way,
Battersea
London SW11 3SX
Tel (0208) 288 8950 Fax (0871) 918 2798
www.extensionarchitecture.co.uk

This drawing is prepared solely for design and planning submission purposes. It is not intended or suitable for either building regulations or construction purposes and should not be used for such. All dimension shall be check and confirmed with site rep. and any discrepancies between the drawings and site shall be reported to PM. This drawing to be read in conjunction with engineers specification and details. For construction information please refer to all drawings and specification of works.

For any structural steelworks details please refer to structural engineer's drawings & calculations.

The copyright of the drawing and designs remains with Extension Architecture. All copies are only for information about the application, they may not be used for any other purpose without the express written permission of Extension Architecture.

CLIENT: Vik Barodia	NOTES			SCALE: 1 : 100	DATE: 16.02.2024
PROJECT: 1 Lambourne Drive, KT11 3LB	VERSION	DESCRIPTION	DATE	DRAWN: SF	VERSION
TITLE: Existing & Proposed Section-AA				SHEET REF. NO: 1LB -PL-REVB -11	



EXISTING SECTION A-A



PROPOSED SECTION A-A

Scale 1:100 @A3 0 1 2 3 4 5m
Scale 1:50 @A3 0 0.5 1 1.5 2 2.5m
Scale 1:20 @A3 0 20 40 60 80 100m


extension architecture
3 River Reach, Gartons Way,
Battersea
London SW11 3SX
Tel (0208) 288 8950 Fax (0871) 918 2798
www.extensionarchitecture.co.uk

This drawing is prepared solely for design and planning submission purposes. It is not intended or suitable for either building regulations or construction purposes and should not be used for such. All dimension shall be check and confirmed with site rep. and any discrepancies between the drawings and site shall be reported to PM. This drawing to be read in conjunction with engineers specification and details. For construction information please refer to all drawings and specification of works.

For any structural steelworks details please refer to structural engineer's drawings & calculations.

The copyright of the drawing and designs remains with Extension Architecture. All copies are only for information about the application, they may not be used for any other purpose without the express written permission of Extension Architecture.

CLIENT: Vik Barodia	NOTES			SCALE: 1 : 100	DATE: 16.02.2024
PROJECT: 1 Lambourne Drive, KT11 3LB	VERSION	DESCRIPTION	DATE	DRAWN: SF	VERSION
TITLE: Existng and Proposed Section B-B				SHEET REF. NO: 1LB -PL-REVB -12	

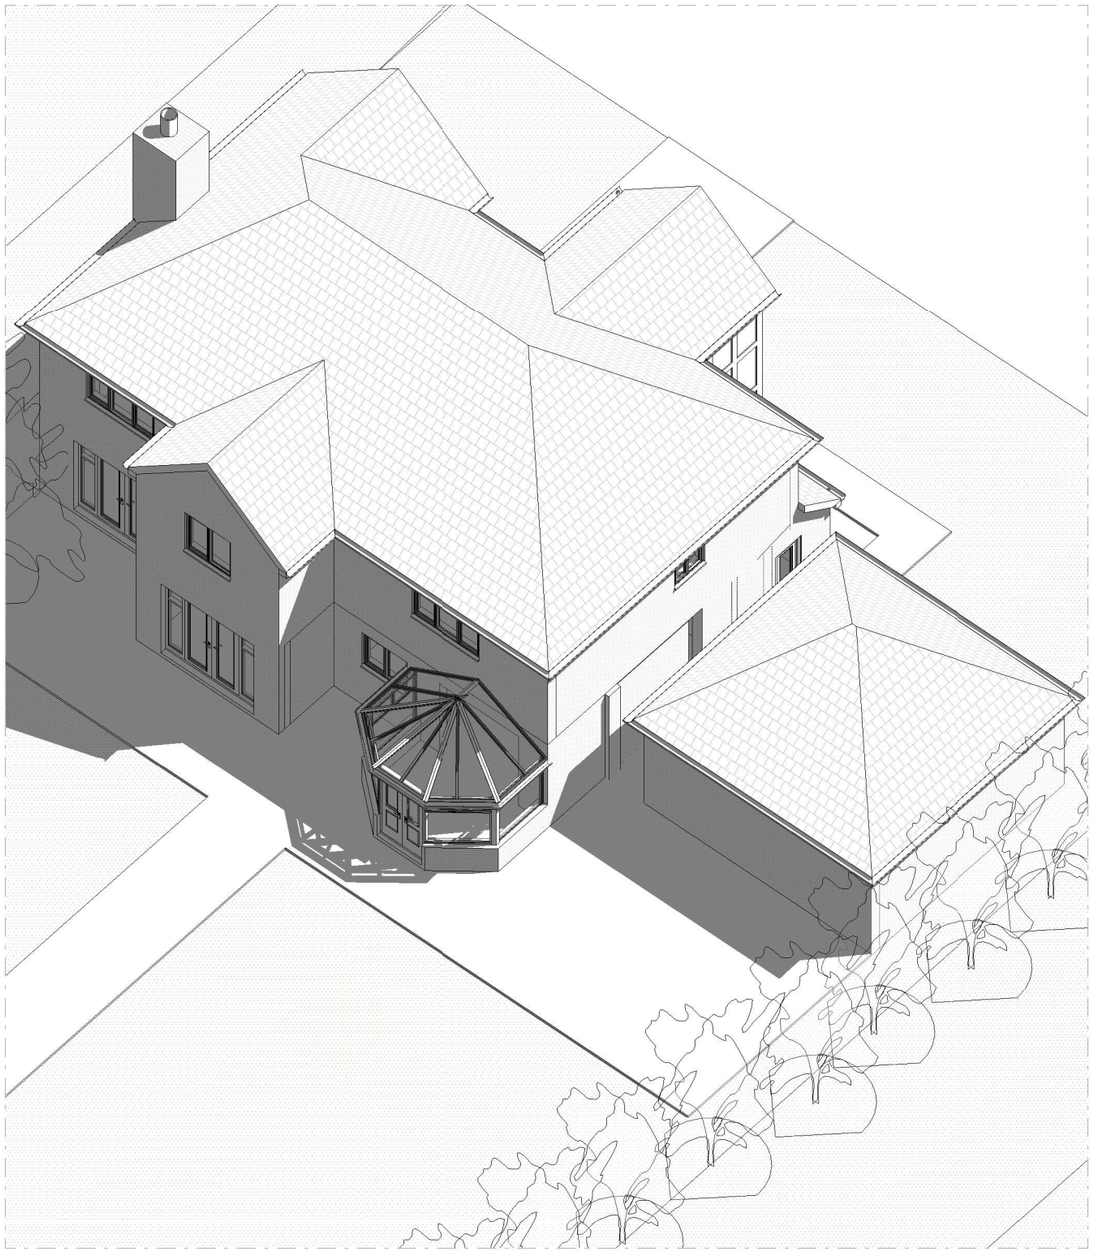

EXISTING ORTHOGRAPHIC VIEW



PROPOSED ORTHOGRAPHIC VIEW

Scale 1:100 @A3 0 1 2 3 4 5m

Scale 1:50 @A3 0 0.5 1 1.5 2 2.5m

Scale 1:20 @A3 0 20 40 60 80 100m

extension architecture

3 River Reach, Gartons Way,
Battersea
London SW11 3SX
Tel (0208) 288 8950 Fax (0871) 918 2798
www.extensionarchitecture.co.uk

This drawing is prepared solely for design and planning submission purposes. It is not intended or suitable for either building regulations or construction purposes and should not be used for such. All dimension shall be check and confirmed with site rep. and any discrepancies between the drawings and site shall be reported to PM. This drawing to be read in conjunction with engineers specification and details. For construction information please refer to all drawings and specification of works.

For any structural steelworks details please refer to structural engineer's drawings & calculations.

The copyright of the drawing and designs remains with Extension Architecture. All copies are only for information about the application, they may not be used for any other purpose without the express written permission of Extension Architecture.

CLIENT: Vik Barodia

PROJECT: 1 Lambourne Drive, KT11 3LB

TITLE: Existing & Proposed Orthographic View

NOTES

VERSION	DESCRIPTION	DATE

SCALE

DATE: 16.02.2024

DRAWN: SF

VERSION

SHEET REF. NO: 1LB -PL-REVB -13



PROPOSED 3D

Scale 1:100 @A3 — 0 1 2 3 4 5m

Scale 1:50 @A3 — 0 0.5 1 1.5 2 2.5m

Scale 1:20 @A3 — 0 20 40 60 80 100m

extension architecture

3 River Reach, Gartons Way,
Battersea
London SW11 3SX
Tel (0208) 288 8950 Fax (0871) 918 2798
www.extensionarchitecture.co.uk

This drawing is prepared solely for design and planning submission purposes. It is not intended or suitable for either building regulations or construction purposes and should not be used for such. All dimension shall be check and confirmed with site rep. and any discrepancies between the drawings and site shall be reported to PM. This drawing to be read in conjunction with engineers specification and details. For construction information please refer to all drawings and specification of works.

For any structural steelworks details please refer to structural engineer's drawings & calculations.

The copyright of the drawing and designs remains with Extension Architecture. All copies are only for information about the application, they may not be used for any other purpose without the express written permission of Extension Architecture.

CLIENT: Vik Barodia

PROJECT: 1 Lambourne Drive, KT11 3LB

TITLE: Proposed Rear Perspective

NOTES

VERSION	DESCRIPTION	DATE


SCALE:

DATE: 16.02.2024

DRAWN: SF

VERSION:

SHEET REF. NO: 1LB -PL-REVB -14

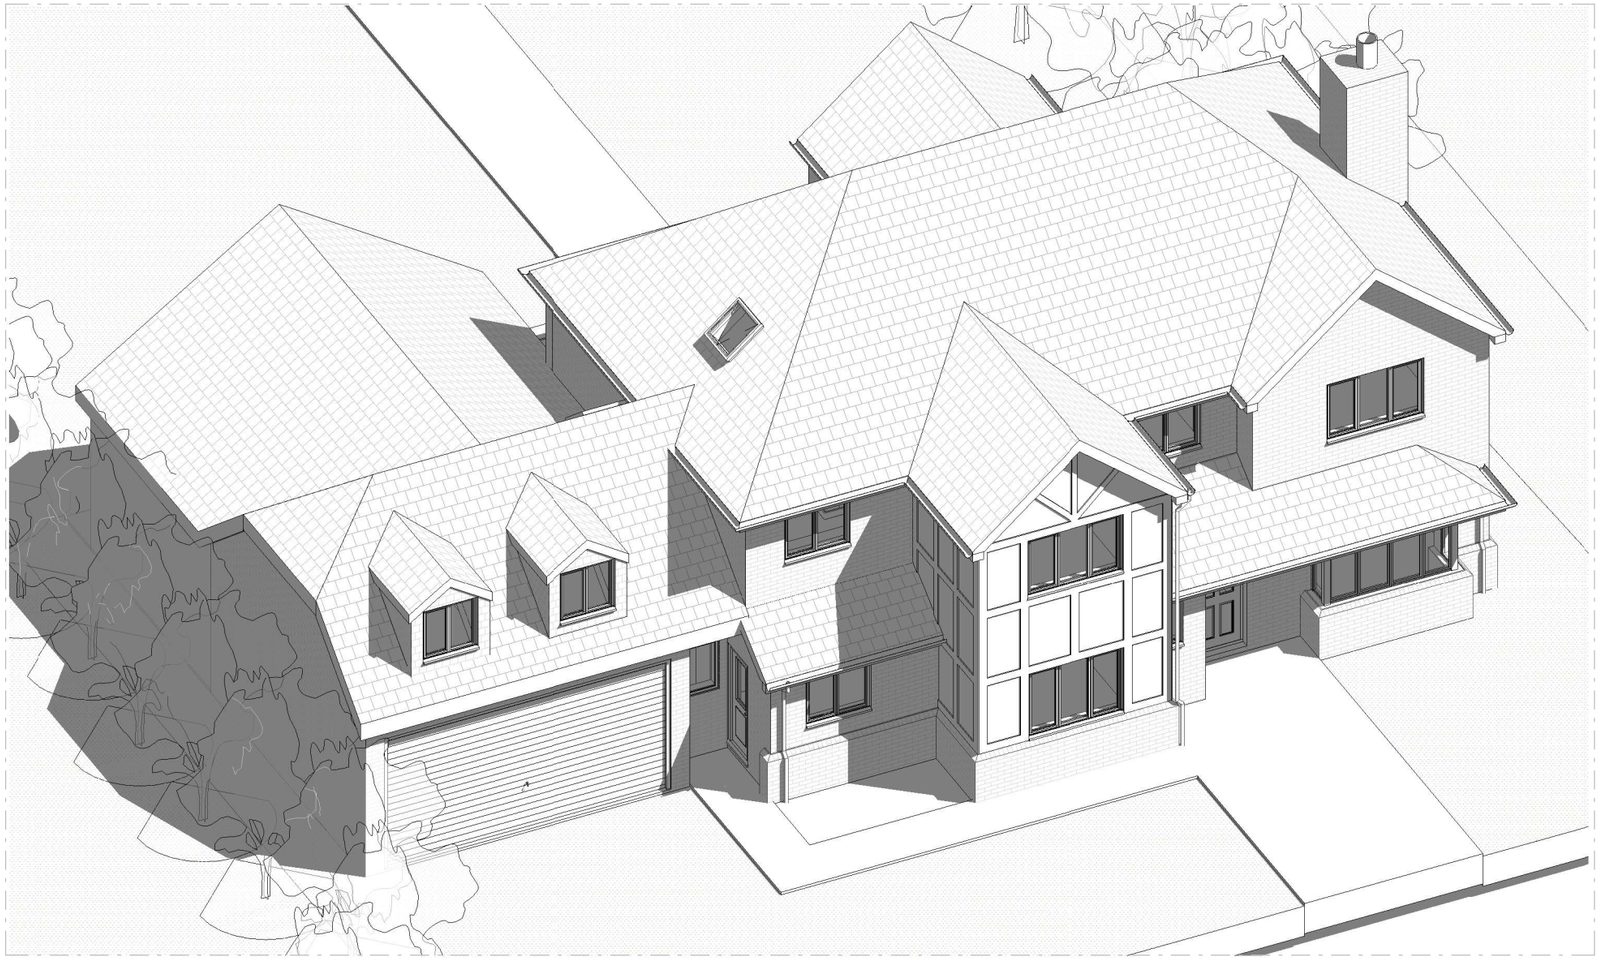

PROPOSED 3D

Scale 1:100 @A3 0 1 2 3 4 5m

Scale 1:50 @A3 0 0.5 1 1.5 2 2.5m

Scale 1:20 @A3 0 20 40 60 80 100m

extension architecture

3 River Reach, Gartons Way,
Battersea
London SW11 3SX
Tel (0208) 288 8950 Fax (0871) 918 2798
www.extensionarchitecture.co.uk

This drawing is prepared solely for design and planning submission purposes. It is not intended or suitable for either building regulations or construction purposes and should not be used for such. All dimension shall be check and confirmed with site rep. and any discrepancies between the drawings and site shall be reported to PM. This drawing to be read in conjunction with engineers specification and details. For construction information please refer to all drawings and specification of works.

For any structural steelworks details please refer to structural engineer's drawings & calculations.

The copyright of the drawing and designs remains with Extension Architecture. All copies are only for information about the application, they may not be used for any other purpose without the express written permission of Extension Architecture.

CLIENT: Vik Barodia

PROJECT: 1 Lambourne Drive, KT11 3LB

TITLE: Proposed Front Perspective

NOTES

VERSION	DESCRIPTION	DATE

SCALE

DATE: 16.02.2024

DRAWN: SF

VERSION

SHEET REF. NO: 1LB -PL-REVB -15