Detail design Drawings

Date:01/08/2024

Scope: Loft conversion,Internal Reconfiguration and single storey rear extension




extension architecture
3 River Reach, Gartons Way, Battersea
London SW11 3SX
Tel (0208) 288 8950 Fax (0871) 918 2798
www.extensionarchitecture.co.uk

Project Name: 1 Lambourne drive cobham
Address: 1 Lambourne drive, KT11, 3LB
Client: Vik Barodia

Drawing No.	Drawings Title	Scale
1LD-TD-01	Existing Ground Floor Plan	1:100
1LD-TD-02	Proposed Ground Floor Plan	1:100
1LD-TD-03	Existing First Floor Plan	1:100
1LD-TD-04	Proposed First Floor Plan	1:100
1LD-TD-05	Existing Roof Floor Plan	1:100
1LD-TD-06	Proposed Roof Floor Plan	1:100
1LD-TD-07	Existing & Proposed Front Elevation	1:100
1LD-TD-08	Proposed & Proposed Rear Elevation	1:100
1LD-TD-09	Existing & Proposed Left Elevation	1:100
1LD-TD-10	Existing & Proposed Right Elevation	1:100
1LD-TD-11	Existing & Proposed Section A-A	1:100
1LD-TD-12	Existing & Proposed Section B-B	1:100
1LD-TD-13	Stud wall Internal wall elevation (1/3)	1: 100
1LD-TD-14	Internal wall elevation (2/3)	1: 100
1LD-TD-15	Internal wall elevation (3/3)	1: 100
1LD-TD-16	Roof specification	1:100
1LD-TD-17	Exterior Specification (1/4)	1:100
1LD-TD-18	Exterior Specification (2/4)	1:100
1LD-TD-19	Exterior Specification (3/4)	1:100
1LD-TD-20	Exterior Specification (4/4)	1:100
1LD-TD-21	Door,Window & Skylight location plan(1/3)	1:100
1LD-TD-22	Door,Window & Skylight location plan(2/3)	1:100
1LD-TD-23	Door,Window & Skylight location plan(3/3)	1:100
1LD-TD-24	Window schedule	1:20
1LD-TD-25	Internal door & Skylight schedule	1:20
1LD-TD-26	External door schedule	1:20
1LD-TD-27	Ground floor Flooring Specifications	1:100
1LD-TD-28	First floor Flooring Specifications	1:100
1LD-TD-29	Ground floor skirting Specifications	1:100
1LD-TD-30	First floor Skirting Specifications	1:100
1LD-TD-31	Ground floor Wall Finish Specifications	1:100
1LD-TD-32	First floor Wall Finish Specifications	1: 100
1LD-TD-33	Ground floor Coving Specifications	1: 100
1LD-TD-34	Staircase detail drawing (1/2)	1: 100
1LD-TD-35	Staircase detail drawing (2/2)	1: 100
1LD-M&E-01	Ground Floor - Mechanical & Electrical drawings (1/2)	1:100
1LD-M&E-02	First Floor -Mechanical & Electrical drawings (2/2)	1:100

extension architecture
3 River Reach, Gartons Way, Battersea
London SW11 3SX
Tel (0208) 288 8950 Fax (0871) 918 2798
www.extensionarchitecture.co.uk

Project Name: 1 Lambourne drive cobham
Address: 1 Lambourne drive, KT11, 3LB
Client: Vik Barodia

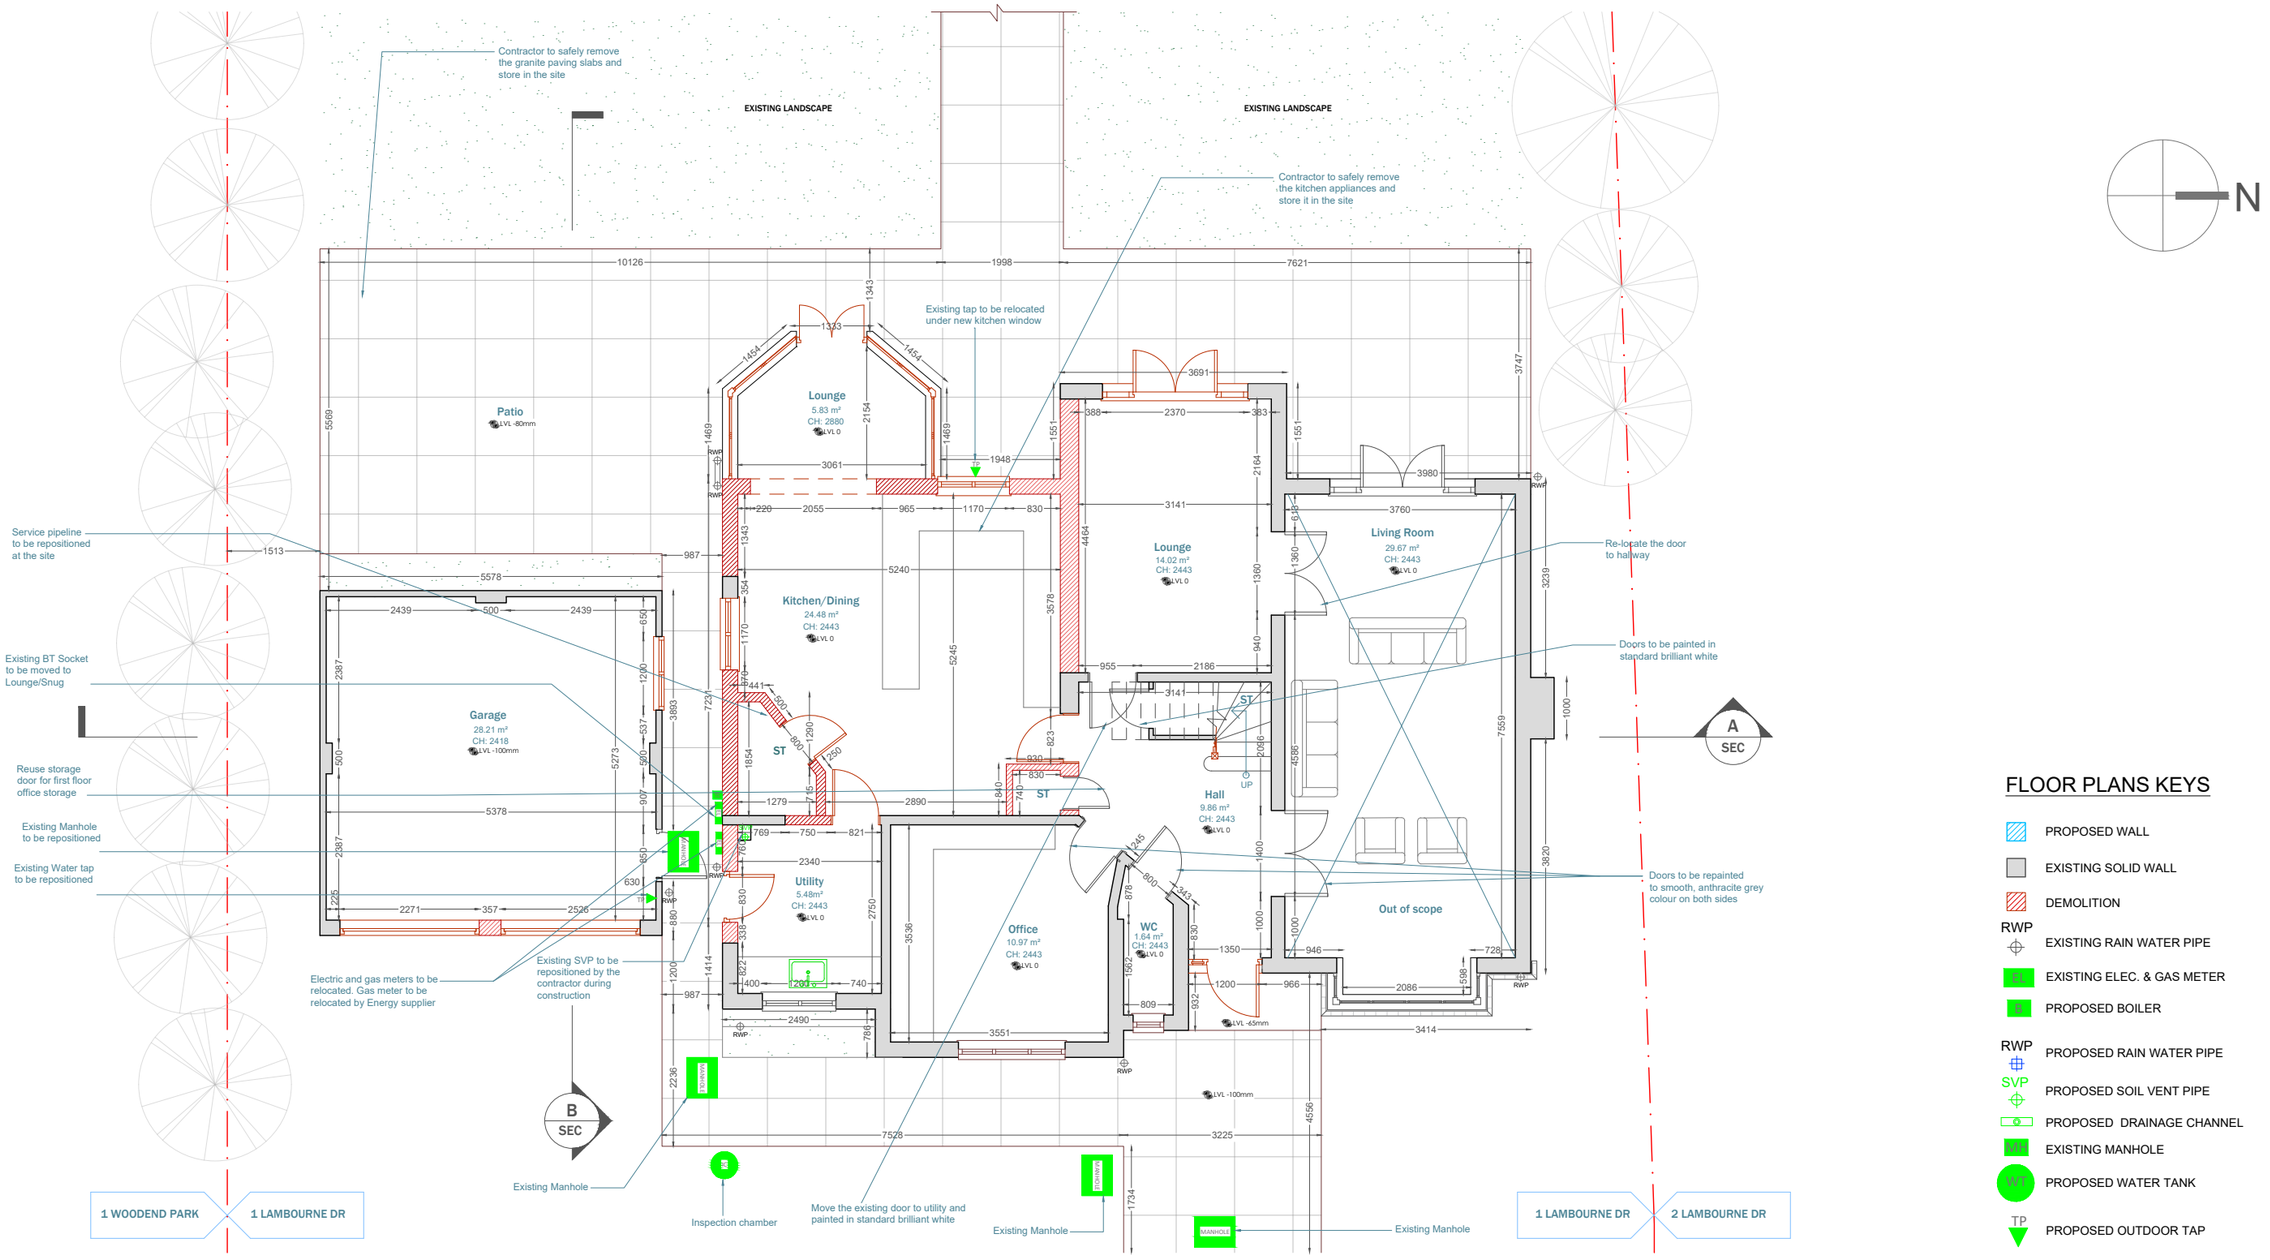

FLOOR PLANS KEYS

- PROPOSED WALL
- EXISTING SOLID WALL
- DEMOLITION
- RWP — EXISTING RAIN WATER PIPE
- EGM — EXISTING ELEC. & GAS METER
- B — PROPOSED BOILER
- RWP — PROPOSED RAIN WATER PIPE
- SVP — PROPOSED SOIL VENT PIPE
- PROPOSED DRAINAGE CHANNEL
- MH — EXISTING MANHOLE
- WT — PROPOSED WATER TANK
- TP — PROPOSED OUTDOOR TAP

EXISTING GROUND FLOOR PLAN

Scale 1:100 @A3 — 0 1 2 3 4 5m
Scale 1:50 @A3 — 0 0.5 1 1.5 2 2.5m
Scale 1:20 @A3 — 0 20 40 60 80 100m


extension architecture
3 River Reach, Gartons Way, Battersea
London SW11 3SX
Tel (0208) 288 8950 Fax (0871) 918 2798
www.extensionarchitecture.co.uk

This drawing is prepared solely for design and planning submission purposes. It is not intended or suitable for either building regulations or construction purposes and should not be used for such. All dimension shall be check and confirmed with site rep. and any discrepancies between the drawings and site shall be reported to PM. This drawing to be read in conjunction with engineers specification and details.
For construction information please refer to all drawings and specification of works.

For any structural steelworks details please refer to structural engineer's drawings & calculations.

The copyright of the drawing and designs remains with Extension Architecture. All copies are only for information about the application, they may not be used for any other purpose without the express written permission of Extension Architecture.

CLIENT: Vik Barodia	NOTES			SCALE: 1:100	DATE: 01.08.2024
PROJECT: 1 Lambourne Drive, KT11 3LB	VERSION	DESCRIPTION	DATE	DRAWN: BOUSIA	VERSION
TITLE: Existing Ground Floor Plan				SHEET REF. NO: 1LD-TD-01	

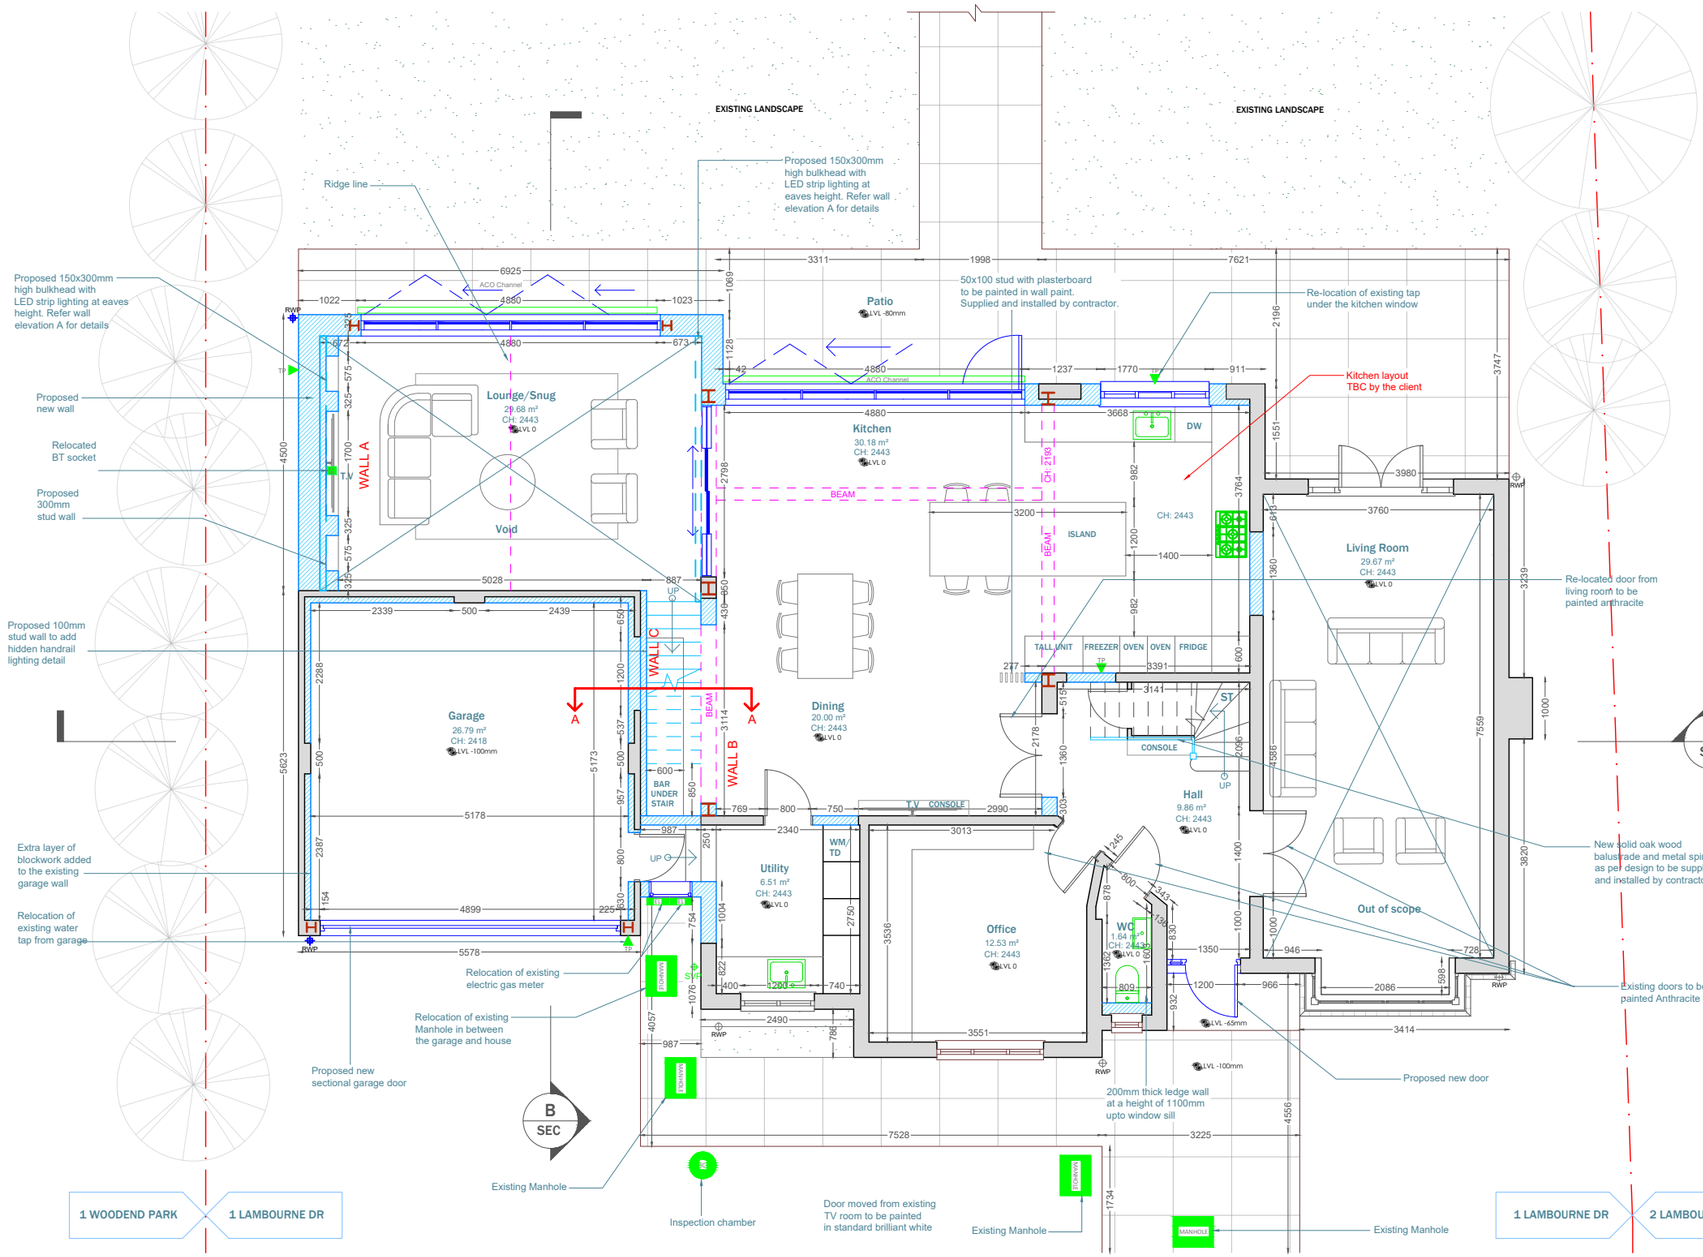

N

Proposed staircase to mezzanine floor

No of riser : 12
Going : 220mm
Riser : 188mm

FLOOR PLANS KEYS

- PROPOSED WALL
- EXISTING SOLID WALL
- DEMOLITION
- RWP — EXISTING RAIN WATER PIPE
- EXISTING ELEC. & GAS METER
- PROPOSED BOILER
- RWP — PROPOSED RAIN WATER PIPE
- SVP — PROPOSED SOIL VENT PIPE
- PROPOSED DRAINAGE CHANNEL
- MH — EXISTING MANHOLE
- WT — PROPOSED WATER TANK
- TP — PROPOSED OUTDOOR TAP

PROPOSED GROUND FLOOR PLAN

Scale 1:100 @A3 — 0 1 2 3 4 5m
Scale 1:50 @A3 — 0 0.5 1 1.5 2 2.5m
Scale 1:20 @A3 — 0 20 40 60 80 100m


extension architecture
3 River Reach, Gartons Way, Battersea
London SW11 3SX
Tel (0208) 288 8950 Fax (0871) 918 2798
www.extensionarchitecture.co.uk

This drawing is prepared solely for design and planning submission purposes. It is not intended or suitable for either building regulations or construction purposes and should not be used for such. All dimension shall be check and confirmed with site rep. and any discrepancies between the drawings and site shall be reported to PM. This drawing to be read in conjunction with engineers specification and details.
For construction information please refer to all drawings and specification of works.

For any structural steelworks details please refer to structural engineer's drawings & calculations.

The copyright of the drawing and designs remains with Extension Architecture. All copies are only for information about the application, they may not be used for any other purpose without the express written permission of Extension Architecture.

CLIENT: Vik Barodia	NOTES	SCALE: 1:100	DATE: 01.08.2024
PROJECT: 1 Lambourne Drive, KT11 3LB	VERSION / DESCRIPTION / DATE	DRAWN: BOUSIA	VERSION
TITLE: **Proposed Ground Floor Plan**		SHEET REF. NO: 1LD-TD-01	

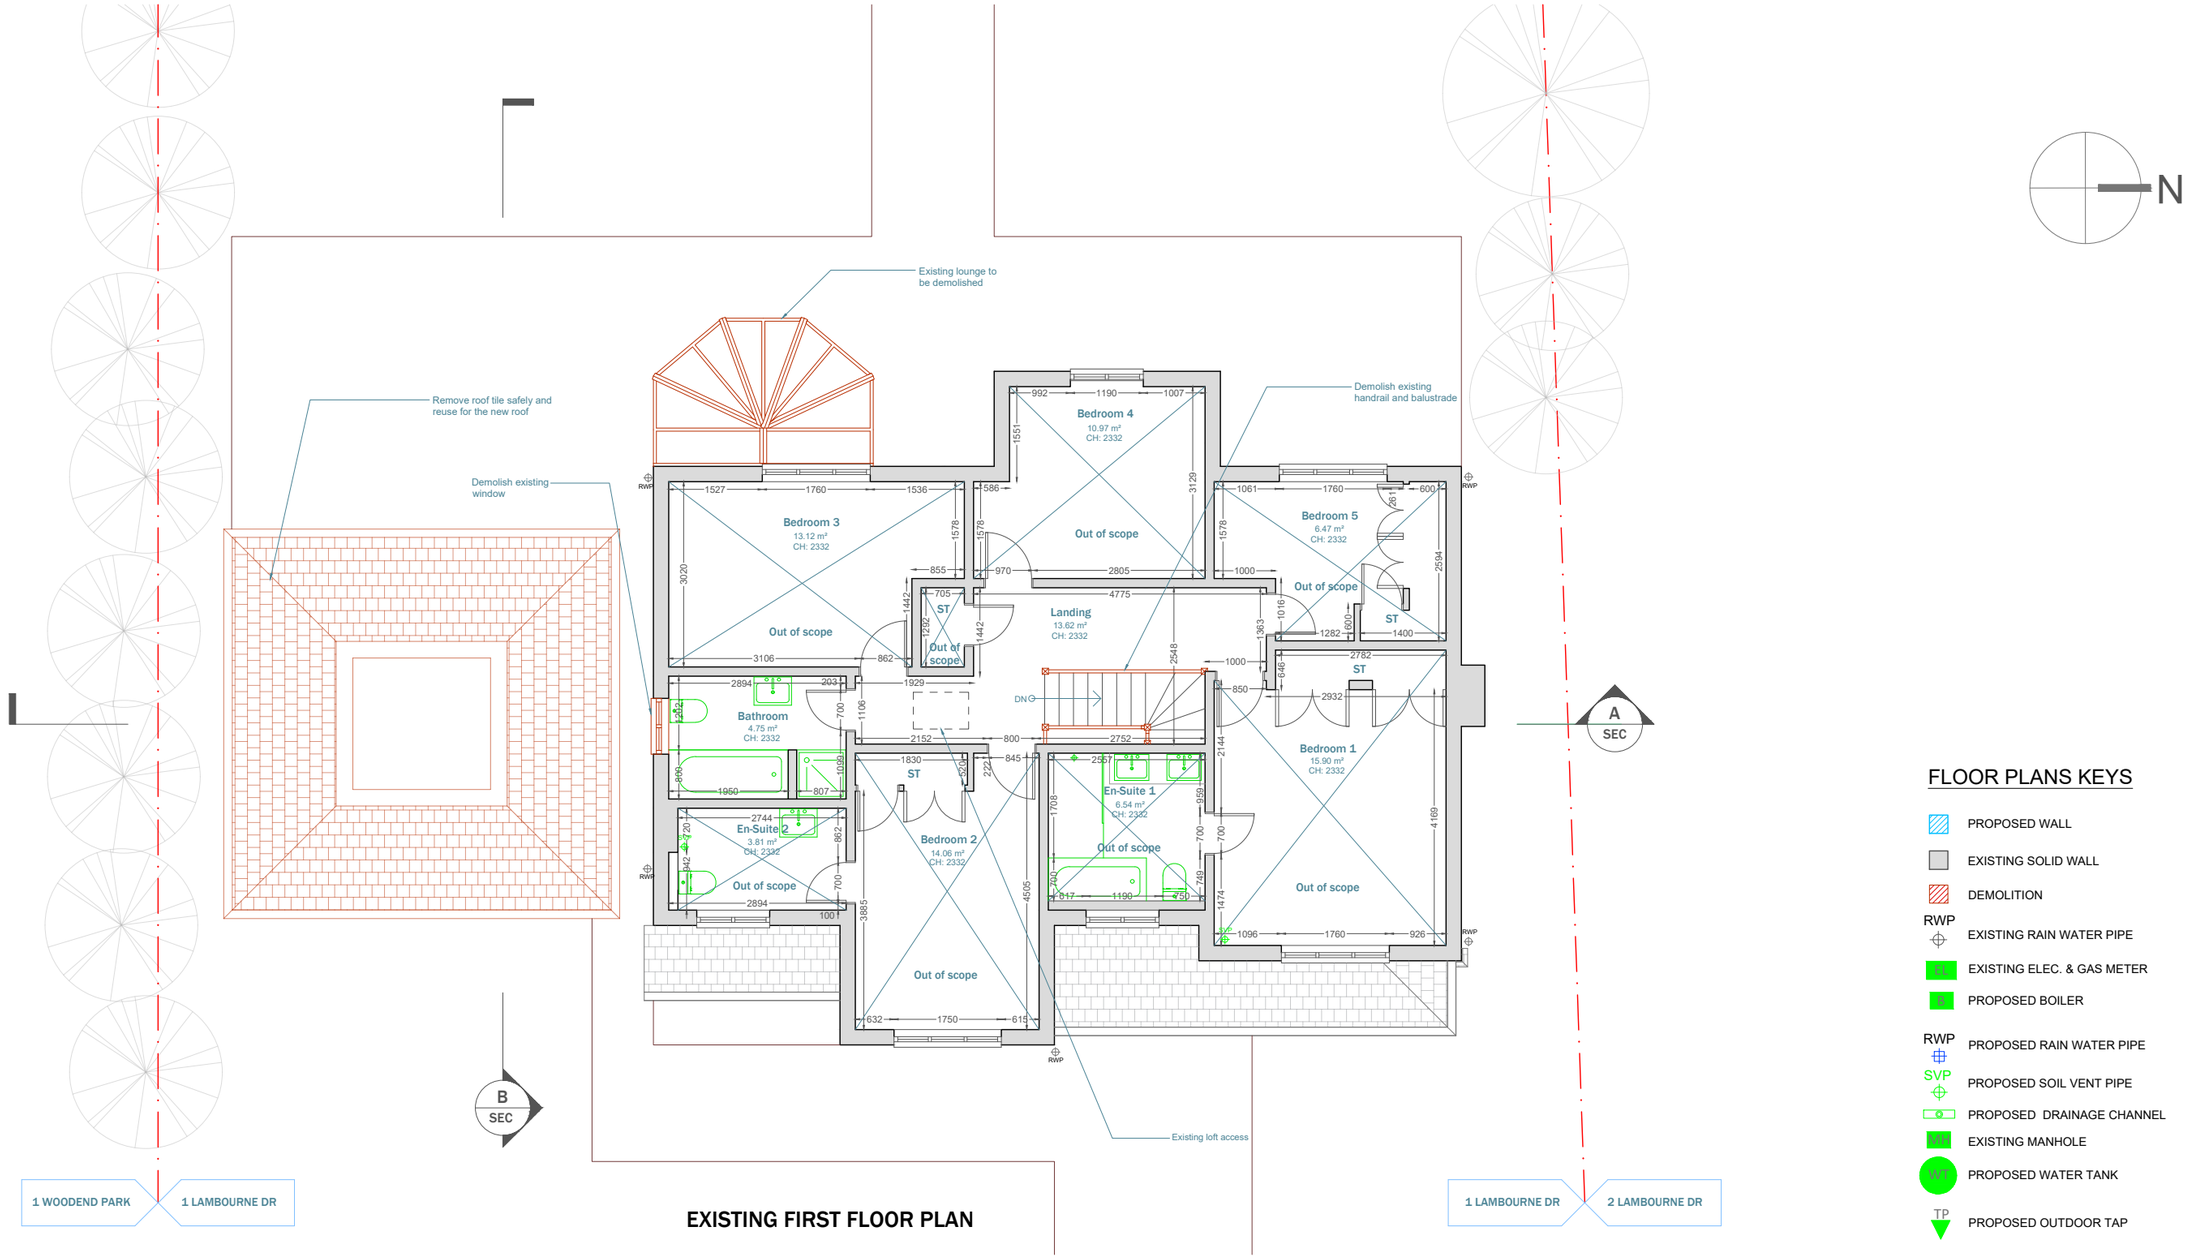

EXISTING FIRST FLOOR PLAN

N

FLOOR PLANS KEYS

- PROPOSED WALL
- EXISTING SOLID WALL
- DEMOLITION
- RWP — EXISTING RAIN WATER PIPE
- EM — EXISTING ELEC. & GAS METER
- B — PROPOSED BOILER
- RWP — PROPOSED RAIN WATER PIPE
- SVP — PROPOSED SOIL VENT PIPE
- PROPOSED DRAINAGE CHANNEL
- MH — EXISTING MANHOLE
- WT — PROPOSED WATER TANK
- TP — PROPOSED OUTDOOR TAP

Scale 1:100 @A3 — 0 1 2 3 4 5m
Scale 1:50 @A3 — 0 0.5 1 1.5 2 2.5m
Scale 1:20 @A3 — 0 20 40 60 80 100m

extension architecture
3 River Reach, Gartons Way, Battersea
London SW11 3SX
Tel (0208) 288 8950 Fax (0871) 918 2798
www.extensionarchitecture.co.uk

This drawing is prepared solely for design and planning submission purposes. It is not intended or suitable for either building regulations or construction purposes and should not be used for such. All dimension shall be check and confirmed with site rep. and any discrepancies between the drawings and site shall be reported to PM. This drawing to be read in conjunction with engineers specification and details.
For construction information please refer to all drawings and specification of works.

For any structural steelworks details please refer to structural engineer's drawings & calculations.


The copyright of the drawing and designs remains with Extension Architecture. All copies are only for information about the application, they may not be used for any other purpose without the express written permission of Extension Architecture.

CLIENT: Vik Barodia
PROJECT: 1 Lambourne Drive, KT11 3LB
TITLE: **Existing First Floor Plan**

NOTES

VERSION	DESCRIPTION	DATE

SCALE: **1:100**
DATE: **01.08.2024**
DRAWN: **BOUSIA**
VERSION:
SHEET REF. NO: **1LD-TD-03**

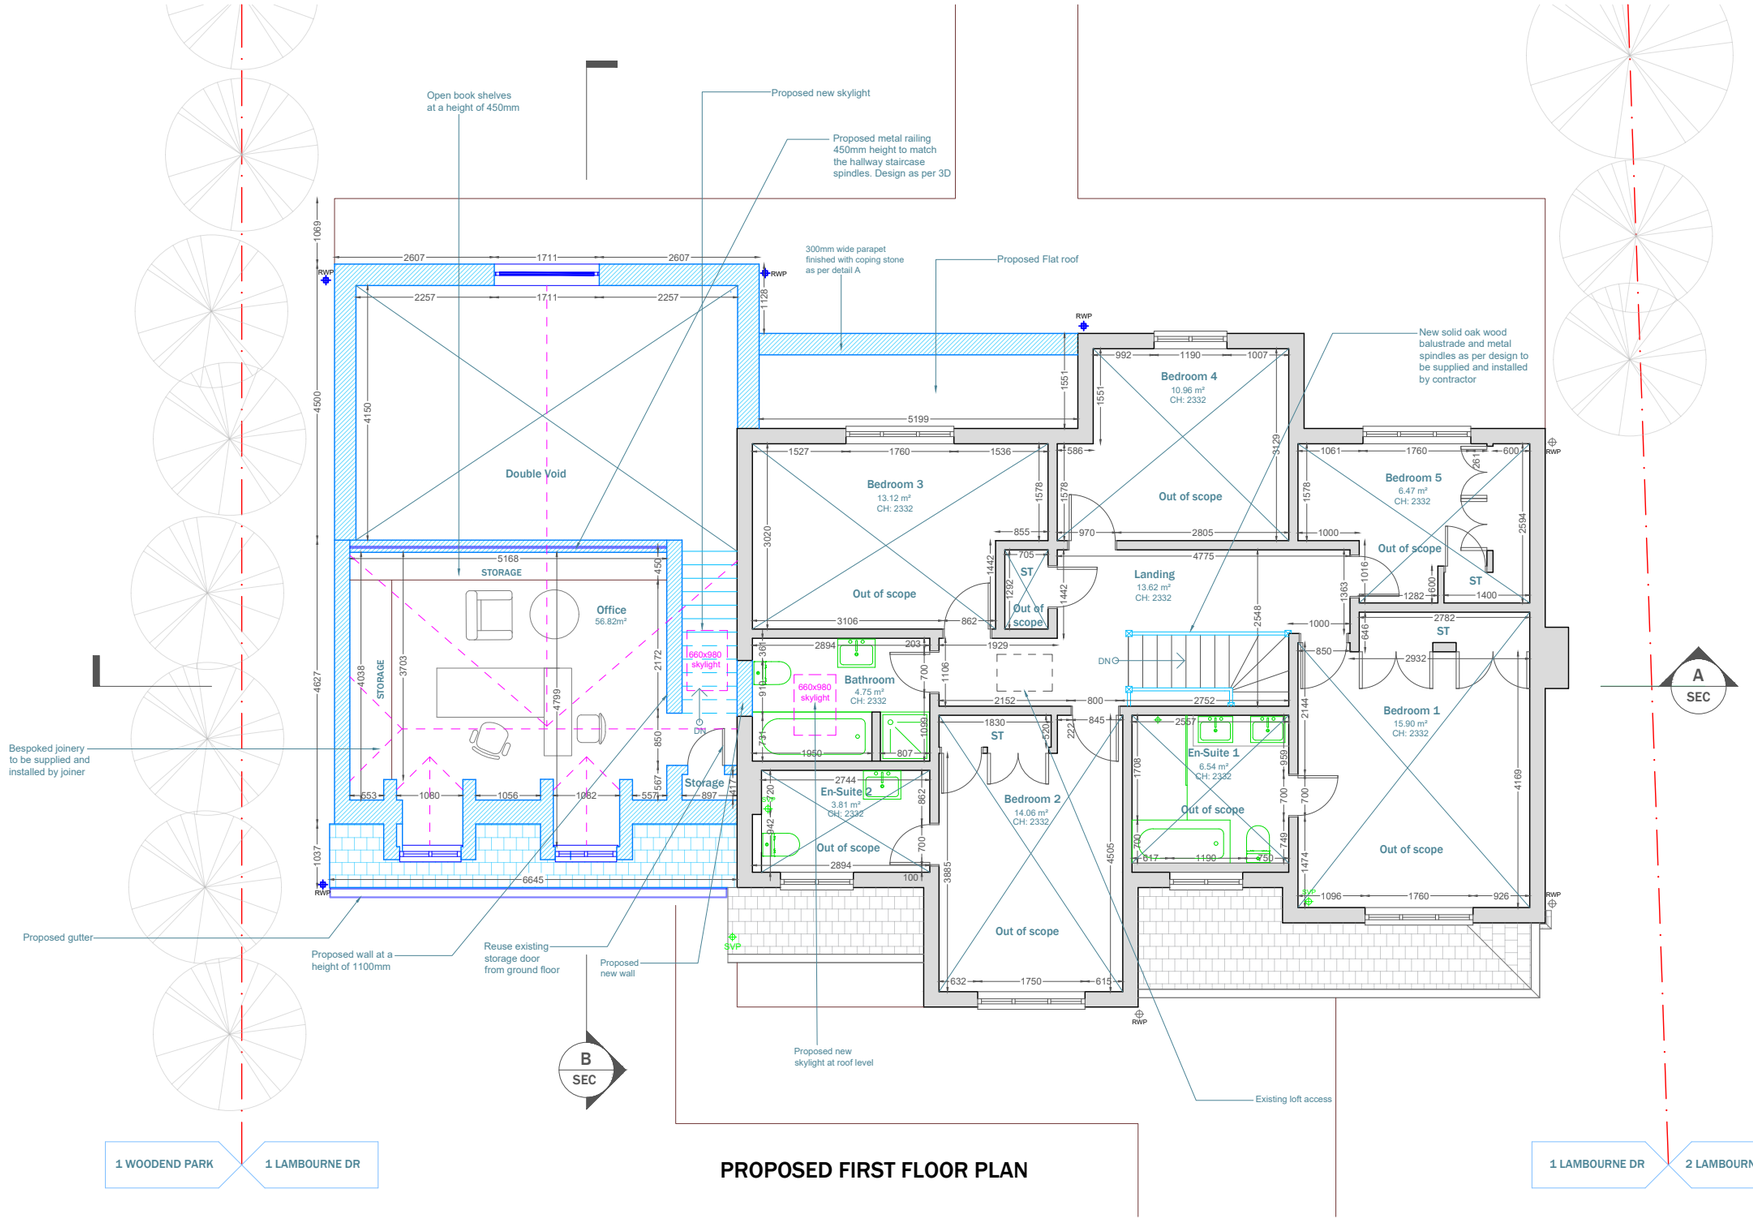

N

FLOOR PLANS KEYS

- PROPOSED WALL
- EXISTING SOLID WALL
- DEMOLITION
- RWP — EXISTING RAIN WATER PIPE
- EXISTING ELEC. & GAS METER
- PROPOSED BOILER
- RWP — PROPOSED RAIN WATER PIPE
- SVP — PROPOSED SOIL VENT PIPE
- PROPOSED DRAINAGE CHANNEL
- EXISTING MANHOLE
- PROPOSED WATER TANK
- TP — PROPOSED OUTDOOR TAP

Scale 1:100 @A3 — 0 1 2 3 4 5m
Scale 1:50 @A3 — 0 0.5 1 1.5 2 2.5m
Scale 1:20 @A3 — 0 20 40 60 80 100m


extension architecture
3 River Reach, Gartons Way, Battersea
London SW11 3SX
Tel (0208) 288 8950 Fax (0871) 918 2798
www.extensionarchitecture.co.uk

This drawing is prepared solely for design and planning submission purposes. It is not intended or suitable for either building regulations or construction purposes and should not be used for such. All dimension shall be check and confirmed with site rep. and any discrepancies between the drawings and site shall be reported to PM. This drawing to be read in conjunction with engineers specification and details.
For construction information please refer to all drawings and specification of works.

For any structural steelworks details please refer to structural engineer's drawings & calculations.

The copyright of the drawing and designs remains with Extension Architecture. All copies are only for information about the application, they may not be used for any other purpose without the express written permission of Extension Architecture.

CLIENT: Vik Barodia	NOTES			SCALE: 1:100	DATE: 01.08.2024
PROJECT: 1 Lambourne Drive, KT11 3LB	VERSION	DESCRIPTION	DATE	DRAWN: BOUSIA	VERSION
TITLE: **Proposed First Floor Plan**				SHEET REF. NO: 1LD-TD-04	

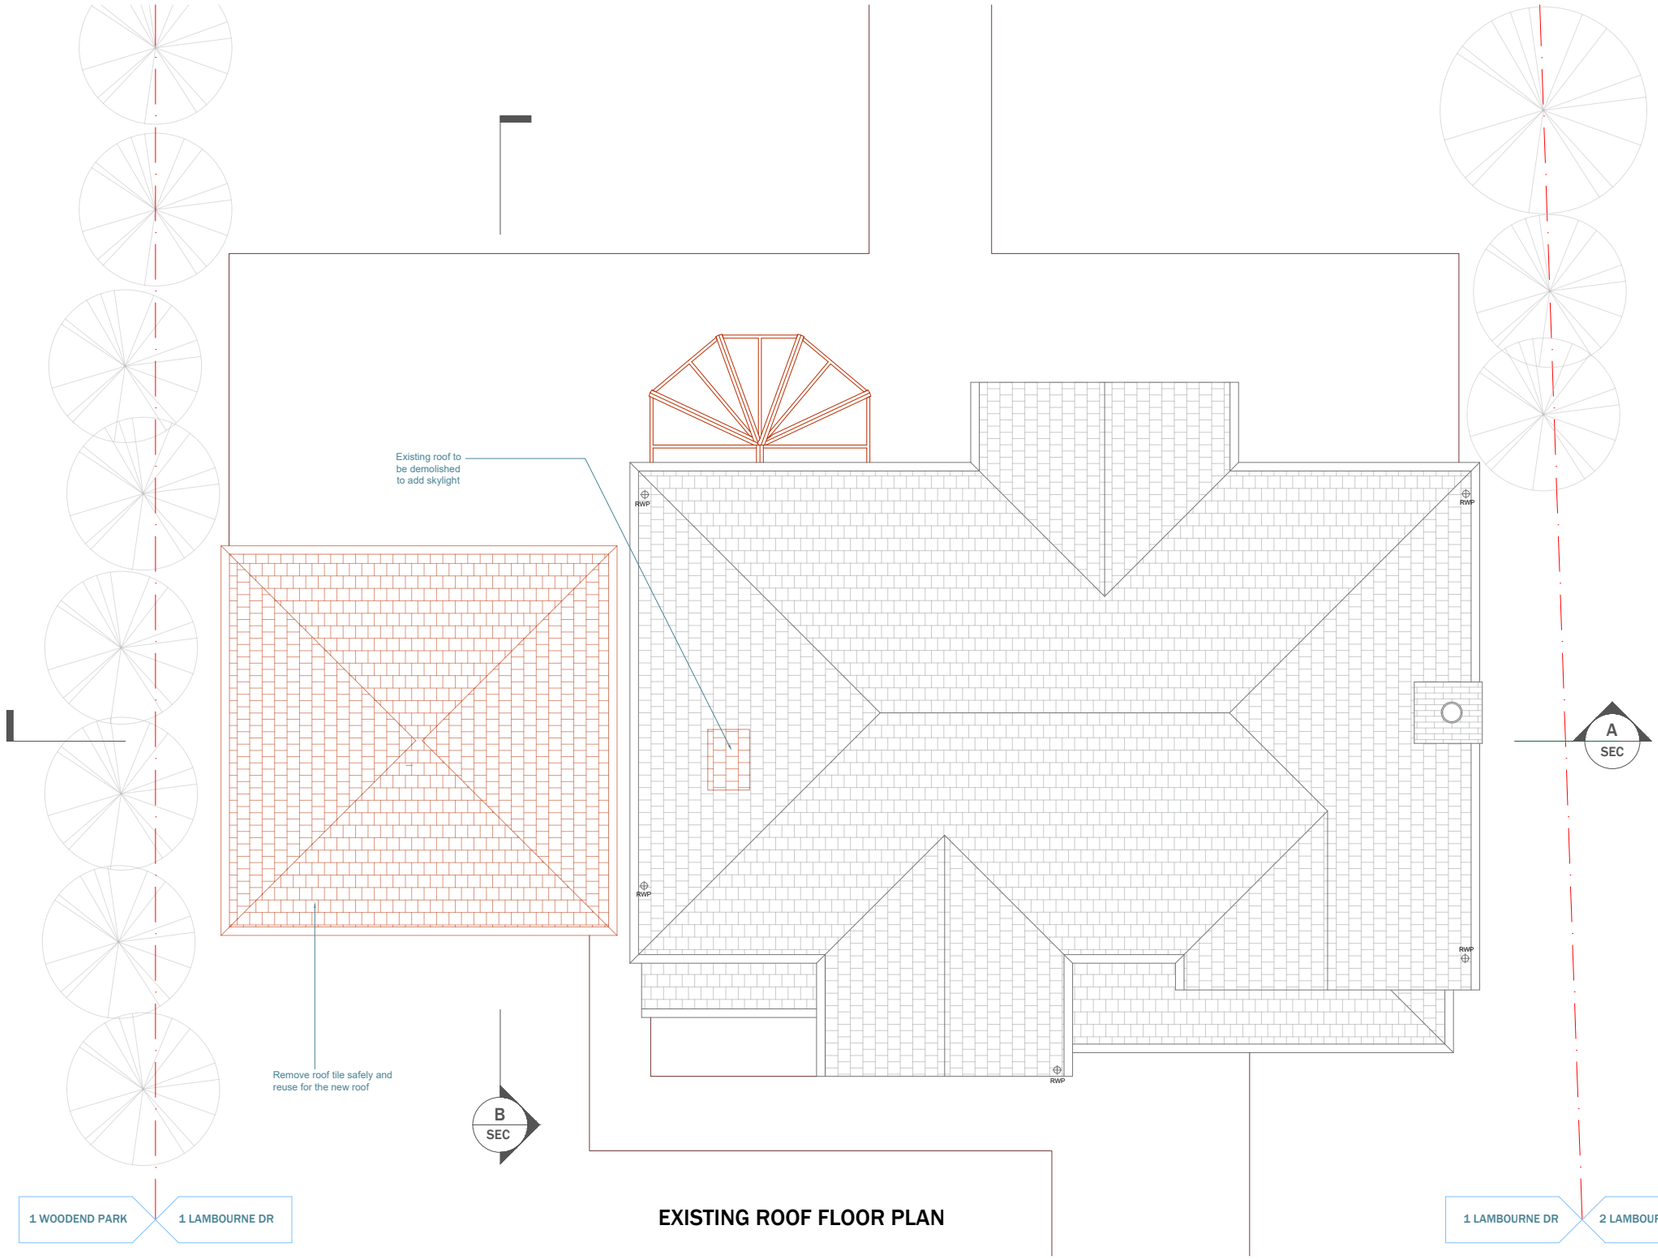

N

ROOF PLANS KEYS

- EXISTING ROOF
- PROPOSED SLOPE ROOF
- PROPOSED FLAT ROOF
- RWP — EXISTING RAIN WATER PIPE
- RWP — PROPOSED RAIN WATER PIPE
- EXISTING GUTTERING
- PROPOSED GUTTERING
- SVP — PROPOSED SOIL VENT PIPE

EXISTING ROOF FLOOR PLAN

Scale 1:100 @A3 — 0 1 2 3 4 5m

Scale 1:50 @A3 — 0 0.5 1 1.5 2 2.5m

Scale 1:20 @A3 — 0 20 40 60 80 100m


extension architecture
3 River Reach, Gartons Way, Battersea
London SW11 3SX
Tel (0208) 288 8950 Fax (0871) 918 2798
www.extensionarchitecture.co.uk

This drawing is prepared solely for design and planning submission purposes. It is not intended or suitable for either building regulations or construction purposes and should not be used for such. All dimension shall be check and confirmed with site rep. and any discrepancies between the drawings and site shall be reported to PM. This drawing to be read in conjunction with engineers specification and details.
For construction information please refer to all drawings and specification of works.

For any structural steelworks details please refer to structural engineer's drawings & calculations.

The copyright of the drawing and designs remains with Extension Architecture. All copies are only for information about the application, they may not be used for any other purpose without the express written permission of Extension Architecture.

CLIENT: Vik Barodia	NOTES			SCALE: 1:100	DATE: 01.08.2024
PROJECT: 1 Lambourne Drive, KT11 3LB	VERSION	DESCRIPTION	DATE	DRAWN: BOUSIA	VERSION
TITLE: **Existing Roof Floor Plan**				SHEET REF. NO: 1LD-TD-05	

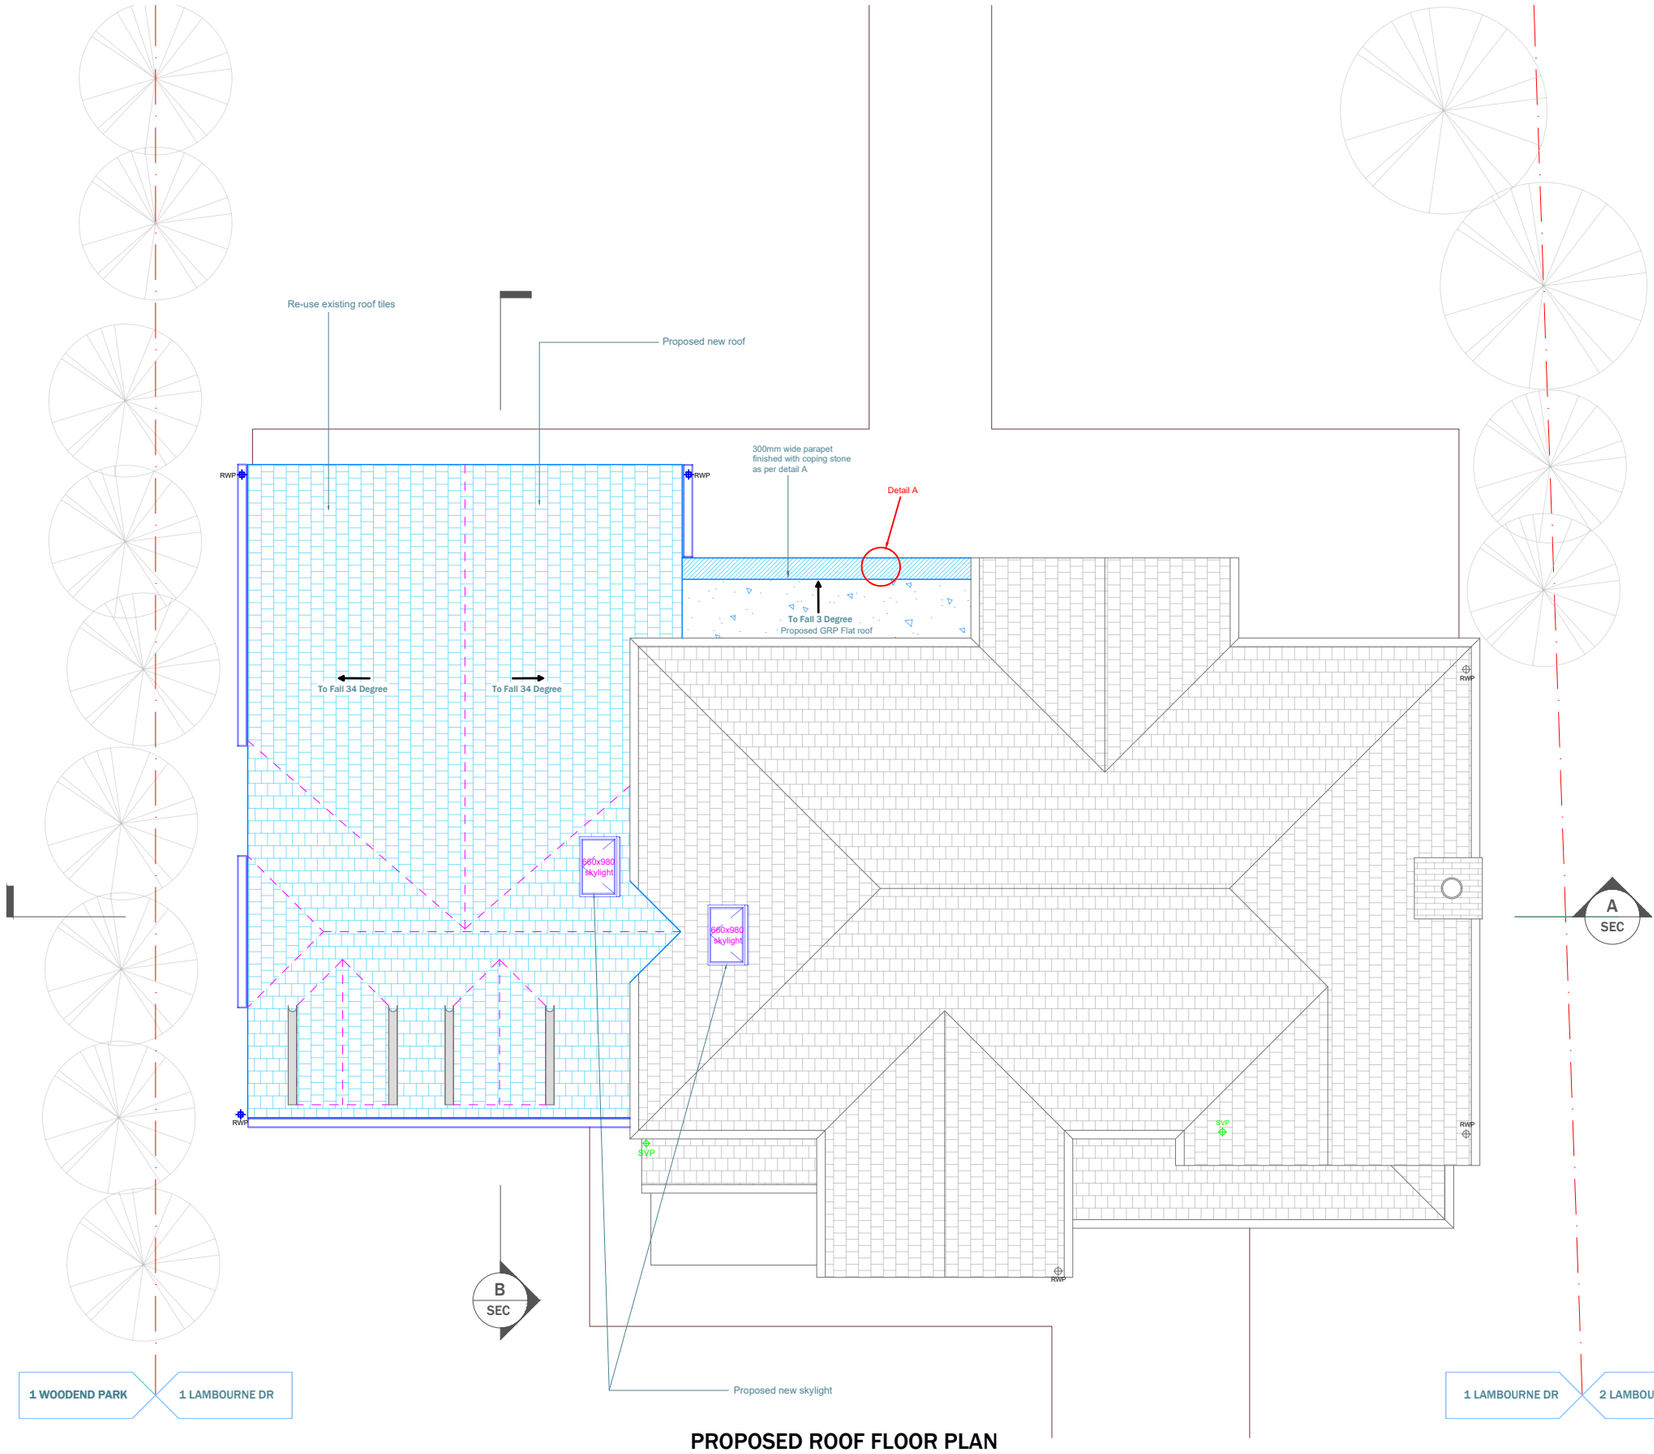

PROPOSED ROOF FLOOR PLAN


N

ROOF PLANS KEYS

- EXISTING ROOF
- PROPOSED SLOPE ROOF
- PROPOSED FLAT ROOF
- RWP — EXISTING RAIN WATER PIPE
- RWP — PROPOSED RAIN WATER PIPE
- EXISTING GUTTERING
- PROPOSED GUTTERING
- SVP — PROPOSED SOIL VENT PIPE

PARAPET DETAIL WITH BOX GUTTER

PARAPET HEIGHT - 250mm

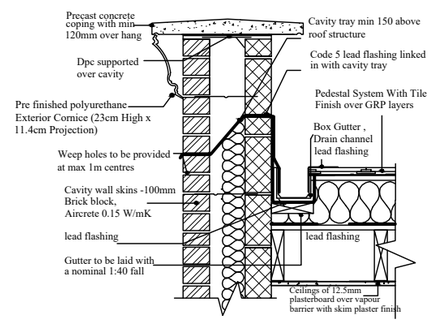

DETAIL A - 1:20

Scale 1:100 @A3 — 0 1 2 3 4 5m

Scale 1:50 @A3 — 0 0.5 1 1.5 2 2.5m

Scale 1:20 @A3 — 0 20 40 60 80 100m

extension architecture
3 River Reach, Gartons Way, Battersea
London SW11 3SX
Tel (0208) 288 8950 Fax (0871) 918 2798
www.extensionarchitecture.co.uk

This drawing is prepared solely for design and planning submission purposes. It is not intended or suitable for either building regulations or construction purposes and should not be used for such. All dimension shall be check and confirmed with site rep. and any discrepancies between the drawings and site shall be reported to PM. This drawing to be read in conjunction with engineers specification and details.
For construction information please refer to all drawings and specification of works.

For any structural steelworks details please refer to structural engineer's drawings & calculations.

The copyright of the drawing and designs remains with Extension Architecture. All copies are only for information about the application, they may not be used for any other purpose without the express written permission of Extension Architecture.

CLIENT: Vik Barodia

PROJECT: 1 Lambourne Drive, KT11 3LB

TITLE: **Proposed Roof Floor Plan**

NOTES

VERSION	DESCRIPTION	DATE

SCALE: **1:100**

DATE: **01.08.2024**

DRAWN: **BOUSIA**

VERSION:


SHEET REF. NO: **1LD-TD-06**



EXISTING FRONT ELEVATION

ELEVATION KEYS

- PROPOSED ROOF
- PROPOSED WALL
- PROPOSED RAIN WATER PIPE
- EXISTING GUTTERING
- PROPOSED GUTTERING
- EXISTING & PROPOSED SOIL VENT PIPE

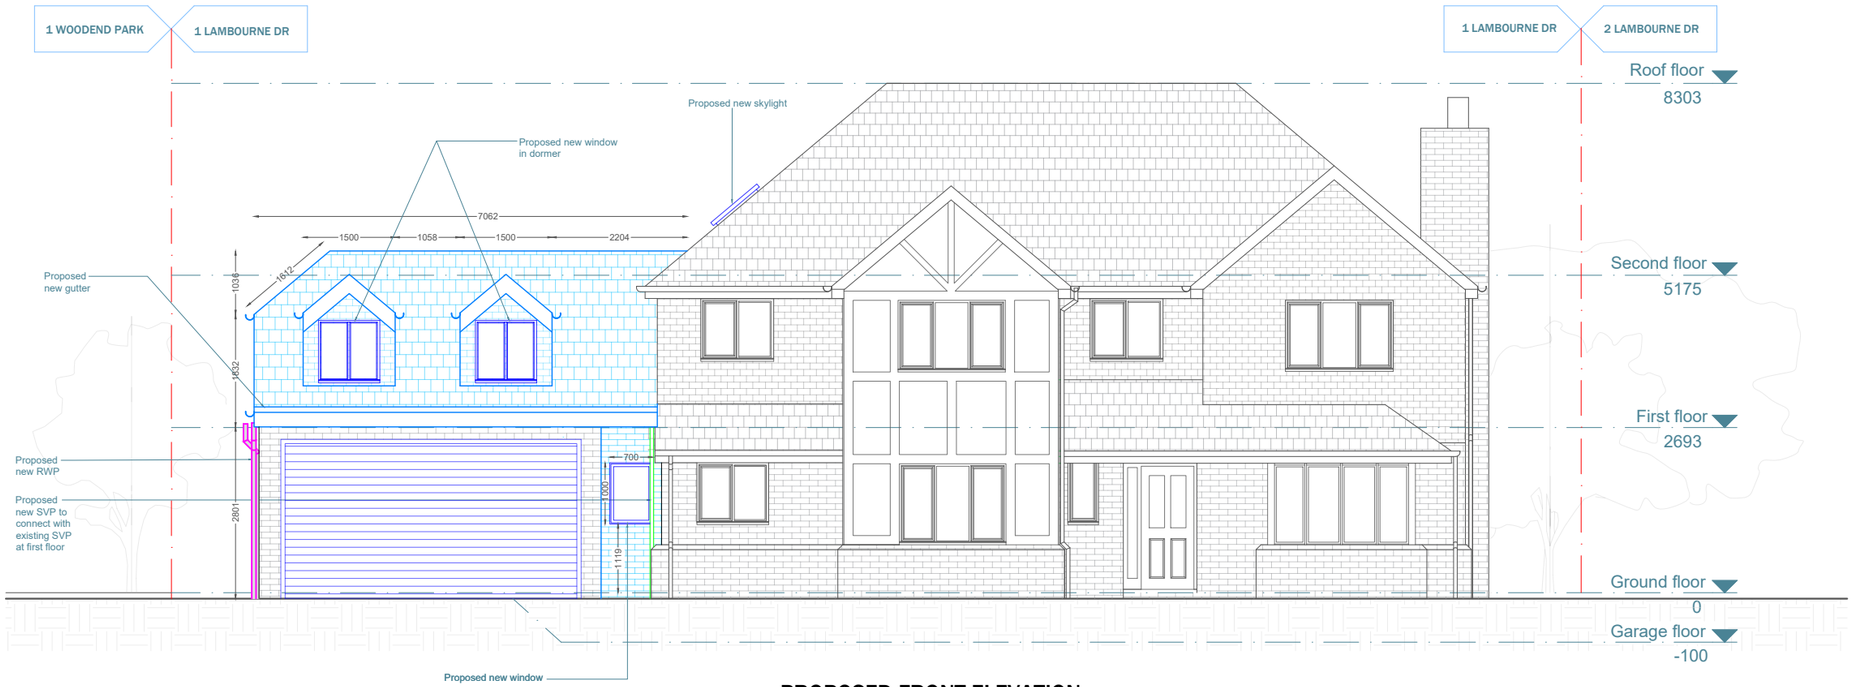

PROPOSED FRONT ELEVATION

Scale 1:100 @A3 — 0 1 2 3 4 5m

Scale 1:50 @A3 — 0 0.5 1 1.5 2 2.5m

Scale 1:20 @A3 — 0 20 40 60 80 100m

extension architecture
3 River Reach, Gartons Way, Battersea
London SW11 3SX
Tel (0208) 288 8950 Fax (0871) 918 2798
www.extensionarchitecture.co.uk

This drawing is prepared solely for design and planning submission purposes. It is not intended or suitable for either building regulations or construction purposes and should not be used for such. All dimension shall be check and confirmed with site rep. and any discrepancies between the drawings and site shall be reported to PM. This drawing to be read in conjunction with engineers specification and details.
For construction information please refer to all drawings and specification of works.

For any structural steelworks details please refer to structural engineer's drawings & calculations.


The copyright of the drawing and designs remains with Extension Architecture. All copies are only for information about the application, they may not be used for any other purpose without the express written permission of Extension Architecture.

CLIENT	Vik Barodia
PROJECT	1 Lambourne Drive, KT11 3LB
TITLE	**Existing & Proposed Rear Elevation**


NOTES

VERSION	DESCRIPTION	DATE

SCALE	**1:100**
DATE	**01.08.2024**
DRAWN	**BOUSIA**
VERSION	
SHEET REF. NO	**1LD-TD-07**

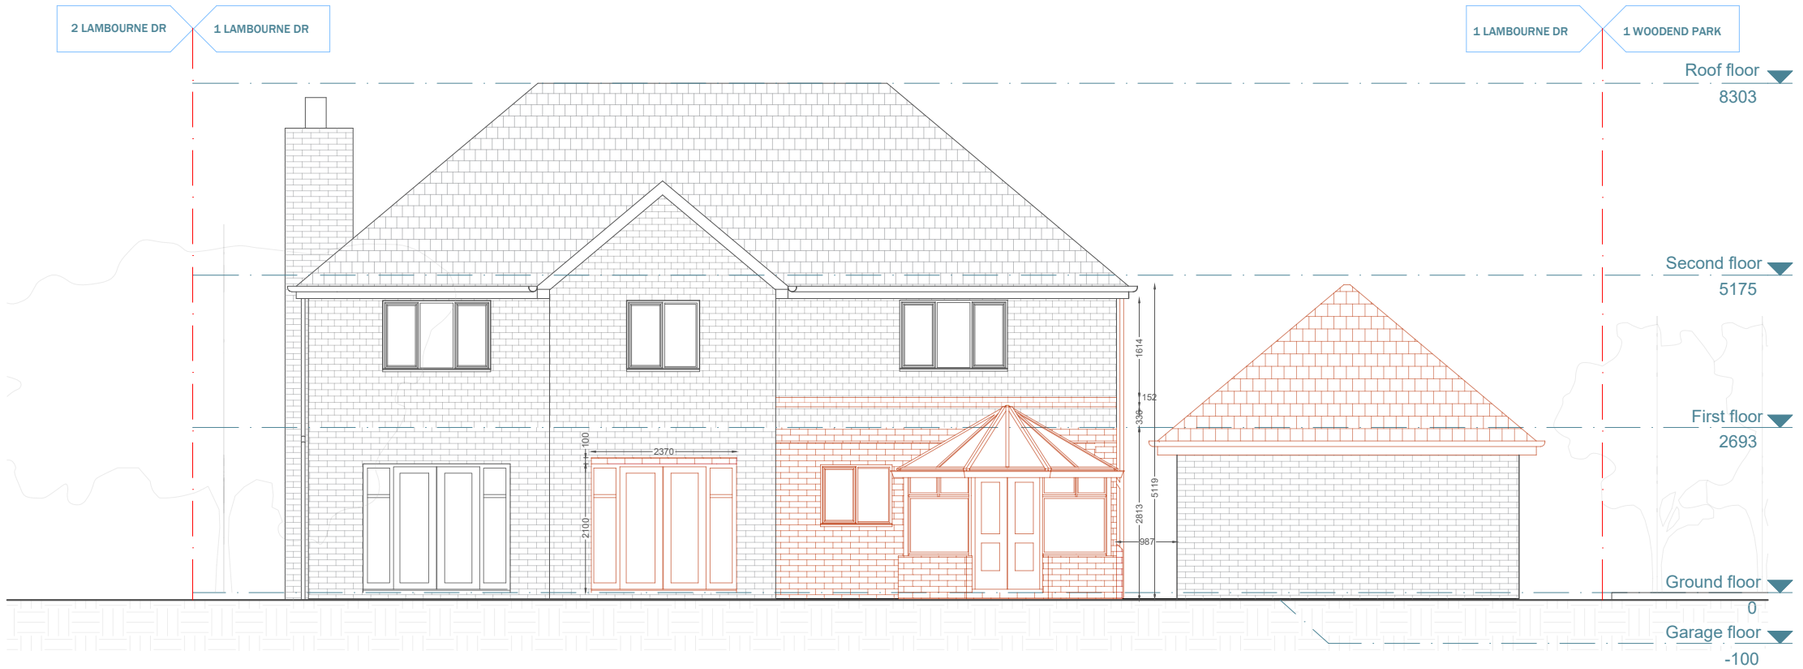

EXISTING REAR ELEVATION

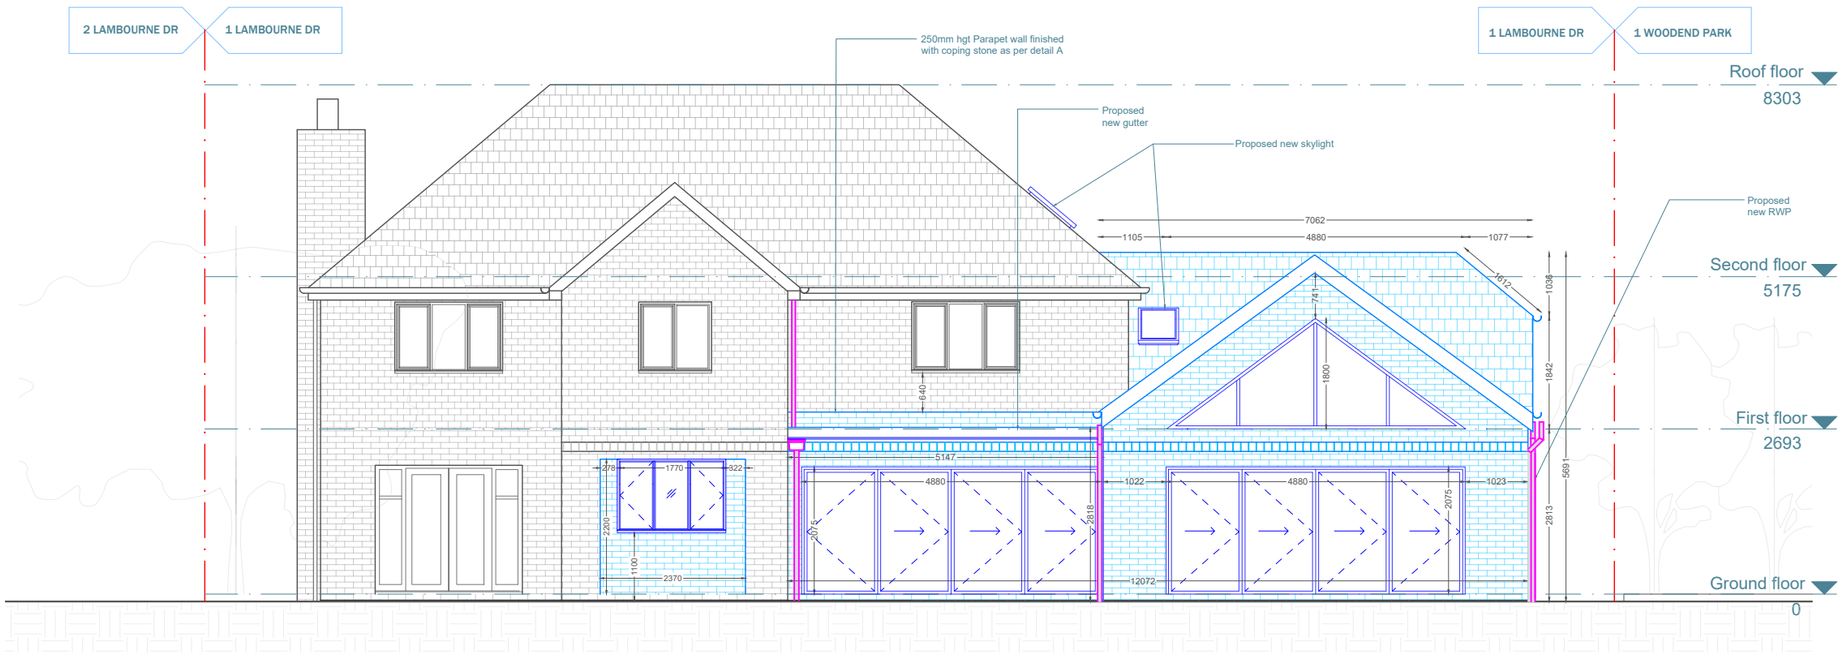

PROPOSED REAR ELEVATION

ELEVATION KEYS

- PROPOSED ROOF
- PROPOSED WALL
- PROPOSED RAIN WATER PIPE
- EXISTING GUTTERING
- PROPOSED GUTTERING
- EXISTING & PROPOSED SOIL VENT PIPE

Scale 1:100 @A3 — 0 1 2 3 4 5m

Scale 1:50 @A3 — 0 0.5 1 1.5 2 2.5m

Scale 1:20 @A3 — 0 20 40 60 80 100m

extension architecture
3 River Reach, Gartons Way, Battersea
London SW11 3SX
Tel (0208) 288 8950 Fax (0871) 918 2798
www.extensionarchitecture.co.uk

This drawing is prepared solely for design and planning submission purposes. It is not intended or suitable for either building regulations or construction purposes and should not be used for such. All dimension shall be check and confirmed with site rep. and any discrepancies between the drawings and site shall be reported to PM. This drawing to be read in conjunction with engineers specification and details.
For construction information please refer to all drawings and specification of works.

For any structural steelworks details please refer to structural engineer's drawings & calculations.

The copyright of the drawing and designs remains with Extension Architecture. All copies are only for information about the application, they may not be used for any other purpose without the express written permission of Extension Architecture.

CLIENT: Vik Barodia

PROJECT: 1 Lambourne Drive, KT11 3LB

TITLE: **Existing & Proposed Rear Elevation**

NOTES

VERSION	DESCRIPTION	DATE


SCALE: **1:100**

DATE: **01.08.2024**

DRAWN: **BOUSIA**

VERSION


SHEET REF. NO: **1LD-TD-08**

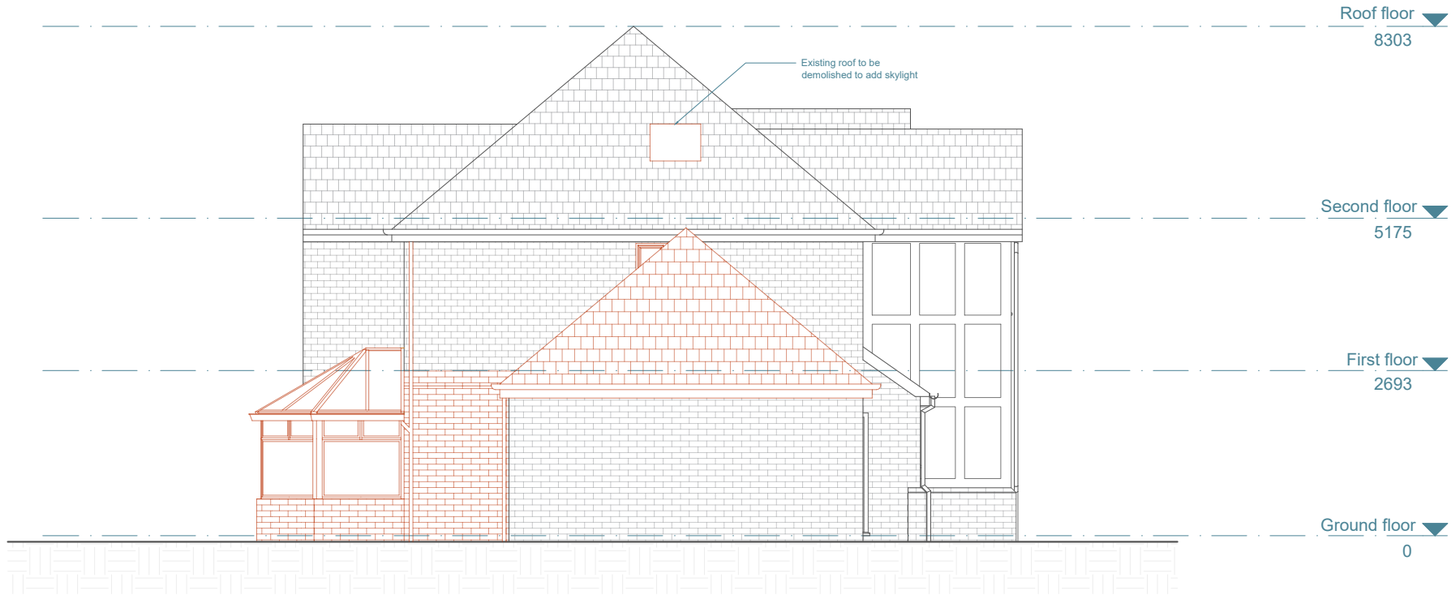

EXISTING LEFT ELEVATION

ELEVATION KEYS

- PROPOSED ROOF
- PROPOSED WALL
- PROPOSED RAIN WATER PIPE
- EXISTING GUTTERING
- PROPOSED GUTTERING
- EXISTING & PROPOSED SOIL VENT PIPE

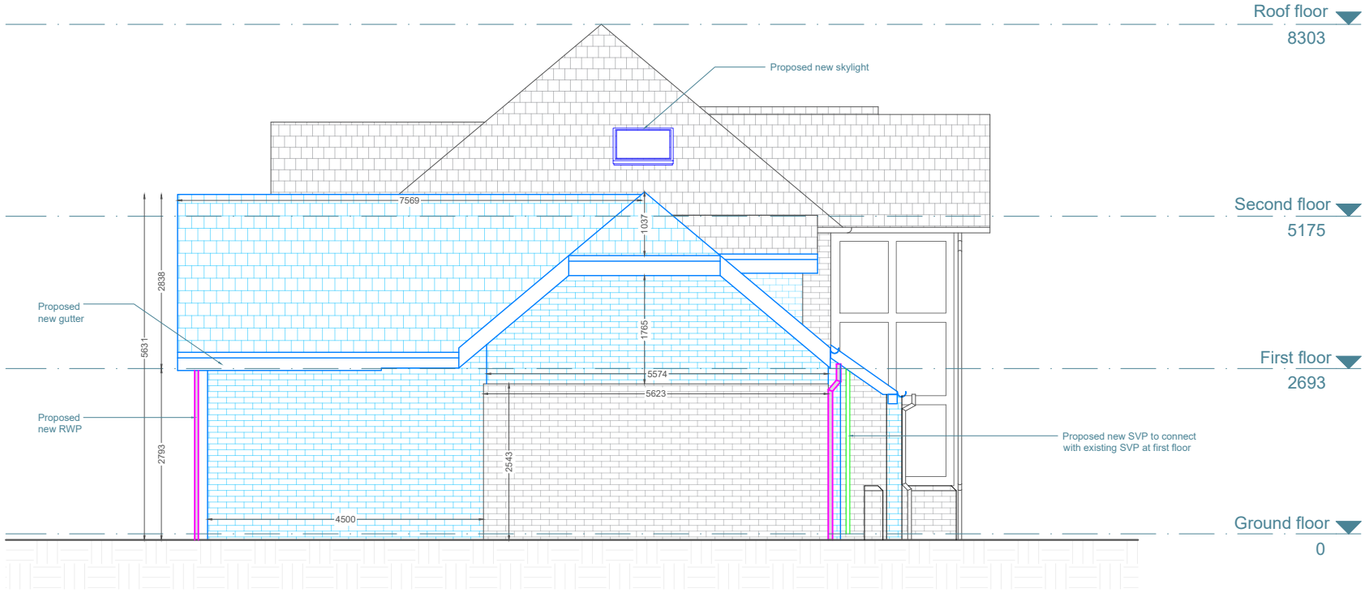

PROPOSED LEFT ELEVATION

Scale 1:100 @A3 0 1 2 3 4 5m

Scale 1:50 @A3 0 0.5 1 1.5 2 2.5m

Scale 1:20 @A3 0 20 40 60 80 100m


extension architecture
3 River Reach, Gartons Way, Battersea
London SW11 3SX
Tel (0208) 288 8950 Fax (0871) 918 2798
www.extensionarchitecture.co.uk

This drawing is prepared solely for design and planning submission purposes. It is not intended or suitable for either building regulations or construction purposes and should not be used for such. All dimension shall be check and confirmed with site rep. and any discrepancies between the drawings and site shall be reported to PM. This drawing to be read in conjunction with engineers specification and details.
For construction information please refer to all drawings and specification of works.


For any structural steelworks details please refer to structural engineer's drawings & calculations.

The copyright of the drawing and designs remains with Extension Architecture. All copies are only for information about the application, they may not be used for any other purpose without the express written permission of Extension Architecture.

CLIENT: Vik Barodia	NOTES			SCALE: 1:100	DATE: 01.08.2024
PROJECT: 1 Lambourne Drive, KT11 3LB	VERSION	DESCRIPTION	DATE	DRAWN: BOUSIA	VERSION
TITLE: **Existing & Proposed Left Elevation**				SHEET REF. NO: 1LD-TD-09	

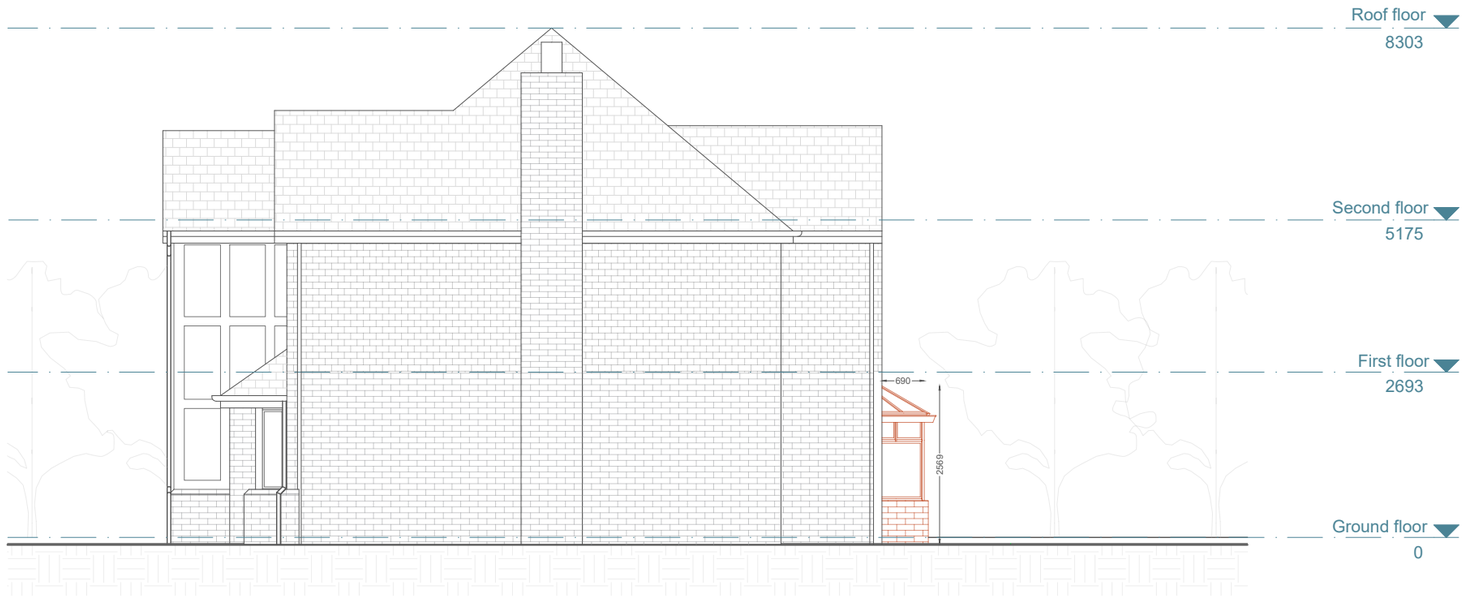

EXISTING RIGHT ELEVATION

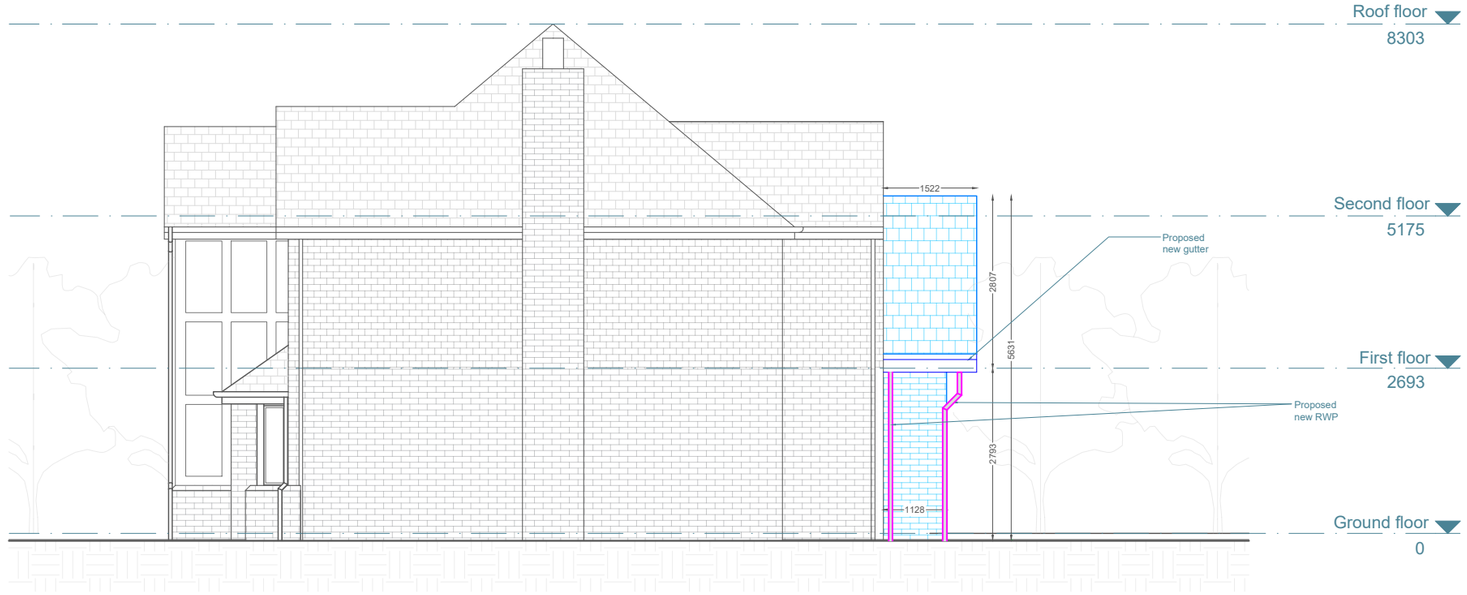

PROPOSED RIGHT ELEVATION

ELEVATION KEYS

- PROPOSED ROOF
- PROPOSED WALL
- PROPOSED RAIN WATER PIPE
- EXISTING GUTTERING
- PROPOSED GUTTERING
- EXISTING & PROPOSED SOIL VENT PIPE

Scale 1:100 @A3 0 1 2 3 4 5m

Scale 1:50 @A3 0 0.5 1 1.5 2 2.5m

Scale 1:20 @A3 0 20 40 60 80 100m


extension architecture
3 River Reach, Gartons Way, Battersea
London SW11 3SX
Tel (0208) 288 8950 Fax (0871) 918 2798
www.extensionarchitecture.co.uk

This drawing is prepared solely for design and planning submission purposes. It is not intended or suitable for either building regulations or construction purposes and should not be used for such. All dimension shall be check and confirmed with site rep. and any discrepancies between the drawings and site shall be reported to PM. This drawing to be read in conjunction with engineers specification and details.
For construction information please refer to all drawings and specification of works.

For any structural steelworks details please refer to structural engineer's drawings & calculations.

The copyright of the drawing and designs remains with Extension Architecture. All copies are only for information about the application, they may not be used for any other purpose without the express written permission of Extension Architecture.


CLIENT: Vik Barodia	NOTES			SCALE: 1:100	DATE: 01.08.2024
PROJECT: 1 Lambourne Drive, KT11 3LB	VERSION	DESCRIPTION	DATE	DRAWN: BOUSIA	VERSION
TITLE: **Existing & Proposed Right Elevation**				SHEET REF. NO: 1LD-TD-10	

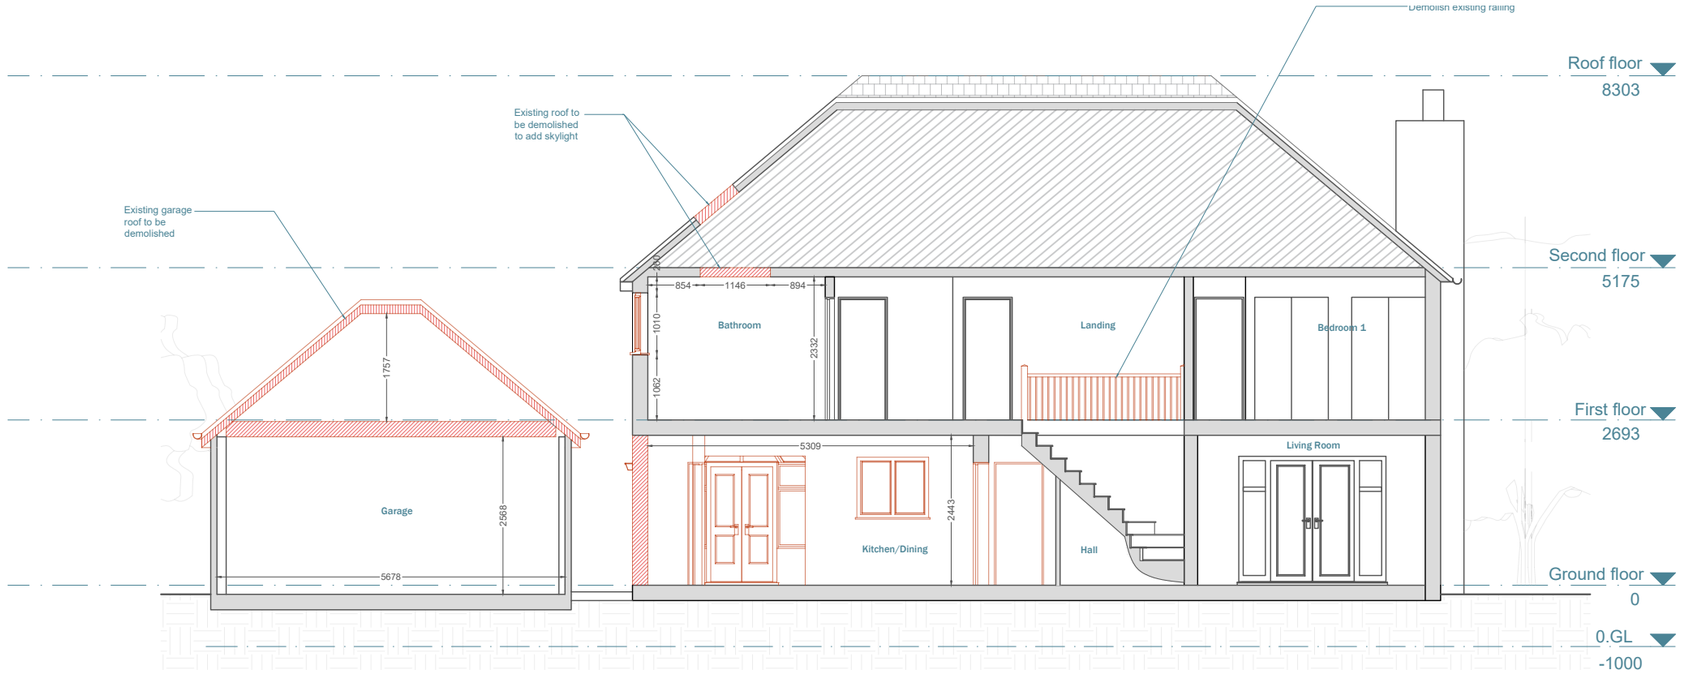

EXISTING SECTION - AA

SECTION KEYS

- EXISTING ROOF
- PROPOSED ROOF
- PROPOSED WALL
- DEMOLITION

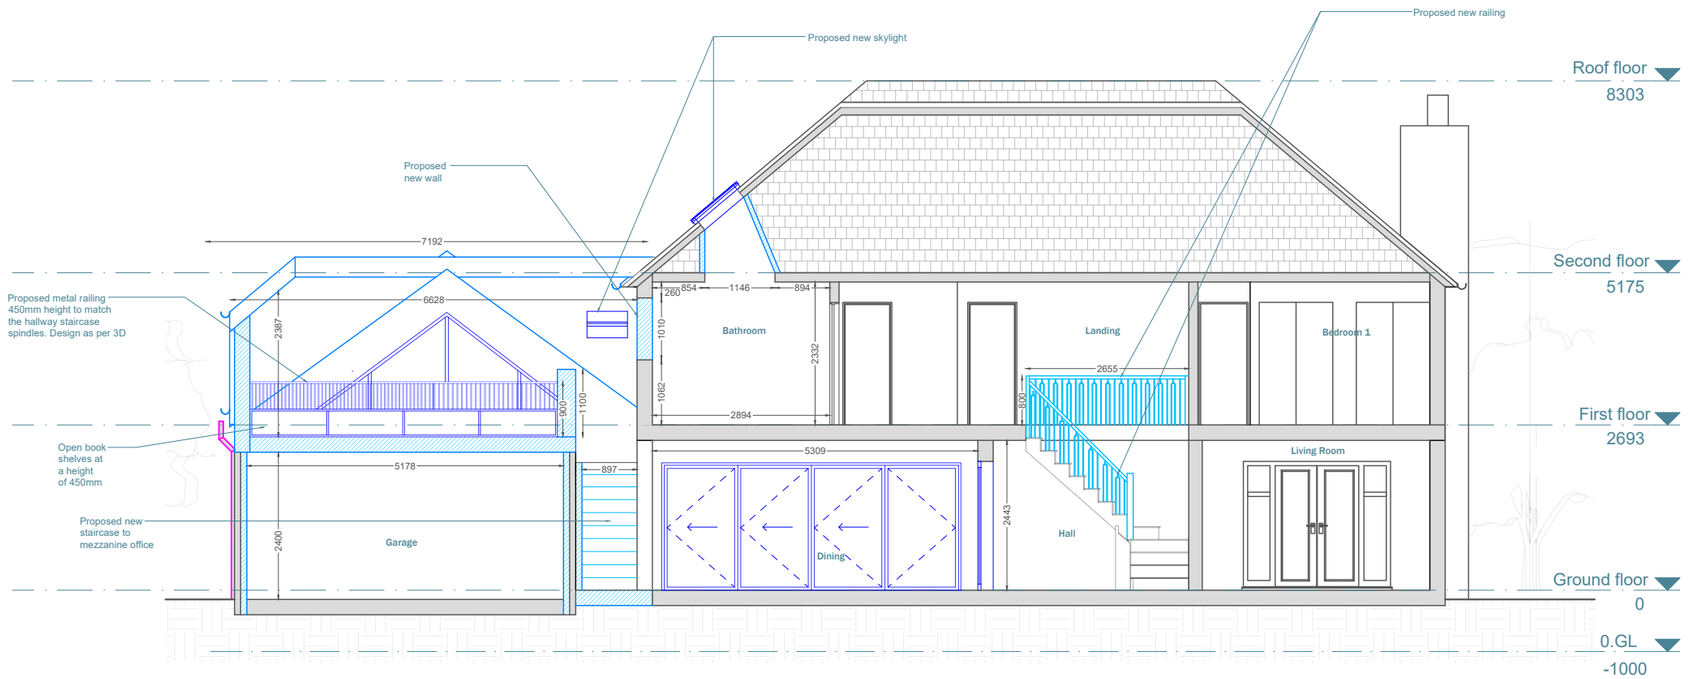

PROPOSED SECTION - AA

Scale 1:100 @A3 0 1 2 3 4 5m

Scale 1:50 @A3 0 0.5 1 1.5 2 2.5m

Scale 1:20 @A3 0 20 40 60 80 100m


extension architecture
3 River Reach, Gartons Way, Battersea
London SW11 3SX
Tel (0208) 288 8950 Fax (0871) 918 2798
www.extensionarchitecture.co.uk

This drawing is prepared solely for design and planning submission purposes. It is not intended or suitable for either building regulations or construction purposes and should not be used for such. All dimension shall be check and confirmed with site rep. and any discrepancies between the drawings and site shall be reported to PM. This drawing to be read in conjunction with engineers specification and details.
For construction information please refer to all drawings and specification of works.

For any structural steelworks details please refer to structural engineer's drawings & calculations.

The copyright of the drawing and designs remains with Extension Architecture. All copies are only for information about the application, they may not be used for any other purpose without the express written permission of Extension Architecture.


CLIENT: Vik Barodia	NOTES			SCALE: 1:100	DATE: 01.08.2024
PROJECT: 1 Lambourne Drive, KT11 3LB	VERSION	DESCRIPTION	DATE	DRAWN: BOUSIA	VERSION
TITLE: Existing & Proposed Section A-A				SHEET REF. NO: 1LD-TD-11	

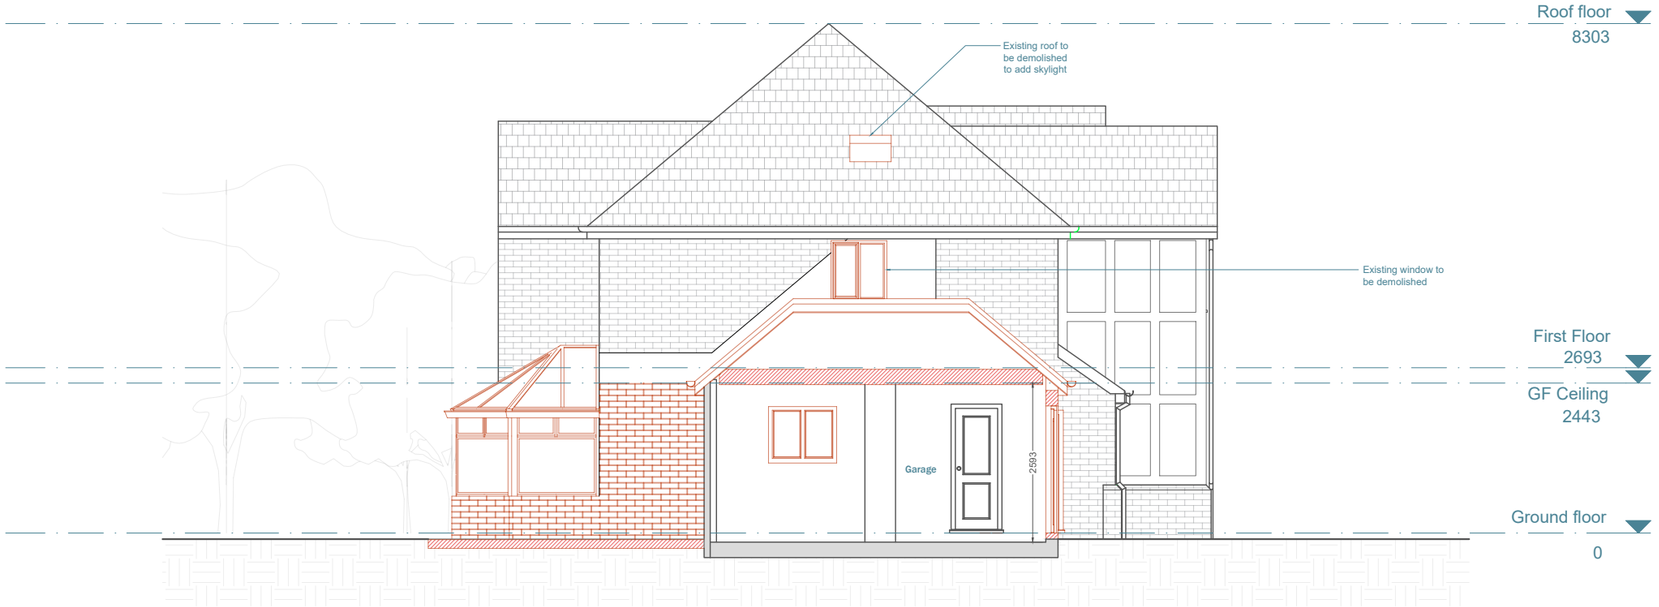

PROPOSED SECTION - BB

SECTION KEYS

- EXISTING ROOF
- PROPOSED ROOF
- PROPOSED WALL
- DEMOLITION

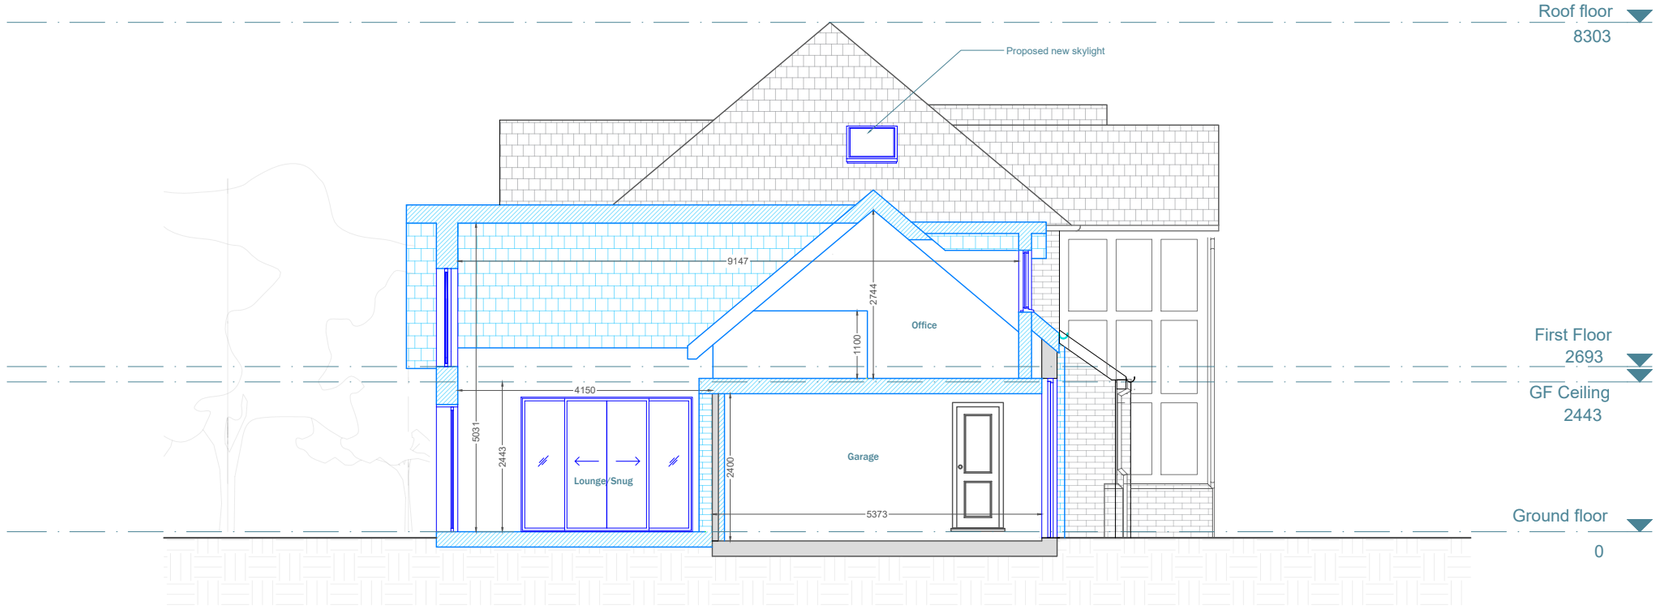

PROPOSED SECTION - BB

Scale 1:100 @A3 0 1 2 3 4 5m

Scale 1:50 @A3 0 0.5 1 1.5 2 2.5m

Scale 1:20 @A3 0 20 40 60 80 100m

extension architecture
3 River Reach, Gartons Way, Battersea
London SW11 3SX
Tel (0208) 288 8950 Fax (0871) 918 2798
www.extensionarchitecture.co.uk

This drawing is prepared solely for design and planning submission purposes. It is not intended or suitable for either building regulations or construction purposes and should not be used for such. All dimension shall be check and confirmed with site rep. and any discrepancies between the drawings and site shall be reported to PM. This drawing to be read in conjunction with engineers specification and details.
For construction information please refer to all drawings and specification of works.

For any structural steelworks details please refer to structural engineer's drawings & calculations.

The copyright of the drawing and designs remains with Extension Architecture. All copies are only for information about the application, they may not be used for any other purpose without the express written permission of Extension Architecture.

CLIENT: Vik Barodia

PROJECT: 1 Lambourne Drive, KT11 3LB

TITLE: **Existing & Proposed Section B-B**

NOTES

VERSION	DESCRIPTION	DATE

SCALE: **1:100**

DATE: **01.08.2024**


DRAWN: **BOUSIA**

VERSION


SHEET REF. NO: **1LD-TD-12**

NOTE:


*INTERNAL DIMENSIONS TBC DEPENDING ON THE SIZE OF MEDIA APPLIANCES

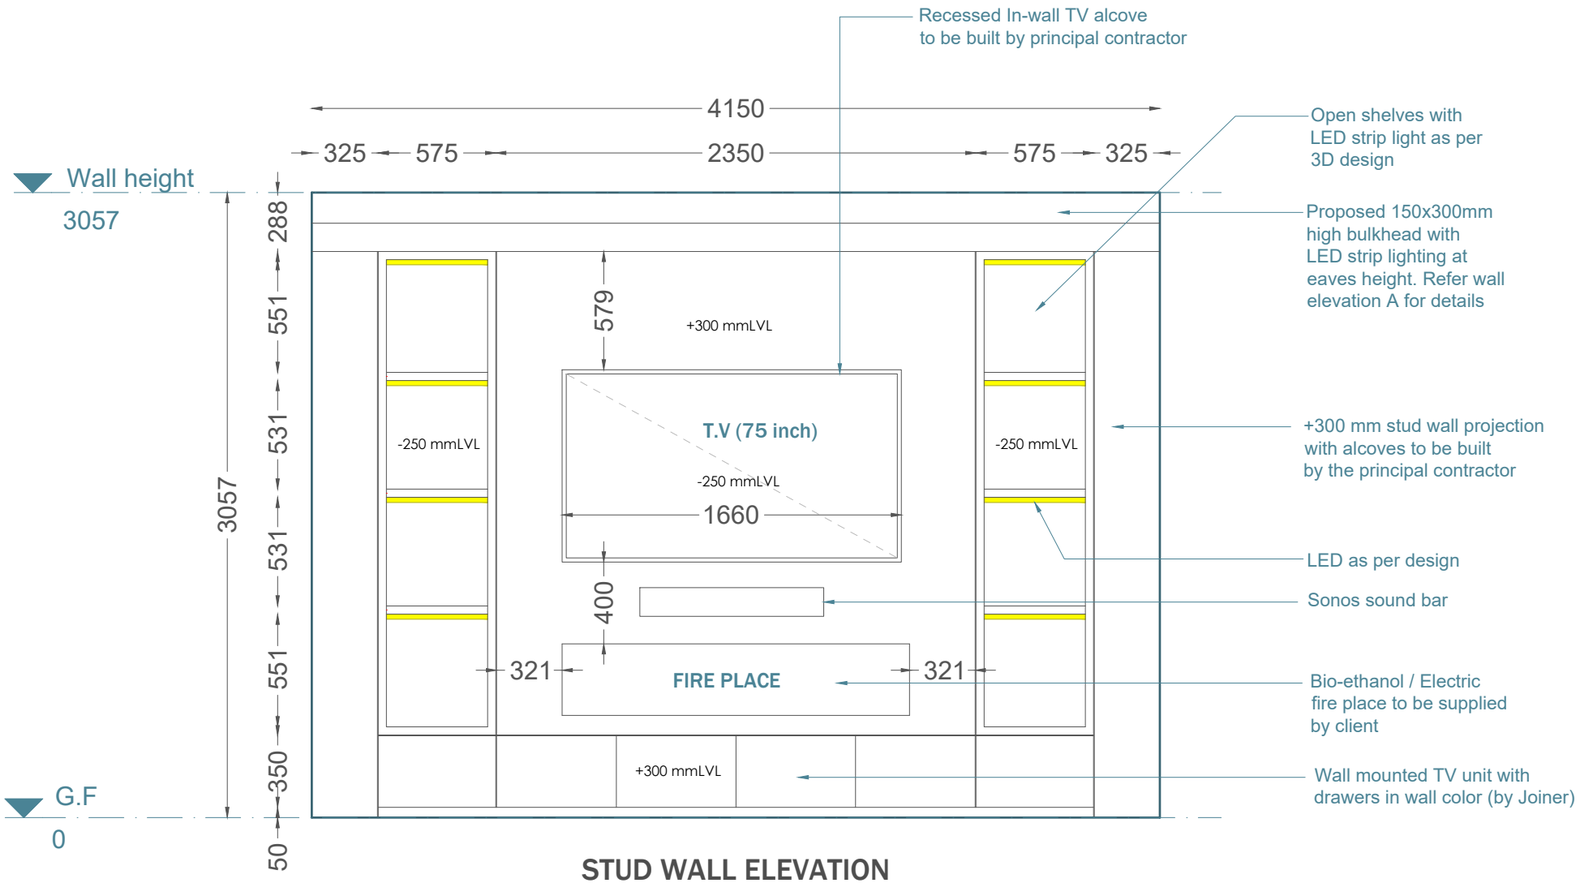


STUD WALL ELEVATION

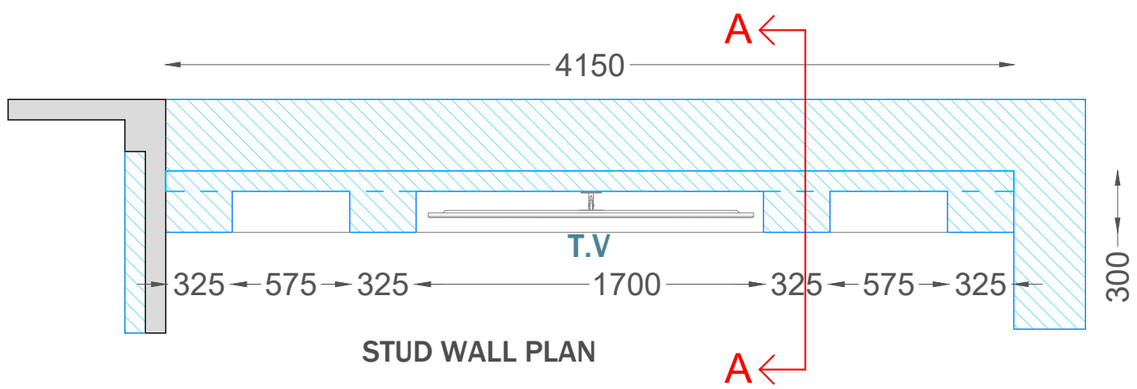

STUD WALL PLAN

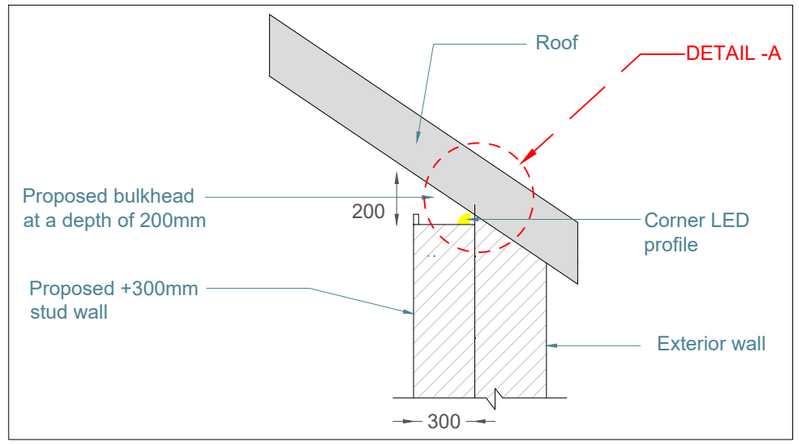

SECTION - AA, SCALE - 1:20

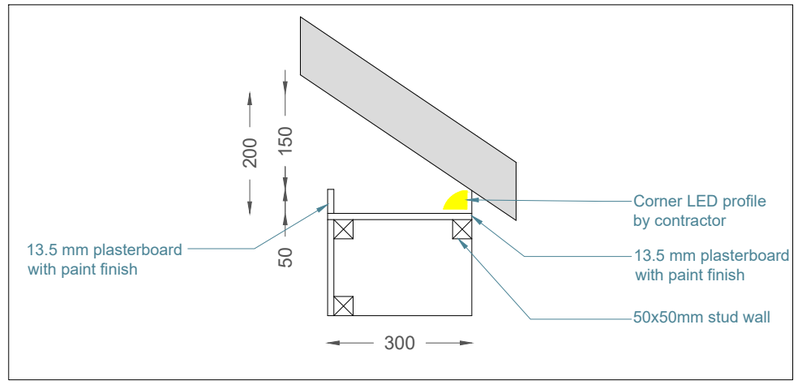

DETAIL - A, SCALE - 1:5



Reference render image

Scale 1:100 @A3 0 1 2 3 4 5m

Scale 1:50 @A3 0 0.5 1 1.5 2 2.5m

Scale 1:20 @A3 0 20 40 60 80 100m


extension architecture
3 River Reach, Gartons Way, Battersea
London SW11 3SX
Tel (0208) 288 8950 Fax (0871) 918 2798
www.extensionarchitecture.co.uk

This drawing is prepared solely for design and planning submission purposes. It is not intended or suitable for either building regulations or construction purposes and should not be used for such. All dimension shall be check and confirmed with site rep. and any discrepancies between the drawings and site shall be reported to PM. This drawing to be read in conjunction with engineers specification and details.
For construction information please refer to all drawings and specification of works.


For any structural steelworks details please refer to structural engineer's drawings & calculations.

The copyright of the drawing and designs remains with Extension Architecture. All copies are only for information about the application, they may not be used for any other purpose without the express written permission of Extension Architecture.

CLIENT Vik Barodia	NOTES			SCALE 1:30	DATE 01.08.2024	
PROJECT 1 Lambourne Drive, KT11 3LB	VERSION	DESCRIPTION	DATE	DRAWN BOUSIA	VERSION	
TITLE **Stud wall internal elevation detail (1/3)**				SHEET REF. NO 1LD-TD-13		

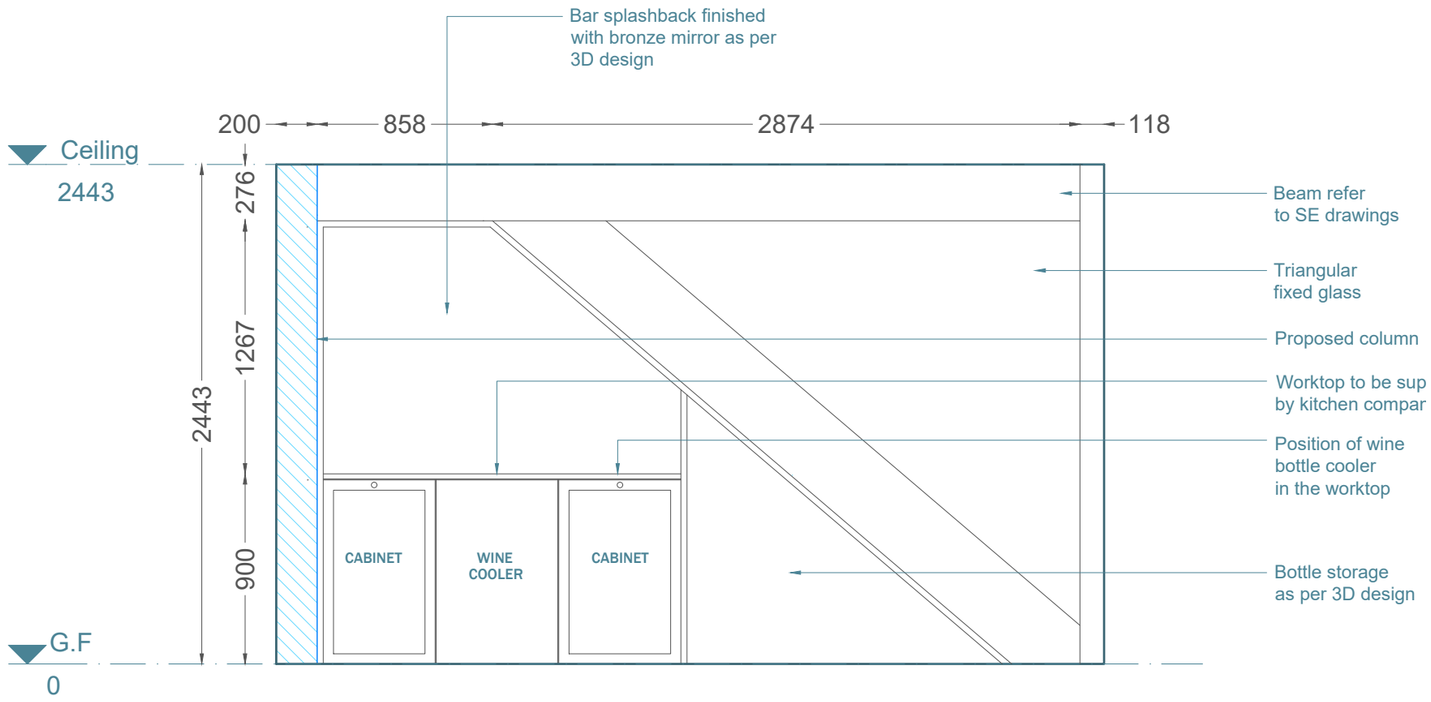

WALL ELEVATION - B

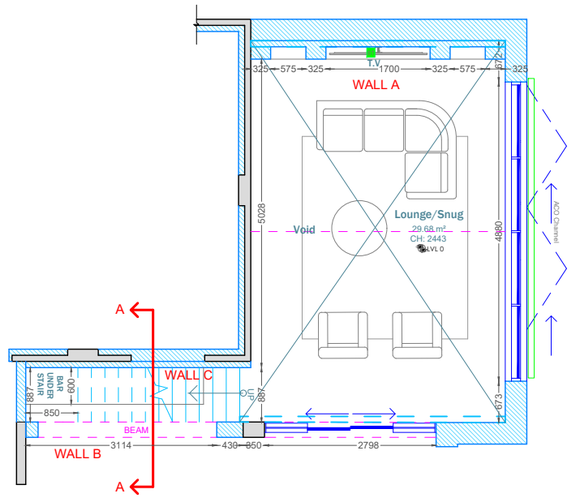

KEY PLAN - 1:100





Reference render image

Scale 1:100 @A3 0 1 2 3 4 5m

Scale 1:50 @A3 0 0.5 1 1.5 2 2.5m

Scale 1:20 @A3 0 20 40 60 80 100m


extension architecture
3 River Reach, Gartons Way, Battersea
London SW11 3SX
Tel (0208) 288 8950 Fax (0871) 918 2798
www.extensionarchitecture.co.uk

This drawing is prepared solely for design and planning submission purposes. It is not intended or suitable for either building regulations or construction purposes and should not be used for such. All dimension shall be check and confirmed with site rep. and any discrepancies between the drawings and site shall be reported to PM. This drawing to be read in conjunction with engineers specification and details.
For construction information please refer to all drawings and specification of works.


For any structural steelworks details please refer to structural engineer's drawings & calculations.

The copyright of the drawing and designs remains with Extension Architecture. All copies are only for information about the application, they may not be used for any other purpose without the express written permission of Extension Architecture.


CLIENT: Vik Barodia	NOTES			SCALE: 1:30	DATE: 01.08.2024
PROJECT: 1 Lambourne Drive, KT11 3LB	VERSION	DESCRIPTION	DATE	DRAWN: BOUSIA	VERSION
TITLE: Internal wall elevation detail (2/3)				SHEET REF. NO: 1LD-TD-14	

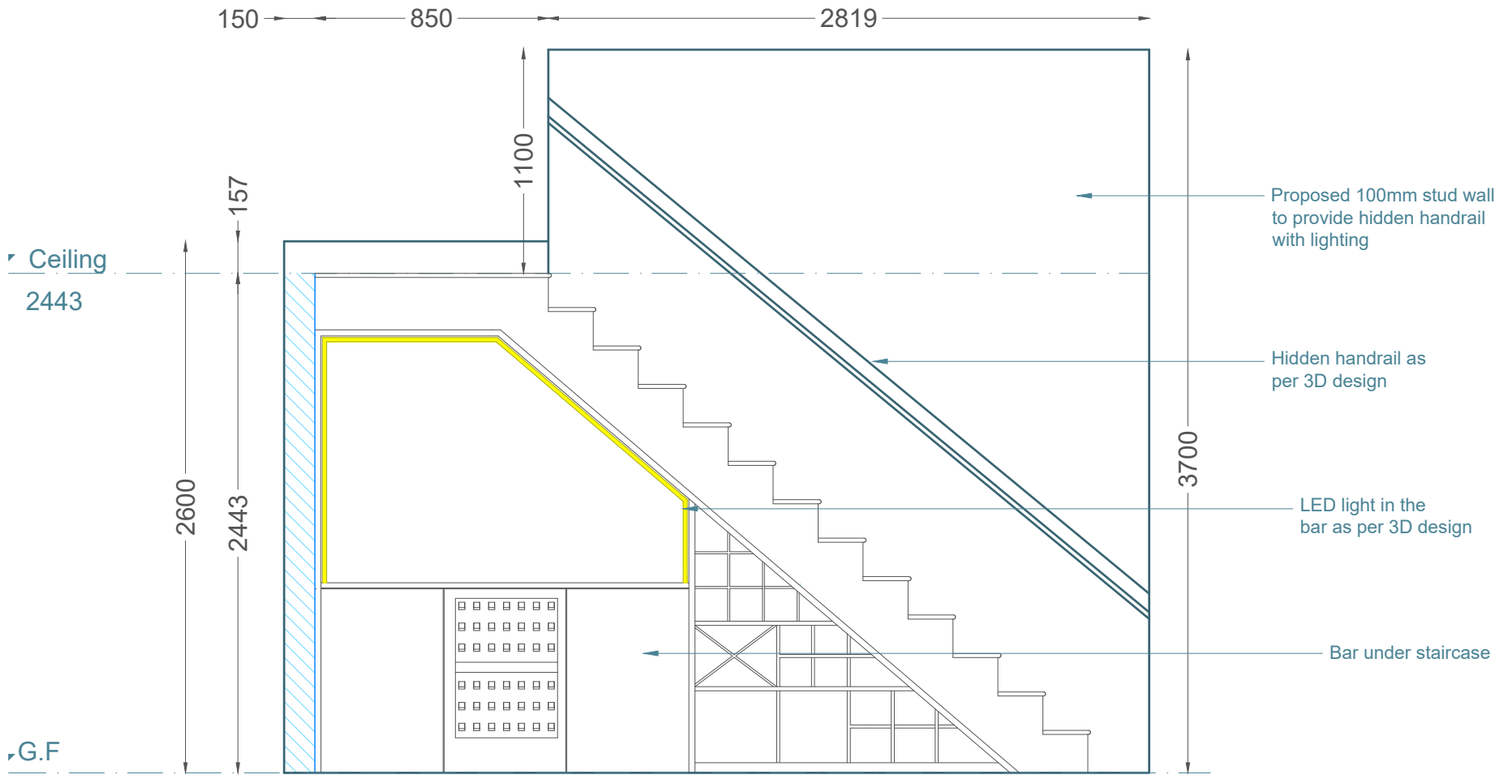

STAIRCASE SECTIONAL ELEVATION - AA

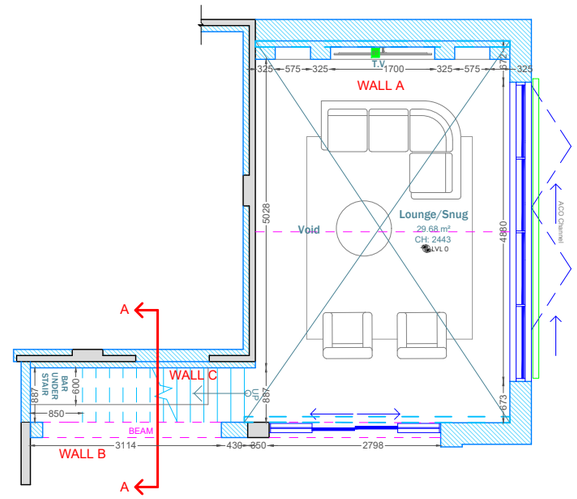

KEY PLAN - 1:100

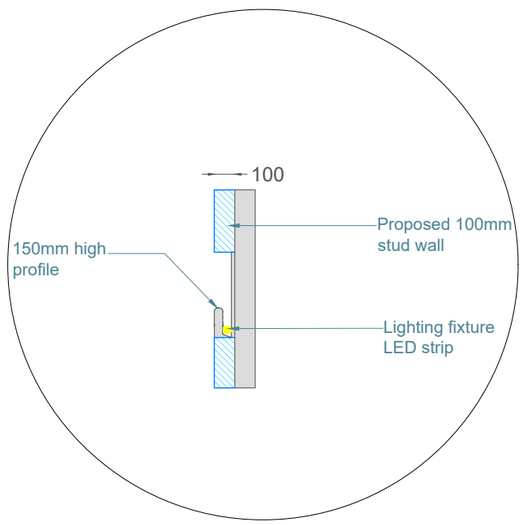

HIDDEN HANDRAIL DETAIL - AA



Hidden handrail reference image



Reference render image

Scale 1:100 @A3 0 1 2 3 4 5m
Scale 1:50 @A3 0 0.5 1 1.5 2 2.5m
Scale 1:20 @A3 0 20 40 60 80 100m

extension architecture
3 River Reach, Gartons Way, Battersea
London SW11 3SX
Tel (0208) 288 8950 Fax (0871) 918 2798
www.extensionarchitecture.co.uk

This drawing is prepared solely for design and planning submission purposes. It is not intended or suitable for either building regulations or construction purposes and should not be used for such. All dimension shall be check and confirmed with site rep. and any discrepancies between the drawings and site shall be reported to PM. This drawing to be read in conjunction with engineers specification and details.
For construction information please refer to all drawings and specification of works.

For any structural steelworks details please refer to structural engineer's drawings & calculations.

The copyright of the drawing and designs remains with Extension Architecture. All copies are only for information about the application, they may not be used for any other purpose without the express written permission of Extension Architecture.

CLIENT: Vik Barodia	NOTES			SCALE: 1:30	DATE: 01.08.2024
PROJECT: 1 Lambourne Drive, KT11 3LB	VERSION	DESCRIPTION	DATE	DRAWN: BOUSIA	VERSION
TITLE: **Wall elevation detail (2/2)**				SHEET REF. NO: 1LD-TD-15	

ROOF FINISH SPECIFICATION

Hatch	Type	Approx. m^2	Supply & Installation
	Proposed brown clay roof tile to match existing roof tile. Angle as per drawings	57 m^2	Contractor
	Proposed GRP Flat roof	5 m^2	Contractor
	Proposed rain water guttering		Contractor
RWP	Proposed Rain Water Pipe		Contractor
SVP	Soil Vent Pipe		Contractor
	Eurodec 50-75mm Twice Weathered Coping Stone 600mm x 300mm - Brick Red	2 m^2	Contractor




Eurodec 50-75mm Twice Weathered Coping Stone 600mm x 300mm - Brick Red



Hopper head

Supply: Contractor
Installation: Contractor

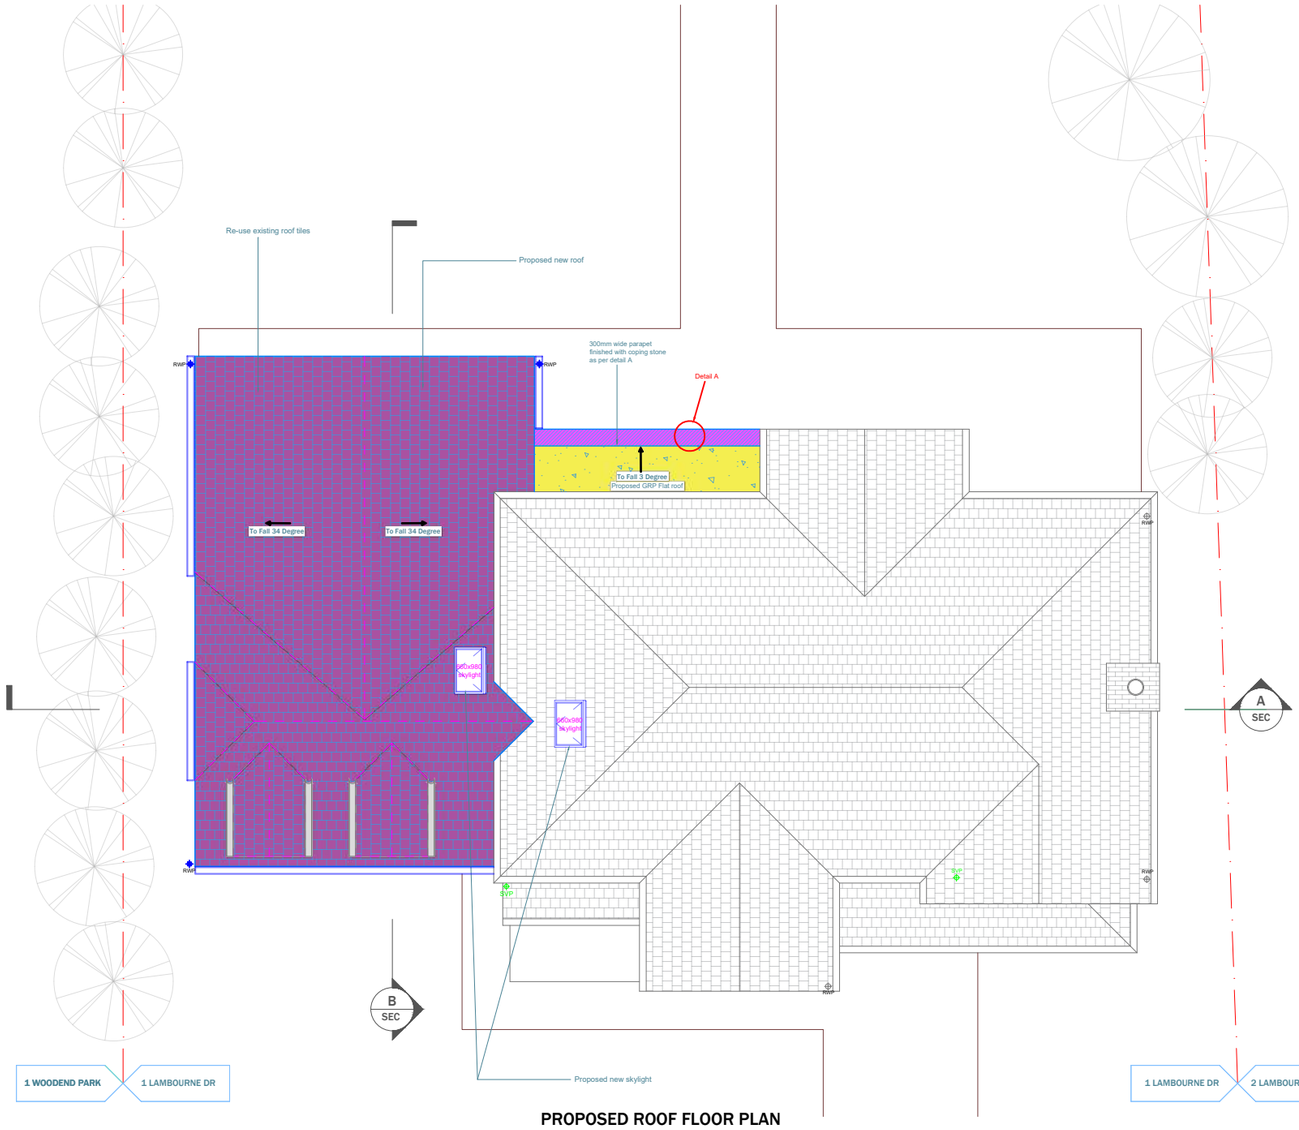

PROPOSED ROOF FLOOR PLAN



Reference image

Flat GRP roof

Supply: Contractor
Installation: Contractor



Reference image

Guttering
UPVC guttering, curved shape - Grey Finish

Supply: Contractor
Installation: Contractor



Reference site image

Clay brown roof tile
clay roof tiles to match existing

Supply: Contractor
Installation: Contractor

Scale 1:100 @A3 0 1 2 3 4 5m
Scale 1:50 @A3 0 0.5 1 1.5 2 2.5m
Scale 1:20 @A3 0 20 40 60 80 100m

extension architecture
3 River Reach, Gartons Way, Battersea
London SW11 3SX
Tel (0208) 288 8950 Fax (0871) 918 2798
www.extensionarchitecture.co.uk

This drawing is prepared solely for design and planning submission purposes. It is not intended or suitable for either building regulations or construction purposes and should not be used for such. All dimension shall be check and confirmed with site rep. and any discrepancies between the drawings and site shall be reported to PM. This drawing to be read in conjunction with engineers specification and details.
For construction information please refer to all drawings and specification of works.

For any structural steelworks details please refer to structural engineer's drawings & calculations.

The copyright of the drawing and designs remains with Extension Architecture. All copies are only for information about the application, they may not be used for any other purpose without the express written permission of Extension Architecture.

CLIENT: Vik Barodia
PROJECT: 1 Lambourne Drive, KT11 3LB
TITLE: **Roof Specification**

NOTES

VERSION	DESCRIPTION	DATE

SCALE
DATE: **01.08.2024**
DRAWN: **BOUSIA**
VERSION
SHEET REF. NO: **1LD-TD-16**


FRONT ELEVATION - EXTERNAL FINISH SPECIFICATION

Hatch	Type	Approx. m^2	Supply	Installation
	*Exposed red brick wall to match the existing site condition	4 m^2	Contractor	Contractor
	Wall hung tile as per site image	4 m^2	Contractor	Contractor
	Brown clay roof tile to match existing roof tile	16 m^2	Contractor	Contractor

* All exposed brick, Brown clay roof tiles to be confirmed at site with the client and the Project Manager prior to supply.



Reference site image for roof tile, Wall hung tile and brick to match the existing

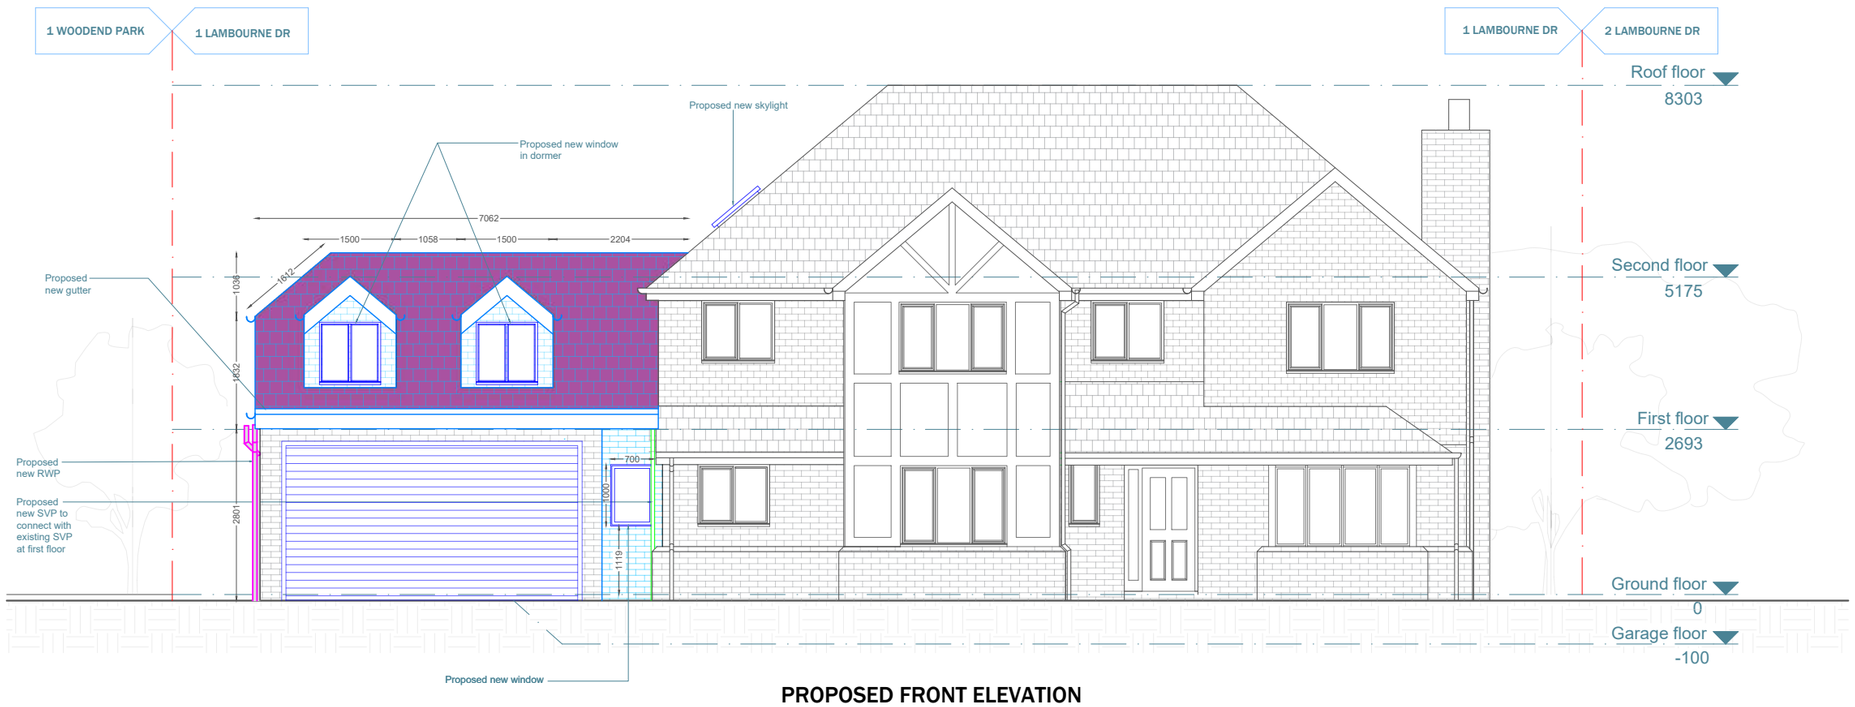

PROPOSED FRONT ELEVATION

Scale 1:100 @A3 0 1 2 3 4 5m

Scale 1:50 @A3 0 0.5 1 1.5 2 2.5m

Scale 1:20 @A3 0 20 40 60 80 100m

extension architecture

3 River Reach, Gartons Way, Battersea
London SW11 3SX

Tel (0208) 288 8950 Fax (0871) 918 2798
www.extensionarchitecture.co.uk

This drawing is prepared solely for design and planning submission purposes. It is not intended or suitable for either building regulations or construction purposes and should not be used for such. All dimension shall be check and confirmed with site rep. and any discrepancies between the drawings and site shall be reported to PM. This drawing to be read in conjunction with engineers specification and details.
For construction information please refer to all drawings and specification of works.

For any structural steelworks details please refer to structural engineer's drawings & calculations.

The copyright of the drawing and designs remains with Extension Architecture. All copies are only for information about the application, they may not be used for any other purpose without the express written permission of Extension Architecture.

CLIENT: Vik Barodia	NOTES			SCALE: 1:100	DATE: 01.08.2024
PROJECT: 1 Lambourne Drive, KT11 3LB	VERSION	DESCRIPTION	DATE	DRAWN: BOUSIA	VERSION
TITLE: **External Specification (1/4)**				SHEET REF. NO: 1LD-TD-17	


REAR ELEVATION - EXTERNAL FINISH SPECIFICATION

Hatch	Type	Approx. m^2	Supply	Installation
	*Exposed red brick wall to match the existing site condition	19 m^2	Contractor	Contractor
	Brown clay roof tile to match existing roof tile	8 m^2	Contractor	Contractor
	Vertical bricks laid to match existing site condition	2 m^2	Contractor	Contractor

* All exposed brick, Brown clay roof tiles to be confirmed at site with the client and the Project Manager prior to supply.



Reference site image for roof tile, vertical brick and brick wall to match the existing

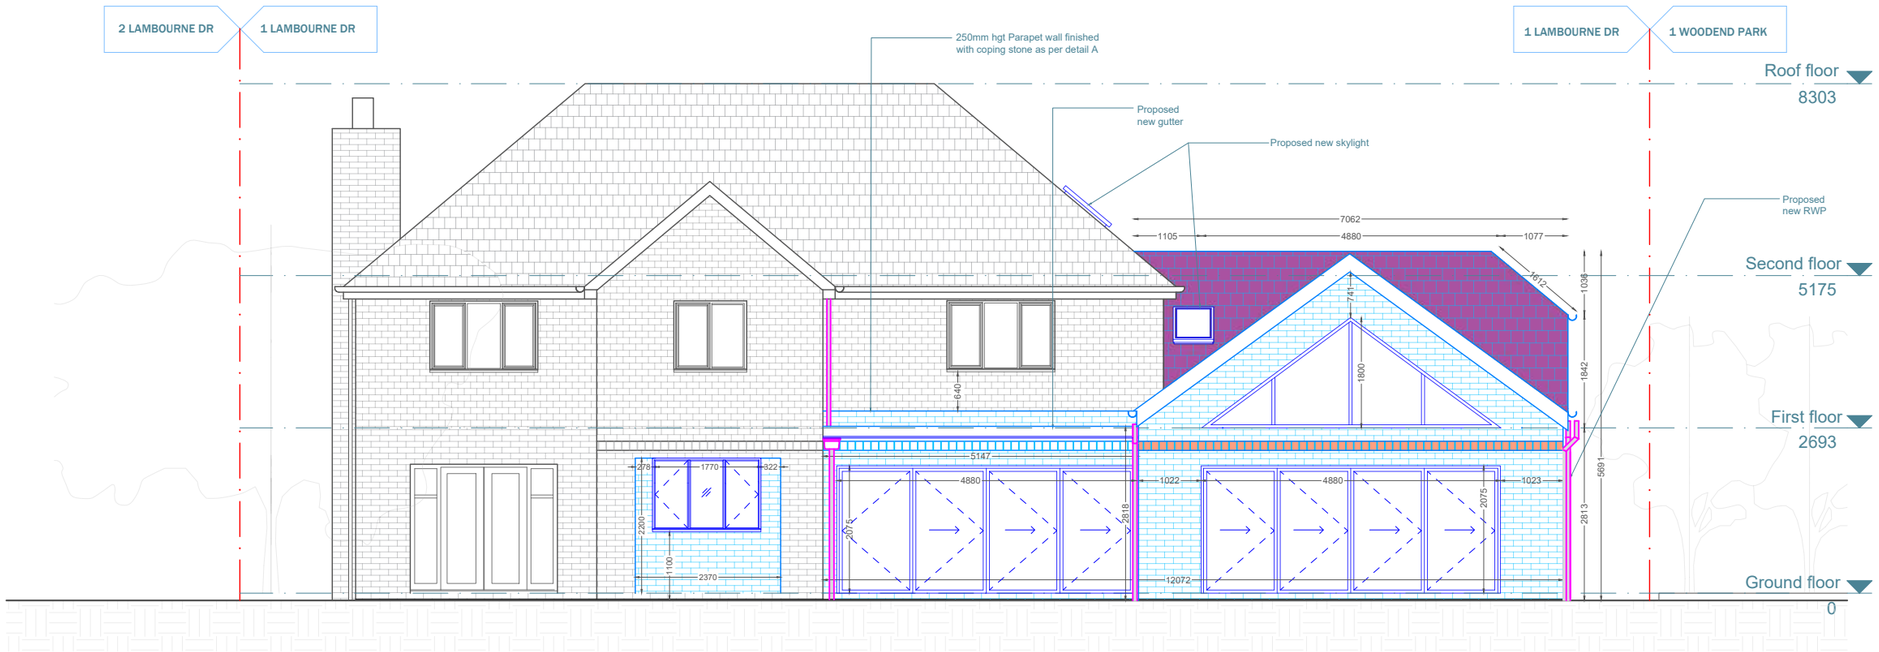

PROPOSED REAR ELEVATION

Scale 1:100 @A3 0 1 2 3 4 5m

Scale 1:50 @A3 0 0.5 1 1.5 2 2.5m

Scale 1:20 @A3 0 20 40 60 80 100m

extension architecture

3 River Reach, Gartons Way, Battersea
London SW11 3SX

Tel (0208) 288 8950 Fax (0871) 918 2798
www.extensionarchitecture.co.uk

This drawing is prepared solely for design and planning submission purposes. It is not intended or suitable for either building regulations or construction purposes and should not be used for such. All dimension shall be check and confirmed with site rep. and any discrepancies between the drawings and site shall be reported to PM. This drawing to be read in conjunction with engineers specification and details.
For construction information please refer to all drawings and specification of works.

For any structural steelworks details please refer to structural engineer's drawings & calculations.

The copyright of the drawing and designs remains with Extension Architecture. All copies are only for information about the application, they may not be used for any other purpose without the express written permission of Extension Architecture.

CLIENT: Vik Barodia	NOTES			SCALE: 1:100	DATE: 01.08.2024
PROJECT: 1 Lambourne Drive, KT11 3LB	VERSION	DESCRIPTION	DATE	DRAWN: BOUSIA	VERSION
TITLE: **External Specification (2/4)**				SHEET REF. NO: 1LD-TD-18	


LEFT ELEVATION - EXTERNAL FINISH SPECIFICATION

Hatch	Type	Approx. m^2	Supply	Installation
	*Exposed red brick wall to match the existing site condition	20 m^2	Contractor	Contractor
	Wall hung tile as per site image	1 m^2	Contractor	Contractor
	Brown clay roof tile to match existing roof tile	16 m^2	Contractor	Contractor

* All exposed brick, Brown clay roof tiles to be confirmed at site with the client and the Project Manager prior to supply.



Reference site image for roof tile and brick to match the existing

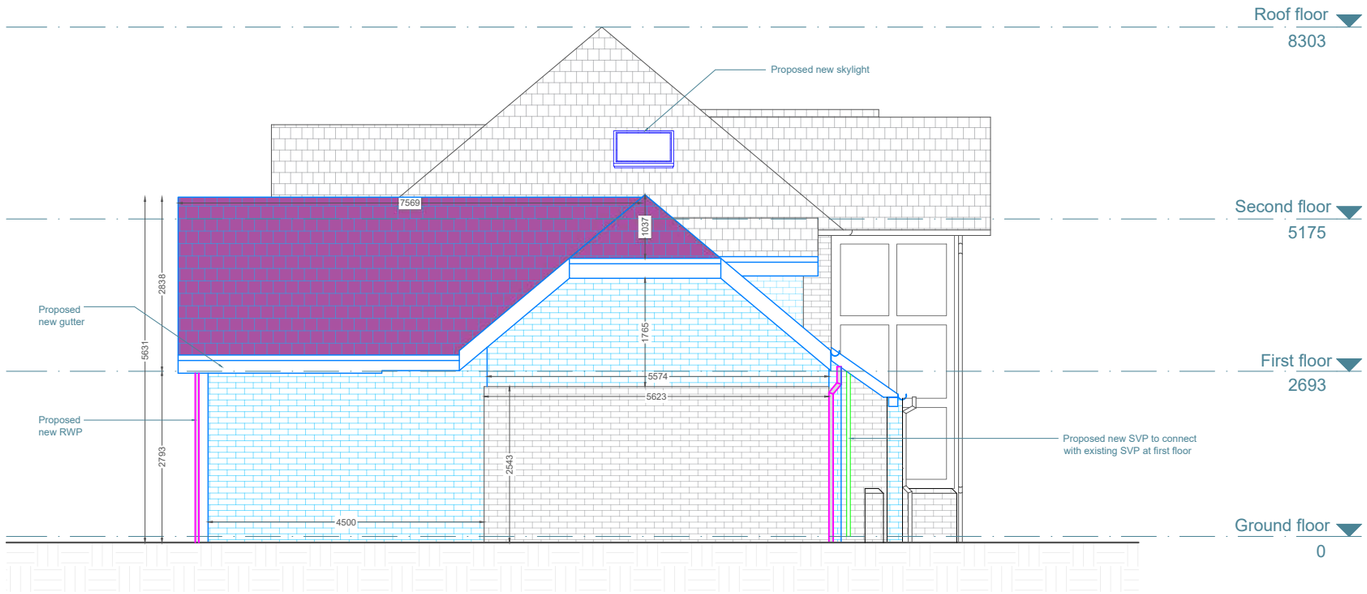

PROPOSED LEFT ELEVATION

Scale 1:100 @A3 0 1 2 3 4 5m

Scale 1:50 @A3 0 0.5 1 1.5 2 2.5m

Scale 1:20 @A3 0 20 40 60 80 100m

extension architecture

3 River Reach, Gartons Way, Battersea
London SW11 3SX

Tel (0208) 288 8950 Fax (0871) 918 2798
www.extensionarchitecture.co.uk

This drawing is prepared solely for design and planning submission purposes. It is not intended or suitable for either building regulations or construction purposes and should not be used for such. All dimension shall be check and confirmed with site rep. and any discrepancies between the drawings and site shall be reported to PM. This drawing to be read in conjunction with engineers specification and details.
For construction information please refer to all drawings and specification of works.

For any structural steelworks details please refer to structural engineer's drawings & calculations.

The copyright of the drawing and designs remains with Extension Architecture. All copies are only for information about the application, they may not be used for any other purpose without the express written permission of Extension Architecture.

CLIENT: Vik Barodia	NOTES			SCALE: 1:100	DATE: 01.08.2024
PROJECT: 1 Lambourne Drive, KT11 3LB	VERSION	DESCRIPTION	DATE	DRAWN: BOUSIA	VERSION
TITLE: **External Specification (3/4)**				SHEET REF. NO: 1LD-TD-19	


RIGHT ELEVATION - EXTERNAL FINISH SPECIFICATION

Hatch	Type	Approx. m^2	Supply	Installation
	*Exposed red brick wall to match the existing site condition	4 m^2	Contractor	Contractor
	Brown clay roof tile to match existing roof tile	4 m^2	Contractor	Contractor

* All exposed brick, Brown clay roof tiles to be confirmed at site with the client and the Project Manager prior to supply.



Reference site image for roof tile and brick to match the existing

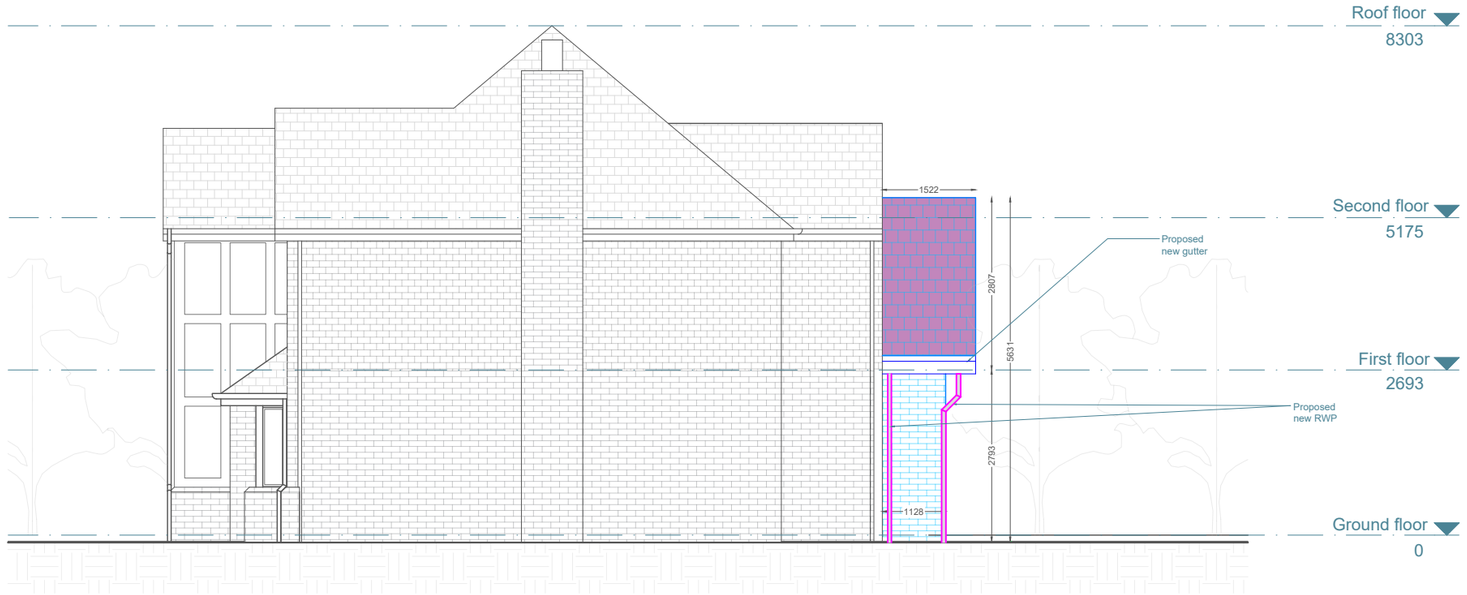

PROPOSED RIGHT ELEVATION

Scale 1:100 @A3 0 1 2 3 4 5m

Scale 1:50 @A3 0 0.5 1 1.5 2 2.5m

Scale 1:20 @A3 0 20 40 60 80 100m

extension architecture

3 River Reach, Gartons Way, Battersea
London SW11 3SX


Tel (0208) 288 8950 Fax (0871) 918 2798
www.extensionarchitecture.co.uk

This drawing is prepared solely for design and planning submission purposes. It is not intended or suitable for either building regulations or construction purposes and should not be used for such. All dimension shall be check and confirmed with site rep. and any discrepancies between the drawings and site shall be reported to PM. This drawing to be read in conjunction with engineers specification and details.
For construction information please refer to all drawings and specification of works.

For any structural steelworks details please refer to structural engineer's drawings & calculations.

The copyright of the drawing and designs remains with Extension Architecture. All copies are only for information about the application, they may not be used for any other purpose without the express written permission of Extension Architecture.

CLIENT Vik Barodia	NOTES			SCALE 1:100	DATE 01.08.2024
PROJECT 1 Lambourne Drive, KT11 3LB	VERSION	DESCRIPTION	DATE	DRAWN BOUSIA	VERSION
TITLE **External Specification (4/4)**				SHEET REF. NO 1LD-TD-20	

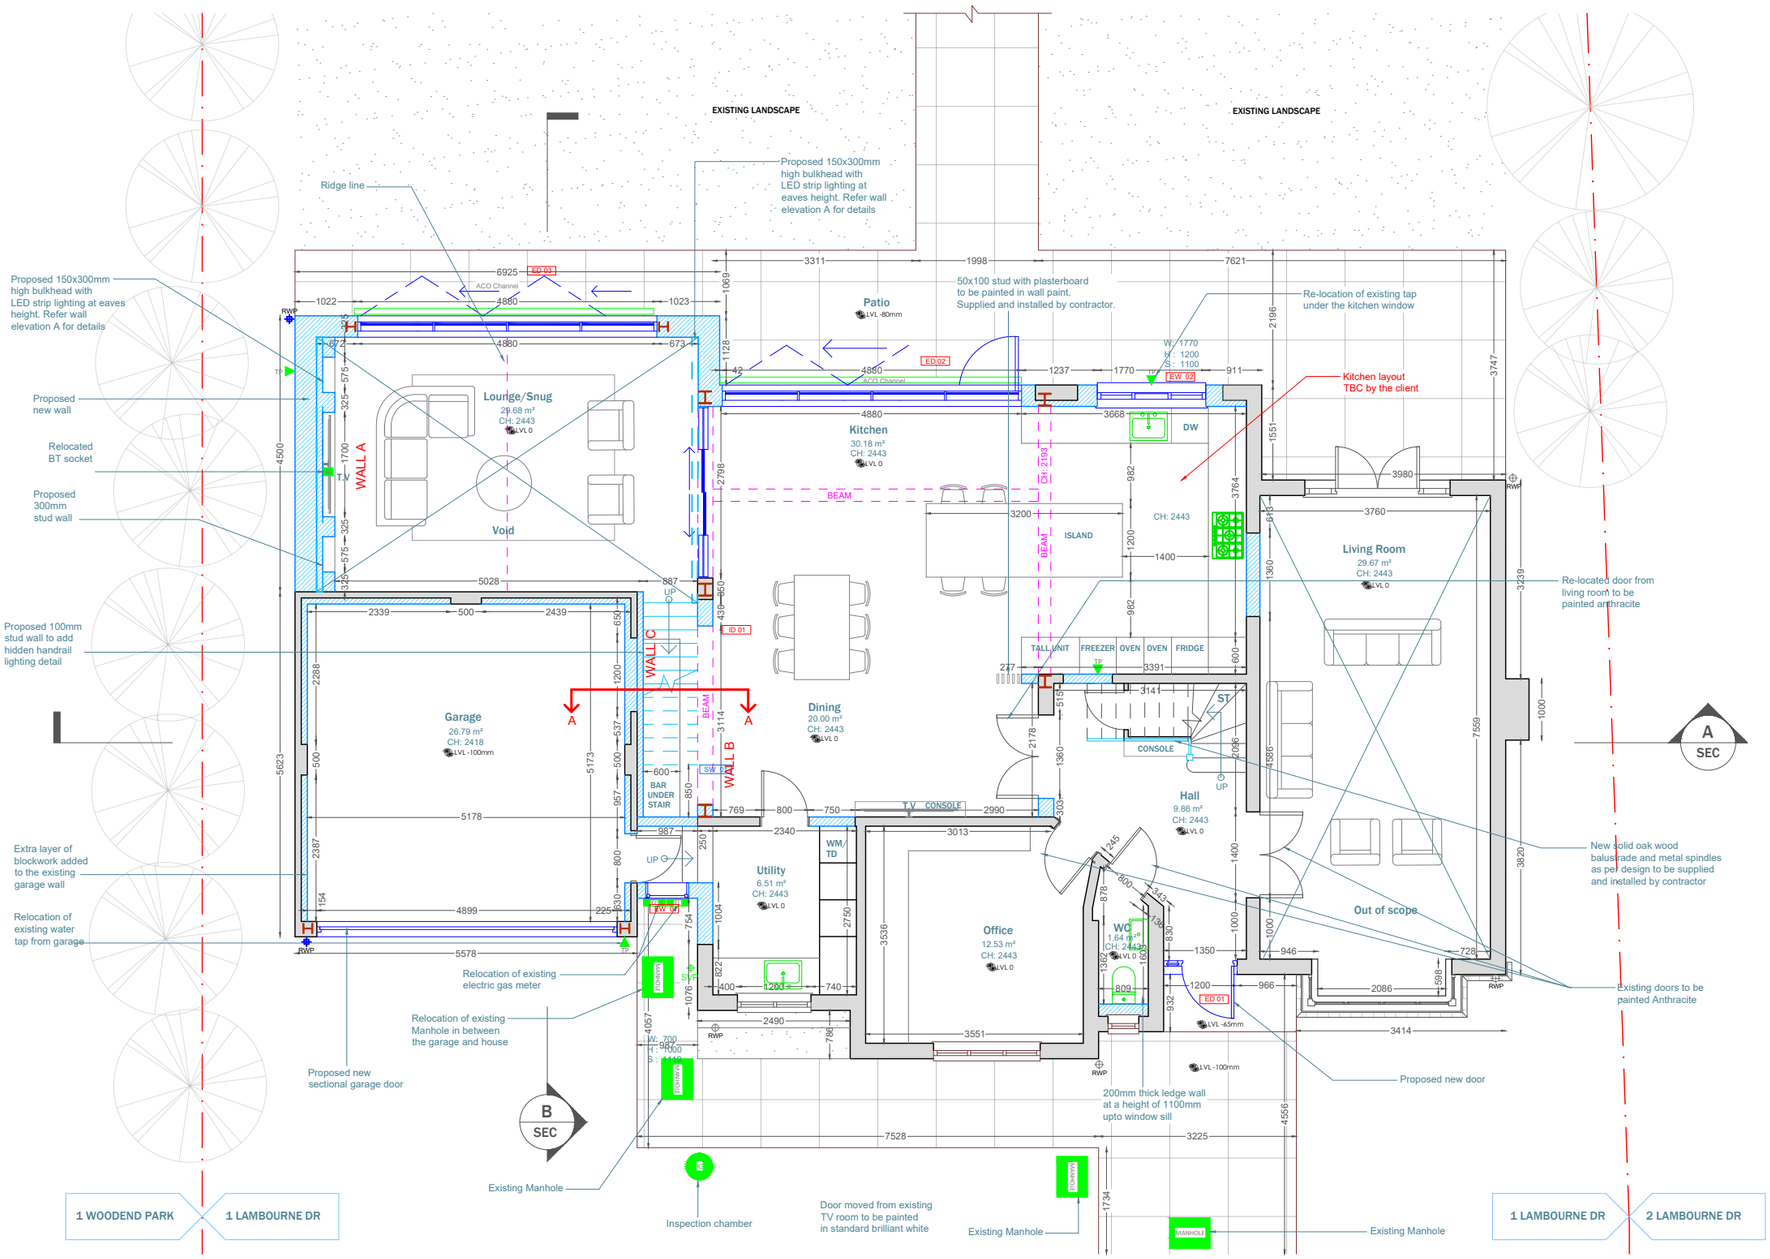

PROPOSED GROUND FLOOR PLAN

Scale 1:100 @A3 0 1 2 3 4 5m
Scale 1:50 @A3 0 0.5 1 1.5 2 2.5m
Scale 1:20 @A3 0 20 40 60 80 100m


extension architecture
3 River Reach, Gartons Way, Battersea
London SW11 3SX
Tel (0208) 288 8950 Fax (0871) 918 2798
www.extensionarchitecture.co.uk

This drawing is prepared solely for design and planning submission purposes. It is not intended or suitable for either building regulations or construction purposes and should not be used for such. All dimension shall be check and confirmed with site rep. and any discrepancies between the drawings and site shall be reported to PM. This drawing to be read in conjunction with engineers specification and details.
For construction information please refer to all drawings and specification of works.

For any structural steelworks details please refer to structural engineer's drawings & calculations.

The copyright of the drawing and designs remains with Extension Architecture. All copies are only for information about the application, they may not be used for any other purpose without the express written permission of Extension Architecture.

CLIENT: Vik Barodia	NOTES			SCALE: 1:100	DATE: 01.08.2024
PROJECT: 1 Lambourne Drive, KT11 3LB	VERSION	DESCRIPTION	DATE	DRAWN: BOUSIA	VERSION
TITLE: Door, Window and Skylight location plan(1/3)				SHEET REF. NO: 1LD-TD-21	

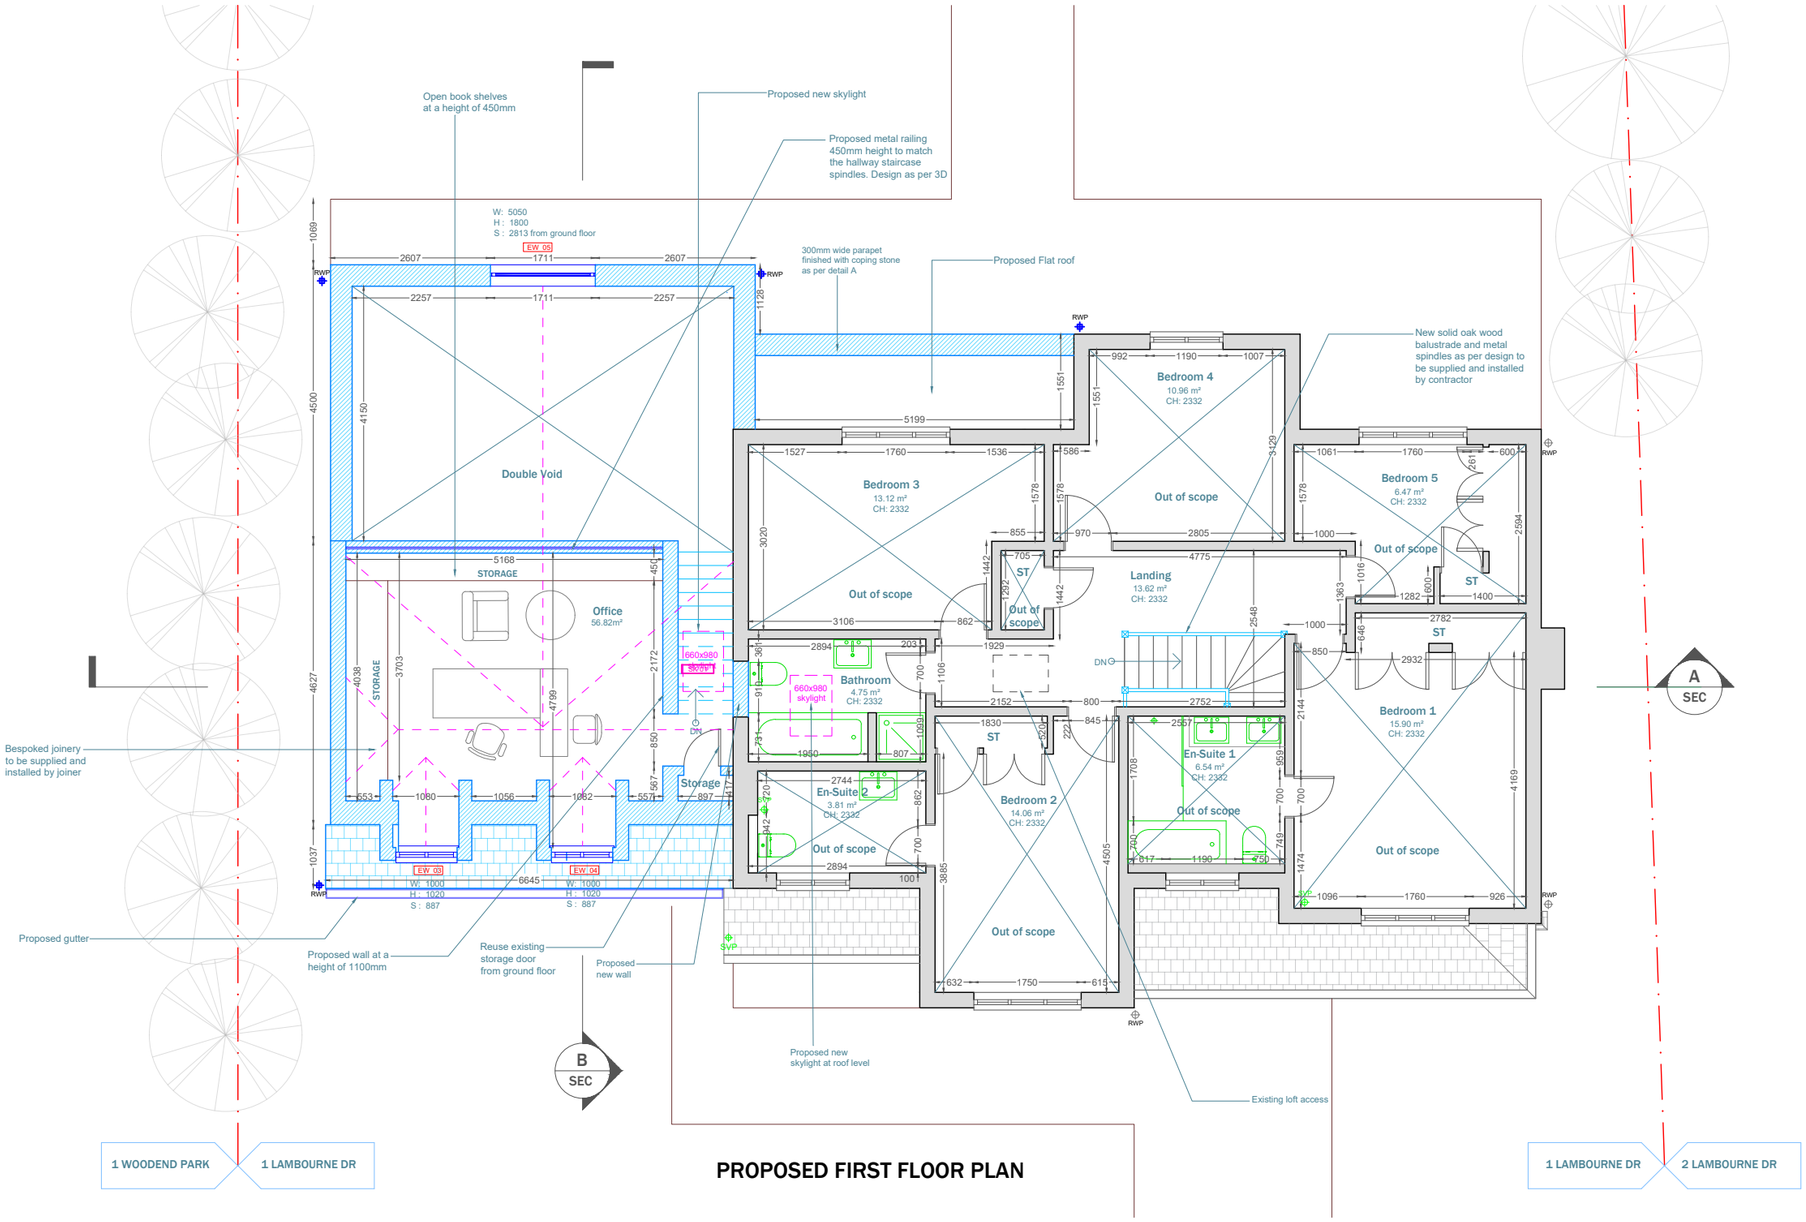

PROPOSED FIRST FLOOR PLAN

Scale 1:100 @A3 0 1 2 3 4 5m
Scale 1:50 @A3 0 0.5 1 1.5 2 2.5m
Scale 1:20 @A3 0 20 40 60 80 100m


extension architecture
3 River Reach, Gartons Way, Battersea
London SW11 3SX
Tel (0208) 288 8950 Fax (0871) 918 2798
www.extensionarchitecture.co.uk

This drawing is prepared solely for design and planning submission purposes. It is not intended or suitable for either building regulations or construction purposes and should not be used for such. All dimension shall be check and confirmed with site rep. and any discrepancies between the drawings and site shall be reported to PM. This drawing to be read in conjunction with engineers specification and details.
For construction information please refer to all drawings and specification of works.

For any structural steelworks details please refer to structural engineer's drawings & calculations.

The copyright of the drawing and designs remains with Extension Architecture. All copies are only for information about the application, they may not be used for any other purpose without the express written permission of Extension Architecture.

CLIENT: Vik Barodia	NOTES			SCALE: 1:100	DATE: 01.08.2024
PROJECT: 1 Lambourne Drive, KT11 3LB	VERSION	DESCRIPTION	DATE	DRAWN: BOUSIA	VERSION
TITLE: Door, Window and Skylight location plan(2/3)				SHEET REF. NO: 1LD-TD-22	

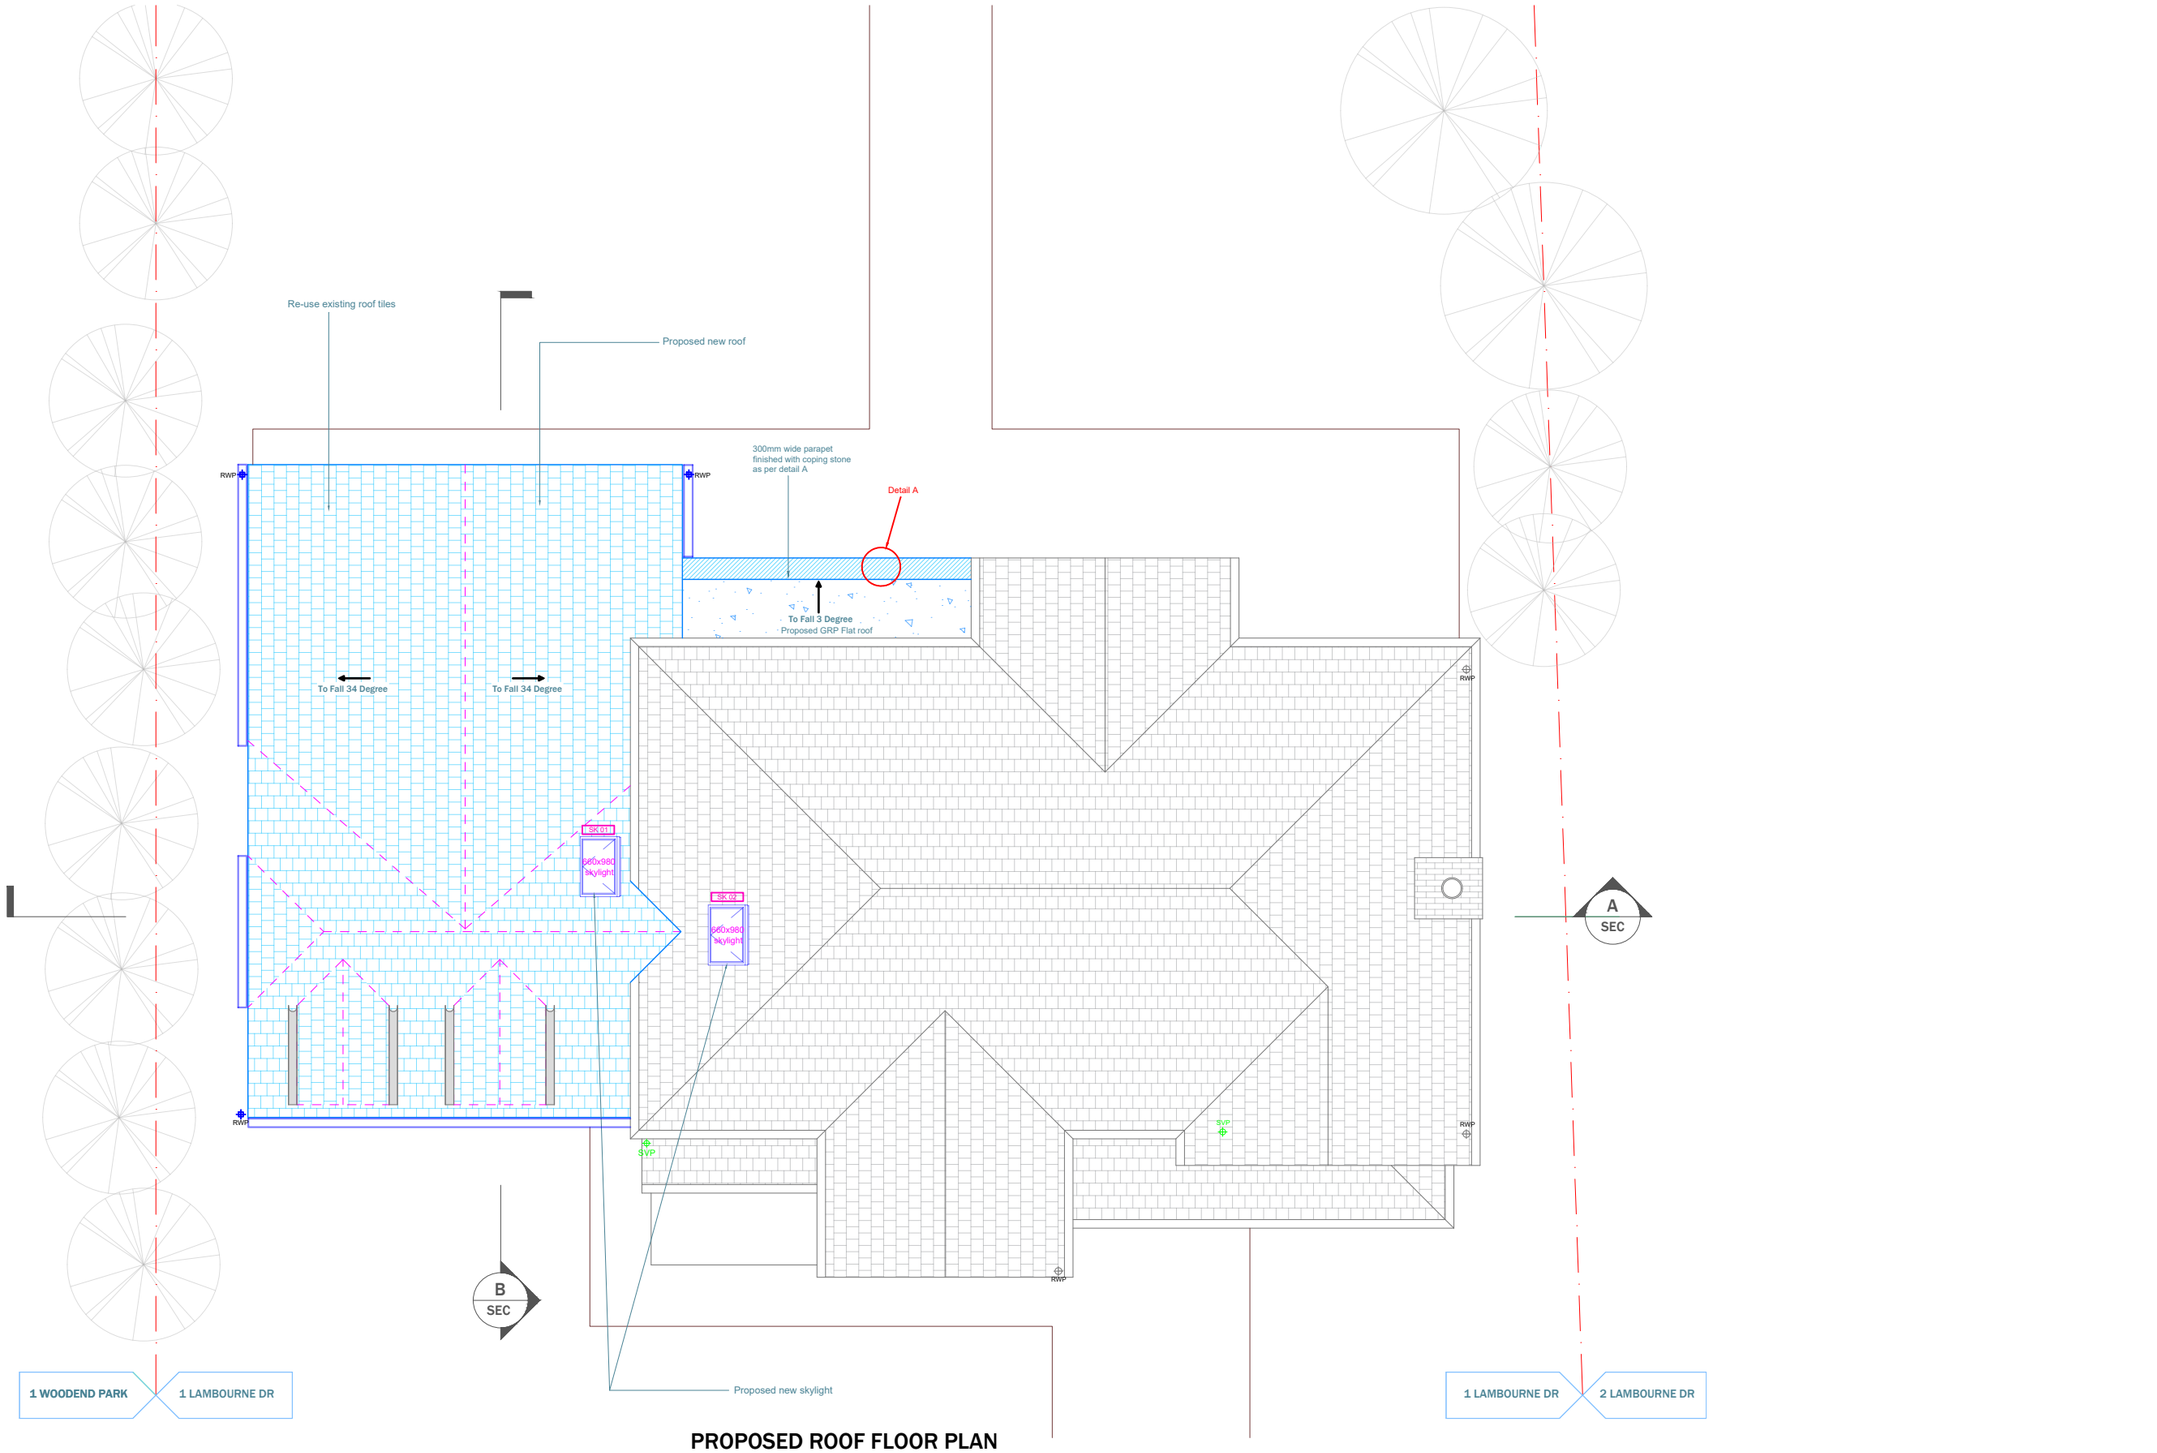

PROPOSED ROOF FLOOR PLAN

Scale 1:100 @A3 0 1 2 3 4 5m
Scale 1:50 @A3 0 0.5 1 1.5 2 2.5m
Scale 1:20 @A3 0 20 40 60 80 100m

extension architecture
3 River Reach, Gartons Way, Battersea
London SW11 3SX
Tel (0208) 288 8950 Fax (0871) 918 2798
www.extensionarchitecture.co.uk






This drawing is prepared solely for design and planning submission purposes. It is not intended or suitable for either building regulations or construction purposes and should not be used for such. All dimension shall be check and confirmed with site rep. and any discrepancies between the drawings and site shall be reported to PM. This drawing to be read in conjunction with engineers specification and details.
For construction information please refer to all drawings and specification of works.

For any structural steelworks details please refer to structural engineer's drawings & calculations.

The copyright of the drawing and designs remains with Extension Architecture. All copies are only for information about the application, they may not be used for any other purpose without the express written permission of Extension Architecture.

CLIENT: Vik Barodia	NOTES			SCALE: 1:100	DATE: 01.08.2024
PROJECT: 1 Lambourne Drive, KT11 3LB	VERSION	DESCRIPTION	DATE	DRAWN: BOUSIA	VERSION
TITLE: **Door, Window and Skylight location plan(3/3)**				SHEET REF. NO: 1LD-TD-23	

Window Schedule

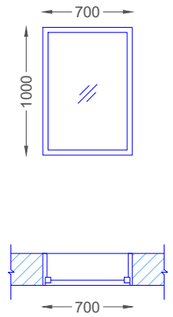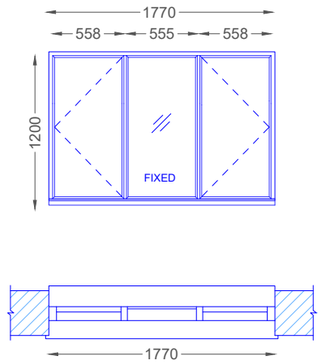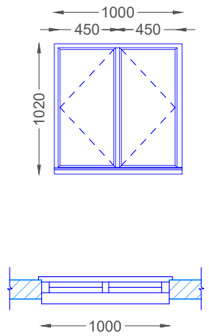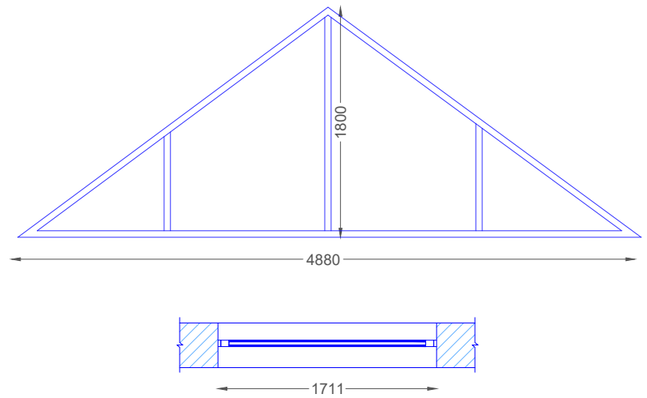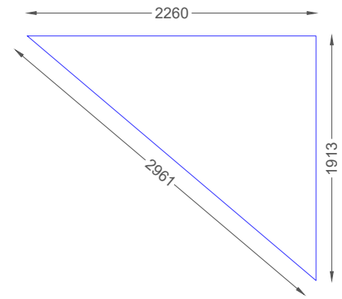Item reference	EW 01	EW 02	EW 03 EW 04	EW 05	SW 01
Panels & opening illustration / drawing	 Sill : 1119	 Sill : 1100	 Sill : 887	 Sill : 2870 from ground floor	
External / Internal	External	External	External	External	Internal
Approx. Dimensions (mm)	700 x 1000	1770 x 1200	1000 x 1020	4880 x 1800	2260 x 1913 x 2961
Location / Room	Ground Floor - Utility	Ground Floor - Kitchen	Mezzanine Floor - Office	Ground Floor - Lounge / Snug (Doube void space)	Ground Floor - Mezzanine stairacase next to bar
Material Specification	UPVC with timber effect fixed glass window All glass double glazed, clear glass.	UPVC with timber effect casement window. All glass double glazed, clear glass.	UPVC with timber effect casement window. All glass double glazed, clear glass.	Aluminium Fixed glass window All glass double glazed, clear glass.	Fixed glass All glass double glazed, clear glass.
Colour / Finish	Exterior: To match existing painted timber windows I Interior: White.	Exterior: To match existing painted timber windows I Interior: White.	Exterior: To match existing painted timber windows I Interior: White.	Exterior: Anthracite grey | Interior: Anthracite grey	-
Opener / Fixed	Openers as per drawing	Openers as per drawing	Openers as per drawing	Openers as per drawing	-
Number required	1	1	2	1	1
Manufacturer	N/A	N/A	N/A	N/A	N/A
Supply & fitted by	EA to supply & fit by window supplier	EA/Client to supply & fit by window supplier	EA/Client to supply & fit by window supplier	EA to supply & fit by window supplier	EA to supply & fit by window supplier
Notes	All dimensions TBC on site	All dimensions TBC on site	All dimensions TBC on site	All dimensions TBC on site	All dimensions TBC on site

Scale 1:100 @A3 0 1 2 3 4 5m

Scale 1:50 @A3 0 0.5 1 1.5 2 2.5m

Scale 1:20 @A3 0 20 40 60 80 100m

extension architecture
3 River Reach, Gartons Way, Battersea
London SW11 3SX
Tel (0208) 288 8950 Fax (0871) 918 2798
www.extensionarchitecture.co.uk

This drawing is prepared solely for design and planning submission purposes. It is not intended or suitable for either building regulations or construction purposes and should not be used for such. All dimension shall be check and confirmed with site rep. and any discrepancies between the drawings and site shall be reported to PM. This drawing to be read in conjunction with engineers specification and details.
For construction information please refer to all drawings and specification of works.

For any structural steelworks details please refer to structural engineer's drawings & calculations.

The copyright of the drawing and designs remains with Extension Architecture. All copies are only for information about the application, they may not be used for any other purpose without the express written permission of Extension Architecture.

CLIENT Vik Barodia

PROJECT 1 Lambourne Drive, KT11 3LB

TITLE **Window Schedule**

NOTES

VERSION	DESCRIPTION	DATE

SCALE **1:20**


DATE **01.08.2024**

DRAWN **BOUSIA**


VERSION

SHEET REF. NO **1LD-TD-24**

Internal Door

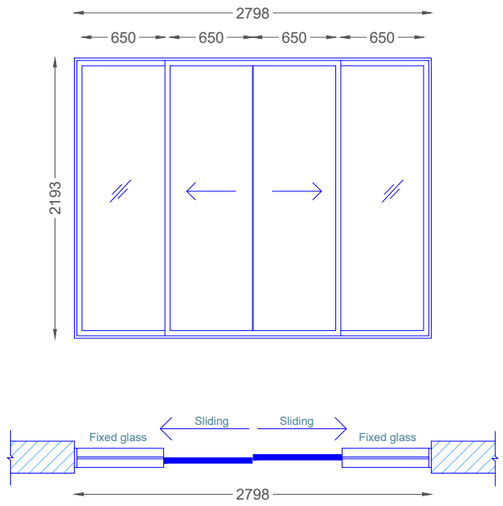Item reference	ID 01
Panels & opening illustration / drawing	
Approx. Dimensions (mm)	2798 x 2193
Location / Room	GF - Kitchen rear
External / Internal	Internal
Material Specification	Aluminium door with 2No. sliding door panels & 2 panels as fixed All glass double glazed, clear glass. Design TBC
Colour / Finish	To be painted anthracite by contractor
Opener / Fixed	Openings as per drawing
Number required	1
Manufacturer	N/A
Supply & fitted by	Client to supply & Contractor to fit
Notes	All dimensions TBC on site

Skylight Schedule

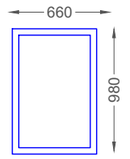Item reference	SK 01 SK 02
Panels & opening illustration / drawing	 Plan View (Position to be checked at site)
Approx. Dimensions (mm)	660 x 980
Location / Room	F.F - Staircase landing & Bedroom 3 bathroom
Material Specification	Skylight, Manually Openable glazing, double glazed clear glass
Colour / Finish	Exterior: Black / Grey | Interior: White
Opener / Fixed	Manual opening Velux, middle-hung
Number required	2
Manufacturer	Velux or Equivalent Product
Supply & fitted by	Contractor to supply & contractor to fit
Notes	All dimensions TBC on site

* NOTE: ALL BATHROOM DOORS TO BE FITTED WITH THUMB TURN LOCK

All Internal & external Door handles with fittings.

Black (to be confirmed by the client). Client to confirm the handle position with the supplier before purchase.

Supply: Client

Installation: Contractor

Scale 1:100 @A3 0 1 2 3 4 5m

Scale 1:50 @A3 0 0.5 1 1.5 2 2.5m

Scale 1:20 @A3 0 20 40 60 80 100m

extension architecture

3 River Reach, Gartons Way, Battersea
London SW11 3SX
Tel (0208) 288 8950 Fax (0871) 918 2798
www.extensionarchitecture.co.uk

This drawing is prepared solely for design and planning submission purposes. It is not intended or suitable for either building regulations or construction purposes and should not be used for such. All dimension shall be check and confirmed with site rep. and any discrepancies between the drawings and site shall be reported to PM. This drawing to be read in conjunction with engineers specification and details.
For construction information please refer to all drawings and specification of works.

For any structural steelworks details please refer to structural engineer's drawings & calculations.

The copyright of the drawing and designs remains with Extension Architecture. All copies are only for information about the application, they may not be used for any other purpose without the express written permission of Extension Architecture.

CLIENT: Vik Barodia

PROJECT: 1 Lambourne Drive, KT11 3LB

TITLE: **Internal door and Skylight schedule**

NOTES

VERSION	DESCRIPTION	DATE

SCALE: **1:20**




DATE: **01.08.2024**

DRAWN: **BOUSIA**

VERSION

SHEET REF. NO: **1LD-TD-25**

External Door

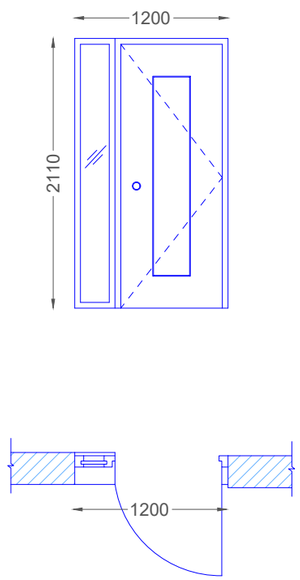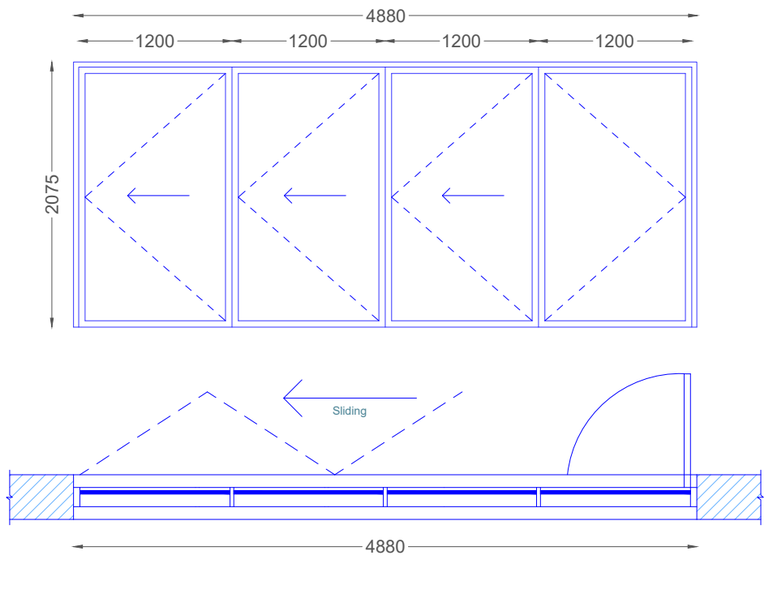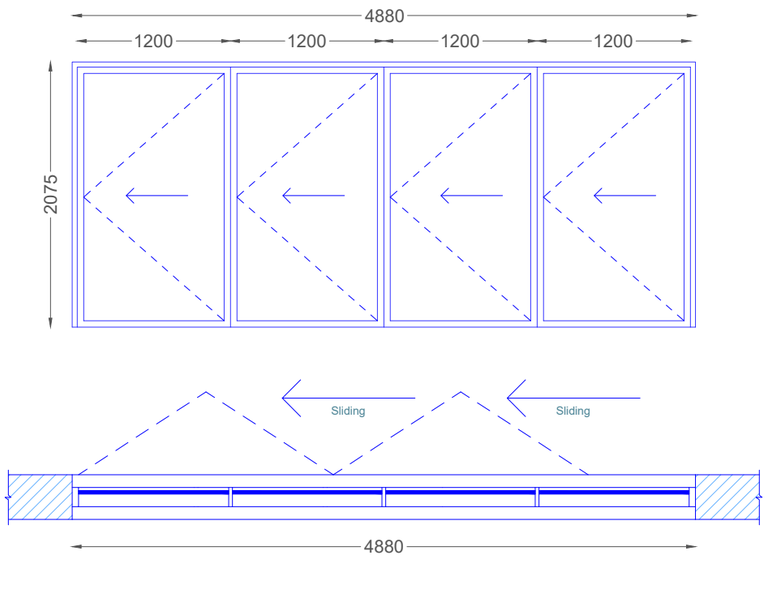Item reference	ED 01	ED 02	ED 03
Panels & opening illustration / drawing	Design TBC 		
Approx. Dimensions (mm)	1200 x 2110	4880 x 2075	4880 x 2075
Location / Room	GF- Hall	GF- Kitchen rear	GF- Lounge/Snug
External / Internal	External	External	External
Material Specification	Composite / Timber door	Aluminium door - with 3No. panels as Bi-fold door & 1 panel as openable All glass double glazed, clear glass. Design TBC	Aluminium door - with 4No.Bi-fold door panels All glass double glazed, clear glass. Design TBC
Colour / Finish	Primed smooth Anthracite grey	Smooth finish. Exterior - Anthracite grey & Interior: Anthracite grey	Smooth finish. Exterior - Anthracite grey & Interior: Anthracite grey
Opener / Fixed	Openings as per drawing	Openings as per drawing	Openings as per drawing
Number required	1	1	1
Manufacturer	N/A	N/A	N/A
Supply & fitted by	Client to supply & Specialist to fit	EA to supply & fit	EA to supply & fit
Notes	All dimensions TBC on site	All dimensions TBC on site	All dimensions TBC on site

* NOTE: ALL BATHROOM DOORS TO BE FITTED WITH THUMB TURN LOCK

All Internal & external Door handles with fittings.
Black (to be confirmed by the client). Client to confirm the handle position with the supplier before purchase.

Supply: Client
Installation: Contractor

Scale 1:100 @A3 0 1 2 3 4 5m
Scale 1:50 @A3 0 0.5 1 1.5 2 2.5m
Scale 1:20 @A3 0 20 40 60 80 100m

extension architecture
3 River Reach, Gartons Way, Battersea
London SW11 3SX
Tel (0208) 288 8950 Fax (0871) 918 2798
www.extensionarchitecture.co.uk

This drawing is prepared solely for design and planning submission purposes. It is not intended or suitable for either building regulations or construction purposes and should not be used for such. All dimension shall be check and confirmed with site rep. and any discrepancies between the drawings and site shall be reported to PM. This drawing to be read in conjunction with engineers specification and details.
For construction information please refer to all drawings and specification of works.

For any structural steelworks details please refer to structural engineer's drawings & calculations.

The copyright of the drawing and designs remains with Extension Architecture. All copies are only for information about the application, they may not be used for any other purpose without the express written permission of Extension Architecture.

CLIENT: Vik Barodia	NOTES			SCALE: 1:50	DATE: 01.08.2024
PROJECT: 1 Lambourne Drive, KT11 3LB	VERSION	DESCRIPTION	DATE	DRAWN: BOUSIA	VERSION
TITLE: **External door schedule**				SHEET REF. NO: 1LD-TD-26	

GROUND FLOOR FLOORING - SPECIFICATION


Hatch	Type	Location	Approx. m^2	Supply	Installation
	Amtico luxury vinyl plank style flooring 3mm.	Hall,WC, Office,Dining, Kitchen, Utility & Lounge/Snug	102 m^2	Client	Contractor TBC
	40mm oiled solid wooden tread to match the design of amtico flooring	Staircase	4m^2	Client	Contractor

Proposed mezzanine floor staircase structure (Ground floor to mezzanine)

Timber staircase structure. Design as per 3d

*Material to be confirmed

Supply: Contractor
Installation: Contractor

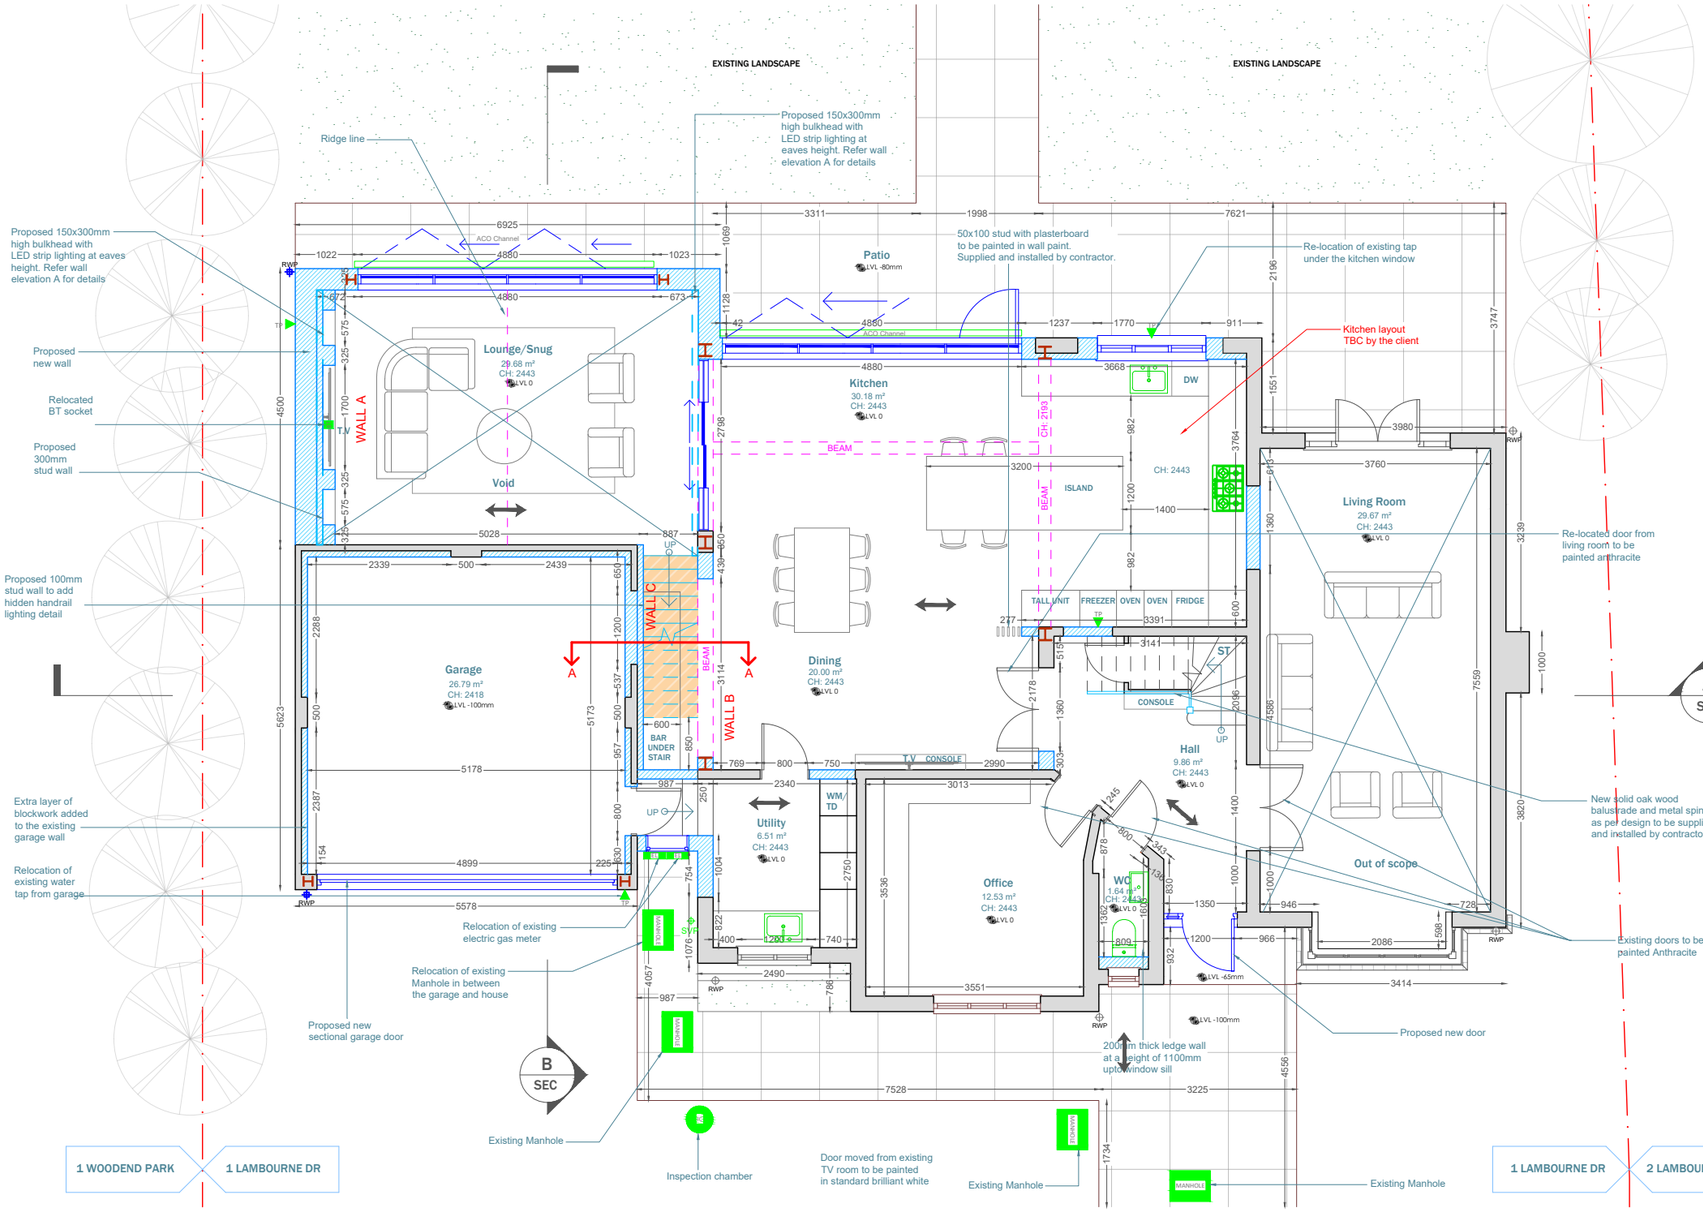

PROPOSED GROUND FLOOR PLAN

1. Amtico luxury vinyl plank style flooring 3mm.

Supply: Client
Installation: Contractor
*EA/client to supply all the fixing materials for the flooring like glue, screws, underlay (if any), etc. Contractor to inform the requirements to the client & Project Manager in advance.

2. 40mm oiled solid wooden tread to match the design of amtico flooring

*Material to be confirmed

Supply: Client
Installation: Contractor

Ground floor existing staircase

Finish Materials:

Going and Tread to be painted Anthracite grey

Supply: Client
Installation: Client
*Client to supply all the fixing materials for the flooring like glue, screws, underlay (if any), etc. Contractor to inform the requirements to the client & Project Manager in advance.

Ground floor staircase railing

New Railing and Spindles

Paint color : TBC by Client
*Material to be confirmed

Ground floor staircase railing

New Railing and Spindles

Paint color : TBC by Client
*Material to be confirmed

Scale 1:100 @A3 0 1 2 3 4 5m
Scale 1:50 @A3 0 0.5 1 1.5 2 2.5m
Scale 1:20 @A3 0 20 40 60 80 100m

extension architecture
3 River Reach, Gartons Way, Battersea
London SW11 3SX
Tel (0208) 288 8950 Fax (0871) 918 2798
www.extensionarchitecture.co.uk

This drawing is prepared solely for design and planning submission purposes. It is not intended or suitable for either building regulations or construction purposes and should not be used for such. All dimension shall be check and confirmed with site rep. and any discrepancies between the drawings and site shall be reported to PM. This drawing to be read in conjunction with engineers specification and details.
For construction information please refer to all drawings and specification of works.


For any structural steelworks details please refer to structural engineer's drawings & calculations.

The copyright of the drawing and designs remains with Extension Architecture. All copies are only for information about the application, they may not be used for any other purpose without the express written permission of Extension Architecture.

CLIENT: Vik Barodia	NOTES			SCALE: 1:100	DATE: 01.08.2024
PROJECT: 1 Lambourne Drive, KT11 3LB	VERSION	DESCRIPTION	DATE	DRAWN: BOUSIA	VERSION
TITLE: **Ground floor - Flooring Specification**				SHEET REF. NO: 1LD-TD-27	

FIRST FLOOR FLOORING - SPECIFICATION

Hatch	Type	Location	Approx. m^2	Supply	Installation
	Amtico luxury vinyl plank style flooring 3mm.	Office and Landing	25 m^2	Client	Contractor TBC
	Ply floor board(Storage) - Not flooring finish				

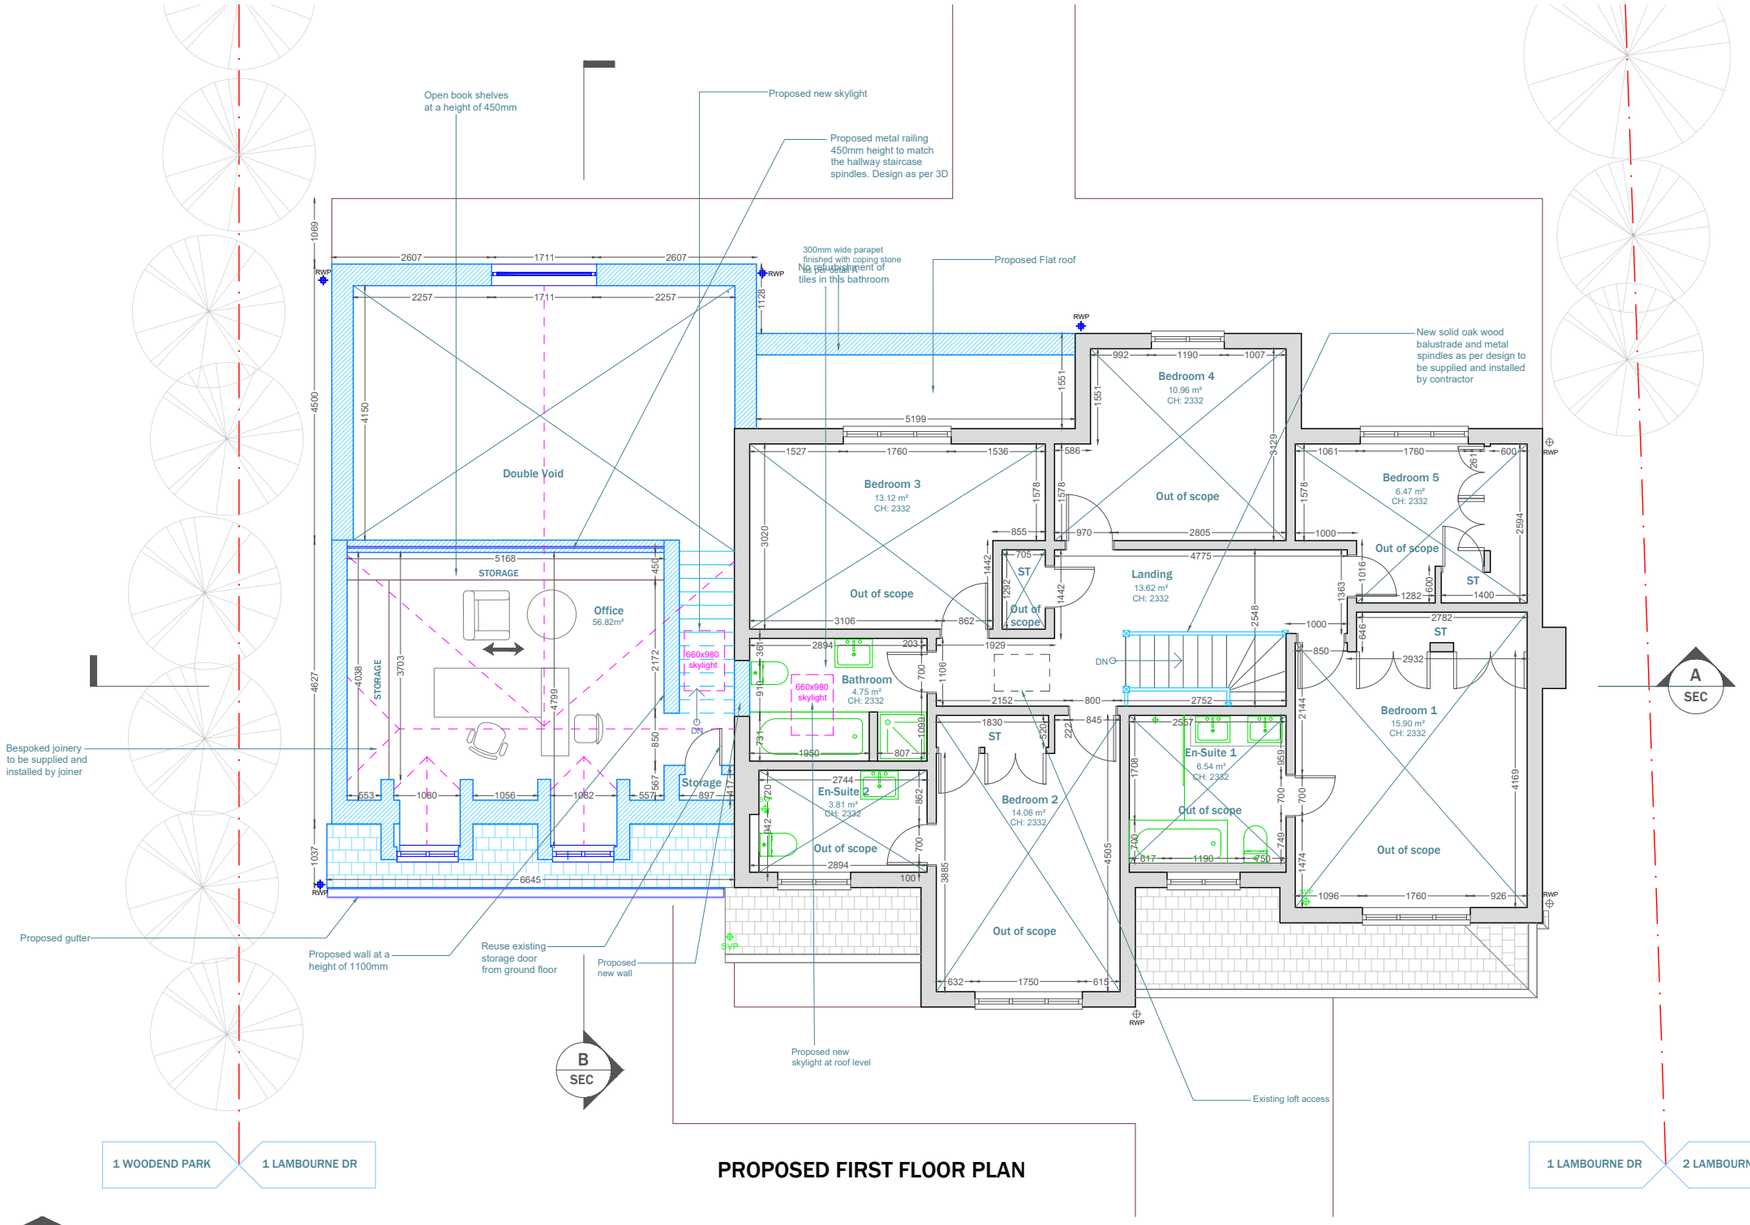

PROPOSED FIRST FLOOR PLAN

1. Amtico luxury vinyl plank style flooring 3mm.

Supply: Client

Installation: Contractor

*EA/client to supply all the fixing materials for the flooring like glue, screws, underlay (if any), etc. Contractor to inform the requirements to the client & Project Manager in advance.

Scale 1:100 @A3 0 1 2 3 4 5m

Scale 1:50 @A3 0 0.5 1 1.5 2 2.5m

Scale 1:20 @A3 0 20 40 60 80 100m

extension architecture

3 River Reach, Gartons Way, Battersea
London SW11 3SX

Tel (0208) 288 8950 Fax (0871) 918 2798
www.extensionarchitecture.co.uk

This drawing is prepared solely for design and planning submission purposes. It is not intended or suitable for either building regulations or construction purposes and should not be used for such. All dimension shall be check and confirmed with site rep. and any discrepancies between the drawings and site shall be reported to PM. This drawing to be read in conjunction with engineers specification and details.
For construction information please refer to all drawings and specification of works.

For any structural steelworks details please refer to structural engineer's drawings & calculations.


The copyright of the drawing and designs remains with Extension Architecture. All copies are only for information about the application, they may not be used for any other purpose without the express written permission of Extension Architecture.

CLIENT: Vik Barodia	NOTES			SCALE: 1:100	DATE: 01.08.2024
PROJECT: 1 Lambourne Drive, KT11 3LB	VERSION	DESCRIPTION	DATE	DRAWN: BOUSIA	VERSION
TITLE: First floor - Flooring Specification				SHEET REF. NO: 1LD-TD-28	

GROUND FLOOR SKIRTING - SPECIFICATION

Hatch	Type	Supply	Installation
	*Existing Skirting to be retained and new skirting to match the existing	Contractor	Contractor
	*Proposed Architrave to match existing skirting	Contractor	Contractor

* All skirting & Architrave to be confirmed at site with the client and the Project Manager prior to supply

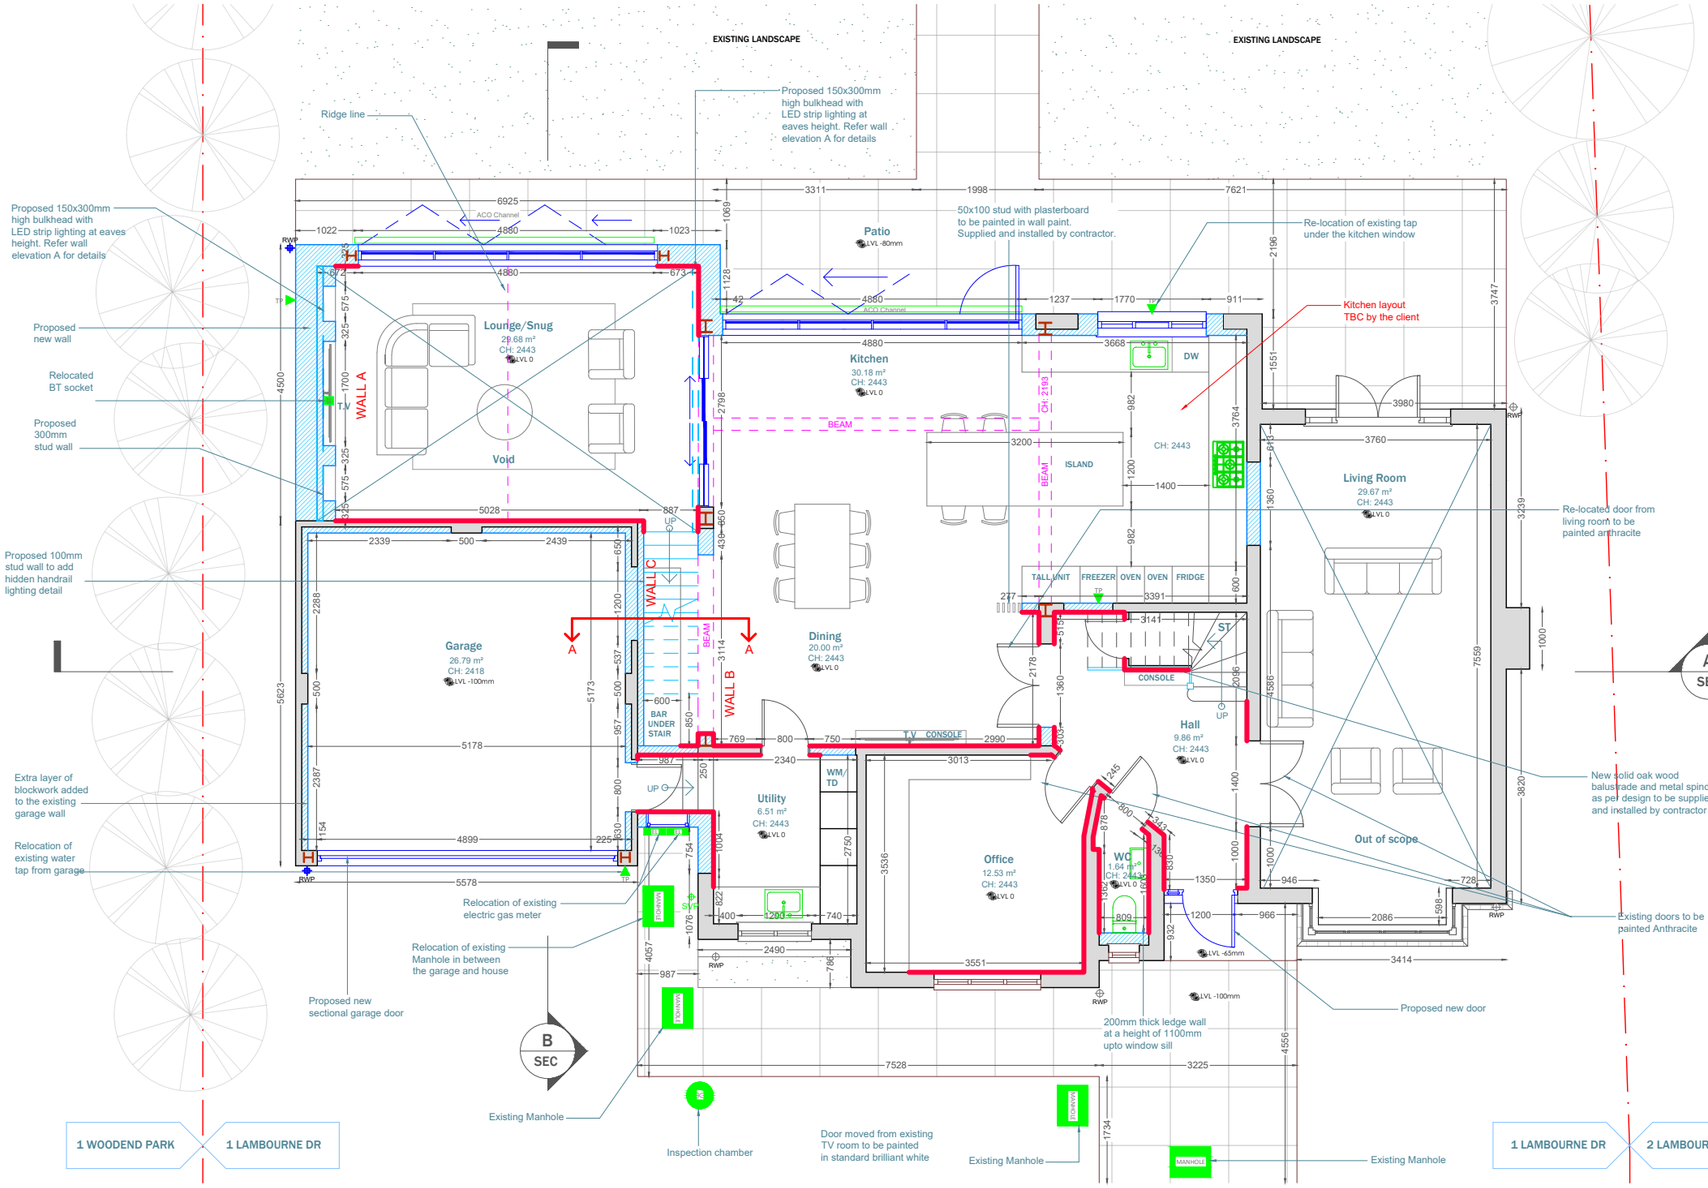

PROPOSED GROUND FLOOR PLAN


Reference image



Existing Skirting

MDF Skirting Board

Supply: Contractor
Installation: Contractor

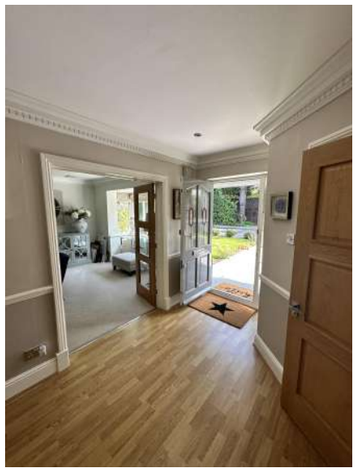

Existing Architrave

Reference site image

Scale 1:100 @A3 0 1 2 3 4 5m
Scale 1:50 @A3 0 0.5 1 1.5 2 2.5m
Scale 1:20 @A3 0 20 40 60 80 100m

extension architecture
3 River Reach, Gartons Way, Battersea
London SW11 3SX
Tel (0208) 288 8950 Fax (0871) 918 2798
www.extensionarchitecture.co.uk

This drawing is prepared solely for design and planning submission purposes. It is not intended or suitable for either building regulations or construction purposes and should not be used for such. All dimension shall be check and confirmed with site rep. and any discrepancies between the drawings and site shall be reported to PM. This drawing to be read in conjunction with engineers specification and details.
For construction information please refer to all drawings and specification of works.

For any structural steelworks details please refer to structural engineer's drawings & calculations.


The copyright of the drawing and designs remains with Extension Architecture. All copies are only for information about the application, they may not be used for any other purpose without the express written permission of Extension Architecture.

CLIENT: Vik Barodia	NOTES			SCALE: 1:100	DATE: 01.08.2024
PROJECT: 1 Lambourne Drive, KT11 3LB	VERSION	DESCRIPTION	DATE	DRAWN: BOUSIA	VERSION
TITLE: **Ground Floor Skirting Specification**				SHEET REF. NO: **1LD-TD-29**	

FIRST FLOOR SKIRTING - SPECIFICATION

Hatch	Type	Supply	Installation
	*New Skirting to match existing	Contractor	Contractor
	*Proposed Architrave to match existing skirting	Contractor	Contractor

* All skirting & Architrave to be confirmed at site with the client and the Project Manager prior to supply

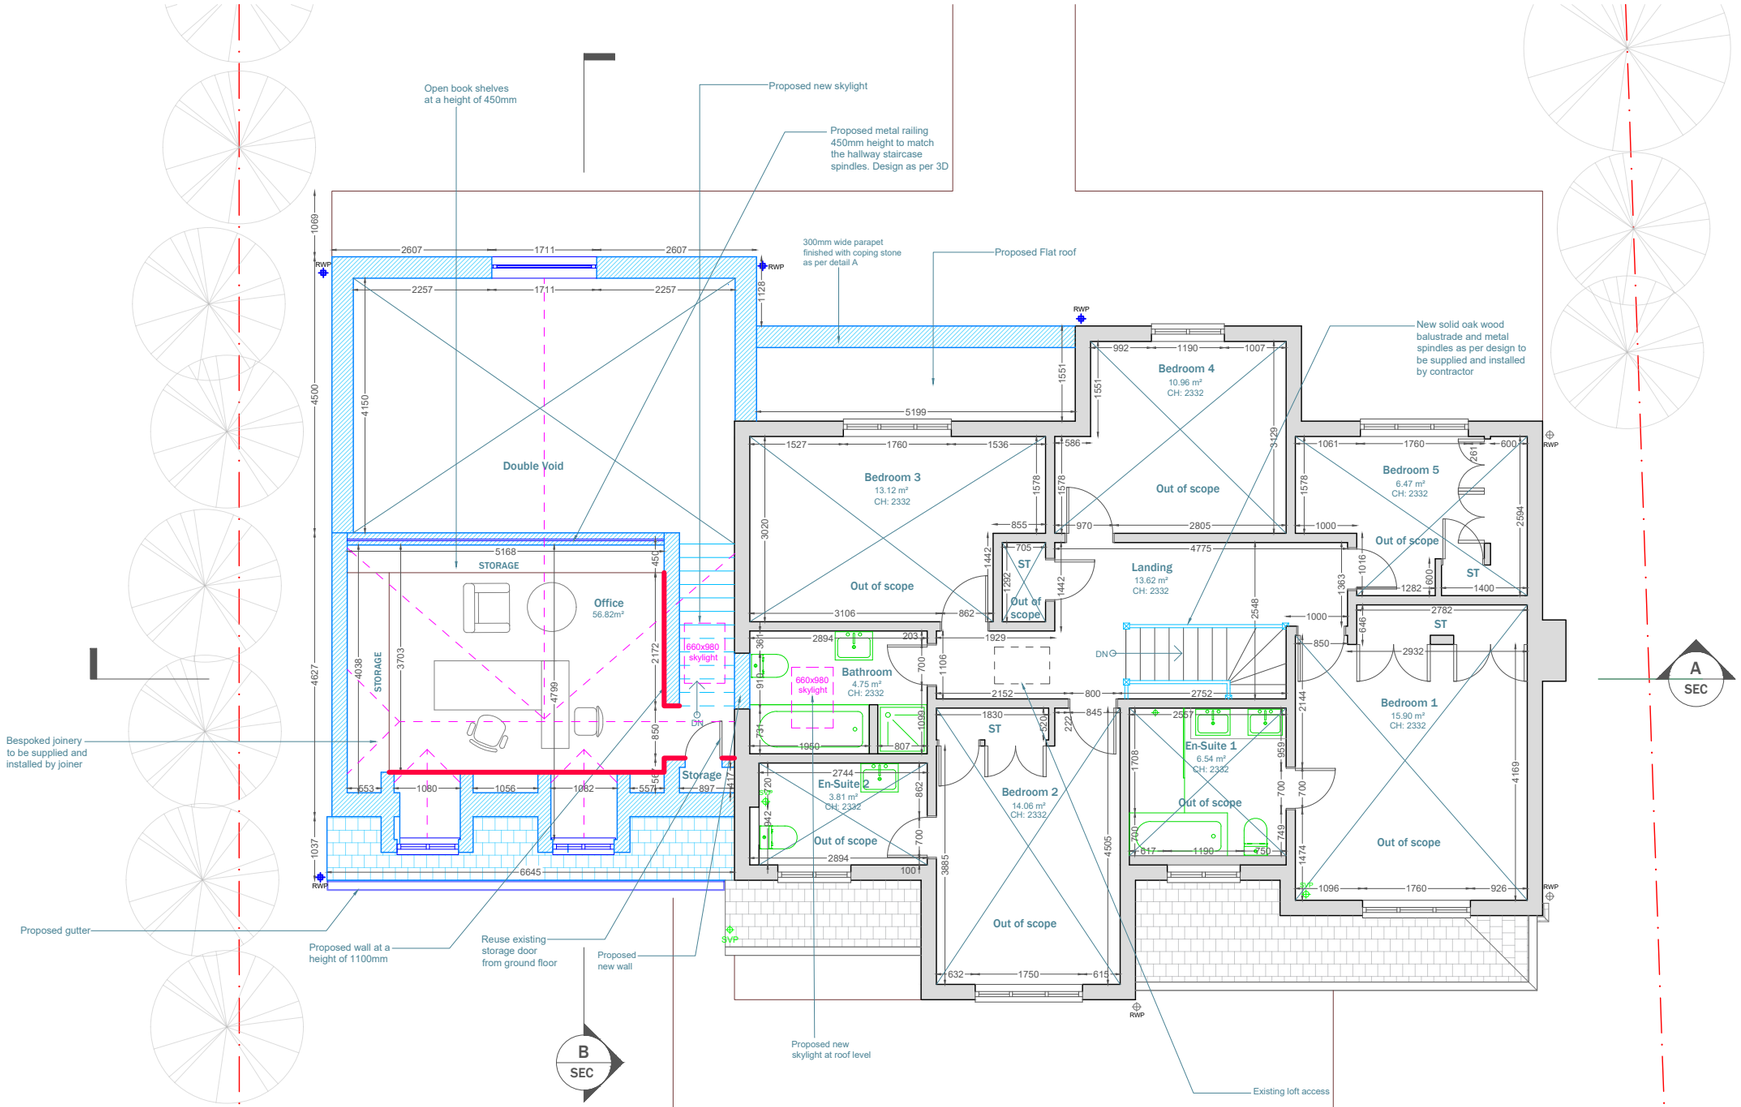

PROPOSED FIRST FLOOR PLAN

Reference image



Existing Skirting
MDF Skirting Board

Supply: Contractor
Installation: Contractor

Scale 1:100 @A3 0 1 2 3 4 5m
Scale 1:50 @A3 0 0.5 1 1.5 2 2.5m
Scale 1:20 @A3 0 20 40 60 80 100m

extension architecture
3 River Reach, Gartons Way, Battersea
London SW11 3SX
Tel (0208) 288 8950 Fax (0871) 918 2798
www.extensionarchitecture.co.uk

This drawing is prepared solely for design and planning submission purposes. It is not intended or suitable for either building regulations or construction purposes and should not be used for such. All dimension shall be check and confirmed with site rep. and any discrepancies between the drawings and site shall be reported to PM. This drawing to be read in conjunction with engineers specification and details.
For construction information please refer to all drawings and specification of works.


For any structural steelworks details please refer to structural engineer's drawings & calculations.

The copyright of the drawing and designs remains with Extension Architecture. All copies are only for information about the application, they may not be used for any other purpose without the express written permission of Extension Architecture.

CLIENT: Vik Barodia	NOTES			SCALE: 1:100	DATE: 01.08.2024
PROJECT: 1 Lambourne Drive, KT11 3LB	VERSION	DESCRIPTION	DATE	DRAWN: BOUSIA	VERSION
TITLE: **First Floor skirting specification**				SHEET REF. NO: 1LD-TD-30	

GROUND FLOOR - WALL FINISH SPECIFICATION

Hatch	Type	Location	Supply	Installation
	Full height paint finish. Colour TBC	Hall, Dining, Kitchen, Lounge/Snug, Utility & Office	Client	Contractor
	Quartz backsplash (600mm High)	Kitchen	Client	Quartz supplier
	60x120cm marble wall tiles at a height of 1100 mm and anthracite grey paint finish above	WC	Client	Contractor

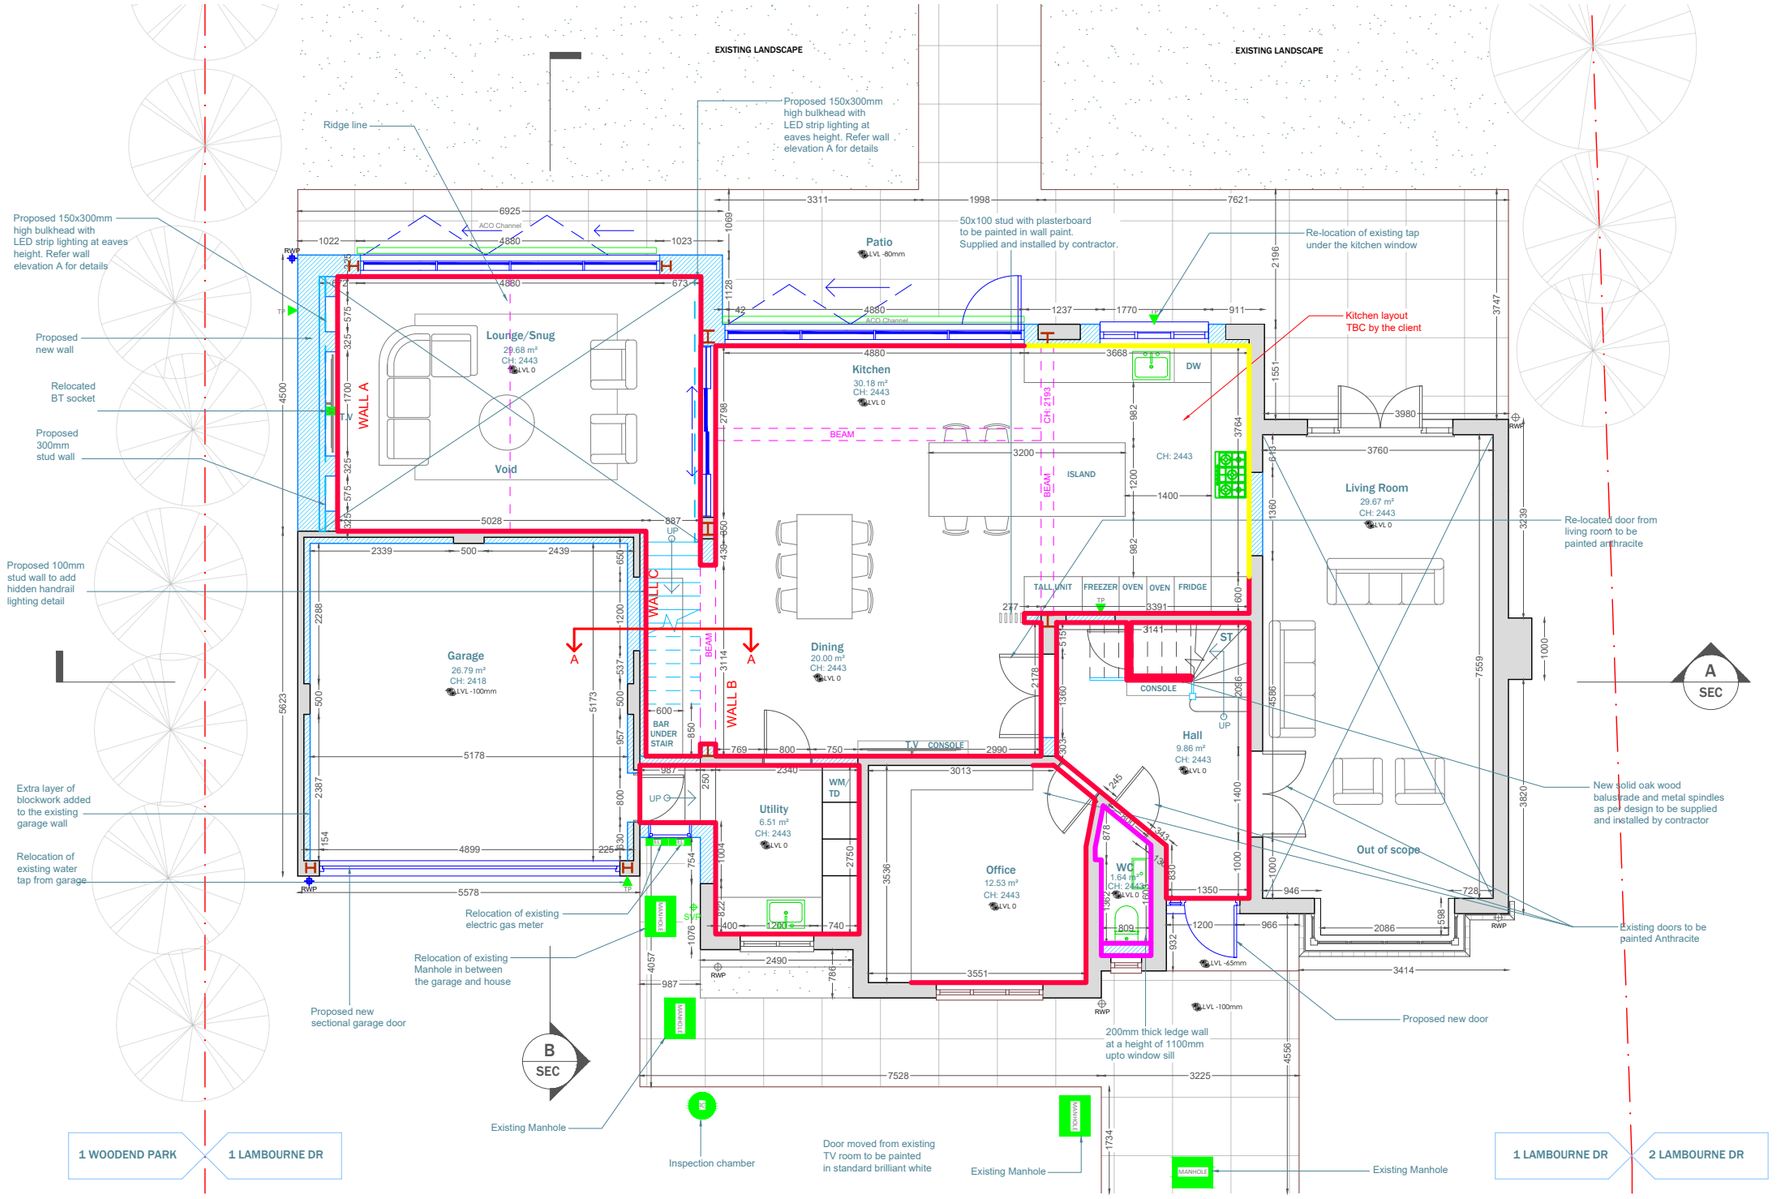

PROPOSED GROUND FLOOR PLAN

1. Quartz splashback

*Material to be confirmed

Supply: Client

Installation: Quartz supplier

*Client to supply all the fixing materials for the laying like glue, etc. Contractor to inform the requirements to the client & Project Manager in advance.

2. 60 x 120cm marble texture tiles

*Material to be confirmed

Supply: Client

Installation: Contractor

*Client to supply all the fixing materials for the flooring like glue, screws, underlay (if any), etc. Contractor to inform the requirements to the client & Project Manager in advance.

Scale 1:100 @A3 0 1 2 3 4 5m

Scale 1:50 @A3 0 0.5 1 1.5 2 2.5m

Scale 1:20 @A3 0 20 40 60 80 100m

extension architecture

3 River Reach, Gartons Way, Battersea
London SW11 3SX

Tel (0208) 288 8950 Fax (0871) 918 2798
www.extensionarchitecture.co.uk

This drawing is prepared solely for design and planning submission purposes. It is not intended or suitable for either building regulations or construction purposes and should not be used for such. All dimension shall be check and confirmed with site rep. and any discrepancies between the drawings and site shall be reported to PM. This drawing to be read in conjunction with engineers specification and details. For construction information please refer to all drawings and specification of works.


For any structural steelworks details please refer to structural engineer's drawings & calculations.

The copyright of the drawing and designs remains with Extension Architecture. All copies are only for information about the application, they may not be used for any other purpose without the express written permission of Extension Architecture.

CLIENT: Vik Barodia	NOTES			SCALE: 1:100	DATE: 01.08.2024
PROJECT: 1 Lambourne Drive, KT11 3LB	VERSION	DESCRIPTION	DATE	DRAWN: BOUSIA	VERSION
TITLE: Ground floor - Wall finish Specification				SHEET REF. NO: 1LD-TD-31	

FIRST FLOOR - WALL FINISH SPECIFICATION

Hatch	Type	Location	Supply	Installation
	Full height paint finish. Colour TBC	Office, Landing & Storage	Client	Contractor

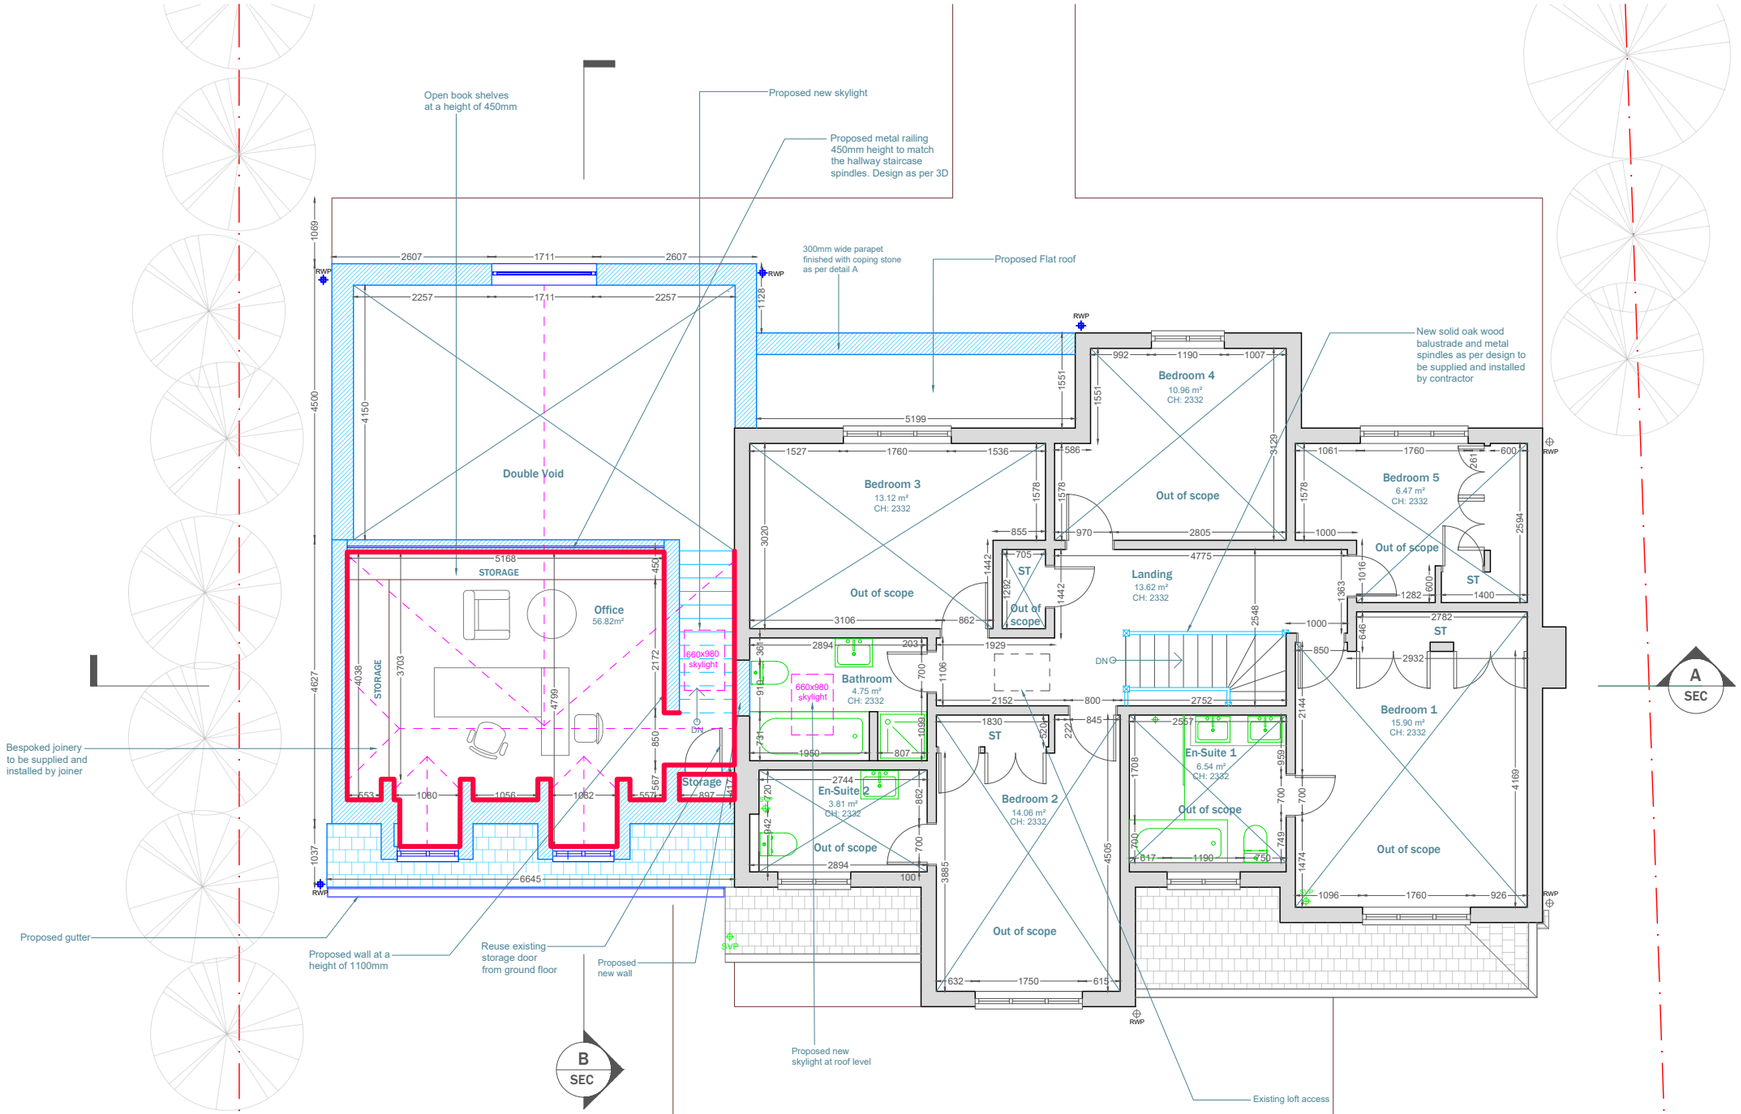

PROPOSED FIRST FLOOR PLAN

Scale 1:100 @A3 0 1 2 3 4 5m
Scale 1:50 @A3 0 0.5 1 1.5 2 2.5m
Scale 1:20 @A3 0 20 40 60 80 100m

extension architecture
3 River Reach, Gartons Way, Battersea
London SW11 3SX
Tel (0208) 288 8950 Fax (0871) 918 2798
www.extensionarchitecture.co.uk

This drawing is prepared solely for design and planning submission purposes. It is not intended or suitable for either building regulations or construction purposes and should not be used for such. All dimension shall be check and confirmed with site rep. and any discrepancies between the drawings and site shall be reported to PM. This drawing to be read in conjunction with engineers specification and details.
For construction information please refer to all drawings and specification of works.


For any structural steelworks details please refer to structural engineer's drawings & calculations.

The copyright of the drawing and designs remains with Extension Architecture. All copies are only for information about the application, they may not be used for any other purpose without the express written permission of Extension Architecture.

CLIENT: Vik Barodia	NOTES			SCALE: 1:100	DATE: 01.08.2024
PROJECT: 1 Lambourne Drive, KT11 3LB	VERSION	DESCRIPTION	DATE	DRAWN: BOUSIA	VERSION
TITLE: First floor - Wall finish Specification				SHEET REF. NO: 1LD-TD-32	

GROUND AND FIRST FLOOR COVING - SPECIFICATION

Hatch	Type	Location	Supply	Installation
	Retain existing coving	Hallway, WC	Client	Contractor
	Classic Coving WT11 126mm x 106mm x 2m	Kitchen, Dining & Utility	Client	Contractor

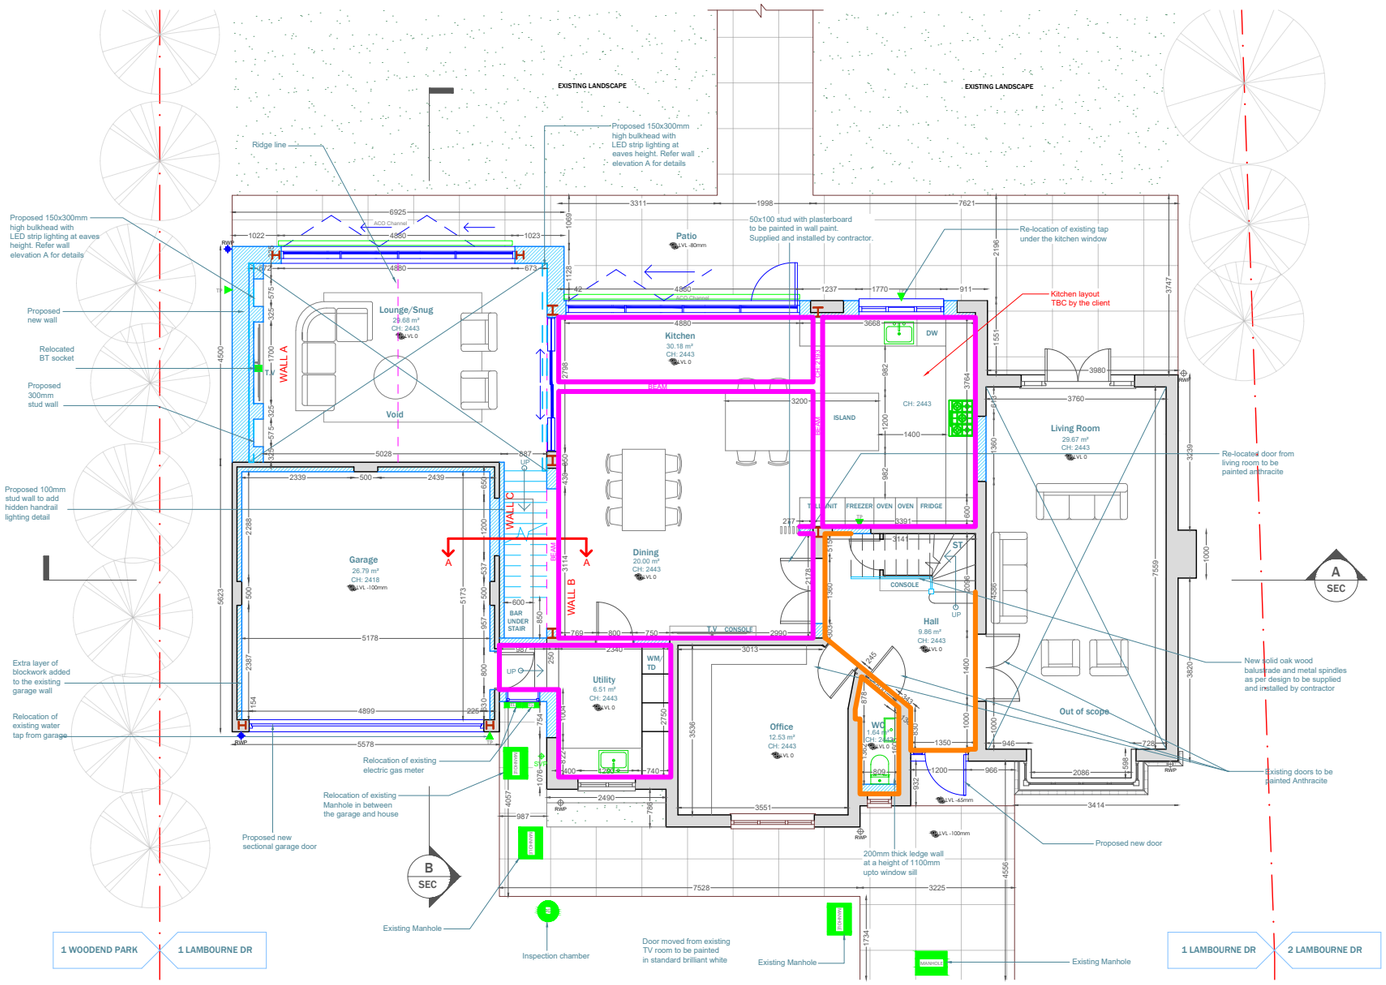

PROPOSED GROUND FLOOR PLAN



Reference site image



Reference image

Coving

Classic Coving WT11 126mm x 106mm x 2m

Supply: Client

Installation: Contractor

Scale 1:100 @A3 0 1 2 3 4 5m

Scale 1:50 @A3 0 0.5 1 1.5 2 2.5m

Scale 1:20 @A3 0 20 40 60 80 100m

extension architecture

3 River Reach, Gartons Way, Battersea
London SW11 3SX


Tel (0208) 288 8950 Fax (0871) 918 2798
www.extensionarchitecture.co.uk

This drawing is prepared solely for design and planning submission purposes. It is not intended or suitable for either building regulations or construction purposes and should not be used for such. All dimension shall be check and confirmed with site rep. and any discrepancies between the drawings and site shall be reported to PM. This drawing to be read in conjunction with engineers specification and details.
For construction information please refer to all drawings and specification of works.

For any structural steelworks details please refer to structural engineer's drawings & calculations.


The copyright of the drawing and designs remains with Extension Architecture. All copies are only for information about the application, they may not be used for any other purpose without the express written permission of Extension Architecture.

CLIENT: Vik Barodia	NOTES			SCALE: 1:100	DATE: 01.08.2024
PROJECT: 1 Lambourne Drive, KT11 3LB	VERSION	DESCRIPTION	DATE	DRAWN: BOUSIA	VERSION
TITLE: **Ground Floor Coving Specification**				SHEET REF. NO: 1LD-TD-33	

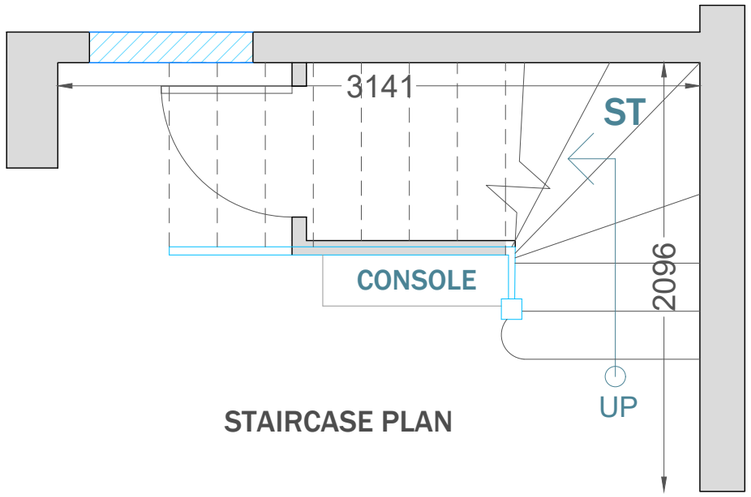

STAIRCASE PLAN

KEY PLAN - 1:30

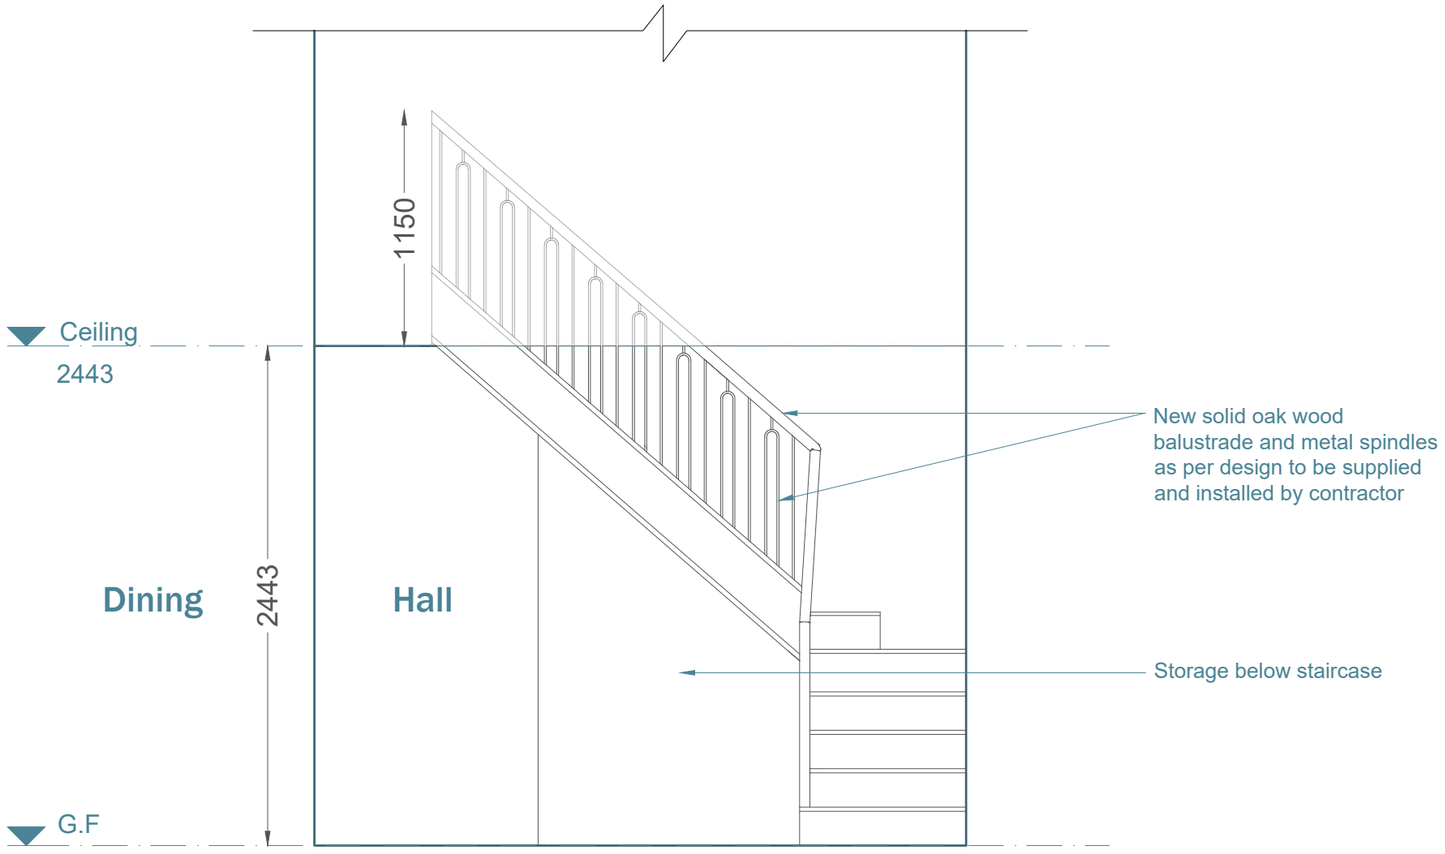

STAIRCASE ELEVATION

Existing stair from GF to FF
No. of risers: 14
Going: 235mm
Riser: 190mm

Existing ground floor staircase (Ground floor to First floor)

Going and Riser to be painted. Colour TBC
Supply: Client
Installation: Contractor

Railing & Spindles:

- Solid oak wood balustrade and metal spindles as per design.
- Staircase tread & riser to be carpet as per 3D design with staircase runner

Supply: Contractor
Installation: Contractor



Existing staircase reference image



Proposed staircase reference image

Scale 1:100 @A3 0 1 2 3 4 5m
Scale 1:50 @A3 0 0.5 1 1.5 2 2.5m
Scale 1:20 @A3 0 20 40 60 80 100m


extension architecture
3 River Reach, Gartons Way, Battersea
London SW11 3SX
Tel (0208) 288 8950 Fax (0871) 918 2798
www.extensionarchitecture.co.uk

This drawing is prepared solely for design and planning submission purposes. It is not intended or suitable for either building regulations or construction purposes and should not be used for such. All dimension shall be check and confirmed with site rep. and any discrepancies between the drawings and site shall be reported to PM. This drawing to be read in conjunction with engineers specification and details.
For construction information please refer to all drawings and specification of works.

For any structural steelworks details please refer to structural engineer's drawings & calculations.

The copyright of the drawing and designs remains with Extension Architecture. All copies are only for information about the application, they may not be used for any other purpose without the express written permission of Extension Architecture.

CLIENT Vik Barodia	NOTES			SCALE 1:30	DATE 01.08.2024
PROJECT 1 Lambourne Drive, KT11 3LB	VERSION	DESCRIPTION	DATE	DRAWN BOUSIA	VERSION
TITLE **Staircase detail drawing (1/2)**				SHEET REF. NO 1LD-TD-34	

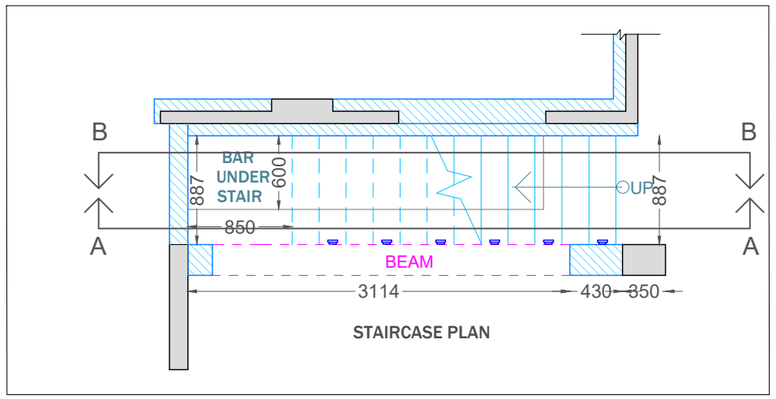

KEY PLAN - 1:50


Proposed staircase from GF to mezzanine floor

No. of risers: 12
Going: 220mm
Riser: 188mm

Handrail:

- Hidden handrail as per 3D design with Strip lighting

Supply: Contractor
Installation: Contractor

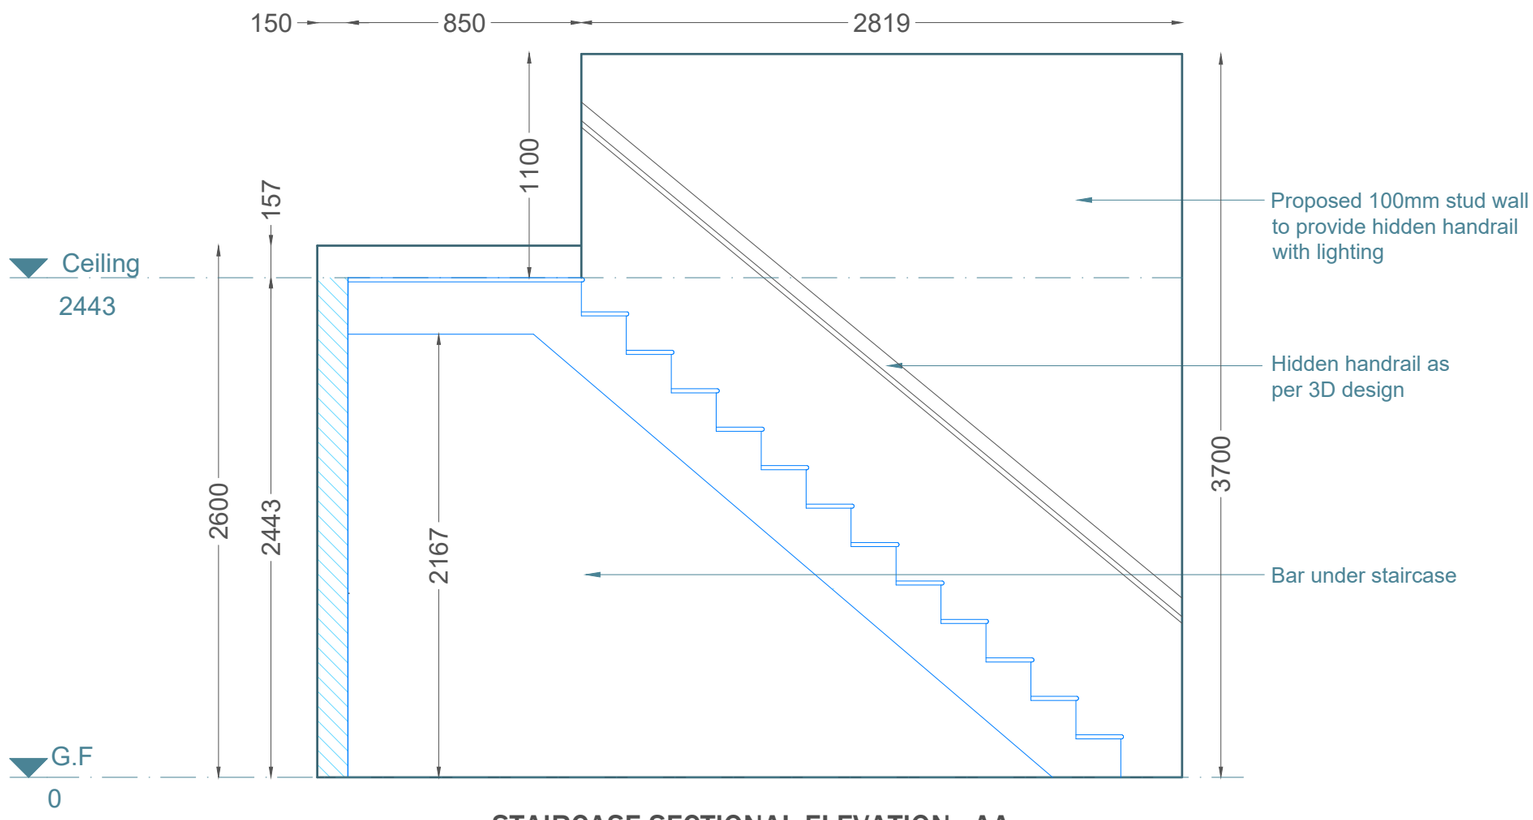

STAIRCASE SECTIONAL ELEVATION - AA

Proposed staircase
(Ground floor to Mezzanine floor)

Timber staircase structure

Going finished with wood
Riser finished with white


Supply: Contractor
Installation: Contractor

Staircase Finishes

Timber Staircase design TBC.



Proposed staircase reference image

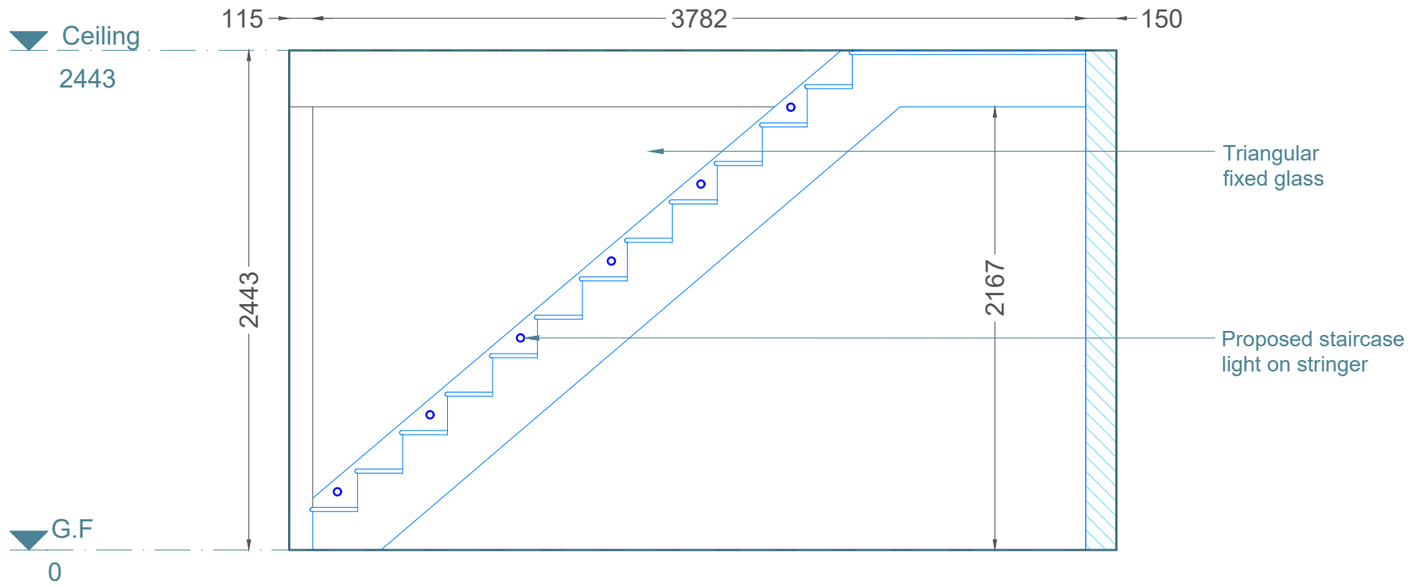

STAIRCASE SECTIONAL ELEVATION - BB

Scale 1:100 @A3 0 1 2 3 4 5m
Scale 1:50 @A3 0 0.5 1 1.5 2 2.5m
Scale 1:20 @A3 0 20 40 60 80 100m


extension architecture
3 River Reach, Gartons Way, Battersea
London SW11 3SX
Tel (0208) 288 8950 Fax (0871) 918 2798
www.extensionarchitecture.co.uk

This drawing is prepared solely for design and planning submission purposes. It is not intended or suitable for either building regulations or construction purposes and should not be used for such. All dimension shall be check and confirmed with site rep. and any discrepancies between the drawings and site shall be reported to PM. This drawing to be read in conjunction with engineers specification and details.
For construction information please refer to all drawings and specification of works.

For any structural steelworks details please refer to structural engineer's drawings & calculations.

The copyright of the drawing and designs remains with Extension Architecture. All copies are only for information about the application, they may not be used for any other purpose without the express written permission of Extension Architecture.

CLIENT: Vik Barodia	NOTES			SCALE: 1:30	DATE: 01.08.2024
PROJECT: 1 Lambourne Drive, KT11 3LB	VERSION	DESCRIPTION	DATE	DRAWN: BOUSIA	VERSION
TITLE: Staircase detail drawing (2/2)				SHEET REF. NO: 1LD-TD-35	

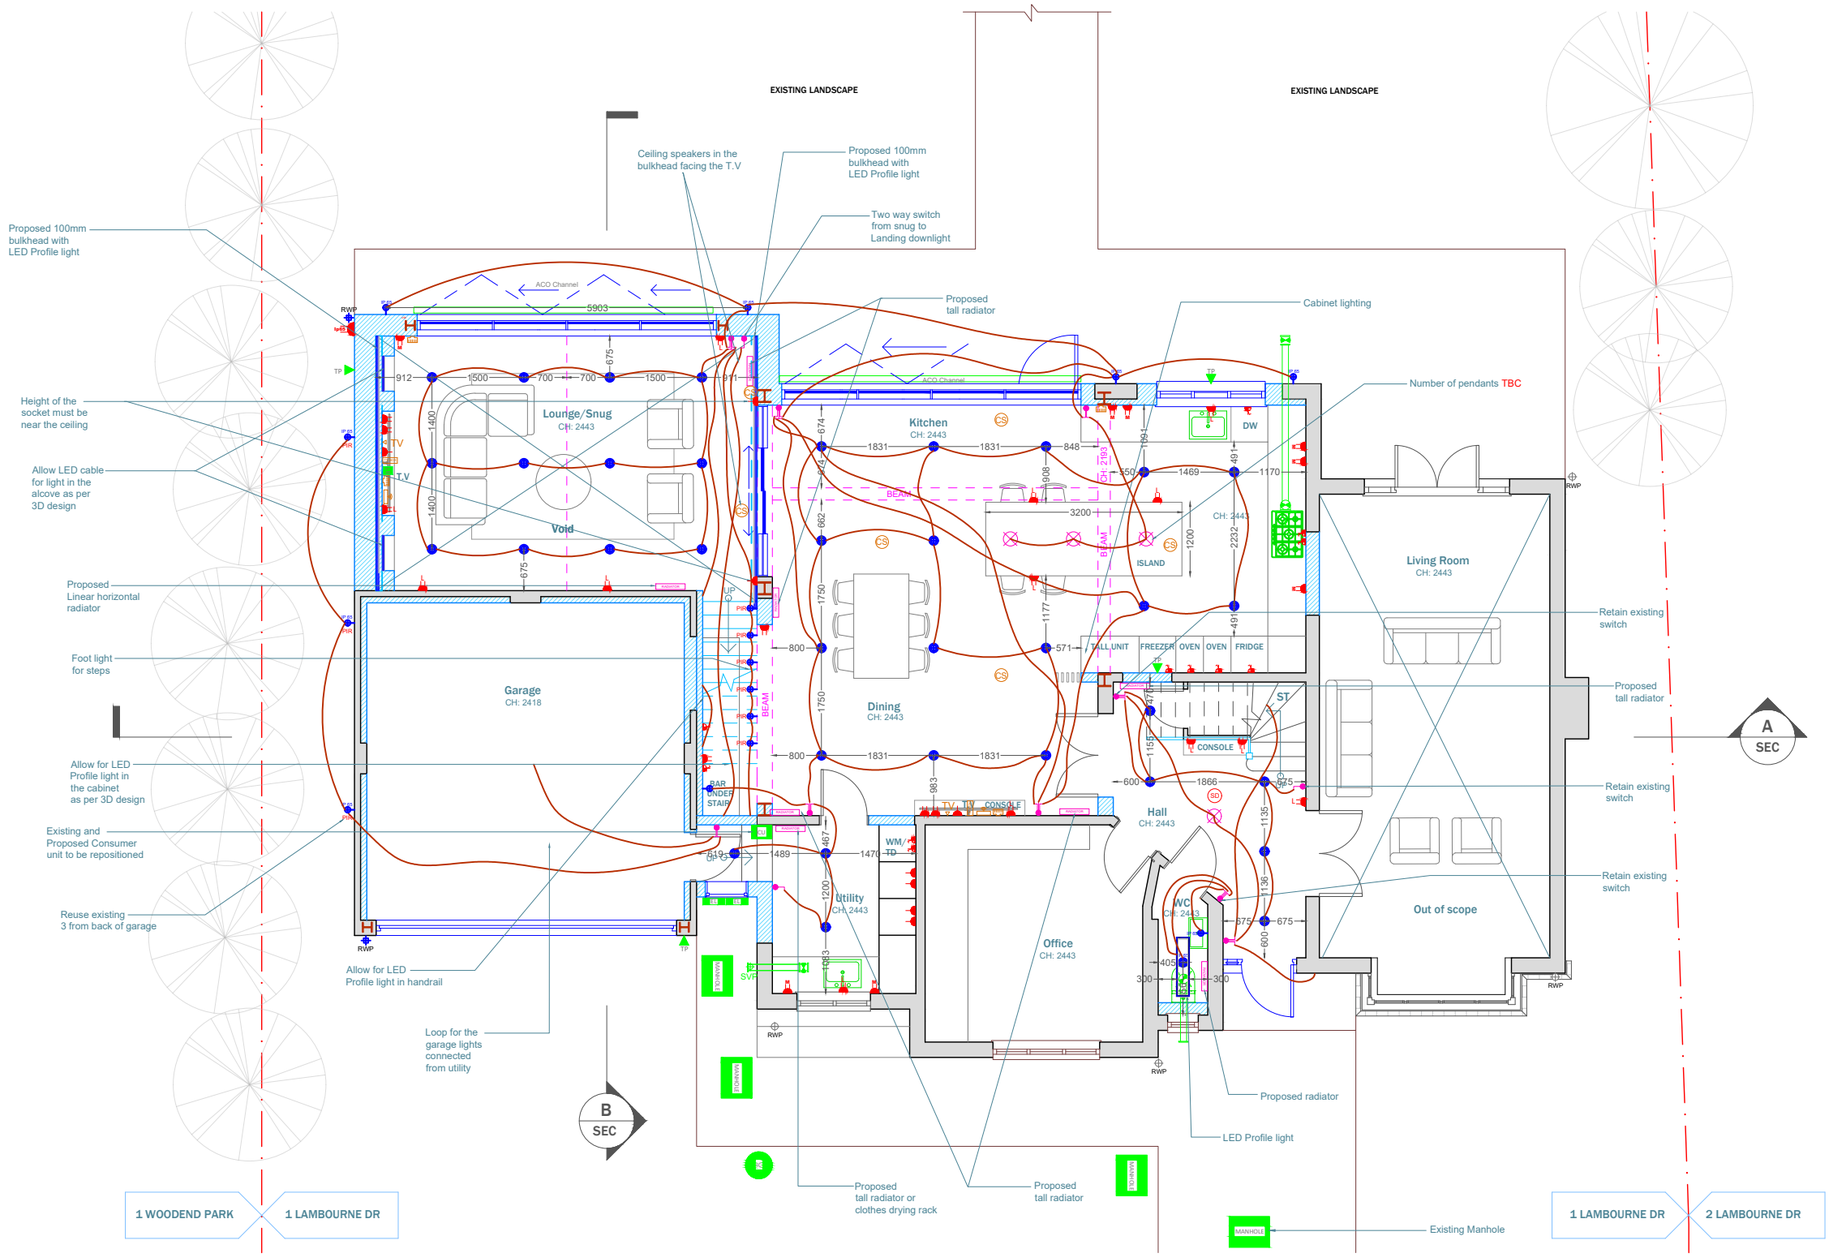

PROPOSED GROUND FLOOR PLAN

MECHANICAL & HEATING	
	Extractor fan (Ceiling mounted)
	Extractor fan (Wall mounted)
	Extractor fan (cooker hood)
W TANK	Water tank
BOILER	Boiler
ELEC. METER	Electric meter
GAS METER	Gas meter
T	Thermostat
RADIATOR	Existing Radiator
RADIATOR	Proposed Radiator
TOWEL RAIL	Heated towel rail (duel fuel electric)
ELECTRIC CAR CHARGER	Electric car charger

Extra Notes:

- Extractor spur above door where possible
- All bedside sockets & switches to be 650mm from floor. *TBC at site
- All low height sockets to be 450mm from floor.
- All standard switches to be 1400mm from the floor. *Any alterations to this must be confirmed at site with the client/EA and the project manager.
- All kitchen sockets must be minimum 150mm above the finished worktop surface
- All proposed wall mount radiator must be minimum 50mm above skirting where possible.

LUMINARIES	
	Outdoor up & down wall light (LED GU10)
	Ceiling downlight (LED GU10s)
IP65	Ceiling downlight (IP65 Waterproof)
	Pendant light
IP65	Wall light(IP65 Waterproof)
	Wall light
IP65	Flood light (IP65 Waterproof)
	Ceiling mounted lighting
	1 Gang Switch - Rocker
	2 Gang Switch - Rocker
	3 Gang Switch - Rocker
	4 Gang Switch - Rocker
	1 Gang Switch - Dimmer
2 Dimmer	2 Gang Switch - Dimmer
3 Dimmer	3 Gang Switch - Dimmer
4 Dimmer	4 Gang Switch - Dimmer
POWER - *Refer notes for heights	
	Single Socket
	Double Socket
	Double Socket (Low level)
	Double Socket (Floor)
	Double Socket (mid height) - Min. 1050mm from the floor
	Double Socket with USB (mid height)
SS	Double Socket (shaver)
	Spur
	Spur (extractor fan)
IP65	External wall socket (IP65 Waterproof)
FUSE BOX	Fuse box

COMMUNICATION	
CS	Ceiling speaker
TV	TV Point
TEL	Telephone Socket
	TV Ariel
TV BOX	TV Box (Sky/Virgin)
	Wifi Internet Router
	Wifi Range Extender
	CAT6 Socket
DB	Door Bell
FIRE DETECTION & SAFETY	
CMD	Carbon Monoxide detector, mains operated, battery back up
SD	Smoke detector, mains operated, battery back up
HD	Heat detector, mains operated, battery back up
CAM	Ring Security Camera or similar approved by EA

Scale 1:100 @A3 0 1 2 3 4 5m
Scale 1:50 @A3 0 0.5 1 1.5 2 2.5m
Scale 1:20 @A3 0 20 40 60 80 100m


extension architecture
3 River Reach, Gartons Way, Battersea
London SW11 3SX
Tel (0208) 288 8950 Fax (0871) 918 2798
www.extensionarchitecture.co.uk

This drawing is prepared solely for design and planning submission purposes. It is not intended or suitable for either building regulations or construction purposes and should not be used for such. All dimension shall be check and confirmed with site rep. and any discrepancies between the drawings and site shall be reported to PM. This drawing to be read in conjunction with engineers specification and details.
For construction information please refer to all drawings and specification of works.

For any structural steelworks details please refer to structural engineer's drawings & calculations.

The copyright of the drawing and designs remains with Extension Architecture. All copies are only for information about the application, they may not be used for any other purpose without the express written permission of Extension Architecture.

CLIENT: Vik Barodia	NOTES			SCALE: 1:100	DATE: 01.08.2024
PROJECT: 1 Lambourne Drive, KT11 3LB	VERSION	DESCRIPTION	DATE	DRAWN: BOUSIA	VERSION
TITLE: G.F- Mechanical & Electrical drawing (1/2)				SHEET REF. NO: 1LD-TD-M&E-01	

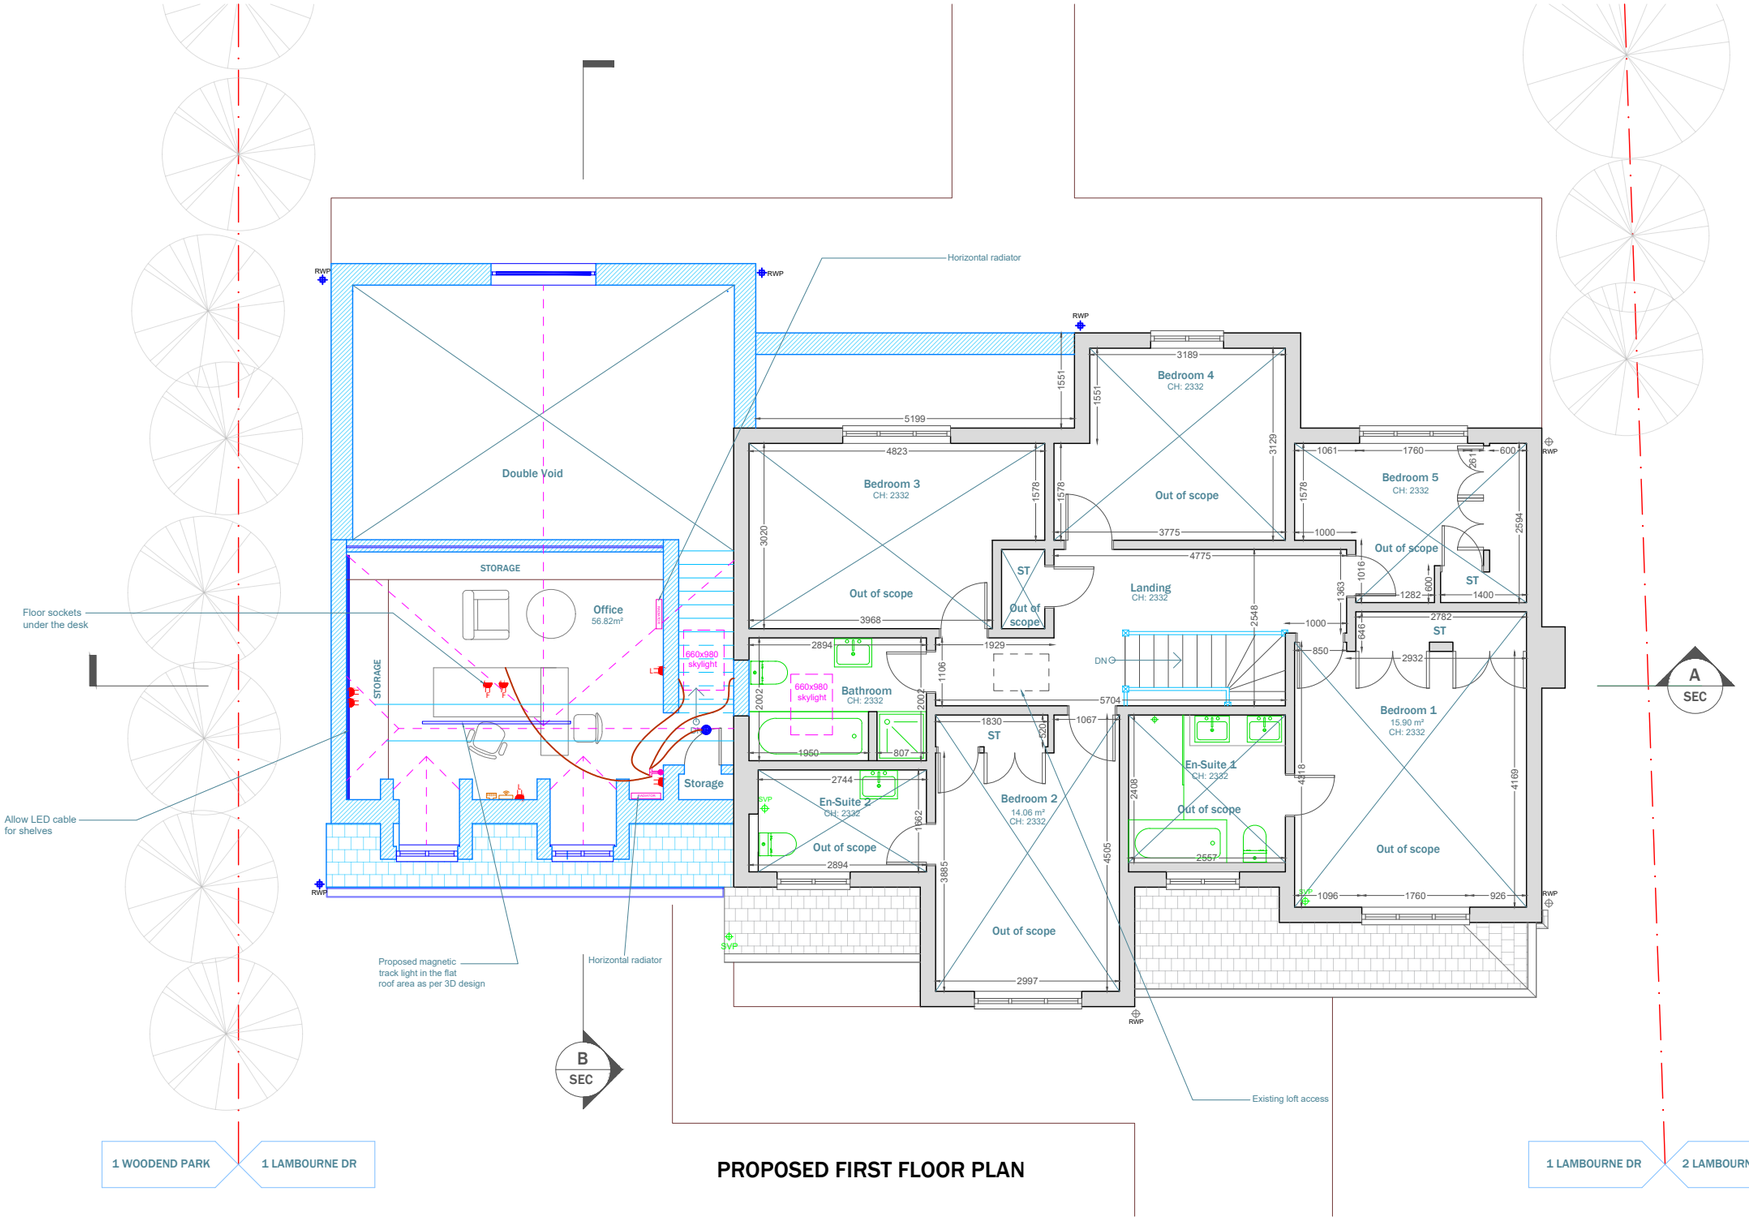

PROPOSED FIRST FLOOR PLAN

MECHANICAL & HEATING	
	Extractor fan (Ceiling mounted)
	Extractor fan (Wall mounted)
	Extractor fan (cooker hood)
W TANK	Water tank
BOILER	Boiler
ELEC METER	Electric meter
GAS METER	Gas meter
T	Thermostat
RADIATOR	Existing Radiator
RADIATOR	Proposed Radiator
TOWEL RAIL	Heated towel rail (duel fuel electric)
ELECTRIC CAR CHARGER	Electric car charger

Extra Notes:

- Extractor spur above door where possible
- All bedside sockets & switches to be 650mm from floor. *TBC at site
- All low height sockets to be 450mm from floor.
- All standard switches to be 1400mm from the floor. *Any alterations to this must be confirmed at site with the client/EA and the project manager.
- All kitchen sockets must be minimum 150mm above the finished worktop surface
- All proposed wall mount radiator must be minimum 50mm above skirting where possible.

LUMINARIES	
	Outdoor up & down wall light (LED GU10)
	Ceiling downlight (LED GU10s)
IP 65	Ceiling downlight (IP65 Waterproof)
	Pendant light
IP65	Wall light(IP65 Waterproof)
	Wall light
IP65	Flood light (IP65 Waterproof)
	Ceiling mounted lighting
	1 Gang Switch - Rocker
	2 Gang Switch - Rocker
	3 Gang Switch - Rocker
	4 Gang Switch - Rocker
	1 Gang Switch - Dimmer
2 Dimmer	2 Gang Switch - Dimmer
3 Dimmer	3 Gang Switch - Dimmer
4 Dimmer	4 Gang Switch - Dimmer
POWER - *Refer notes for heights	
L	Single Socket
	Double Socket
L	Double Socket (Low level)
F	Double Socket (Floor)
	Double Socket (mid height) - Min. 1050mm from the floor
USB	Double Socket with USB (mid height)
SS	Double Socket (shaver)
	Spur
F	Spur (extractor fan)
IP65	External wall socket (IP65 Waterproof)
FUSE BOX	Fuse box
COMMUNICATION	
CS	Ceiling speaker
TV	TV Point
TEL	Telephone Socket
	TV Ariel
TV BOX	TV Box (Sky/Virgin)
	Wifi Internet Router
	Wifi Range Extender
	CAT6 Socket
DB	Door Bell
FIRE DETECTION & SAFETY	
CMD	Carbon Monoxide detector, mains operated, battery back up
SD	Smoke detector, mains operated, battery back up
HD	Heat detector, mains operated, battery back up
CAM	Ring Security Camera or similar approved by EA

Scale 1:100 @A3 — 0 1 2 3 4 5m
Scale 1:50 @A3 — 0 0.5 1 1.5 2 2.5m
Scale 1:20 @A3 — 0 20 40 60 80 100m

extension architecture
3 River Reach, Gartons Way, Battersea
London SW11 3SX
Tel (0208) 288 8950 Fax (0871) 918 2798
www.extensionarchitecture.co.uk

This drawing is prepared solely for design and planning submission purposes. It is not intended or suitable for either building regulations or construction purposes and should not be used for such. All dimension shall be check and confirmed with site rep. and any discrepancies between the drawings and site shall be reported to PM. This drawing to be read in conjunction with engineers specification and details.
For construction information please refer to all drawings and specification of works.

For any structural steelworks details please refer to structural engineer's drawings & calculations.

The copyright of the drawing and designs remains with Extension Architecture. All copies are only for information about the application, they may not be used for any other purpose without the express written permission of Extension Architecture.

CLIENT: Vik Barodia	NOTES			SCALE: 1:100	DATE: 01.08.2024
PROJECT: 1 Lambourne Drive, KT11 3LB	VERSION	DESCRIPTION	DATE	DRAWN: BOUSIA	VERSION
TITLE: F.F - Mechanical & Electrical drawing (2/2)				SHEET REF. NO: 1LD-TD-M&E-02	

Pendant Lights
All pendant lights to be supplied by client and installed by contractor. Client to supply only the final fixture, all electrical work and associated materials required for installation to be supplied by contractor
Supply: Client
Installation: Contractor

Wall Mounted Lights (interior)
All inside wall mounted lights to be supplied by client and installed by contractor. Client to supply only the final fixture, all electrical work and associated materials required for installation to be supplied by contractor
Supply: Client
Installation: Contractor

Wall Mounted Lights (exterior)
All external wall mounted lights to be supplied by client and installed by contractor. Client to supply only the final fixture, all electrical work and associated materials required for installation to be supplied by contractor. To be IP65 rated.
Supply: Client
Installation: Contractor

LED Strip Lighting
All LED lighting to be supplied by contractor and installed by contractor including all associated materials required for installation, IP rated as required. 3000k warm light.
Supply: Contractor
Installation: Contractor

Ceiling Downlights - White Colour (LED GU10s)
All ceiling downlights **except dimmable LED downlights** to be supplied by contractor and installed by contractor including all associated materials required for installation, IP rated as required. To be; dimmable; LED; 3000k

Standard GU10s Supply: Contractor
Dimamble GU10 Supply : Client
Installation: Contractor

Sockets & Switches
Exposed sockets & switches finish:TBC
White 13A Double Plug Socket, client (TBC) to supply all power sockets, USB sockets, fuse switches, rocker switches, dimmer switches etc.from this range and ensure all have matching finish.
Supply: Client
Installation: Contractor
All Dimmer switches, transformer & dimmable LED downlights supplied by the client are to be checked with the supplier for good quality and a guarantee to avoid flickering. Contractor is **NOT liable if the right fit is not supplied.*

Concealed sockets and switches finish:
Sockets & switches inside kitchen units etc. or otherwise concealed (not viable) may be standard (MK Logic range) plain white fittings. All concealed sockets & switches are to be supplied by the contractor.
Supply: Contractor
Installation: Contractor

All Other Electrical Fittings
All other electrical fittings including fire alarms, smoke detectors, Thermostats, extractor fan for W/C to be supplied and fitted by contractor unless otherwise stated.
Supply: Contractor
Installation: Contractor

Ceiling speakers, wifi router & extender, TV box are to be arranged and supplied by Client
Supply: Client
Installation: Contractor

Existing Radiators
All existing radiators in the First floor to be retained.
Supply: N/A

Proposed Radiators and suitable valves
One proposed radiator in the double storey extension.
One proposed radiator in the loft.
*Client to check the suitable radiator valves for wall or floor mount radiator before purchase as per design.

Supply: Client
Installation: Contractor
***Contractor to confirm wall or floor mount at the site as per site condition**

MECHANICAL & HEATING	
	Extractor fan (Ceiling mounted)
	Extractor fan (Wall mounted)
	Extractor fan (cooker hood)
W TANK	Water tank
BOILER	Boiler
ELEC METER	Electric meter
GAS METER	Gas meter
T	Thermostat
RADIATOR	Existing Radiator
RADIATOR	Proposed Radiator
TOWEL RAIL	Heated towel rail (duel fuel electric)
ELECTRIC CAR CHARGER	Electric car charger

Extra Notes:

- Extractor spur above door where possible
- All bedside sockets & switches to be 650mm from floor. *TBC at site
- All low height sockets to be 450mm from floor.
- All standard switches to be 1400mm from the floor. *Any alterations to this must be confirmed at site with the client/EA and the project manager.
- All kitchen sockets must be minimum 150mm above the finished worktop surface
- RAD All proposed wall mount radiator must be minimum 50mm above skirting where possible.

LUMINARIES	
	Outdoor up & down wall light (LED GU10)
	Ceiling downlight (LED GU10s)
IP65	Ceiling downlight (IP65 Waterproof)
	Pendant light
IP65	Wall light(IP65 Waterproof)
	Wall light
IP65	Flood light (IP65 Waterproof)
	Ceiling mounted lighting
	1 Gang Switch - Rocker
	2 Gang Switch - Rocker
	3 Gang Switch - Rocker
	4 Gang Switch - Rocker
	1 Gang Switch - Dimmer
2 Dimmer	2 Gang Switch - Dimmer
3 Dimmer	3 Gang Switch - Dimmer
4 Dimmer	4 Gang Switch - Dimmer
POWER - *Refer notes for heights	
L	Single Socket
	Double Socket
L	Double Socket (Low level)
F	Double Socket (Floor)
	Double Socket (mid height) - Min. 1050mm from the floor
	Double Socket with USB (mid height)
SS	Double Socket (shaver)
	Spur
	Spur (extractor fan)
IP65	External wall socket (IP65 Waterproof)
FUSE BOX	Fuse box
COMMUNICATION	
CS	Ceiling speaker
TV ▷	TV Point
TEL ▶	Telephone Socket
	TV Ariel
TV BOX	TV Box (Sky/Virgin)
	Wifi Internet Router
	Wifi Range Extender
	CAT6 Socket
DB	Door Bell
FIRE DETECTION & SAFETY	
CMD	Carbon Monoxide detector, mains operated, battery back up
SD	Smoke detector, mains operated, battery back up
HD	Heat detector, mains operated, battery back up
CAM	Ring Security Camera or similar approved by EA

Scale 1:100 @A3 0 1 2 3 4 5m
Scale 1:50 @A3 0 0.5 1 1.5 2 2.5m
Scale 1:20 @A3 0 20 40 60 80 100m

extension architecture
3 River Reach, Gartons Way, Battersea
London SW11 3SX
Tel (0208) 288 8950 Fax (0871) 918 2798
www.extensionarchitecture.co.uk

This drawing is prepared solely for design and planning submission purposes. It is not intended or suitable for either building regulations or construction purposes and should not be used for such. All dimension shall be check and confirmed with site rep. and any discrepancies between the drawings and site shall be reported to PM. This drawing to be read in conjunction with engineers specification and details.
For construction information please refer to all drawings and specification of works.

For any structural steelworks details please refer to structural engineer's drawings & calculations.

The copyright of the drawing and designs remains with Extension Architecture. All copies are only for information about the application, they may not be used for any other purpose without the express written permission of Extension Architecture.

CLIENT: Vik Barodia	NOTES			SCALE: N/A	DATE: 01.08.2024
PROJECT: 1 Lambourne Drive, KT11 3LB	VERSION	DESCRIPTION	DATE	DRAWN: BOUSIA	VERSION
TITLE: **Notes - Mechanical & Electrical drawing**				SHEET REF. NO: 1LD-TD-M&E-03	