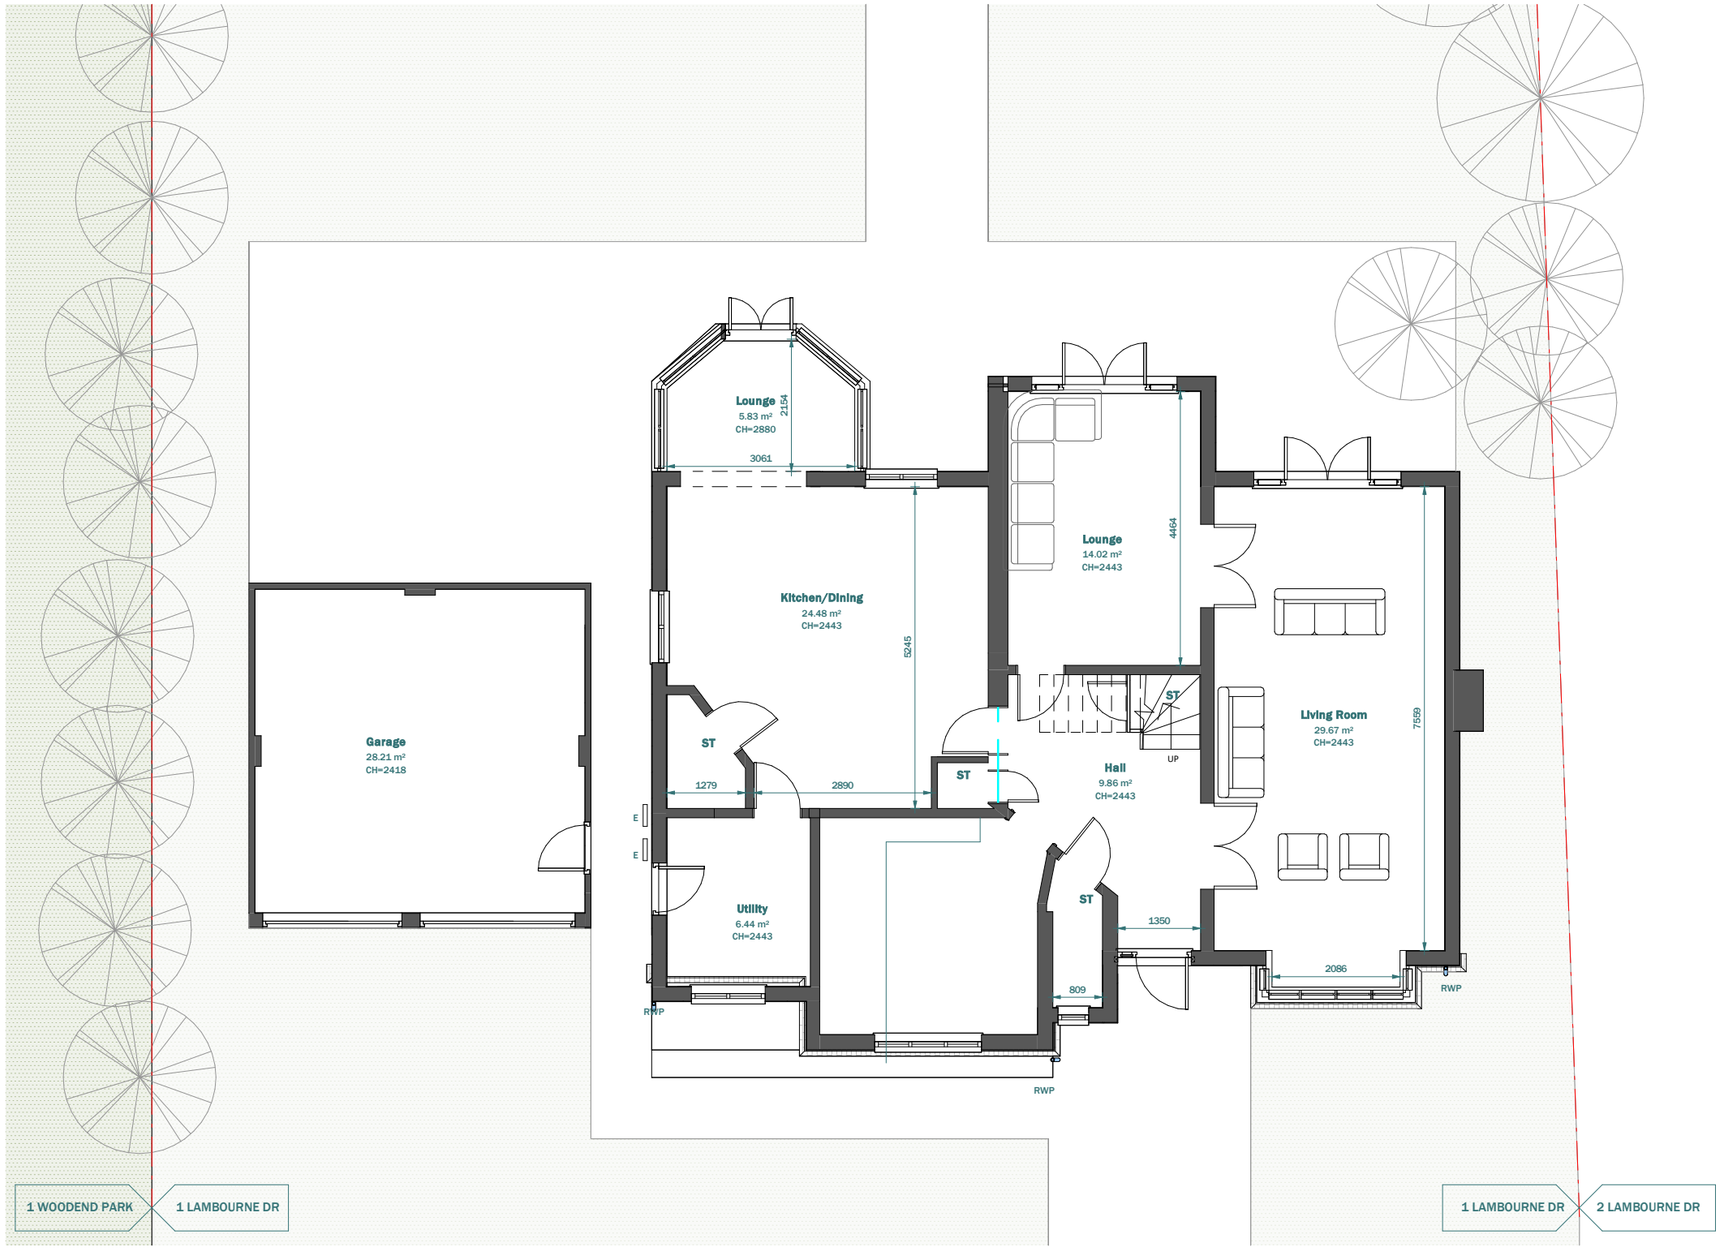


Existing Ground Floor Plan

1 : 100

Scale 1:100
@A3

1m 10m

extension architecture


3 River Reach, Gartons Way,
Battersea
London SW11 3SX
Tel (0208) 288 8950 Fax (0871) 918 2798
www.extensionarchitecture.co.uk

This drawing is prepared solely for design and planning submission purposes. It is not intended or suitable for either building regulations or construction purposes and should not be used for such. All dimension shall be check and confirmed with site rep. and any discrepancies between the drawings and site shall be reported to PM. This drawing to be read in conjunction with engineers specification and details. For construction information please refer to all drawings and specification of works.

For any structural steelworks details please refer to structural engineer's drawings & calculations.

The copyright of the drawing and designs remains with Extension Architecture. All copies are only for information about the application, they may not be used for any other purpose without the express written permission of Extension Architecture.

CLIENT: Vik Barodia	NOTES			SCALE: 1 : 100	DATE: 12.04.2024
PROJECT: 1 Lambourne Drive, KT11 3LB	VERSION	DESCRIPTION	DATE	DRAWN: AY	VERSION
TITLE: Existing Floor Plans				SHEET REF. NO: 1 LD -PL -BR 01	

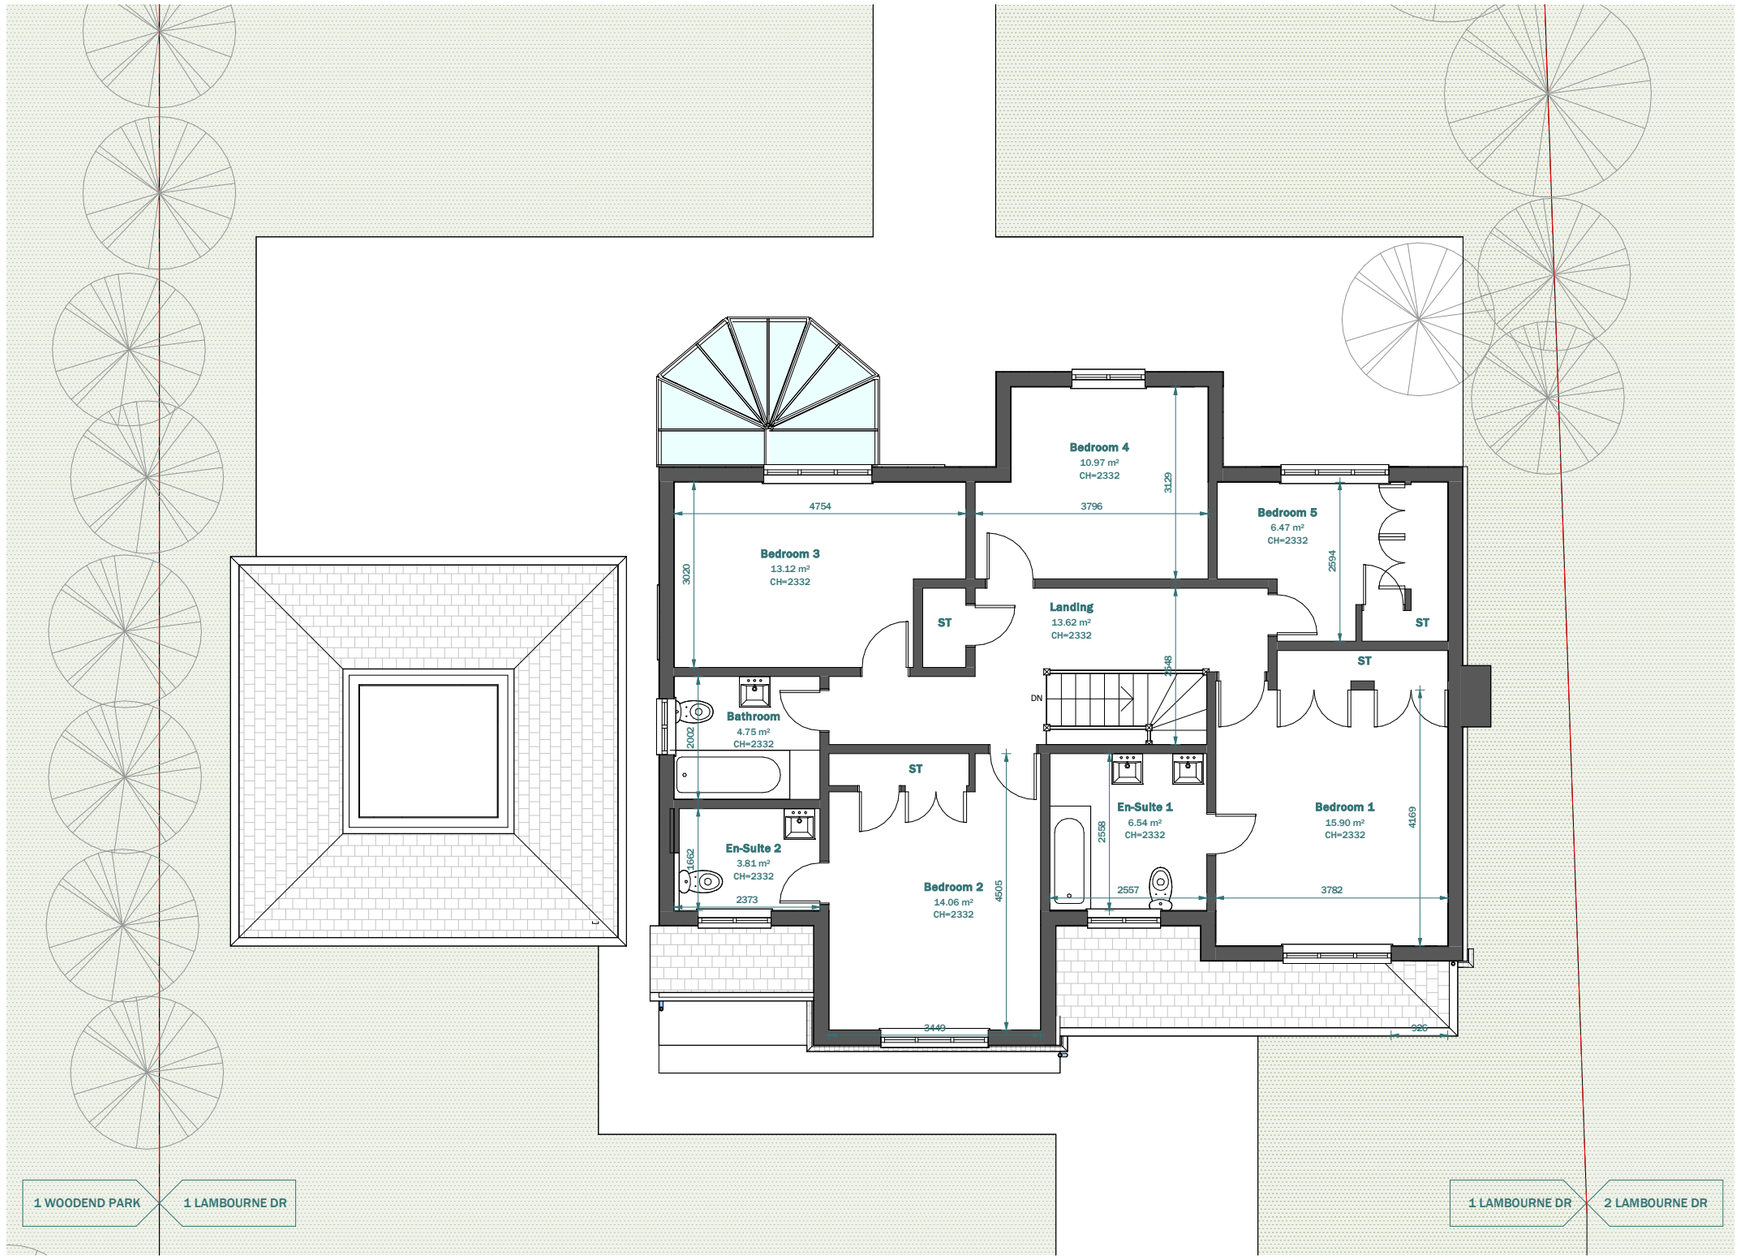

Existing First Floor Plan

1 : 100

Scale 1:100
@A3

1m 10m

extension architecture


3 River Reach, Gartons Way,
Battersea
London SW11 3SX
Tel (0208) 288 8950 Fax (0871) 918 2798
www.extensionarchitecture.co.uk

This drawing is prepared solely for design and planning submission purposes. It is not intended or suitable for either building regulations or construction purposes and should not be used for such. All dimension shall be check and confirmed with site rep. and any discrepancies between the drawings and site shall be reported to PM. This drawing to be read in conjunction with engineers specification and details. For construction information please refer to all drawings and specification of works.

For any structural steelworks details please refer to structural engineer's drawings & calculations.

The copyright of the drawing and designs remains with Extension Architecture. All copies are only for information about the application, they may not be used for any other purpose without the express written permission of Extension Architecture.

CLIENT: Vik Barodia	NOTES			SCALE: 1 : 100	DATE: 12.04.2024
PROJECT: 1 Lambourne Drive, KT11 3LB	VERSION	DESCRIPTION	DATE	DRAWN: AY	VERSION
TITLE: Existing Floor Plans				SHEET REF. NO: 1 LD -PL -BR 02	

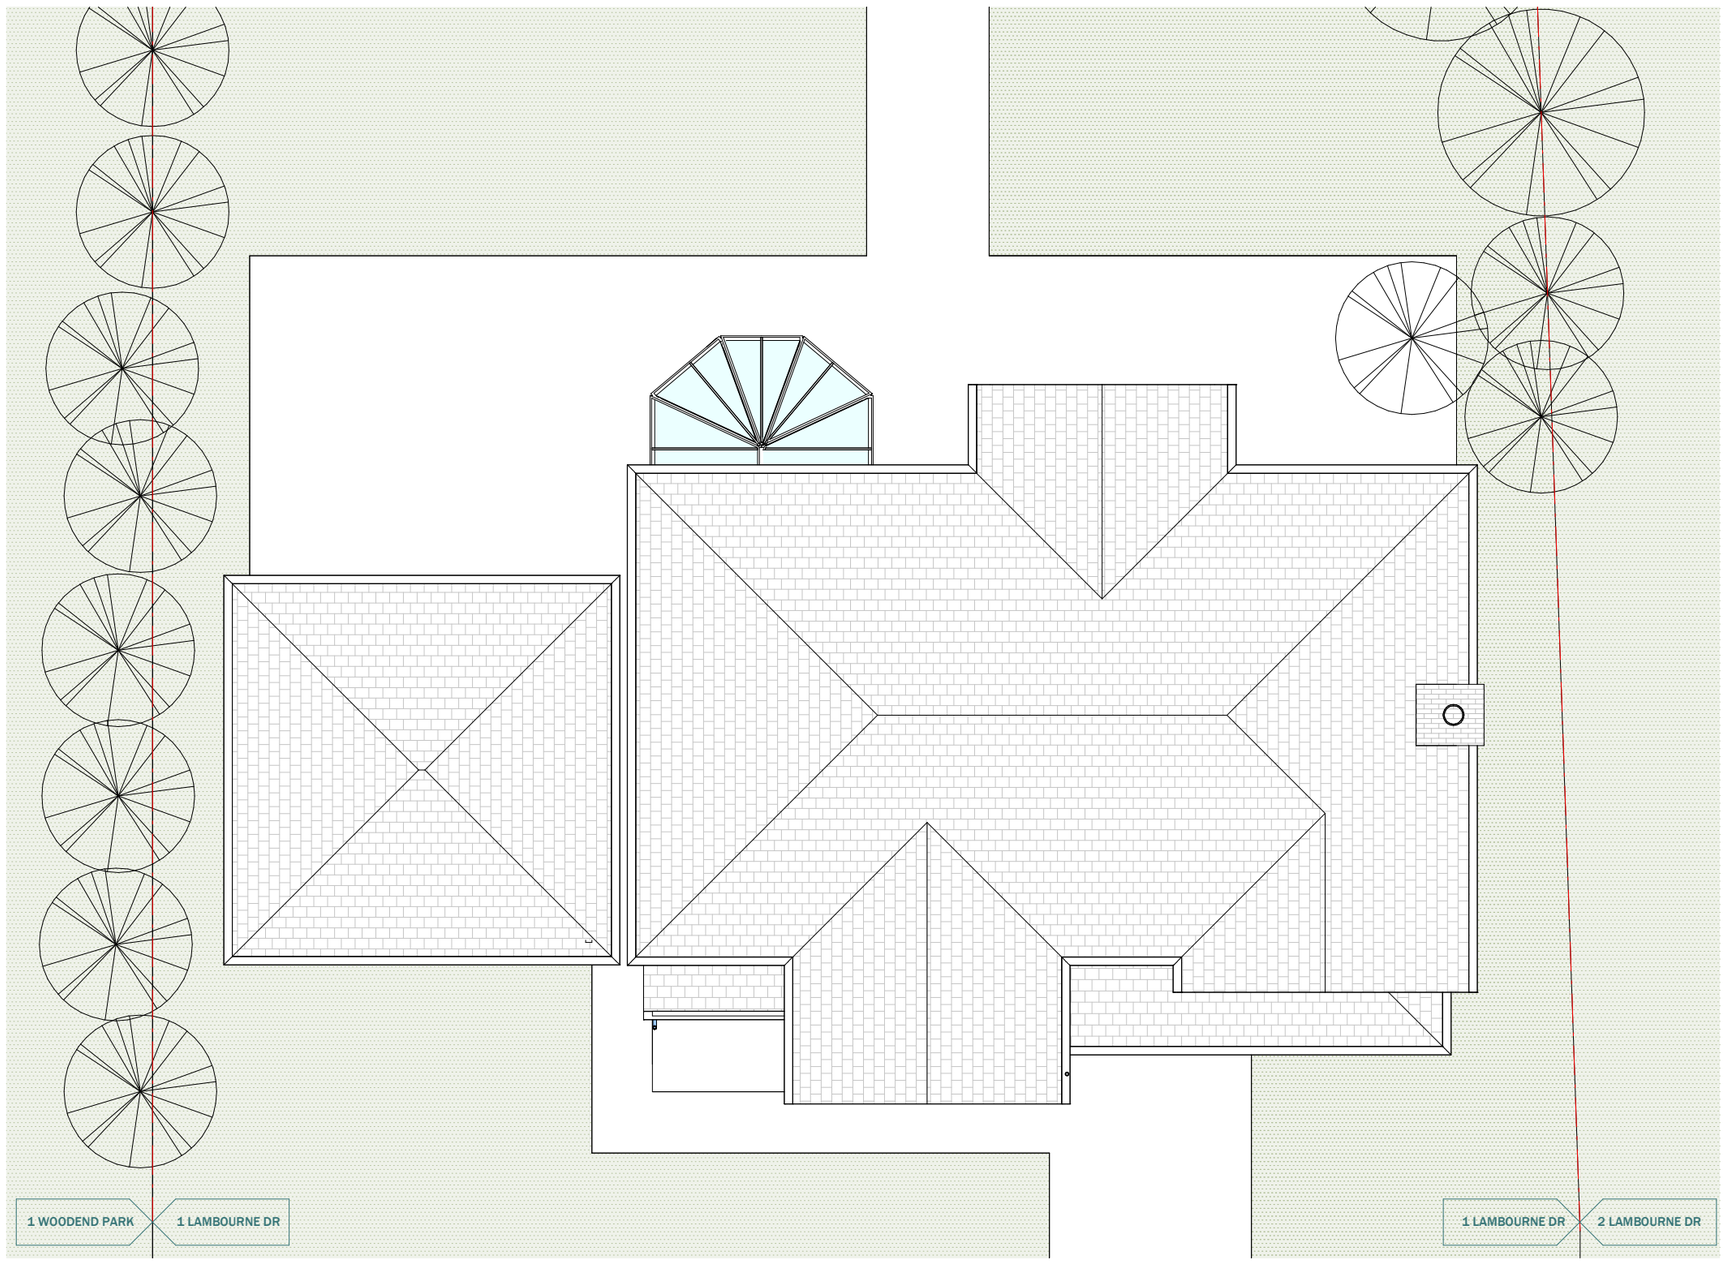

Existing Roof Plan

1 : 100

Scale 1:100
@A3

1m 10m

extension architecture

3 River Reach, Gartons Way,
Battersea
London SW11 3SX
Tel (0208) 288 8950 Fax (0871) 918 2798
www.extensionarchitecture.co.uk

This drawing is prepared solely for design and planning submission purposes. It is not intended or suitable for either building regulations or construction purposes and should not be used for such. All dimension shall be check and confirmed with site rep. and any discrepancies between the drawings and site shall be reported to PM. This drawing to be read in conjunction with engineers specification and details. For construction information please refer to all drawings and specification of works.

For any structural steelworks details please refer to structural engineer's drawings & calculations.

The copyright of the drawing and designs remains with Extension Architecture. All copies are only for information about the application, they may not be used for any other purpose without the express written permission of Extension Architecture.

CLIENT: Vik Barodia	NOTES			SCALE: 1 : 100	DATE: 12.04.2024
PROJECT: 1 Lambourne Drive, KT11 3LB	VERSION	DESCRIPTION	DATE	DRAWN: AY	VERSION
TITLE: Existing Floor Plans				SHEET REF. NO: 1 LD -PL -BR 03	



Existing Front Elevation

1 : 100



Existing Rear Elevation

1 : 100

Scale 1:100
@A3

1m 10m

extension architecture


3 River Reach, Gartons Way,
Battersea
London SW11 3SX
Tel (0208) 288 8950 Fax (0871) 918 2798
www.extensionarchitecture.co.uk

This drawing is prepared solely for design and planning submission purposes. It is not intended or suitable for either building regulations or construction purposes and should not be used for such. All dimension shall be check and confirmed with site rep. and any discrepancies between the drawings and site shall be reported to PM. This drawing to be read in conjunction with engineers specification and details. For construction information please refer to all drawings and specification of works.


For any structural steelworks details please refer to structural engineer's drawings & calculations.

The copyright of the drawing and designs remains with Extension Architecture. All copies are only for information about the application, they may not be used for any other purpose without the express written permission of Extension Architecture.

CLIENT: Vik Barodia	NOTES			SCALE: 1 : 100	DATE: 12.04.2024
PROJECT: 1 Lambourne Drive, KT11 3LB	VERSION	DESCRIPTION	DATE	DRAWN: AY	VERSION
TITLE: Existing Front/Rear Elevations				SHEET REF. NO: 1 LD -PL -BR 04	

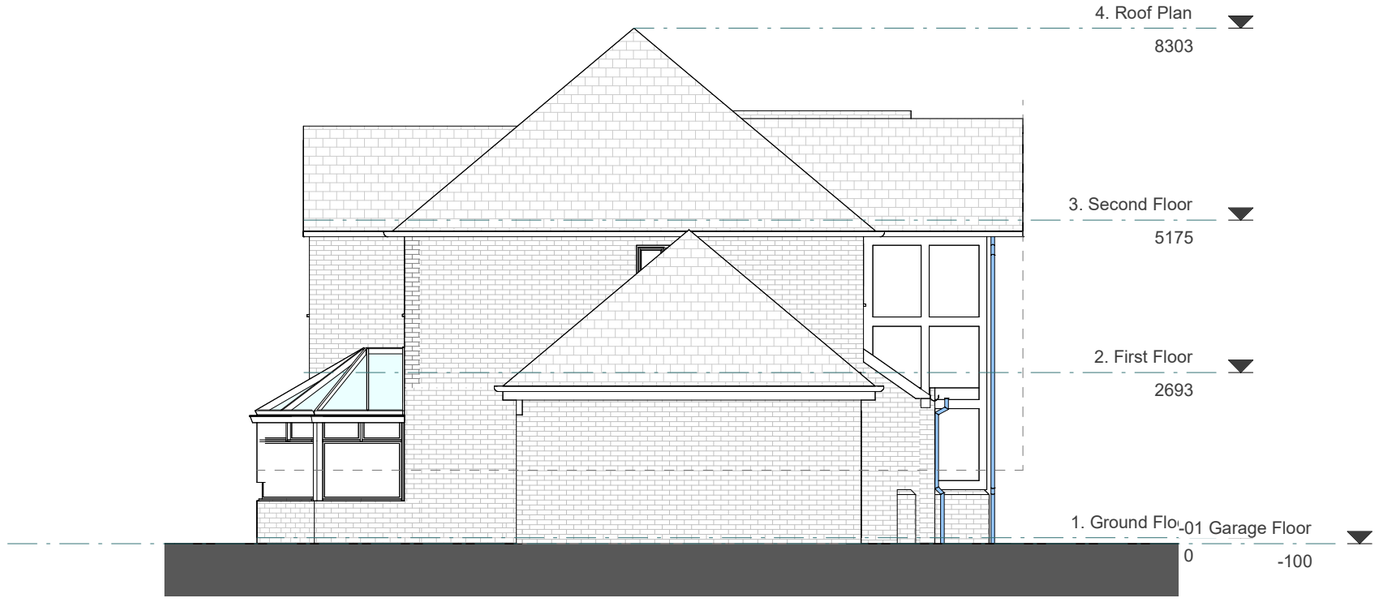

Existing Left Elevation
1 : 100

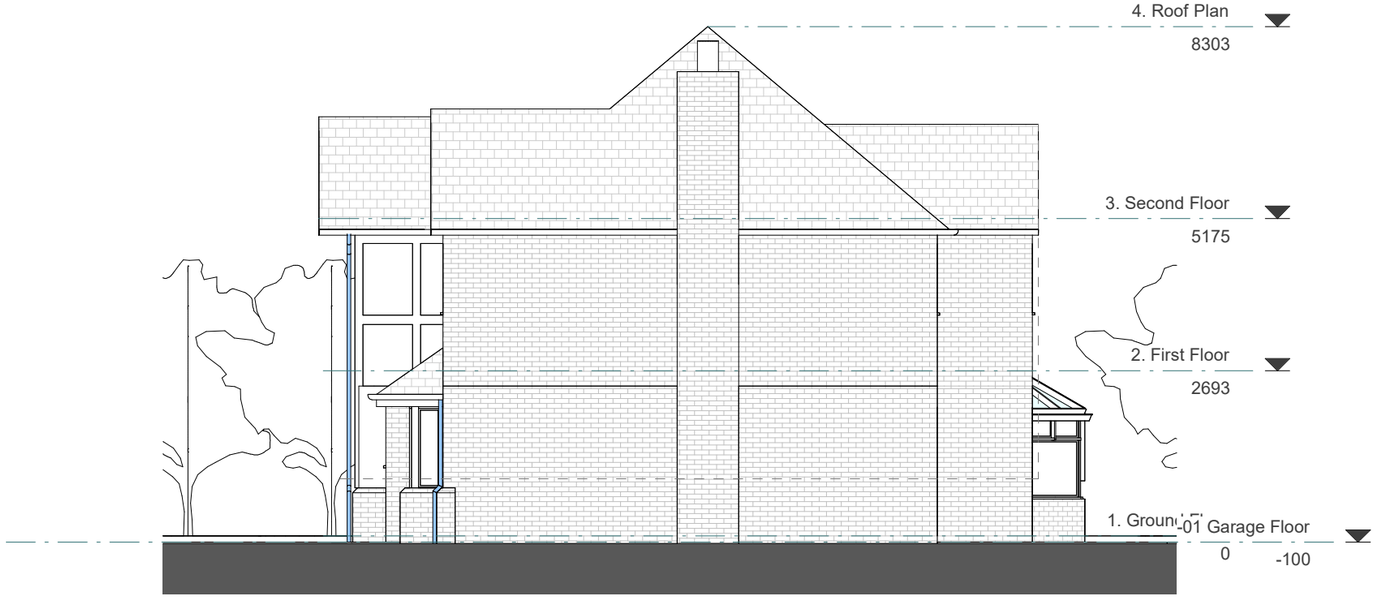

Existing Right Elevation
1 : 100

Scale 1:100
@A3

1m 10m


extension architecture
3 River Reach, Gartons Way,
Battersea
London SW11 3SX
Tel (0208) 288 8950 Fax (0871) 918 2798
www.extensionarchitecture.co.uk

This drawing is prepared solely for design and planning submission purposes. It is not intended or suitable for either building regulations or construction purposes and should not be used for such. All dimension shall be check and confirmed with site rep. and any discrepancies between the drawings and site shall be reported to PM. This drawing to be read in conjunction with engineers specification and details. For construction information please refer to all drawings and specification of works.

For any structural steelworks details please refer to structural engineer's drawings & calculations.

The copyright of the drawing and designs remains with Extension Architecture. All copies are only for information about the application, they may not be used for any other purpose without the express written permission of Extension Architecture.

CLIENT: Vik Barodia	NOTES			SCALE: 1 : 100	DATE: 12.04.2024
PROJECT: 1 Lambourne Drive, KT11 3LB	VERSION	DESCRIPTION	DATE	DRAWN: AY	VERSION
TITLE: Existing Side Elevations				SHEET REF. NO: 1 LD -PL -BR 05	

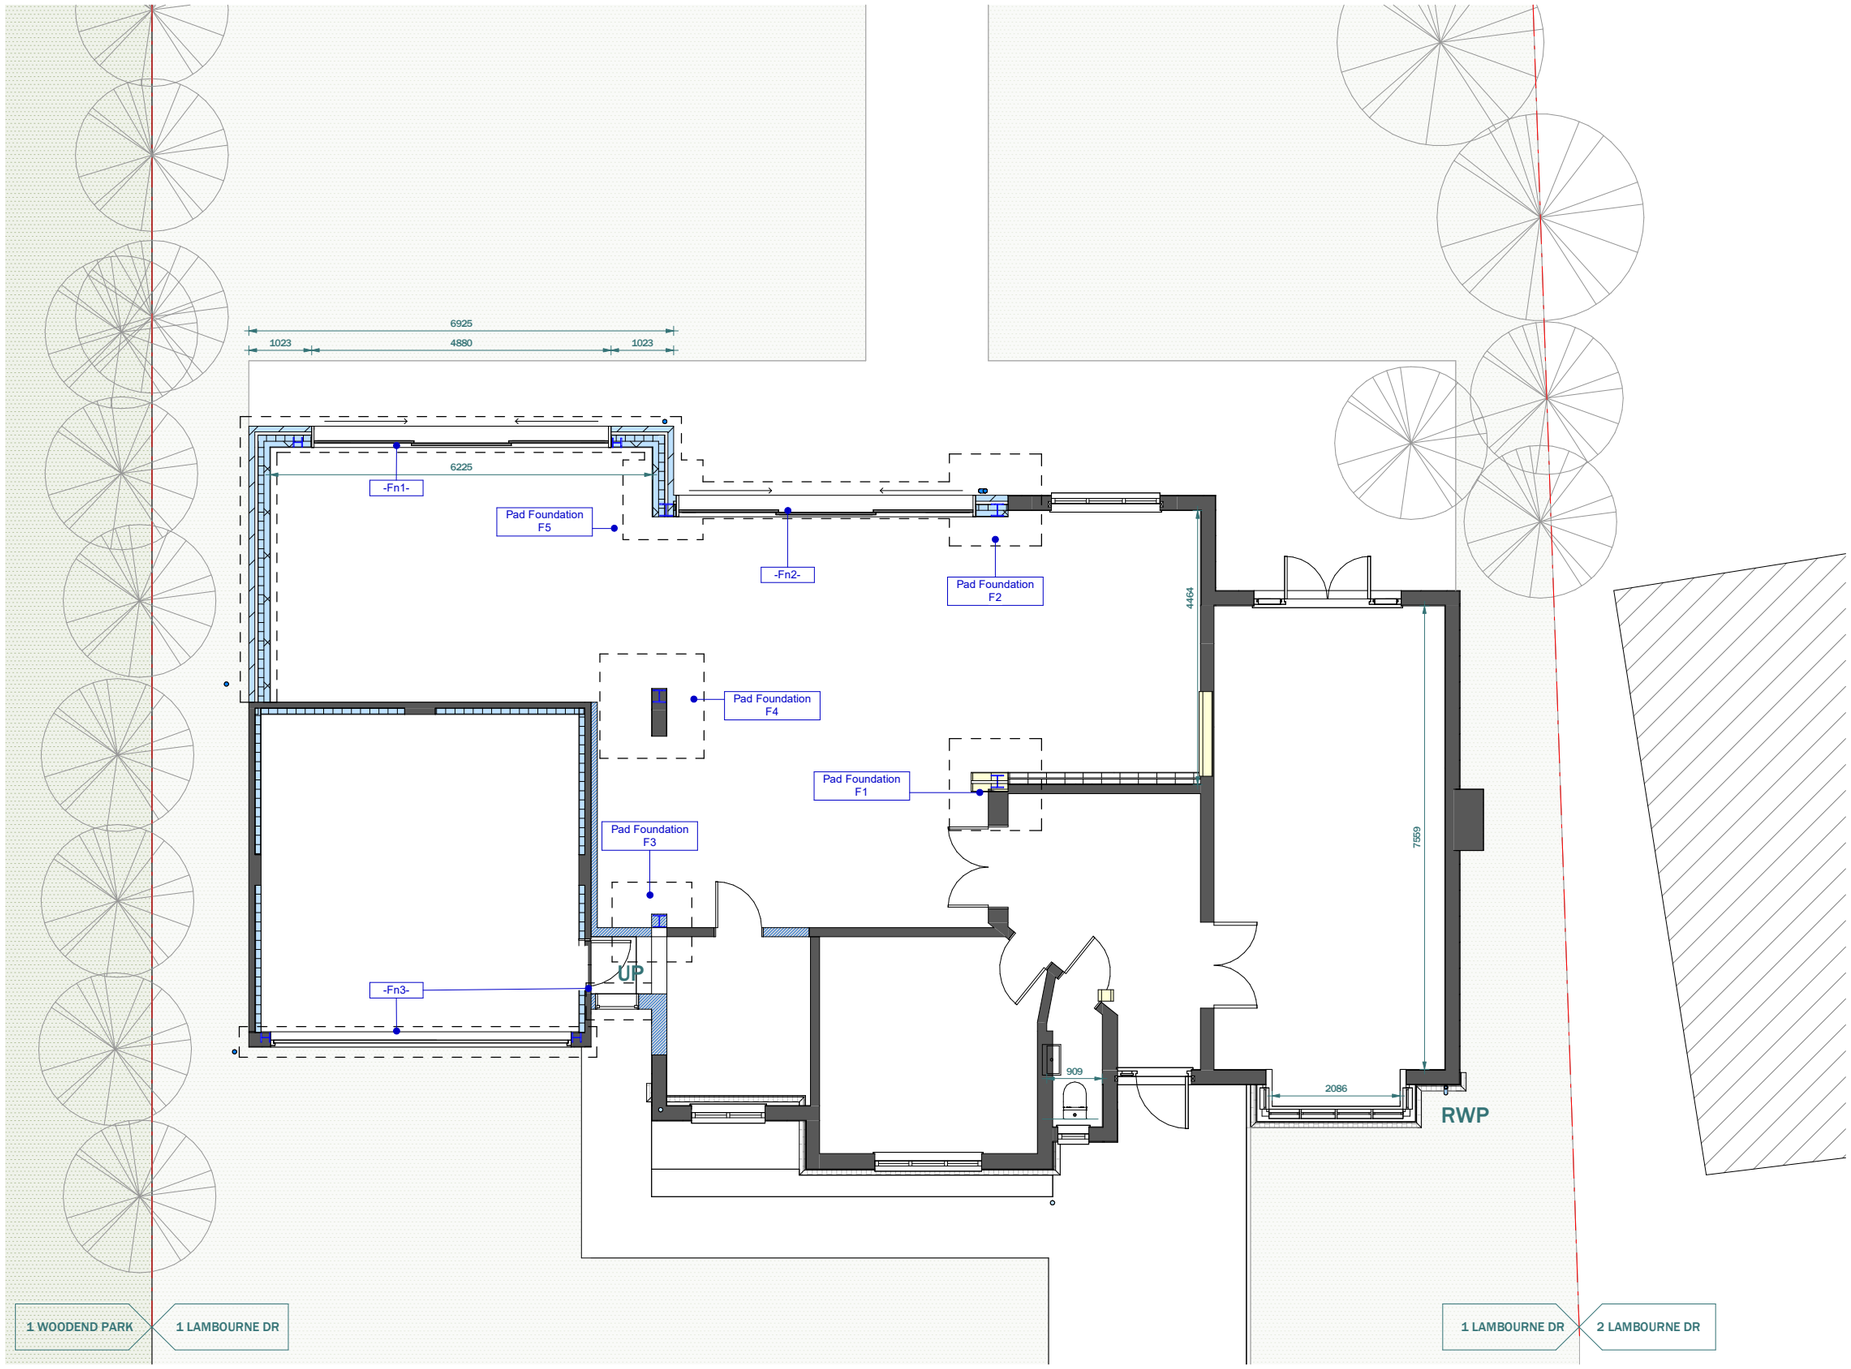

DRAWINGS KEYS

- New Slab Ground Floor
- New Intermediate Timber Floor
- Upgrated Intermediate Floor
- Roof Terrace
- Upgraded Garage Floor
- Upgraded Garage Floor
- Proposed -EXT- Construction Elements
- Proposed -INT- Construction Elements
- Existing Construction Elements
- Fire Rated Elements
- Structural Steel Beams
- Padstone
- Timber Beams
- Fire Route
- Existing Demolished
- Proposed Fondations
- Assumed Existing Sewer
- Proposed Sewer
- Existing Sewer
- Rain Water Drainage Direction
- Air Extraction Route
- Proposed Joists/Rafters Direction
- Existing Joists/Rafters Direction
- Lintels
- Slope Direction
- Concrete Slab Floor
- Fire Door
- Areas under party wall matters
- SD SMOKE DETECTION & ALARM SYSTEM
- HD HEAT DETECTION & ALARM SYSTEM
- FB FIRE BLANKET
- EXTRACTOR FAN
- HOB GAS/INDUCTION HOB
- HOOD ELECTRIC HOOD
- FIRE EXTINGUISHER
- Extractor Over HOB 30l/s
- Extractor through Wall / Window 30l / S for Kitchen Hob and 60l/S Elsewhere
- Vent Vertical Flue Vent - Through The Roof
- SS (Soil Stack)

Proposed Foundation Floor Plan

1 : 100

Scale 1:100 @A3

1m 10m

extension architecture
3 River Reach, Gartons Way, Battersea
London SW11 3SX
Tel (0208) 288 8950 Fax (0871) 918 2798
www.extensionarchitecture.co.uk

These architectural drawings are prepared by Extension Architecture and are intended for Building Regulation purposes. For any questions regarding regulatory compliance or specific Building Control requirements, please consult your local Building Control Authority. It is highly advisable to liaise with your local Building Control Authority to discuss the specific requirements and to ensure that these drawings align with the local regulations. The builder or contractor should coordinate with Building Control for any necessary site inspections and approvals. While these drawings have been created with utmost care, all measurements and specifications should be validated on-site by the builder or contractor prior to construction. These drawings will serve as a foundation for your discussions with the Building Control Authority. Any modifications or additional documents required for their approval should be addressed in collaboration with the local authority. As part of the construction process, the builder or contractor should maintain comprehensive records of compliance with the Building Regulations, including any changes or variations made during construction.
In the event of on-site changes, queries, or discrepancies, and you wish for Extension Architecture to oversee the construction process, please be aware that this service is chargeable. In the event of any builder errors or issues that necessitate our intervention, a fee would be applicable for Extension Architecture's Project Manager services. All drawings should be read in conjunction with the Structural Engineers drawings. The copyright of the drawing and designs remains with Extension Architecture. All copies are only for information about the application, they may not be used for any other purpose without the express written permission of Extension Architecture.

CLIENT: **Vik Barodia**

PROJECT: **1 Lambourne Drive, KT11 3LB**

TITLE: **Proposed Floor Plans**

NOTES

VERSION	DESCRIPTION	DATE


SCALE

DATE: **12.04.2024**

DRAWN: **AY**

VERSION

SHEET REF. NO: **1 LD -PL -BR 06**

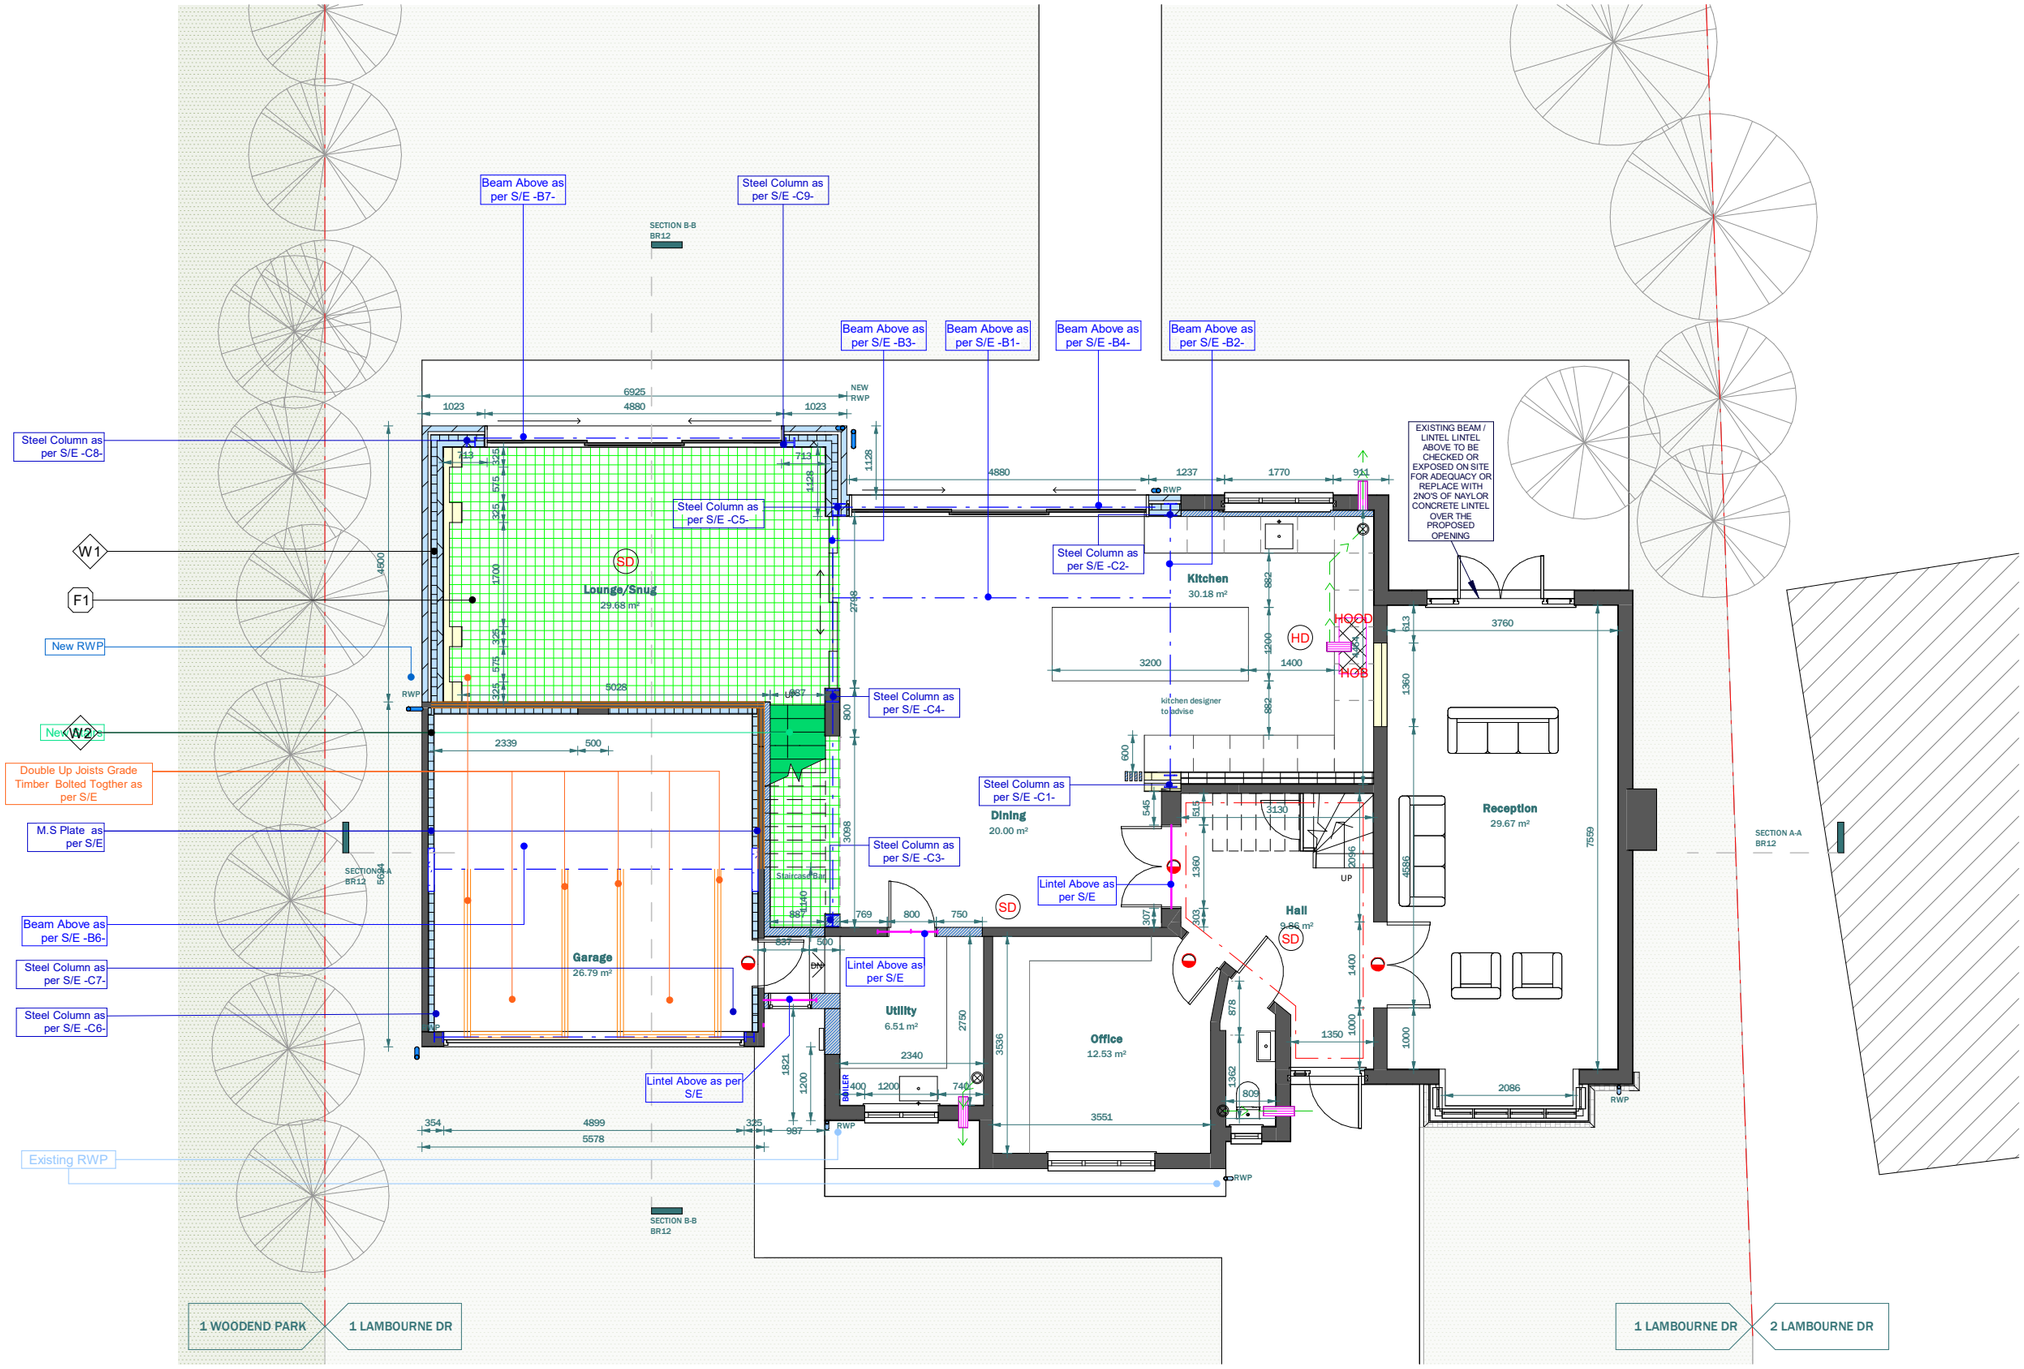

1-Proposed Ground Floor Plan

1 : 100

Scale 1:100 @A3

1m 10m

DRAWINGS KEYS


- New Slab Ground Floor
- New Intermediate Timber Floor
- Upgrated Intermediate Floor
- Roof Terrace
- Upgraded Garage Floor
- Upgraded Garage Floor
- Proposed -EXT- Construction Elements
- Proposed -INT- Construction Elements
- Existing Construction Elements
- Fire Rated Elements
- Structural Steel Beams
- Padstone
- Timber Beams
- Fire Route
- Existing Demolished
- Proposed Fondations
- Assumed Existing Sewer
- Proposed Sewer
- Existing Sewer
- Rain Water Drainage Direction
- Air Extraction Route
- Proposed Joists/Rafters Direction
- Existing Joists/Rafters Direction
- Lintels
- Slope Direction
- Concrete Slab Floor
- Fire Door
- Areas under party wall matters

SD SMOKE DETECTION & ALARM SYSTEM
HD HEAT DETECTION & ALARM SYSTEM
FB FIRE BLANKET
EXTRACTOR FAN
HOB GAS/INDUCTION HOB
HOOD ELECTRIC HOOD
FIRE EXTINGUISHER
Extractor Over HOB 30l/s
Extractor through Wall / Window 30l / S for Kitchen Hob and 60l/S Elsewhere
Vent Vertical Flue Vent - Through The Roof
SS (Soil Stack)

extension architecture
3 River Reach, Gartons Way, Battersea
London SW11 3SX
Tel (0208) 288 8950 Fax (0871) 918 2798
www.extensionarchitecture.co.uk

These architectural drawings are prepared by Extension Architecture and are intended for Building Regulation purposes. For any questions regarding regulatory compliance or specific Building Control requirements, please consult your local Building Control Authority. It is highly advisable to liaise with your local Building Control Authority to discuss the specific requirements and to ensure that these drawings align with the local regulations. The builder or contractor should coordinate with Building Control for any necessary site inspections and approvals. While these drawings have been created with utmost care, all measurements and specifications should be validated on-site by the builder or contractor prior to construction. These drawings will serve as a foundation for your discussions with the Building Control Authority. Any modifications or additional documents required for their approval should be addressed in collaboration with the local authority. As part of the construction process, the builder or contractor should maintain comprehensive records of compliance with the Building Regulations, including any changes or variations made during construction.
In the event of on-site changes, queries, or discrepancies, and you wish for Extension Architecture to oversee the construction process, please be aware that this service is chargeable. In the event of any builder errors or issues that necessitate our intervention, a fee would be applicable for Extension Architecture's Project Manager services. All drawings should be read in conjunction with the Structural Engineers drawings. The copyright of the drawing and designs remains with Extension Architecture. All copies are only for information about the application, they may not be used for any other purpose without the express written permission of Extension Architecture.

CLIENT: Vik Barodia	NOTES			SCALE	DATE: 12.04.2024
PROJECT: 1 Lambourne Drive, KT11 3LB	VERSION	DESCRIPTION	DATE	DRAWN: AY	VERSION
TITLE: Proposed Floor Plans				SHEET REF. NO: 1 LD -PL -BR 07	

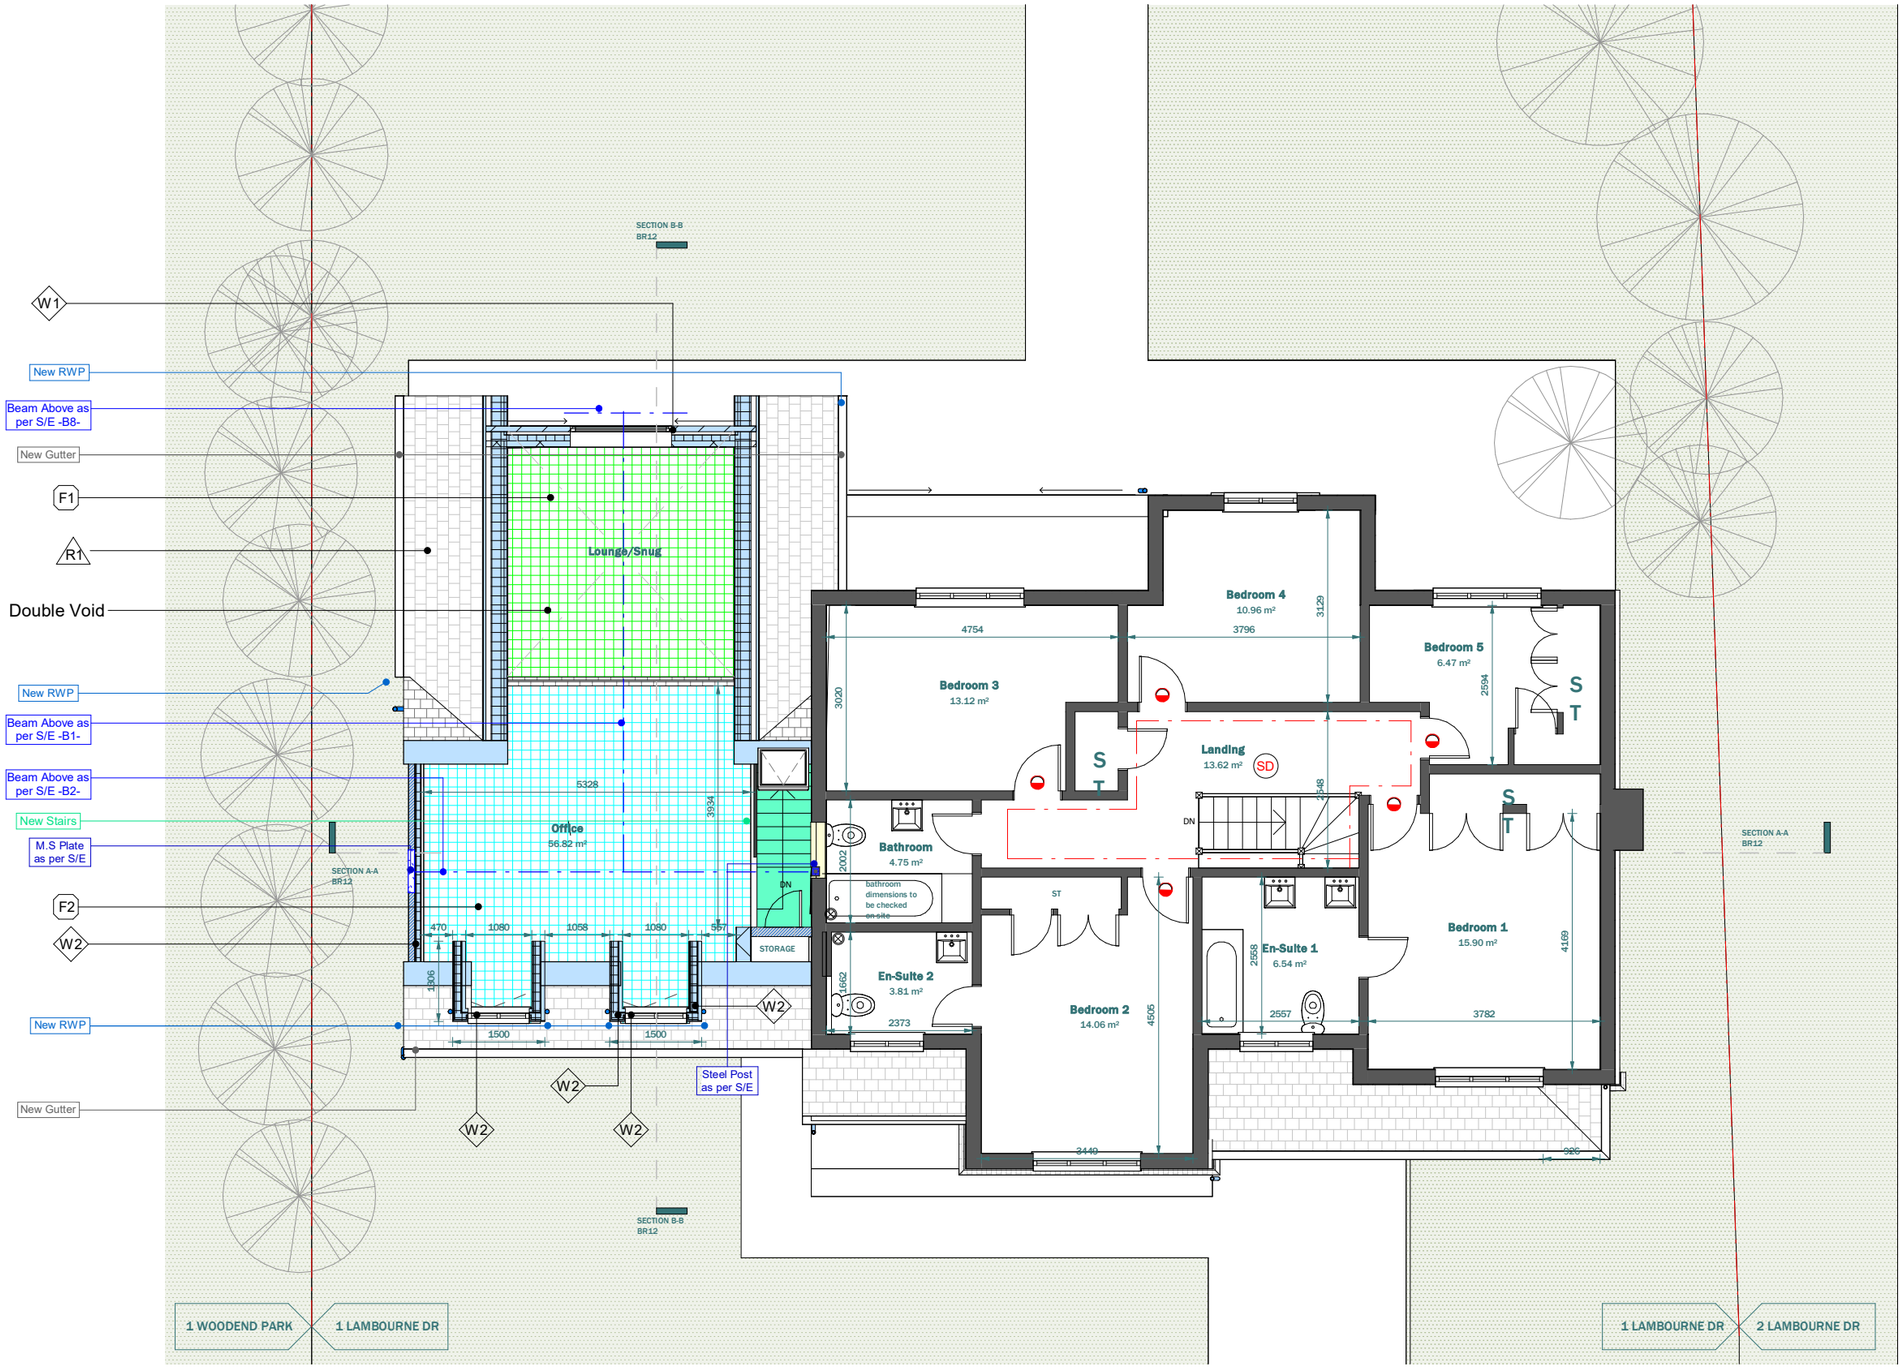

Proposed First Floor Plan

1 : 100

Scale 1:100 @A3

1m 10m

DRAWINGS KEYS

- New Slab Ground Floor
- New Intermediate Timber Floor
- Upgrated Intermediate Floor
- Roof Terrace
- Upgraded Garage Floor
- Upgraded Garage Floor
- Proposed -EXT- Construction Elements
- Proposed -INT- Construction Elements
- Existing Construction Elements
- Fire Rated Elements
- Structural Steel Beams
- Padstone
- Timber Beams
- Fire Route
- Existing Demolished
- Proposed Fondations
- Assumed Existing Sewer
- Proposed Sewer
- Existing Sewer
- Rain Water Drainage Direction
- Air Extraction Route
- Proposed Joists/Rafters Direction
- Existing Joists/Rafters Direction
- Lintels
- Slope Direction
- Concrete Slab Floor
- Fire Door
- Areas under party wall matters

(SD) SMOKE DETECTION & ALARM SYSTEM
(HD) HEAT DETECTION & ALARM SYSTEM
FB FIRE BLANKET
EXTRACTOR FAN
HOB GAS/INDUCTION HOB
HOOD ELECTRIC HOOD
FIRE EXTINGUISHER
Extractor Over HOB 30l/s
Extractor through Wall / Window 30l / S for Kitchen Hob and 60l/S Elsewhere
Vent Vertical Flue Vent - Through The Roof
SS (Soil Stack)

extension architecture
3 River Reach, Gartons Way, Battersea
London SW11 3SX
Tel (0208) 288 8950 Fax (0871) 918 2798
www.extensionarchitecture.co.uk

These architectural drawings are prepared by Extension Architecture and are intended for Building Regulation purposes. For any questions regarding regulatory compliance or specific Building Control requirements, please consult your local Building Control Authority. It is highly advisable to liaise with your local Building Control Authority to discuss the specific requirements and to ensure that these drawings align with the local regulations. The builder or contractor should coordinate with Building Control for any necessary site inspections and approvals. While these drawings have been created with utmost care, all measurements and specifications should be validated on-site by the builder or contractor prior to construction. These drawings will serve as a foundation for your discussions with the Building Control Authority. Any modifications or additional documents required for their approval should be addressed in collaboration with the local authority. As part of the construction process, the builder or contractor should maintain comprehensive records of compliance with the Building Regulations, including any changes or variations made during construction.
In the event of on-site changes, queries, or discrepancies, and you wish for Extension Architecture to oversee the construction process, please be aware that this service is chargeable. In the event of any builder errors or issues that necessitate our intervention, a fee would be applicable for Extension Architecture's Project Manager services. All drawings should be read in conjunction with the Structural Engineers drawings. The copyright of the drawing and designs remains with Extension Architecture.
All copies are only for information about the application, they may not be used for any other purpose without the express written permission of Extension Architecture.

CLIENT: **Vik Barodia**

PROJECT: **1 Lambourne Drive, KT11 3LB**

TITLE: **Proposed Floor Plans**

NOTES

VERSION	DESCRIPTION	DATE


SCALE

DATE: **12.04.2024**

DRAWN: **AY**

VERSION

SHEET REF. NO: **1 LD -PL -BR 08**

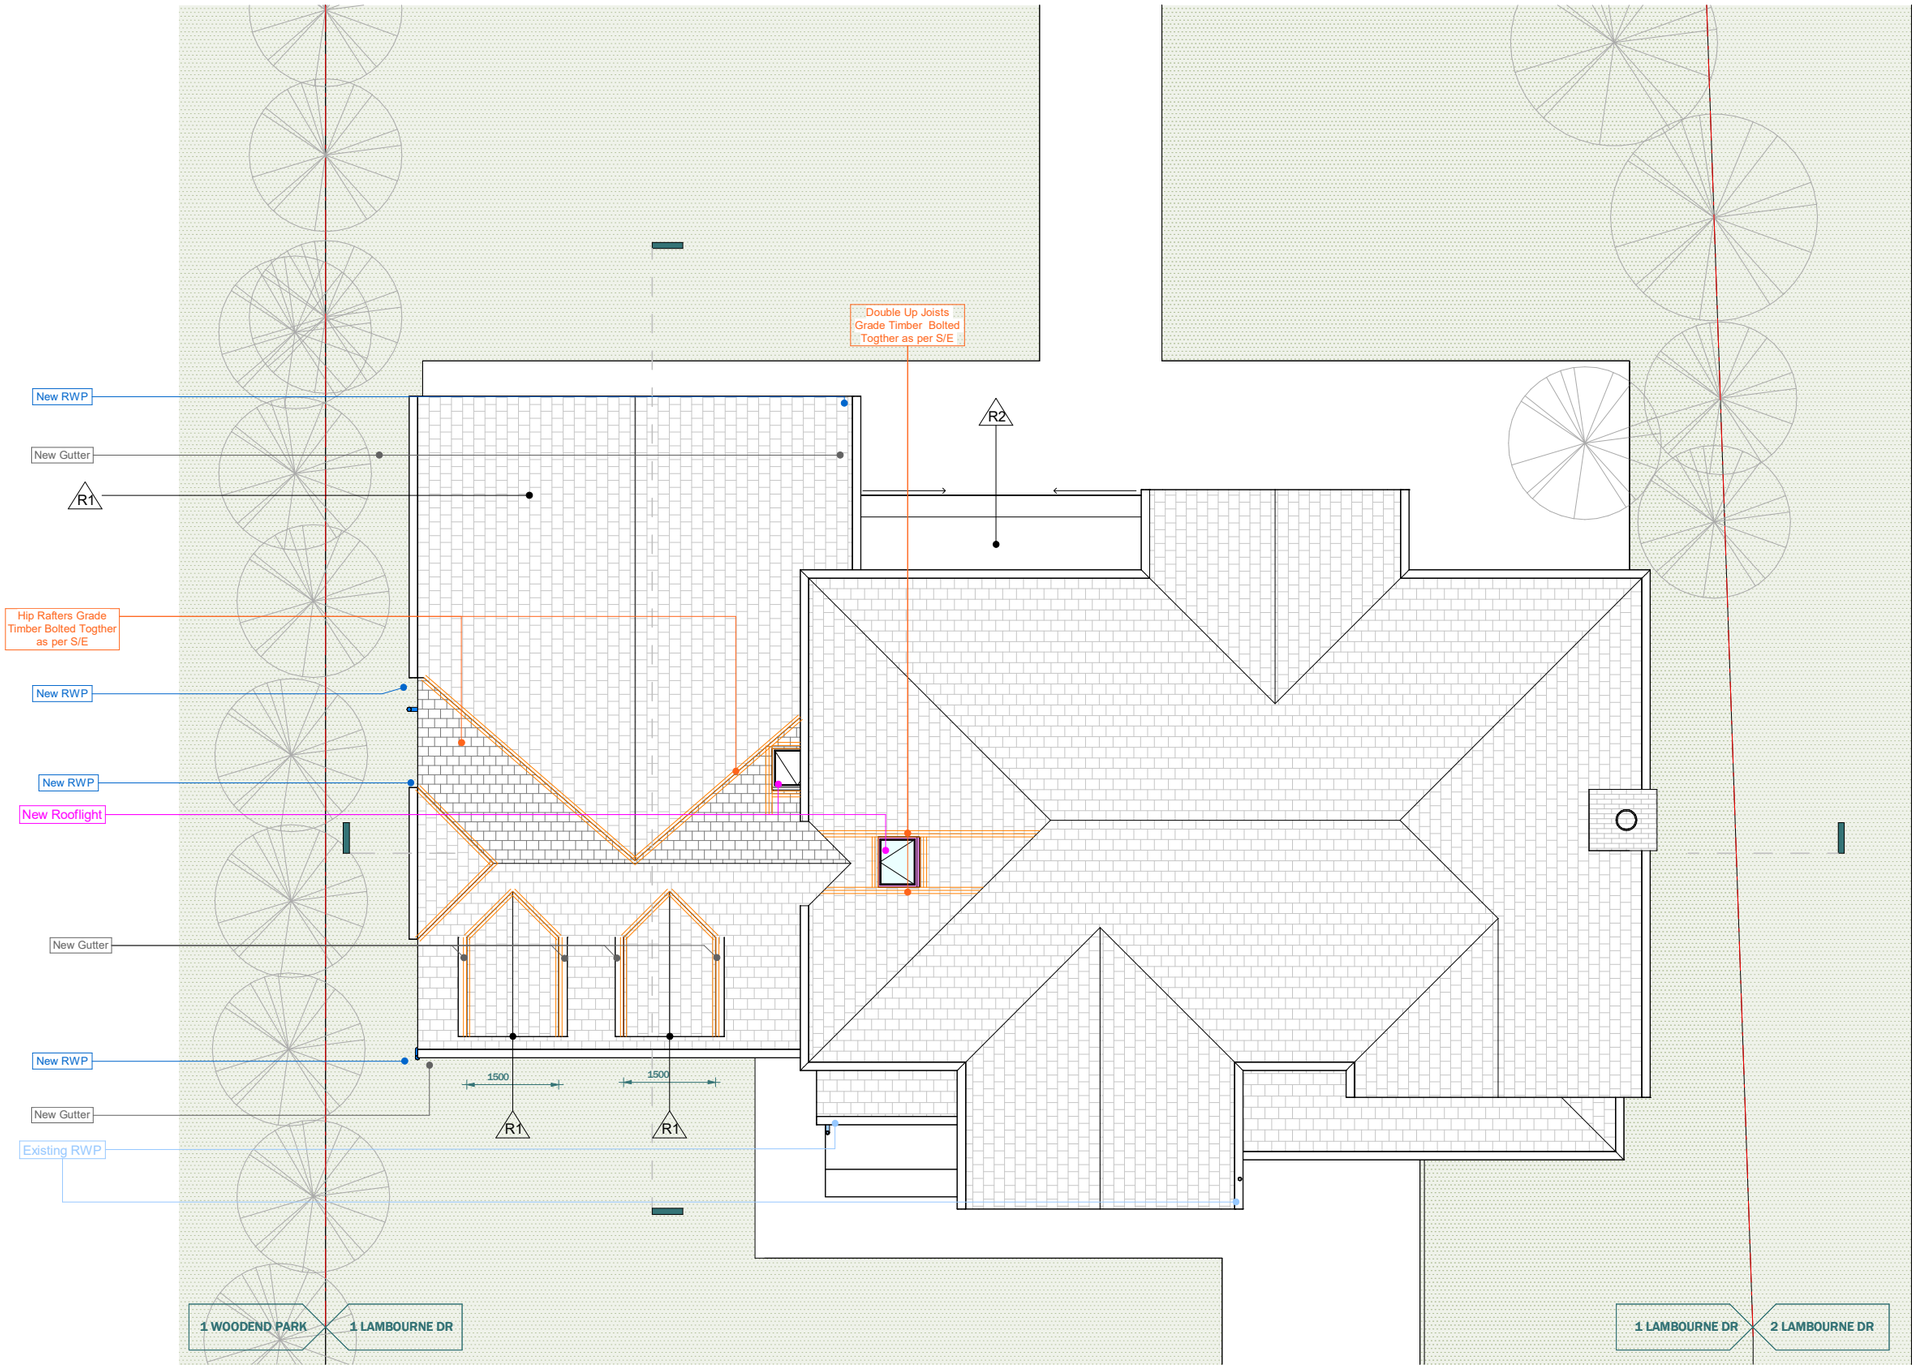

Proposed Roof Plan

1 : 100

Scale 1:100 @A3

1m 10m

DRAWINGS KEYS

- New Slab Ground Floor
- New Intermediate Timber Floor
- Upgrated Intermediate Floor
- Roof Terrace
- Upgraded Garage Floor
- Upgraded Garage Floor
- Proposed -EXT- Construction Elements
- Proposed -INT- Construction Elements
- Existing Construction Elements
- Fire Rated Elements
- Structural Steel Beams
- Padstone
- Timber Beams
- Fire Route
- Existing Demolished
- Proposed Fondations
- Assumed Existing Sewer
- Proposed Sewer
- Existing Sewer
- Rain Water Drainage Direction
- Air Extraction Route
- Proposed Joists/Rafters Direction
- Existing Joists/Rafters Direction
- Lintels
- Slope Direction
- Concrete Slab Floor
- Fire Door
- Areas under party wall matters
- SD SMOKE DETECTION & ALARM SYSTEM
- HD HEAT DETECTION & ALARM SYSTEM
- FB FIRE BLANKET
- EXTRACTOR FAN
- HOB GAS/INDUCTION HOB
- HOOD ELECTRIC HOOD
- FIRE EXTINGUISHER
- Extractor Over HOB 30l/s
- Extractor through Wall / Window 30l / S for Kitchen Hob and 60l/S Elsewhere
- Vent Vertical Flue Vent - Through The Roof
- SS (Soil Stack)

extension architecture
3 River Reach, Gartons Way, Battersea
London SW11 3SX
Tel (0208) 288 8950 Fax (0871) 918 2798
www.extensionarchitecture.co.uk

These architectural drawings are prepared by Extension Architecture and are intended for Building Regulation purposes. For any questions regarding regulatory compliance or specific Building Control requirements, please consult your local Building Control Authority. It is highly advisable to liaise with your local Building Control Authority to discuss the specific requirements and to ensure that these drawings align with the local regulations. The builder or contractor should coordinate with Building Control for any necessary site inspections and approvals. While these drawings have been created with utmost care, all measurements and specifications should be validated on-site by the builder or contractor prior to construction. These drawings will serve as a foundation for your discussions with the Building Control Authority. Any modifications or additional documents required for their approval should be addressed in collaboration with the local authority. As part of the construction process, the builder or contractor should maintain comprehensive records of compliance with the Building Regulations, including any changes or variations made during construction. In the event of on-site changes, queries, or discrepancies, and you wish for Extension Architecture to oversee the construction process, please be aware that this service is chargeable. In the event of any builder errors or issues that necessitate our intervention, a fee would be applicable for Extension Architecture's Project Manager services. All drawings should be read in conjunction with the Structural Engineers drawings. The copyright of the drawing and designs remains with Extension Architecture. All copies are only for information about the application, they may not be used for any other purpose without the express written permission of Extension Architecture.

CLIENT: **Vik Barodia**

PROJECT: **1 Lambourne Drive, KT11 3LB**

TITLE: **Proposed Floor Plans**

NOTES

VERSION	DESCRIPTION	DATE

SCALE

DATE: **12.04.2024**

DRAWN: **AY**


VERSION

SHEET REF. NO: **1 LD -PL -BR 09**



Proposed Front Elevation

1 : 100

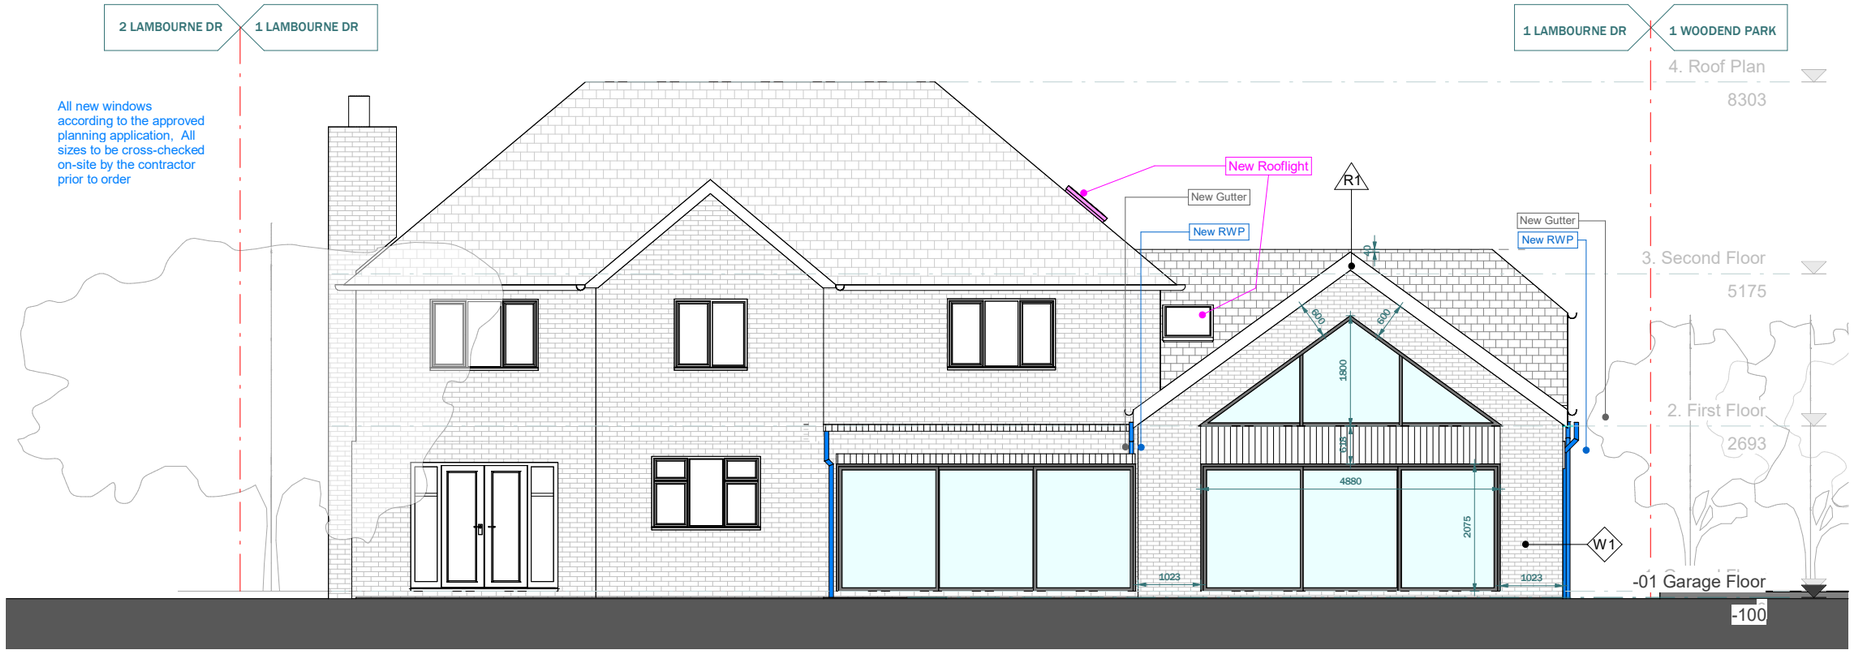

Proposed Rear Elevation

1 : 100

Scale 1:100 @A3

1m 10m

DRAWINGS KEYS

- New Slab Ground Floor
- New Intermediate Timber Floor
- Upgrated Intermediate Floor
- Roof Terrace
- Upgraded Garage Floor
- Upgraded Garage Floor
- Proposed -EXT- Construction Elements
- Proposed -INT- Construction Elements
- Existing Construction Elements
- Fire Rated Elements
- Structural Steel Beams
- Padstone
- Timber Beams
- Fire Route
- Existing Demolished
- Proposed Fondations
- Assumed Existing Sewer
- Proposed Sewer
- Existing Sewer
- Rain Water Drainage Direction
- Air Extraction Route
- Proposed Joists/Rafters Direction
- Existing Joists/Rafters Direction
- Lintels
- Slope Direction
- Concrete Slab Floor
- Fire Door
- Areas under party wall matters

- SD SMOKE DETECTION & ALARM SYSTEM
- HD HEAT DETECTION & ALARM SYSTEM
- FB FIRE BLANKET
- EXTRACTOR FAN
- HOB GAS/INDUCTION HOB
- HOOD ELECTRIC HOOD
- FIRE EXTINGUISHER
- Extractor Over HOB 30l/s
- Extractor through Wall / Window 30l / S for Kitchen Hob and 60l/S Elsewhere
- Vent Vertical Flue Vent - Through The Roof
- SS (Soil Stack)

extension architecture
3 River Reach, Gartons Way, Battersea
London SW11 3SX
Tel (0208) 288 8950 Fax (0871) 918 2798
www.extensionarchitecture.co.uk

These architectural drawings are prepared by Extension Architecture and are intended for Building Regulation purposes. For any questions regarding regulatory compliance or specific Building Control requirements, please consult your local Building Control Authority. It is highly advisable to liaise with your local Building Control Authority to discuss the specific requirements and to ensure that these drawings align with the local regulations. The builder or contractor should coordinate with Building Control for any necessary site inspections and approvals. While these drawings have been created with utmost care, all measurements and specifications should be validated on-site by the builder or contractor prior to construction. These drawings will serve as a foundation for your discussions with the Building Control Authority. Any modifications or additional documents required for their approval should be addressed in collaboration with the local authority. As part of the construction process, the builder or contractor should maintain comprehensive records of compliance with the Building Regulations, including any changes or variations made during construction. In the event of on-site changes, queries, or discrepancies, and you wish for Extension Architecture to oversee the construction process, please be aware that this service is chargeable. In the event of any builder errors or issues that necessitate our intervention, a fee would be applicable for Extension Architecture's Project Manager services. All drawings should be read in conjunction with the Structural Engineers drawings. The copyright of the drawing and designs remains with Extension Architecture. All copies are only for information about the application, they may not be used for any other purpose without the express written permission of Extension Architecture.

CLIENT: **Vik Barodia**

PROJECT: **1 Lambourne Drive, KT11 3LB**

TITLE: **Proposed Front/Rear Elevations**

NOTES

VERSION	DESCRIPTION	DATE

SCALE

DATE: **12.04.2024**

DRAWN: **AY**

VERSION

SHEET REF. NO: **1 LD -PL -BR 10**


A mains-operated hardwired and interlinked smoke detector system to be installed within each habitable space, the circulation space and a heat detector in the kitchen area. If similar systems are already installed, contractor to check suitability and conditions and confirm with BCO if remedial works or replacement are required.
All habitable rooms to have direct access to a protected escape route with the travel distance from the flat entrance door to any point in the protected escape route to be a maximum of 9m OR the travel distance from the flat entrance door to any point in any habitable room to be a maximum of 9m with cooking facilities to be remote from the main entrance door and not impeding the escape route from anywhere in the flat.
Inner rooms (allowed on storeys up to max 4.5m above GL) to have at least an escape window or door leading to an external safe space.
All elements (walls, floors, ceilings including underside of staircases, doors and any glazing) forming the protected escape route within the flat to have minimum 30 minutes fire resistance.
Existing elements enclosing the protected escape route within the flat to be checked on-site by BCO. Upgrading/replacement may be required to achieve compliance.
If existing windows are retained and have to be used as egress windows, compliance to be confirmed on-site by BCO. For information regarding egress windows refer to the specification sheet.
All elements (walls, floors, ceilings including underside of staircases, doors and any glazing) between the flat and other flats OR between the flat and common parts of the building to have minimum 60 minutes fire resistance.
Existing elements between flat and other flats OR between flat and common parts of the building to be checked on-site by BCO. Upgrading/replacement may be required to achieve compliance.
Where any work is carried out to existing elements, this should not make the fire resistance any worse and should be upgraded to minimum 60 minutes fire resistance.
Fire strategy to be approved by BCO prior to commencement of works on-site.

Gallery to comply with diagram 2.15 of AD Part B:


- Visible area to be at least 50% of the floor area in the lower room;
- Distance between the further point at gallery level and the top step of the staircase to be maximum 7.5m;
- Distance between the exit door (in the lower room) and the bottom step of the staircase to be maximum 3m;

Any cooking facilities within a room containing a gallery should comply with one of the following conditions:
- be enclosed with fire resisting construction;
- be remote from the stair to the gallery and positioned such that they do not prejudice escape from the gallery;

Diagram 2.15 of AD Part B does not apply if the gallery complies with one of the following:
- Is provided with an alternative exit;
- Is provided with an egress window, where the gallery floor is a maximum of 4.5m above ground level;

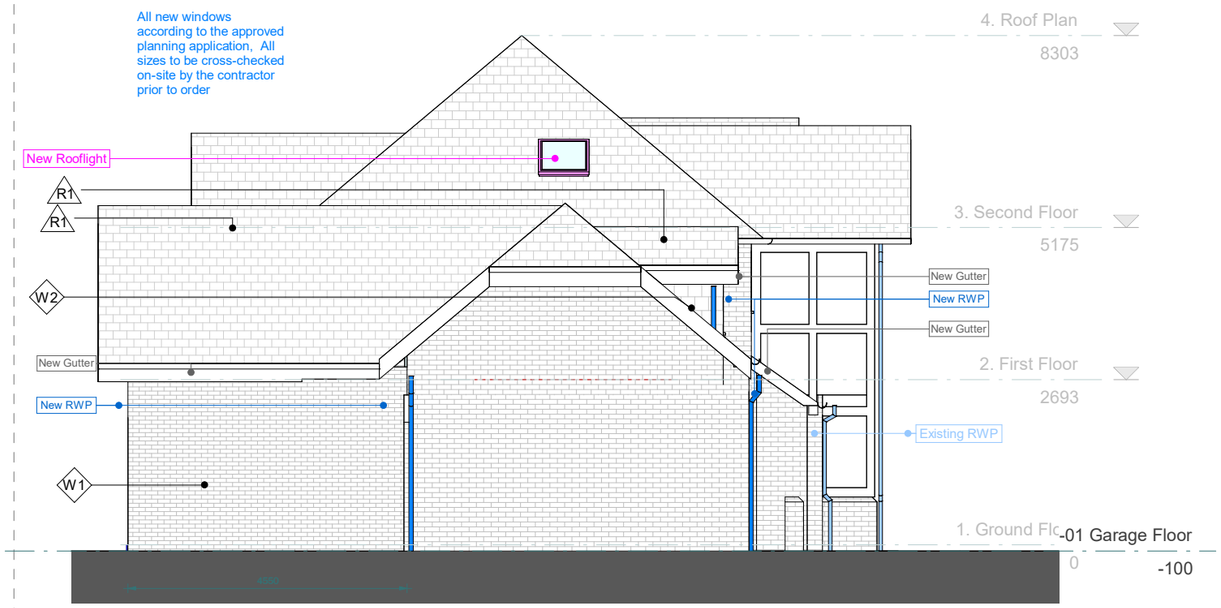

Proposed Left Elevation
1 : 100

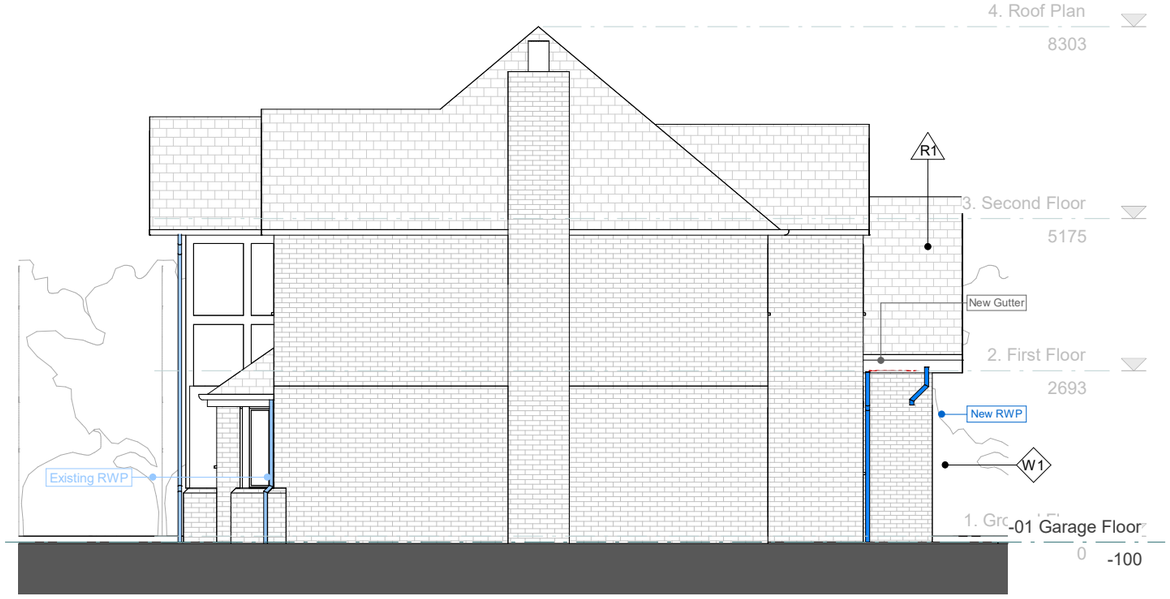

Proposed Right Elevation
1 : 100

Scale 1:100 @A3
1m
10m

DRAWINGS KEYS

- New Slab Ground Floor
- New Intermediate Timber Floor
- Upgrated Intermediate Floor
- Roof Terrace
- Upgraded Garage Floor
- Upgraded Garage Floor
- Proposed -EXT- Construction Elements
- Proposed -INT- Construction Elements
- Existing Construction Elements
- Fire Rated Elements
- Structural Steel Beams
- Padstone
- Timber Beams
- Fire Route
- Existing Demolished
- Proposed Fondations
- Assumed Existing Sewer
- Proposed Sewer
- Existing Sewer
- Rain Water Drainage Direction
- Air Extraction Route
- Proposed Joists/Rafters Direction
- Existing Joists/Rafters Direction
- Lintels
- Slope Direction
- Concrete Slab Floor
- Fire Door
- Areas under party wall matters

- SD — SMOKE DETECTION & ALARM SYSTEM
- HD — HEAT DETECTION & ALARM SYSTEM
- FB — FIRE BLANKET
- EXTRACTOR FAN
- HOB — GAS/INDUCTION HOB
- HOOD — ELECTRIC HOOD
- FIRE EXTINGUISHER
- Extractor Over HOB 30l/s
- Extractor through Wall / Window 30l / S for Kitchen Hob and 60l/S Elsewhere
- Vent — Vertical Flue Vent - Through The Roof
- SS (Soil Stack)

extension architecture
3 River Reach, Gartons Way, Battersea
London SW11 3SX
Tel (0208) 288 8950 Fax (0871) 918 2798
www.extensionarchitecture.co.uk

These architectural drawings are prepared by Extension Architecture and are intended for Building Regulation purposes. For any questions regarding regulatory compliance or specific Building Control requirements, please consult your local Building Control Authority. It is highly advisable to liaise with your local Building Control Authority to discuss the specific requirements and to ensure that these drawings align with the local regulations. The builder or contractor should coordinate with Building Control for any necessary site inspections and approvals. While these drawings have been created with utmost care, all measurements and specifications should be validated on-site by the builder or contractor prior to construction. These drawings will serve as a foundation for your discussions with the Building Control Authority. Any modifications or additional documents required for their approval should be addressed in collaboration with the local authority. As part of the construction process, the builder or contractor should maintain comprehensive records of compliance with the Building Regulations, including any changes or variations made during construction. In the event of on-site changes, queries, or discrepancies, and you wish for Extension Architecture to oversee the construction process, please be aware that this service is chargeable. In the event of any builder errors or issues that necessitate our intervention, a fee would be applicable for Extension Architecture's Project Manager services. All drawings should be read in conjunction with the Structural Engineers drawings. The copyright of the drawing and designs remains with Extension Architecture. All copies are only for information about the application, they may not be used for any other purpose without the express written permission of Extension Architecture.

CLIENT: **Vik Barodia**

PROJECT: **1 Lambourne Drive, KT11 3LB**

TITLE: **Proposed Side Elevations**

NOTES

VERSION	DESCRIPTION	DATE


SCALE

DATE: **12.04.2024**


DRAWN: **AY**

VERSION

SHEET REF. NO: **1 LD -PL -BR 11**

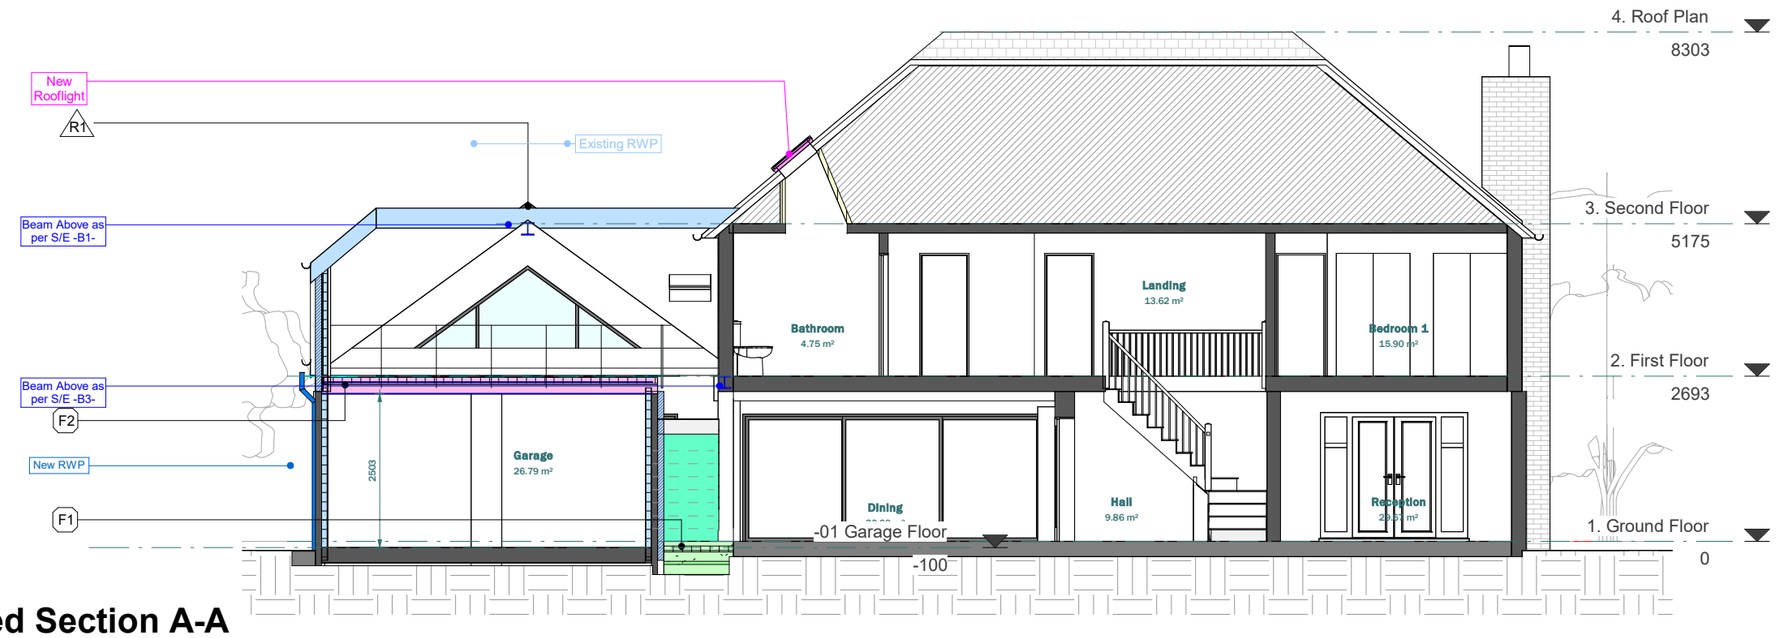

Proposed Section A-A
1 : 100

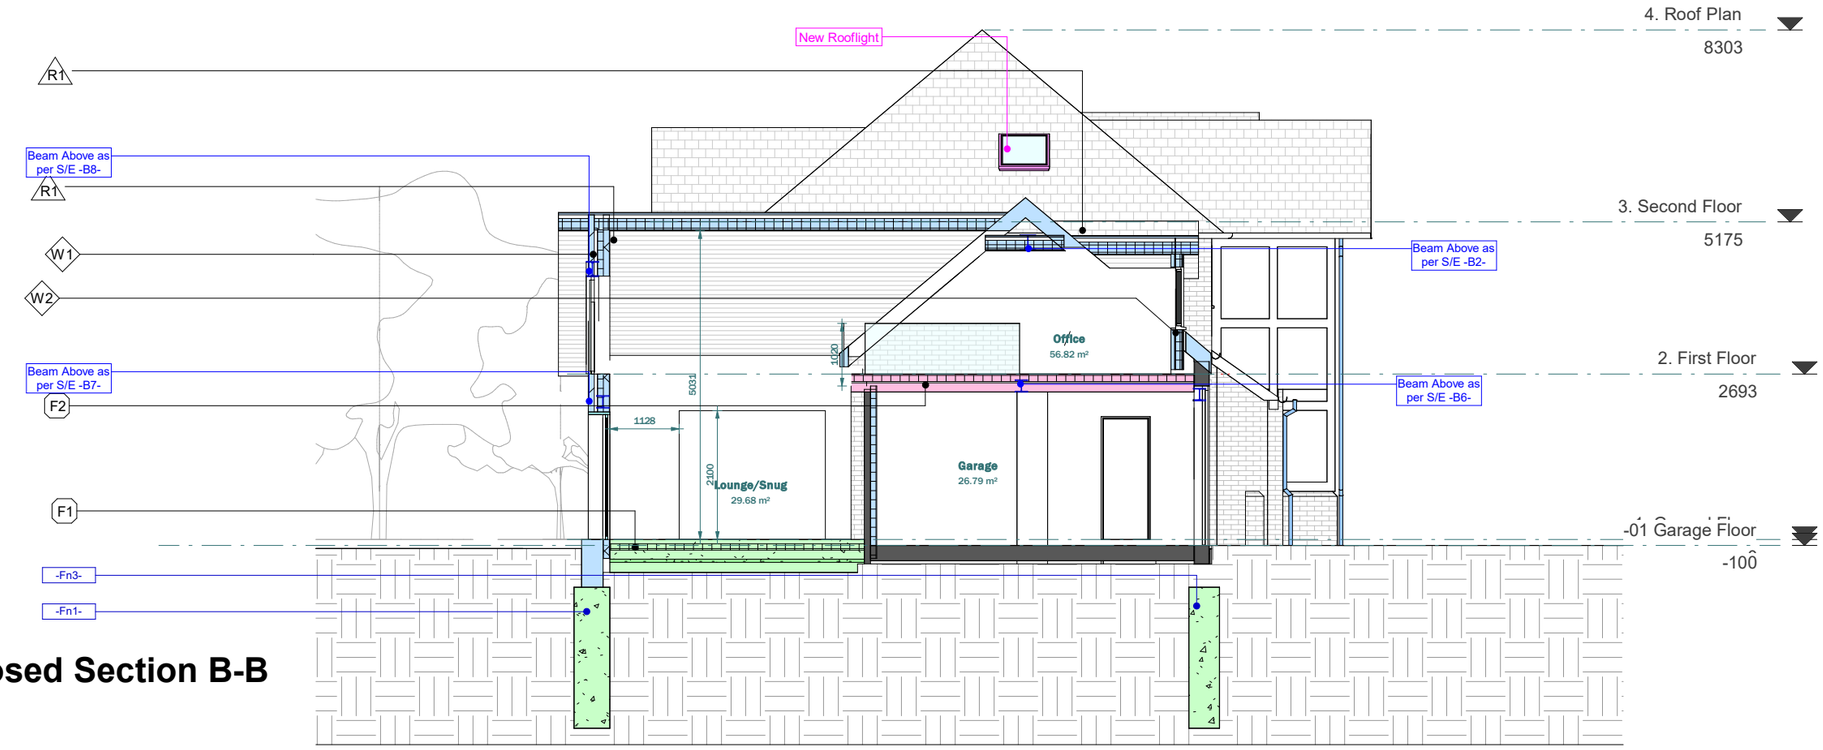

Proposed Section B-B
1 : 100

Scale 1:100 @A3

1m 10m

DRAWINGS KEYS

- New Slab Ground Floor
- New Intermediate Timber Floor
- Upgrated Intermediate Floor
- Roof Terrace
- Upgraded Garage Floor
- Upgraded Garage Floor
- Proposed -EXT- Construction Elements
- Proposed -INT- Construction Elements
- Existing Construction Elements
- Fire Rated Elements
- Structural Steel Beams
- Padstone
- Timber Beams
- Fire Route
- Existing Demolished
- Proposed Fondations
- Assumed Existing Sewer
- Proposed Sewer
- Existing Sewer
- Rain Water Drainage Direction
- Air Extraction Route
- Proposed Joists/Rafters Direction
- Existing Joists/Rafters Direction
- Lintels
- Slope Direction
- Concrete Slab Floor
- Fire Door
- Areas under party wall matters

- SD SMOKE DETECTION & ALARM SYSTEM
- HD HEAT DETECTION & ALARM SYSTEM
- FB FIRE BLANKET
- EXTRACTOR FAN
- HOB GAS/INDUCTION HOB
- HOOD ELECTRIC HOOD
- FIRE EXTINGUISHER
- Extractor Over HOB 30l/s
- Extractor through Wall / Window 30l / S for Kitchen Hob and 60l/S Elsewhere
- Vent Vertical Flue Vent - Through The Roof
- SS (Soil Stack)

extension architecture
3 River Reach, Gartons Way, Battersea
London SW11 3SX
Tel (0208) 288 8950 Fax (0871) 918 2798
www.extensionarchitecture.co.uk

These architectural drawings are prepared by Extension Architecture and are intended for Building Regulation purposes. For any questions regarding regulatory compliance or specific Building Control requirements, please consult your local Building Control Authority. It is highly advisable to liaise with your local Building Control Authority to discuss the specific requirements and to ensure that these drawings align with the local regulations. The builder or contractor should coordinate with Building Control for any necessary site inspections and approvals. While these drawings have been created with utmost care, all measurements and specifications should be validated on-site by the builder or contractor prior to construction. These drawings will serve as a foundation for your discussions with the Building Control Authority. Any modifications or additional documents required for their approval should be addressed in collaboration with the local authority. As part of the construction process, the builder or contractor should maintain comprehensive records of compliance with the Building Regulations, including any changes or variations made during construction. In the event of on-site changes, queries, or discrepancies, and you wish for Extension Architecture to oversee the construction process, please be aware that this service is chargeable. In the event of any builder errors or issues that necessitate our intervention, a fee would be applicable for Extension Architecture's Project Manager services. All drawings should be read in conjunction with the Structural Engineers drawings. The copyright of the drawing and designs remains with Extension Architecture. All copies are only for information about the application, they may not be used for any other purpose without the express written permission of Extension Architecture.

CLIENT: **Vik Barodia**

PROJECT: **1 Lambourne Drive, KT11 3LB**

TITLE: **Proposed Sections**

NOTES

VERSION	DESCRIPTION	DATE


SCALE

DATE: **12.04.2024**

DRAWN: **AY**

VERSION

SHEET REF. NO: **1 LD -PL -BR 12**

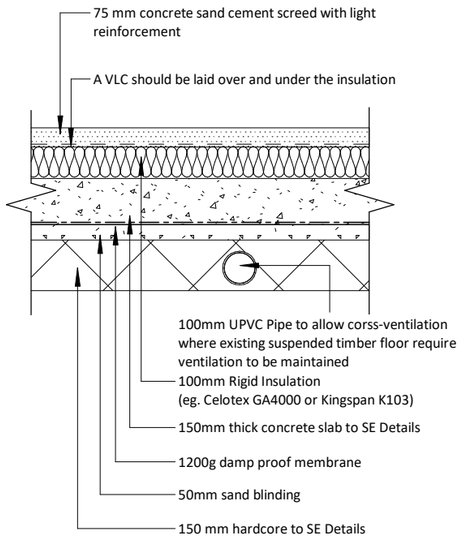

SOLID GROUND FLOOR DETAIL

U Value of 0.15 W/m²K


To meet min U value required of 0.15 W/m²K

Solid ground floor to consist of consolidated well-rammed hardcore to SE specification. Blinded with 50mm sand blinding. Provide 100mm ST2 or Gen2 ground bearing slab concrete mix to conform to BS 8500-2 over a 1200 gauge polythene DPM. DPM to be lapped in with DPC in walls. Floor to be insulated over slab and DPM with Rigid Insulation. 25mm insulation to continue around floor perimeters to avoid thermal bridging. A VCL should be laid over the insulation boards and turned up 100mm at room perimeters behind the skirting, all joints to be lapped 150mm and sealed. Finish with 65mm sand/cement finishing screed with light mesh reinforcement.
Where drain runs pass under new floor, provide A142 mesh 1.0m wide and min 50mm concrete cover over length of drain.
Where existing suspended timber floor air bricks are covered by new extension, ensure cross-ventilation is maintained by connecting to 100mm dia UPVC pipes with 100mm concrete cover laid under the extension. Pipes to terminate at new 65mm x 215mm air bricks with cavity tray over.

DETAIL -F1-
1 : 20

WARM FLAT ROOF

U Value of 0.15 W/m²K

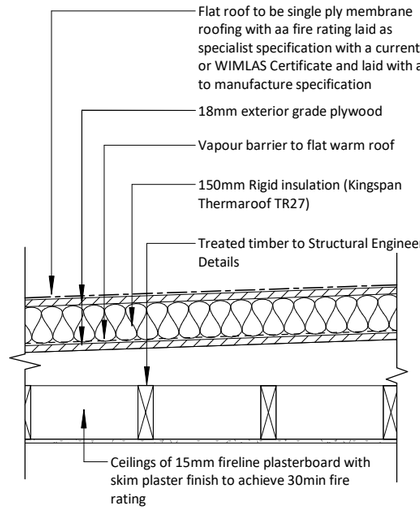


To achieve U value 0.15 W/m²K

Flat roof to be single ply membrane roofing providing aa fire rating for surface spread of flame with a current BBA or WIMLAS Certificate and laid to specialist specification. Single ply membrane to be fixed to 18mm exterior quality plywood over insulation above joist. 18mm external quality plywood decking or similar approved on sw firings to minimum 1 in 80 fall. Joist at ctrs as Structural Engineer's details and calculations. Underside of joists to have 12.5mm foil backed plasterboard and skim. Provide cavity tray to existing house where new roof abuts existing house.
Provide restraint to flat roof by fixing of 30 x 5 x 1000mm ms galvanised lateral restraint straps at maximum 2000mm centres fixed to 100 x 50mm wall plates and anchored to wall.

DETAIL -R2-
1 : 20


UPGRADING FLOOR OVER A COLD SPACE

U-value 0.18 W/m²K

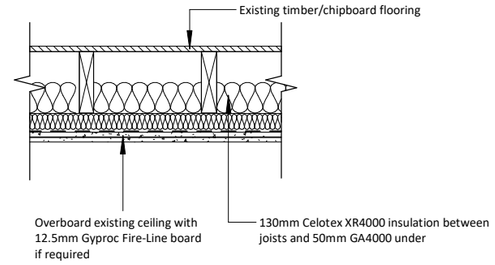


DETAIL -F2-
1 : 20

SOUND INSULATION OF INTERNAL SOIL STACK

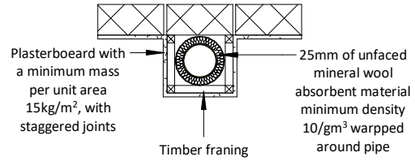


DETAIL -Si-
1 : 20

ABOVE GROUD DRAINAGE

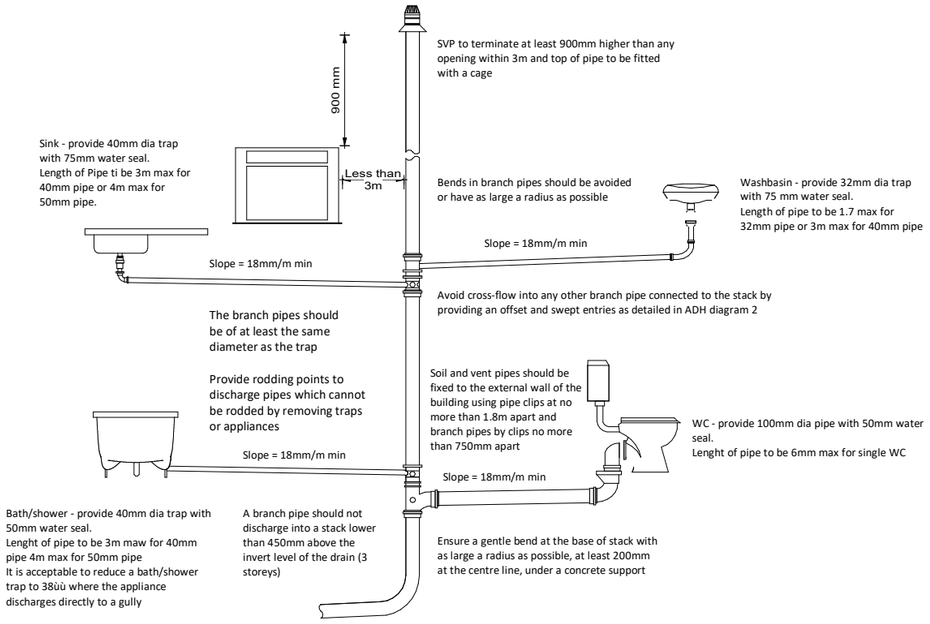

SANITARY-PIPEWORK DETAILS
1 : 50

VENTED PITCHED ROOF

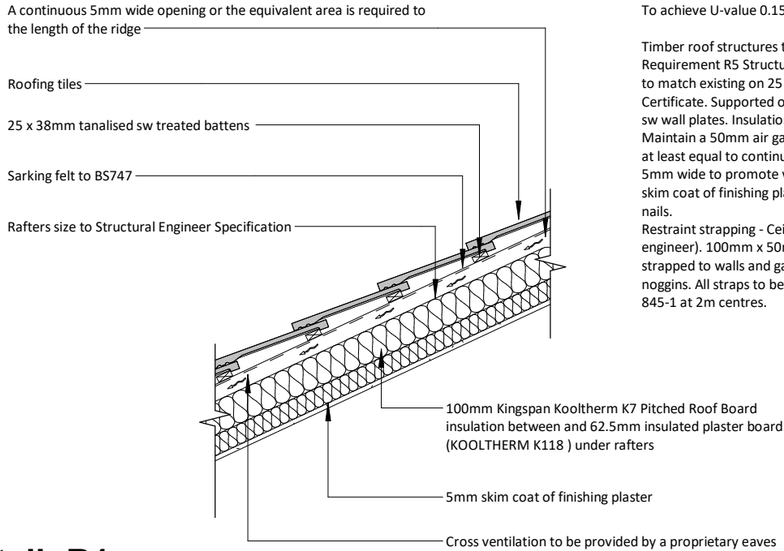

To achieve U-value 0.15 W/m²K

Timber roof structures to be designed by an Engineer in accordance with NHBC Technical Requirement R5 Structural Design. Calculations to be based on BS EN 1995-1-1. Roofing tiles to match existing on 25 x 38mm tanalised sw treated battens on sarking felt to relevant BBA Certificate. Supported on Rafters to engineer's details and calculations. Rafters supported on sw wall plates. Insulation between rafters between and under rafters.
Maintain a 50mm air gap above insulation to ventilate roof. Provide opening at eaves level at least equal to continuous strip 25mm wide and opening at ridge equal to continuous strip 5mm wide to promote ventilation. Fix insulated plasterboard (joints staggered) and 5mm skim coat of finishing plaster to the underside of all ceilings using galvanized plasterboard nails.
Restraint strapping - Ceiling joists tied to rafters (if raised collar roof consult structural engineer). 100mm x 50mm wall plate strapped down to walls. Ceiling joists and rafters to be strapped to walls and gable walls, straps built into cavity, across at least 3 timbers with noggins. All straps to be 1000 x 30 x 5mm galvanized straps or other approved to BSEN 845-1 at 2m centres.

Detail -R1-
1 : 20

Scale 1:100 @A3 0 1 2 3 4 5m
Scale 1:50 @A3 0 0.5 1 1.5 2 2.5m
Scale 1:20 @A3 0 20 40 60 80 100m

extension architecture
3 River Reach, Gartons Way,
Battersea
London SW11 3SX
Tel (0208) 288 8950 Fax (0871) 918 2798
www.extensionarchitecture.co.uk

This drawing is prepared solely for design and planning submission purposes. It is not intended or suitable for either building regulations or construction purposes and should not be used for such. All dimension shall be check and confirmed with site rep. and any discrepancies between the drawings and site shall be reported to PM. This drawing to be read in conjunction with engineers specification and details. For construction information please refer to all drawings and specification of works.

For any structural steelworks details please refer to structural engineer's drawings & calculations.


The copyright of the drawing and designs remains with Extension Architecture. All copies are only for information about the application, they may not be used for any other purpose without the express written permission of Extension Architecture.

CLIENT: Vik Barodia
PROJECT: 1 Lambourne Drive, KT11 3LB
TITLE: Proposed Typical Build-up Details
NOTES
VERSION | DESCRIPTION | DATE
SCALE: As indicated
DRAWN: AY
DATE: 12.04.2024
VERSION
SHEET REF. NO: 1 LD -PL -BR 13

PITCHED ROOF ABUTMENT WITH CAVITY WALL

A stepped cavity tray linked to a stepped flashing should be used. Stepped flashings should be cut from a strip at least 150mm wide. Soakers or a secret gutter should be installed at abutments where slates, flat interlocking tiles plain tiles are used.

Weepholes to be provided min 1 per tray

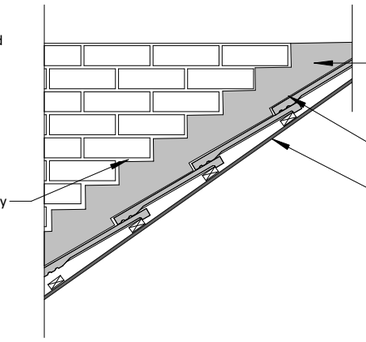

Non-ferrous lead flashing at least Code 4 to be tucked into a mortar joint or chase 25mm deep and at 75mm above the tiling level with a 100mm overlap

Flashing to extend min 150mm over roof tiles

Sarking felt to BS747 turned up at abutment

PITCHED ROOF ABUTMENT WITH CAVITY WALL
1 : 20


LINTEL WITH SLOPE WITHIN THE CAVITY

Additional cavity tray not be required check manufacturers detail

Weep holes (min 2 per lintel at 450mm cntrs

Joint filled with polyethylene foam ans sealant pointing

Ensure masonry overhang does not exceed 25mm

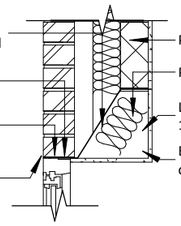

Partial fill cavity wall. Refer to Deatil -W1-

Polyurethane Foam insulation

Lintel to have a nominal 150mm bearing at each end

Ensure lintel is fully bedded on blocklaying motar

Lintel drip to project forward of thr frame

DETAIL -L-
1 : 20

DORMER WALL DETAIL


Roof tile to dormer cheek on 25 x 38mm tanalised sw treated cross battens

External weather board overlaid with a breather membraine.

100mm Celotex GA4000 Insulation in between studs with 62.5mm Celotex PL4050 Insulated Plasterboard finish

Treated timber frame constructed using head & sole plates and vertical studs to Structural Speci

(*Required on dormer cheek walls)15mm thick (or 2 x 9mm) SUPALUX board, or an alternaltive system to provide 60 minutes fire protection, with vapour bareer. Boards fixed to timber studs head nails at nominal 150mm centre.

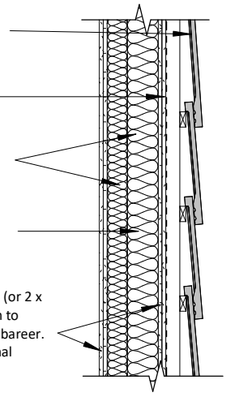


To achieve minimum U Value of 0.18W/m²K

Tiled on treated timber battens with intergrated breathable membrane on a wheater treat external board with intergular fire rating. Wheather board fixed to treated timber frame studs constructed using: 100mm x 50mm head & sole plates and vertical studs (with noggins) at 400mm ctrs or to s/engineer's details & calculations. Insulation between and over studs. Finish with 3mm skim coat of finishing plaster . All junctions to have water tight construction, seal all perimeter joints with tape internally and with silicon sealant externally.

Detail -W2-
1 : 20

HEADROOM FOR NEW STAIRS

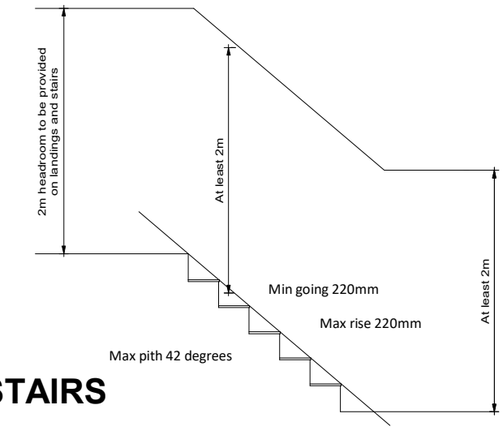

Dimensions to be checked and measured on site prior to fabrication of stairs. Timber stairs to comply with BS585 and with Part K of the Building Regulations. Max rise 220mm, min going 220mm. Two risers plus one going should be between 550 and 700mm. Tapered treads to have going in centre of tread at least the same as the going on the straight. Min 50mm going of tapered treads measured at narrow end. Pitch not to exceed 42 degrees. The width and length of every landing should be at least as great as the smallest width of the flight. Doors which swing across a landing at the bottom of a flight should leave a clear space of at least 400mm across the full width of the flight. Cupboard doors may open across the top landing where the swing is a minimum of 400mm from the tread. Min 2.0m headroom measured vertically above pitch line of stairs and landings. Handrail on staircase to be 900mm above the pitchline, handrail to be at least one side if stairs are less than 1m wide and on both sides if they are wider. Ensure a clear width between handrails of minimum 600mm. Balustrading designed to be unclimbable and should contain no space through which a 100mm sphere could pass. Allow for all structure as designed by a Structural Engineer.

NEW STAIRS
1 : 50


EXTERNAL BRICK WALL DETAIL

U Value of 0.17 W/m²K

102.5 mm Brickwork to Architectural design

Stainless steel retaining wall ties built in at 750 mm ctrs horizontally, 450 mm vertically and 225 mm ctrs at reveals and corners in staggered rows or to SE specification

Walls to be built with 1:1:6 cement mortar or to SE specification

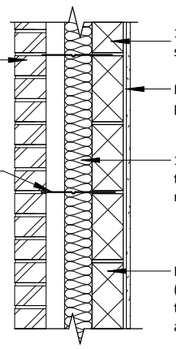

100 mm blockwork to SE specification

Internal finish to be 12.5 mm plasterboard on dabs

100mm Celotex CW4000 fixed to innerleaf w/ 50mm clear residual cavity

Horizontal strip polymer (hyload) damp proof course to both leafs min. 150 mm above external ground level

To achieve minimum U Value of 0.17W/m²K

102.5mm brickwork as architectural design, on blockwork to Structural engineer specification. Ensure a clear residual cavity with Rigid Insulation fixed to inner leaf constructed using 100mm blockwork to Structural engineer specification. Internal finish to be 12.5mm plasterboard on dabs.

Detail -W1-
1 : 20

ROOFLIGHT (STRUCTURE)

Rooflight installed in accordance with manufactures details

Structural head trimmers

90 degree framing angles

Structural cill trimmers

Provide double trimmers where necessary

NOTE : All roof designs must be checked and calculated by a structural engineer

ROOFLIGHT STRUCTURE
1 : 20

Scale 1:100 @A3 0 1 2 3 4 5m

Scale 1:50 @A3 0 0.5 1 1.5 2 2.5m

Scale 1:20 @A3 0 20 40 60 80 100m


extension architecture
3 River Reach, Gartons Way,
Battersea
London SW11 3SX
Tel (0208) 288 8950 Fax (0871) 918 2798
www.extensionarchitecture.co.uk

This drawing is prepared solely for design and planning submission purposes. It is not intended or suitable for either building regulations or construction purposes and should not be used for such. All dimension shall be check and confirmed with site rep. and any discrepancies between the drawings and site shall be reported to PM. This drawing to be read in conjunction with engineers specification and details. For construction information please refer to all drawings and specification of works.

For any structural steelworks details please refer to structural engineer's drawings & calculations.

The copyright of the drawing and designs remains with Extension Architecture. All copies are only for information about the application, they may not be used for any other purpose without the express written permission of Extension Architecture.

CLIENT: Vik Barodia	NOTES			SCALE: As indicated	DATE: 12.04.2024
PROJECT: 1 Lambourne Drive, KT11 3LB	VERSION	DESCRIPTION	DATE	DRAWN: AY	VERSION
TITLE: Proposed Typical Build-up Details				SHEET REF. NO: 1 LD -PL -BR 14	

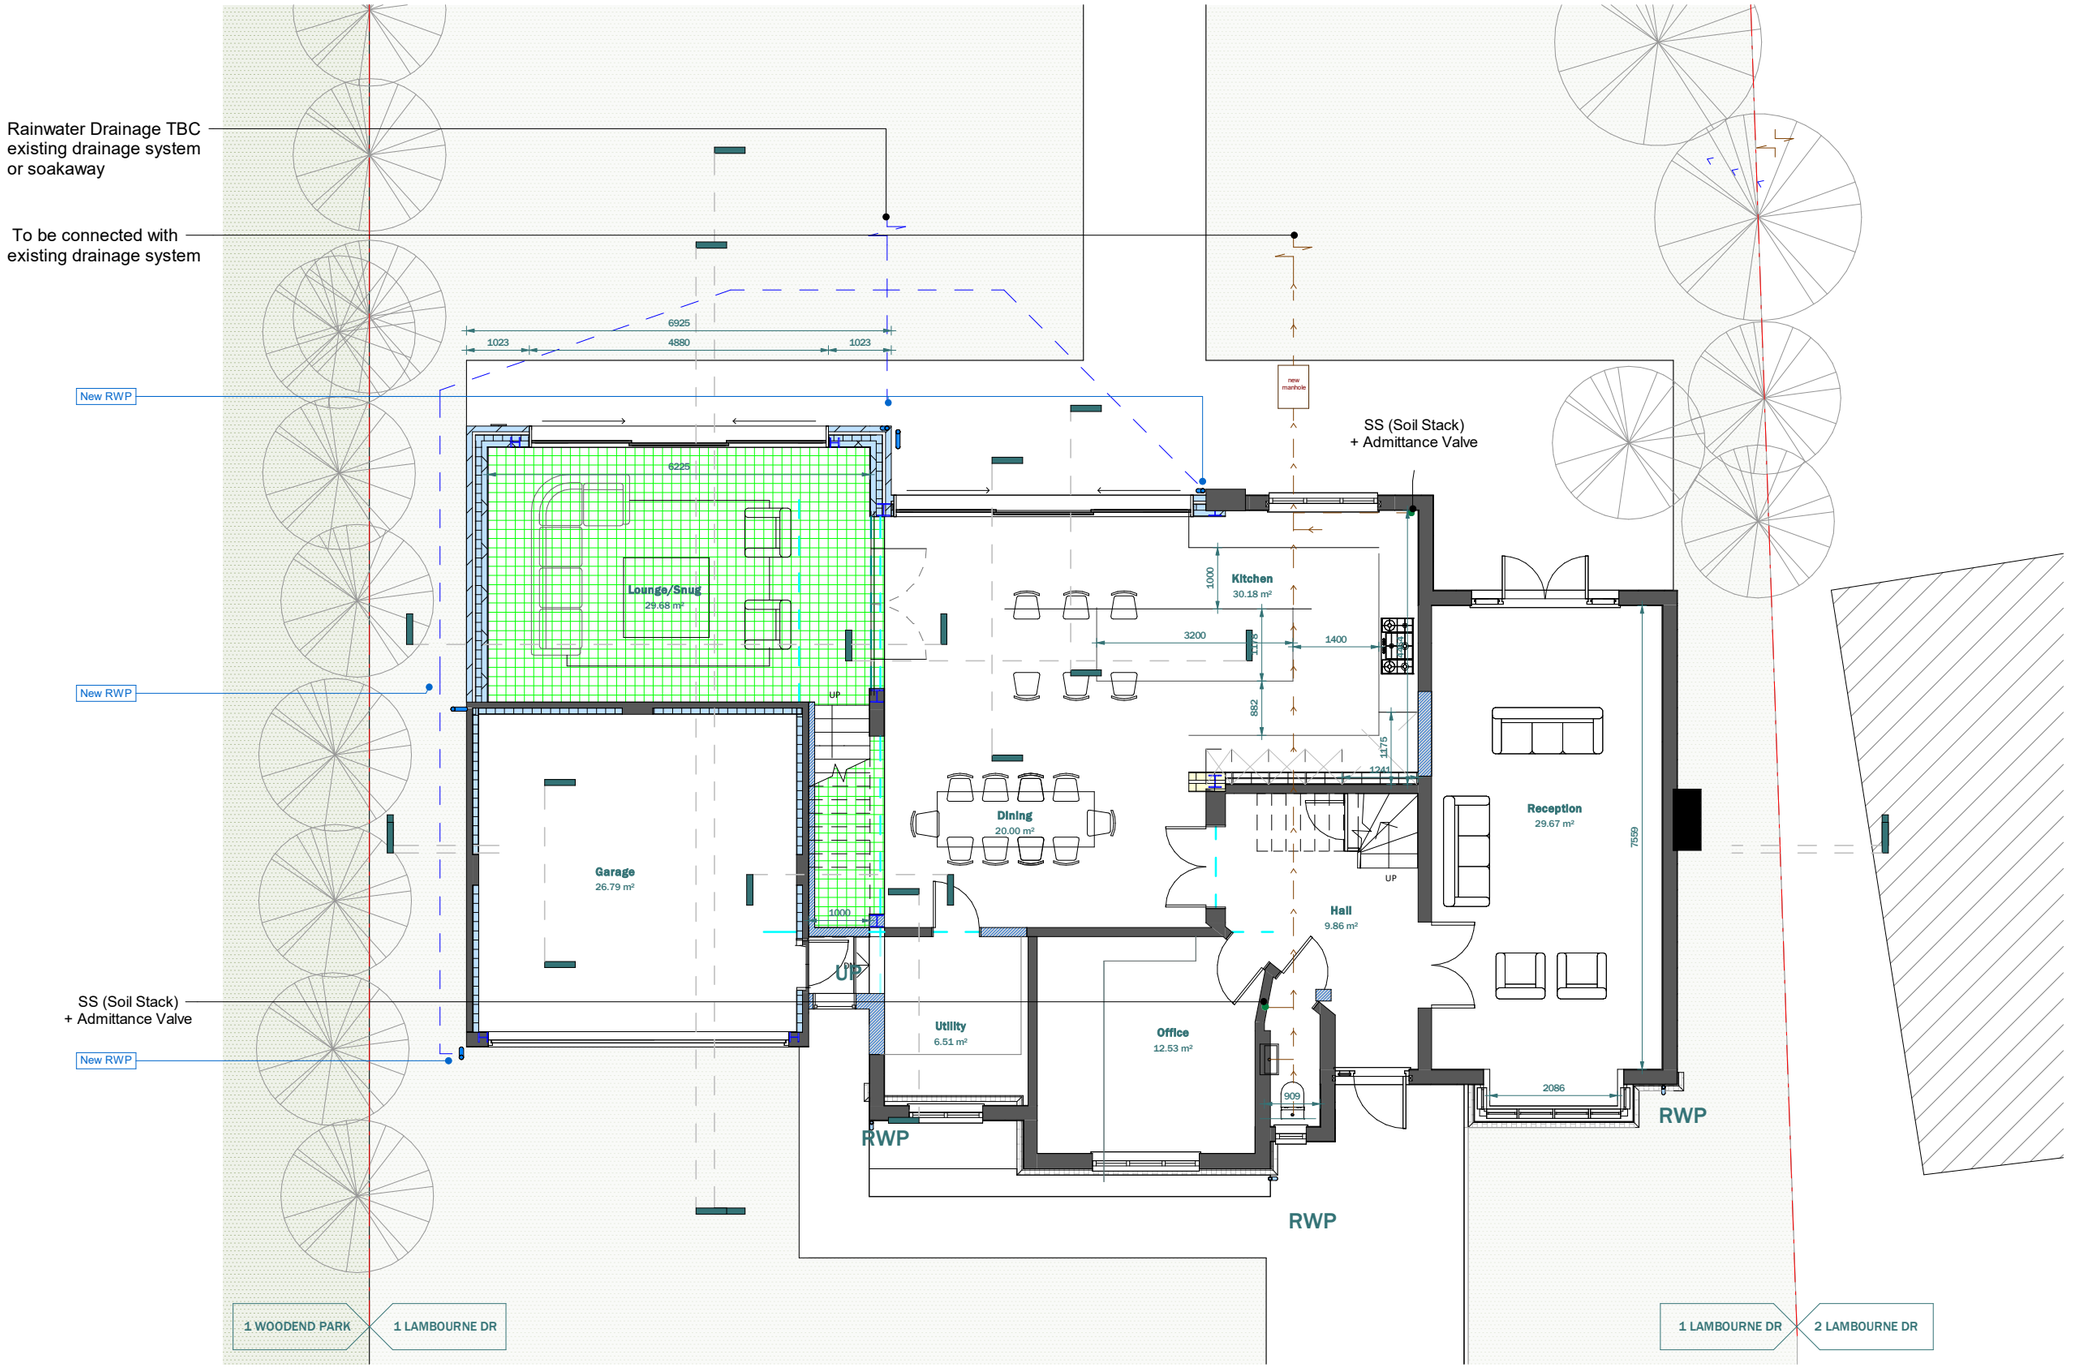

1-Proposed Drainage Plan -Ground Floor-

1 : 100

Scale 1:100 @A3

1m 10m

DRAWINGS KEYS

- New Slab Ground Floor
- New Intermediate Timber Floor
- Upgrated Intermediate Floor
- Roof Terrace
- Upgraded Garage Floor
- Upgraded Garage Floor
- Proposed -EXT- Construction Elements
- Proposed -INT- Construction Elements
- Existing Construction Elements
- Fire Rated Elements
- Structural Steel Beams
- Padstone
- Timber Beams
- Fire Route
- Existing Demolished
- Proposed Fondations
- Assumed Existing Sewer
- Proposed Sewer
- Existing Sewer
- Rain Water Drainage Direction
- Air Extraction Route
- Proposed Joists/Rafters Direction
- Existing Joists/Rafters Direction
- Lintels
- Slope Direction
- Concrete Slab Floor
- Fire Door
- Areas under party wall matters

- SD SMOKE DETECTION & ALARM SYSTEM
- HD HEAT DETECTION & ALARM SYSTEM
- FB FIRE BLANKET
- EXTRACTOR FAN
- HOB GAS/INDUCTION HOB
- HOOD ELECTRIC HOOD
- FIRE EXTINGUISHER
- Extractor Over HOB 30l/s
- Extractor through Wall / Window 30l / S for Kitchen Hob and 60l/S Elsewhere
- Vent Vertical Flue Vent - Through The Roof
- SS (Soil Stack)

extension architecture
3 River Reach, Gartons Way, Battersea
London SW11 3SX
Tel (0208) 288 8950 Fax (0871) 918 2798
www.extensionarchitecture.co.uk

These architectural drawings are prepared by Extension Architecture and are intended for Building Regulation purposes. For any questions regarding regulatory compliance or specific Building Control requirements, please consult your local Building Control Authority. It is highly advisable to liaise with your local Building Control Authority to discuss the specific requirements and to ensure that these drawings align with the local regulations. The builder or contractor should coordinate with Building Control for any necessary site inspections and approvals. While these drawings have been created with utmost care, all measurements and specifications should be validated on-site by the builder or contractor prior to construction. These drawings will serve as a foundation for your discussions with the Building Control Authority. Any modifications or additional documents required for their approval should be addressed in collaboration with the local authority. As part of the construction process, the builder or contractor should maintain comprehensive records of compliance with the Building Regulations, including any changes or variations made during construction. In the event of on-site changes, queries, or discrepancies, and you wish for Extension Architecture to oversee the construction process, please be aware that this service is chargeable. In the event of any builder errors or issues that necessitate our intervention, a fee would be applicable for Extension Architecture's Project Manager services. All drawings should be read in conjunction with the Structural Engineers drawings. The copyright of the drawing and designs remains with Extension Architecture. All copies are only for information about the application, they may not be used for any other purpose without the express written permission of Extension Architecture.

CLIENT: Vik Barodia

PROJECT: 1 Lambourne Drive, KT11 3LB

TITLE: Proposed Drainage Plans

NOTES

VERSION	DESCRIPTION	DATE


SCALE

DATE: 12.04.2024

DRAWN: AY

VERSION

SHEET REF. NO: 1 LD -PL -BR 15

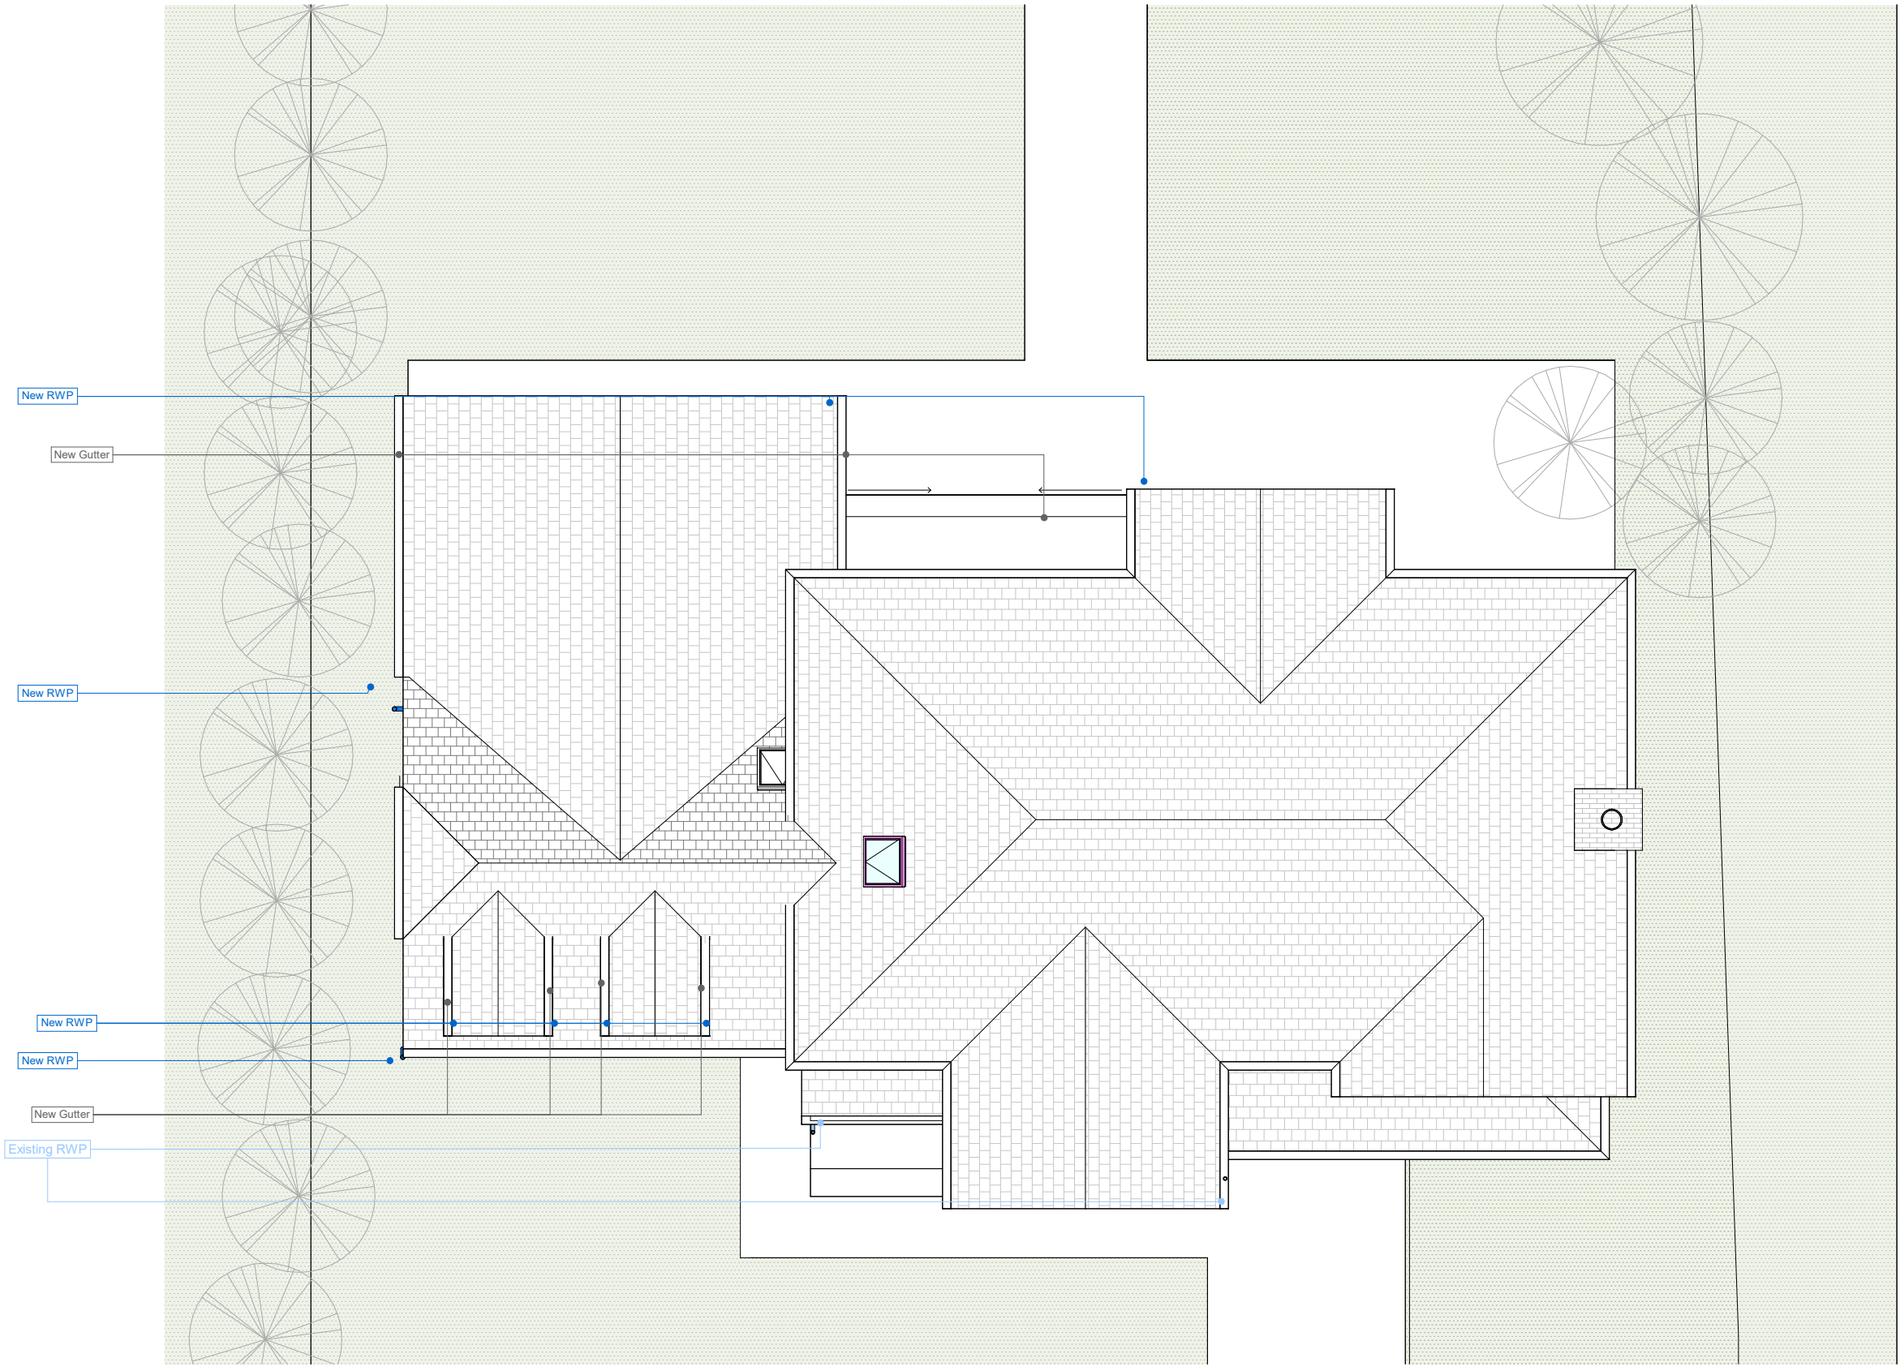

DRAWINGS KEYS

- New Slab Ground Floor
- New Intermediate Timber Floor
- Upgrated Intermediate Floor
- Roof Terrace
- Upgraded Garage Floor
- Upgraded Garage Floor
- Proposed -EXT- Construction Elements
- Proposed -INT- Construction Elements
- Existing Construction Elements
- Fire Rated Elements
- Structural Steel Beams
- Padstone
- Timber Beams
- Fire Route
- Existing Demolished
- Proposed Fondations
- Assumed Existing Sewer
- Proposed Sewer
- Existing Sewer
- Rain Water Drainage Direction
- Air Extraction Route
- Proposed Joists/Rafters Direction
- Existing Joists/Rafters Direction
- Lintels
- Slope Direction
- Concrete Slab Floor
- Fire Door
- Areas under party wall matters

- SD — SMOKE DETECTION & ALARM SYSTEM
- HD — HEAT DETECTION & ALARM SYSTEM
- FB — FIRE BLANKET
- EXTRACTOR FAN
- HOB — GAS/INDUCTION HOB
- HOOD — ELECTRIC HOOD
- FIRE EXTINGUISHER
- Extractor Over HOB 30l/s
- Extractor through Wall / Window 30l / S for Kitchen Hob and 60l/S Elsewhere
- Vent — Vertical Flue Vent - Through The Roof
- SS (Soil Stack)

Scale 1:100 @A3

1m 10m

extension architecture
3 River Reach, Gartons Way, Battersea
London SW11 3SX
Tel (0208) 288 8950 Fax (0871) 918 2798
www.extensionarchitecture.co.uk

These architectural drawings are prepared by Extension Architecture and are intended for Building Regulation purposes. For any questions regarding regulatory compliance or specific Building Control requirements, please consult your local Building Control Authority. It is highly advisable to liaise with your local Building Control Authority to discuss the specific requirements and to ensure that these drawings align with the local regulations. The builder or contractor should coordinate with Building Control for any necessary site inspections and approvals. While these drawings have been created with utmost care, all measurements and specifications should be validated on-site by the builder or contractor prior to construction. These drawings will serve as a foundation for your discussions with the Building Control Authority. Any modifications or additional documents required for their approval should be addressed in collaboration with the local authority. As part of the construction process, the builder or contractor should maintain comprehensive records of compliance with the Building Regulations, including any changes or variations made during construction.
In the event of on-site changes, queries, or discrepancies, and you wish for Extension Architecture to oversee the construction process, please be aware that this service is chargeable. In the event of any builder errors or issues that necessitate our intervention, a fee would be applicable for Extension Architecture's Project Manager services. All drawings should be read in conjunction with the Structural Engineers drawings. The copyright of the drawing and designs remains with Extension Architecture. All copies are only for information about the application, they may not be used for any other purpose without the express written permission of Extension Architecture.

CLIENT: **Vik Barodia**

PROJECT: **1 Lambourne Drive, KT11 3LB**

TITLE: **Proposed Drainage Plans**

NOTES

VERSION	DESCRIPTION	DATE

SCALE

DATE: **12.04.2024**

DRAWN: **AY**

VERSION

SHEET REF. NO: **1 LD -PL -BR 16**

EXTRACT TO WC
W/C to have mechanical ventilation ducted to external air with an extract rating of 15l/s operated via the light switch. Vent to have a 15min overrun if no window in room. Internal doors should be provided with a 10mm gap below the door to aid air circulation. Ventilation provision in accordance with the Domestic Ventilation Compliance Guide. Intermittent extract fans to BS EN 13141-4. All fixed mechanical ventilation systems, where they can be tested and adjusted, shall be commissioned and a commissioning notice given to the Building Control Body.

EXTRACT TO BATHROOM
Bathroom to have mechanical vent ducted to external air to provide min 15 litres / sec extraction. Vent to be connected to light switch and to have 15 minute over run if no window in room. Internal doors should be provided with a 10mm gap below the door to aid air circulation. Ventilation provision in accordance with the Domestic Ventilation Compliance Guide. Intermittent extract fans to BS EN 13141-4. All fixed mechanical ventilation systems, where they can be tested and adjusted, shall be commissioned and a commissioning notice given to the Building Control Body.

ABOVE GROUND DRAINAGE
All new above ground drainage and plumbing to comply with BS EN 12056-2:2000 for sanitary pipework. All drainage to be in accordance with part H of the Building Regulations. Wastes to have 75mm deep anti vac bottle traps and rodding eyes to be provided at changes of direction.
Size of wastes pipes and max length of branch connections (if max length is exceeded then anti vacuum traps to be used)
Wash basin - 1.7m for 32mm pipe 3m for 40mm pipe
Bath/shower - 3m for 40mm pipe 4m for 50mm pipe
W/c - 6m for 100mm pipe for single WC
All branch pipes to connect to 110mm soil and vent pipe terminating min 900mm above any openings within 3m. Or to 110mm upvc soil pipe with accessible internal air admittance valve complying with BS EN 12380, placed at a height so that the outlet is above the trap of the highest fitting.
Waste pipes not to connect within 200mm of the WC connection. Supply hot and cold water to all fittings as appropriate.

HEATING
Extend all heating and hot water services from existing and provide new TRVs to radiators. Heating system to be designed, installed, tested and fully certified by a GAS SAFE registered specialist. All work to be in accordance with the Local Water Authorities bye laws, the Gas Safety (Installation and Use) Regulations 1998 and IEE Regulations.
The energy performance of the new components to be assessed. The results should be recorded and given to the building owner.
All accessible pipes to be insulated to the standards in Table 4.4 Approved Document L.

LEAD WORK AND FLASHINGS
All lead flashings, any valleys or soakers to be Code 5 lead and laid according to Lead Development Association. Flashings to be provided to all jambs and below window openings with welded upstands. Joints to be lapped min 150mm and lead to be dressed 200mm under tiles, etc. All work to be undertaken in accordance with the Lead Development Association recommendations.

SAFETY GLAZING
All glazing in critical locations to be toughened or laminated safety glass to BS 6206, BS EN 14179 or BS EN ISO 12543-1 and Part K (Part N in Wales) of the current Building Regulations, i.e. within 1500mm above floor level in doors and side panels within 300mm of door opening and within 800mm above floor level in windows.

OPENINGS AND RETURNS
An opening or recess greater than 0.1m² shall be at least 550mm from the supported wall (measured internally).

ELECTRIC SPACE HEATING SYSTEMS
Each room to be provided with thermostatic room controls capable of being used to separately to adapt the heating output in each room served by the heating appliance.
Electrical heating system to be installed and commissioned by a member of one of the approved Competent Person schemes. A copy of the commissioning certificate to be given to building control and the owner on completion of the works.
Any electric storage heaters to be provided with automatic control of input charge. The rate of heat release from the appliance to be adjustable, using an adjustable damper or other thermostatically controlled method.
Any electric panel heaters to be provided with time and temperature control to allow separate control for either of the following:
Each room or
Each appliance, where this meets the guidance for thermostatic room controls in Approved Document L para 5.20
Any electric warm air system to be provided with:
A programmable room thermostat or a time switch and room thermostat and
Separately controllable heating zones that meet the guidance for thermostatic room control in Approved Document L para 5.20 to 5.22.

ELECTRICAL
All electrical work required to meet the requirements of Part P (electrical safety) must be designed, installed, inspected and tested by a competent person registered under a competent person self certification scheme such as BRE certification Ltd, BSI, NICEIC Certification Services or Zurich Ltd. An appropriate BS7671 Electrical Installation Certificate is to be issued for the work by a person competent to do so. A copy of a certificate will be given to Building Control on completion.

INTERNAL LIGHTING
Install low energy light fittings that only take lamps having a luminous efficiency better than 80 lumens per circuit watt. All fixed to have lighting capacity (lm) 185 x total floor area, to comply with Part L of the current Building Regulations and the Domestic Building Services Compliance Guide.

PURGE VENTILATION
Minimum total area of opening in accordance with Table 1.4 Approved Document F1.
Hinged or pivot windows with an opening angle of 15 to 30 degrees to have an openable area in excess 1/10 of the floor area of the room.
Sash windows, external doors or hinged pivot windows with an opening angle of equal to or greater than 30 degrees to have an openable area in excess of 1/20 of the floor area of the room.
Purge ventilation should be capable of extracting at least 4 air changes per hour per room directly to the outside.
Internal doors should be provided with a 10mm gap below the door to aid air circulation.

CAVITY BARRIERS
30 minute fire resistant cavity barriers to be provided around openings, at tops of walls, gable end walls, vertically at junctions with separating walls and horizontally at separating floors. Cavity trays to be provided over barriers where required. Trays and cavity barriers to be installed according to manufacturer's details.

MEANS OF ESCAPE - Fire doors
Form a protected escape stairway by providing half hour fire resistance to all partitions. Ceiling to be upgraded to provide half hour fire resistance or modified half hour fire resistance as appropriate. Stairway to be protected at all levels - from the loft room/rooms then leading directly to an external door at ground level (no inner rooms allowed). All doors on to the stairway must be FD20 rated fire doors to BS 476 or the European equivalent BS EN 1634 (fitted with intumescent strips rebated around sides & top of door or frame if required by BCO). Where applicable, any glazing in fire doors to be half hour fire resisting and glazing in the walls forming the escape route enclosure to have 30 minutes fire resistance to at least 1.1m above the floor level or stair pitch line.

DORMER CONSTRUCTION
To achieve minimum U Value of 0.18W/m²K

Tiled on treated timber battens with intergrated breathable membrane on a wheater treat external board with intergular fire rating. Wheather board fixed to treated timber frame studs constructed using: 100mm x 50mm head & sole plates and vertical studs (with noggins) at 400mm ctrs or to s/engineer's details & calculations. Insulation between and over studs. Finish with 3mm skim coat of finishing plaster. All junctions to have water tight construction, seal all perimeter joints with tape internally and with silicon sealant externally.

PITCHED ROOF VENTILATION
Maintain a 50mm air gap above insulation in the roof pitch to ventilate roof. Provide opening at eaves level at least equal to continuous strip 25mm wide and opening at ridge equal to continuous strip 5mm wide to promote ventilation.

NEW STAIRCASE
Dimensions to be checked and measured on site prior to fabrication of stairs. Timber stairs to comply with BS585 and with Part K of the Building Regulations. Max rise 220mm, min going 220mm. Two risers plus one going should be between 550 and 700mm. Tapered treads to have going in centre of tread at least the same as the going on the straight. Min 50mm going of tapered treads measured at narrow end. Pitch not to exceed 42 degrees. The width and length of every landing should be at least as great as the smallest width of the flight. Doors which swing across a landing at the bottom of a flight should leave a clear space of at least 400mm across the full width of the flight. Min 2.0m headroom measured vertically above pitch line of stairs and landings. However, if there is not enough space to achieve this height the headroom will be satisfactory if the height measured at the centre of the stair width is l.9 m reducing to 1.8m at one side of the stair. Handrail on staircase to be 900mm above the pitchline, handrail to be at least one side if stairs are less than 1m wide and on both sides if they are wider. Ensure a clear width between handrails of minimum 600mm. Balustrading designed to be unclimbable and should contain no space through which a 100mm sphere could pass. Allow for all structure as designed by a Structural Engineer.

UPGRADE OF SOLID EXTERNAL WALL
To achieve min U-value 0.30 W/m²K
Existing garage wall to be exposed and checked for its suitability. Upgrade existing solid block wall by providing 50mm Celotex GA4000 insulation internally. Provide 12.5mm with VCL over insulation and finish with 3mm plaster skim.
Provide 25mm x 50mm battens at 600mm centres to give a nominal 25mm cavity between the masonry and insulation, (50mm cavity or vandex slurry to be provided, if required by building control). An injected DPC may also be required to the wall if one is not already present and working.
A lesser provision of insulation may be appropriate where meeting such a standard would result in a reduction of more than 5% in the internal floor area of the room.
All work to be in accordance with BS 8000-8:2023 Design and installation of dry lining systems.

PARTIAL FILL CAVITY WALL
To achieve minimum U Value of 0.17W/m²K

20mm two coat sand/cement render to comply to BS EN 13914-1:2005 with waterproof additive on 100mm lightweight block, on blockwork to Structural engineer specification. Ensure a clear residual cavity with insulation fixed to inner leaf constructed using 100mm blockwork to Structural engineer specification. Internal finish with plaster.

PITCHED ROOF VENTILATION
Maintain a 50mm air gap above insulation in the roof pitch to ventilate roof. Provide opening at eaves level at least equal to continuous strip 25mm wide and opening at ridge equal to continuous strip 5mm wide to promote ventilation.

extension architecture
3 River Reach, Gartons Way,
Battersea
London SW11 3SX
Tel (0208) 288 8950 Fax (0871) 918 2798
www.extensionarchitecture.co.uk

This drawing is prepared solely for design and planning submission purposes. It is not intended or suitable for either building regulations or construction purposes and should not be used for such. All dimension shall be check and confirmed with site rep. and any discrepancies between the drawings and site shall be reported to PM. This drawing to be read in conjunction with engineers specification and details. For construction information please refer to all drawings and specification of works.

For any structural steelworks details please refer to structural engineer's drawings & calculations.

The copyright of the drawing and designs remains with Extension Architecture. All copies are only for information about the application, they may not be used for any other purpose without the express written permission of Extension Architecture.

CLIENT: Vik Barodia
PROJECT: 1 Lambourne Drive, KT11 3LB
TITLE: Specifications
NOTES
VERSION | DESCRIPTION | DATE
DRAWN: AY
12.04.2024
VERSION
SHEET REF. NO: 1 LD -PL -BR 17

PLANNING NOTE - The local Planning department to be consulted on any local requirements relating to Planning Permissions and Permitted Development rights. An Artical 4, which removes certain rights. maybe in place. Prior approval to be sought where required.

SINGLE-STOREY EXTENSION

An extension or addition to your house is considered to be permitted development, not requiring an application for planning permission, provided certain limits and conditions are met.

1. On designated land* - no cladding of the exterior. *Designated land (Article 2(3)) includes national parks and the Broads, Areas of Outstanding Natural Beauty, conservation areas and World Heritage Sites.
2. On designated land* - no side extensions. Rear extension - No permitted development for rear extensions of more than one storey. The regime for larger single-storey rear extensions (see point 9) does NOT apply to houses on designated land.
3. No more than half the area of land around the "original house" would be covered by additions or other buildings. Sheds and other outbuildings must be included when calculating the 50 per cent limit.
4. No extension forward of the principal elevation or side elevation fronting a highway.
5. Materials to be similar in appearance to the existing house.
6. Side extensions to be single storey. Width of side extension must not have a width greater than half the width of the original house.
7. Side extensions to have a maximum height of four metres and width no more than half that of the original house.
8. If the extension is within 2m of a boundary, maximum eaves height should be no higher than 3m to be permitted development.
9. Single-storey rear extensions must not extend beyond the rear wall of the original house by more than 4m if a detached house; or more than 3m for any other house. Where not on designated land (Article 2(3)) or a Site of Special Scientific Interest, this limit is increased to 8m if a detached house; or 6m for any other house.
10. Maximum height of a single-storey rear extension of 4m. (or less than 3m if within 2m of a property boundary)
. Maximum eaves and ridge height of extension no higher than existing house.

TWO-STOREY REAR EXTENSION

An extension or addition to your house is considered to be permitted development, not requiring an application for planning permission, provided certain limits and conditions are met.

1. On designated land extensions of more than one storey are not permitted development. * Designated land includes national parks and the Broads, Areas of Outstanding Natural Beauty, conservation areas and World Heritage Sites.
2. Extensions (including previous extensions) and other buildings must not exceed 50% of the total area of land around the original house. * Sheds and other outbuildings must be included when calculating the above 50% limit.
3. Maximum eaves and ridge height of extension no higher than existing house. If extension is within two metres of a boundary maximum eaves height should be no higher than three metres to be permitted development.
4. Extensions of more than one storey must not extend beyond the rear wall of original house by more than three metres or be within seven metres of any boundary opposite the rear wall of the house.
5. Roof pitch of extensions higher than one storey to match that of the existing house, as far as is practicable.
6. Materials used in exterior work to be similar in appearance to those of the exterior of the existing house.
7. Any upper-floor window in a wall or roof slope in a side elevation must be obscure-glazed and nonopening unless the parts which can be opened are more than 1.7 metres above the floor of the room in which it is installed.
8. No balconies or verandas are permitted development.

CDM REGULATIONS 2015

The client must abide by the Construction Design and Management Regulations 2015. The Client must appoint a Contractor, if more than one Contractor is to be involved, the Client will need to appoint (in writing) a Principal Designer (to plan, manage and coordinate the planning and design work), and a Principal Contractor (to plan, manage and coordinate the construction and ensure there are arrangements in place for managing and organising the project).

Domestic Clients

The Domestic Client is to appoint a Principal Designer and a Principal Contractor when there is more than one Contractor, if not your duties will automatically be transferred to the Contractor or Principal Contractor.

The Designer can take on the duties, provided there is a written agreement between you and the Designer to do so.

The Health and Safety Executive is to be notified as soon as possible before construction work starts if the works:

(a) Last longer than 30 working days and has more than 20 workers working simultaneously at any point in the project.
Or:
(b) Exceeds 500 person days.

SITE PREPARATION

Ground to be prepared for new works by removing all unsuitable material, vegetable matter and tree or shrub roots to a suitable depth to prevent future growth. Seal up, cap off, disconnect and remove existing redundant services as necessary. Reasonable precautions must also be taken to avoid danger to health and safety caused by contaminants and ground gases e.g. landfill gases, radon, vapours etc. on or in the ground covered, or to be covered by the building.

EXISTING STRUCTURE

Existing structure including foundations, beams, walls and lintels carrying new and altered loads are to be exposed and checked for adequacy prior to commencement of work and as required by the Building Control Officer.

MATERIALS AND WORKMANSHIP

All works are to be carried out in a workmanlike manner. All materials and workmanship must comply with Regulation 7 of the Building Regulations, all relevant British Standards, European Standards, Agreement Certificates, Product Certification of Schemes (Kite Marks) etc. Products conforming to a European technical standard or harmonised European product should have a CE marking.

BEAMS

Supply and install new structural elements such as new beams, roof structure, floor structure, bearings, and padstones in accordance with the Structural Engineer's calculations and details. New steel beams to be encased in 12.5mm Gyproc FireLine board with staggered joints, Gyproc FireCase or painted in Nullifire S or similar intumescent paint to provide 1/2 hour fire resistance as agreed with Building Control. All fire protection to be installed as detailed by specialist manufacturer.

STRIP FOUNDATION

Provide 1000mm x 600mm concrete foundation, concrete mix to conform to BS EN 206:2013 and BS 8500-2. All foundations to be a minimum of 1000mm below ground level, exact depth to be agreed on site with Building Control Officer to suit site conditions. All constructed in accordance with 2010 Building Regulations A1/2 and BS 8004:2015 Code of Practice for Foundations. Ensure foundations are constructed below invert level of any adjacent drains. Base of foundations supporting internal walls to be min 600mm below ground level. Sulphate resistant cement to be used if required. Please note that should any adverse soil conditions be found or any major tree roots in excavations, the Building Control Officer is to be contacted and the advice of a Structural Engineer should be sought.

BACKGROUND VENTLATION

Controllable background ventilation at least 1700mm above floor level to be provided to habitable rooms and kitchens at a rate of min 10,000mm², and to wet rooms at a rate of min 5000mm², Background ventilators to be tested to BS EN 13141-1
Background ventilator equivalent area and operation to be measured and recorded.

INTERNAL STUD PARTITIONS

100mm x 50mm softwood treated timbers studs at 400mm ctrs with 50 x 100mm head and sole plates and solid intermediate horizontal noggins at 1/3 height or 450mm. Provide min 10kg/m³ density acoustic soundproof quilt tightly packed (eg. 100mm Rockwool or Isowool mineral fibre sound insulation) in all voids the full depth of the stud. Partitions built off doubled up joists where partitions run parallel or provide noggins where at right angles, or built off DPC on thickened concrete slab if solid ground floor. Walls faced throughout with 12.5mm plaster board with skim plaster finish. Taped and jointed complete with beads and stops.

SMOKE DETECTION

Mains operated linked smoke alarm detection system to BS EN 14604 and BS 5839-6:2019 to at least a Grade D category LD3 standard. System to be mains powered with battery back up. Smoke alarms should be sited so that there is a smoke alarm in the circulation space on all levels/storeys and within 3m of the door to every habitable room. If ceiling mounted they should be 300mm from the walls and light fittings. Mains-wired, interlinked heat detector to be provided to the kitchen and smoke detectors to principal living rooms, if required by Building Control.

INTERMEDIATE FLOORS

Intermediate floor to be 25mm t&g flooring grade chipboard or floorboards laid on C24 joists at 400mm ctrs (see Engineer's calculation for sizes and details). Lay 100mm Rockwool mineral fibre quilt insulation min 10kg/m³ or equivalent between floor joists. Ceiling to be 12.5 Fire-Line plasterboard with skim plaster set and finish. Joist spans over 2.5m to be strutted at mid span using 38 x 38mm herringbone strutting or 38mm solid strutting (at least 2/3 of joist depth). In areas such as kitchens, utility rooms and bathrooms, flooring to be moisture resistant grade in accordance with BS EN 312. Identification marking must be laid upper most to allow easy identification. Provide lateral restraint where joists run parallel to walls, floors are to be strapped to walls with 1200mm x 30mm x 5mm galvanised mild steel straps or other approved in compliance with BS EN 845-1 at max 2.0m centres, straps to be taken across minimum 3 no. joists. Straps to be built into walls. Provide 38mm wide x ¾ depth solid noggins between joists at strap positions.

NEW AND REPLACEMENT WINDOWS

New and replacement windows to be double glazed with 16-20mm argon gap and soft coat low-E glass. Window Energy Rating to be Band B or better and to achieve U-value of 1.4 W/m²K. The door and window openings should be limited to 25% of the extension floor area plus the area of any existing openings covered by the extension.
Insulated plasterboard to be used in reveals to abut jambs and to be considered within reveal soffits. Fully insulated and continuous cavity closers to be used around reveals.
Windows and door frames to be taped to surrounding openings using air sealing tape.
Windows to be fitted with trickle vents to provide adequate background ventilation in accordance with Approved Document F.

DPC

Provide horizontal strip polymer (hyload) damp proof course to both internal and external skins minimum 150mm above external ground level. New DPC to be made continuous with existing DPC's and with floor DPM. Vertical DPC to be installed at all reveals where cavity is closed.

MOVEMENT JOINTS

Movement joints to be provided at the following maximum spacing:
Clay brickwork - 12m.
Calcium silicate brick - 7.5-9m.
Lightweight concrete block - density not exceeding 1,500kg/m3 - 6m.
Dense concrete block - density exceeding 1,500kg/m3 – 7.5-9m.
Any masonry in a parapet wall (length to height ratio greater than 3:1) - half the above spacings and 1.5m from corners.
Movement joint widths for clay bricks to be not less than 1.3mm/m i.e. 12m = 16mm and for other masonry not less than 10mm.
Additional movement joints may be required where the aspect ratio of the wall (length :height) is more than 3:1.
Considerations to be given to BS EN 1996-1-2:2005 Eurocode 6. Design of masonry structure.

CAVITIES

Provide cavity trays over openings and where roofs abut walls. All cavities to be closed at eaves and around openings using Thermabate or similar non combustible insulated cavity closers. Provide vertical DPCs around openings and abutments. All cavity trays must have 150mm upstands and suitable cavity weep holes (min 2) at max 900mm centres.

C2. CONDENSATION

Walls, floors and roof of the building to be designed and constructed so that their structural and thermal performance will not be adversely affected by interstitial condensation, surface condensation or mould growth. Account to be taken of the building's form and orientation in relation to topography, prevailing winds, sunlight and over-shadowing, and the rate at which humidity is generated.
Materials with the highest vapour resistance should be located on the warm side of a thermal element. VCLs to be provided where necessary.
The junctions between elements are designed to Accredited Construction Details or guidance of BRE IP17/01] and BS 5250:2021 Management of moisture in buildings to be followed.

NEW AND REPLACEMENT DOORS

New and replacement doors to achieve a U-Value of 1.4W/m²K. Glazed areas to be double glazed with 16-20mm argon gap and soft low-E glass. Glass to be toughened or laminated safety glass to BS 6206, BS EN 14179 or BS EN ISO 12543-1 and Part K (Part N in Wales) of the current Building Regulations.
Insulated plasterboard to be used in reveals to abut jambs and to be considered within reveal soffits. Fully insulated and continuous cavity closers to be used around reveals.
Windows and door frames to be taped to surrounding openings using air sealing tape.

ROOF LIGHTS

Min U-value of 1.6 W/m²K.
Roof-lights to be double glazed with 16mm argon gap and soft low-E glass. Window Energy Rating to be Band C or better. Roof lights to be fitted in accordance with manufacturer's instructions, with rafters doubled up to sides and suitable flashings provided.

RAINWATER DRAINAGE

New rainwater goods to be new 110mm upvc half round gutters taken to and connected into 68mm dia upvc downpipes

extension architecture
3 River Reach, Gartons Way,
Battersea
London SW11 3SX
Tel (0208) 288 8950 Fax (0871) 918 2798
www.extensionarchitecture.co.uk

This drawing is prepared solely for design and planning submission purposes. It is not intended or suitable for either building regulations or construction purposes and should not be used for such. All dimension shall be check and confirmed with site rep. and any discrepancies between the drawings and site shall be reported to PM. This drawing to be read in conjunction with engineers specification and details. For construction information please refer to all drawings and specification of works.

For any structural steelworks details please refer to structural engineer's drawings & calculations.

The copyright of the drawing and designs remains with Extension Architecture. All copies are only for information about the application, they may not be used for any other purpose without the express written permission of Extension Architecture.

CLIENT: Vik Barodia

PROJECT: 1 Lambourne Drive, KT11 3LB

TITLE: Specifications

NOTES

VERSION	DESCRIPTION	DATE

12.04.2024

DRAWN: AY

VERSION

SHEET REF. NO: 1 LD -PL -BR 18