
THE NEW MASS CONCRETE STRIP FOOTINGS ARE TO BE GRADE 'GEN 3'. THE FOOTINGS ARE BASED ON A SAFE BEARING PRESSURE OF 100kPa.
THE BUILDER AND BUILDING INSPECTOR ARE RESPONSIBLE FOR CONFIRMING THE ADEQUACY OF THE BEARING STRATA. FOOTINGS TO BE 600mm WIDE X 1600mm DEEP NEAR GARDEN HEDGE TREES

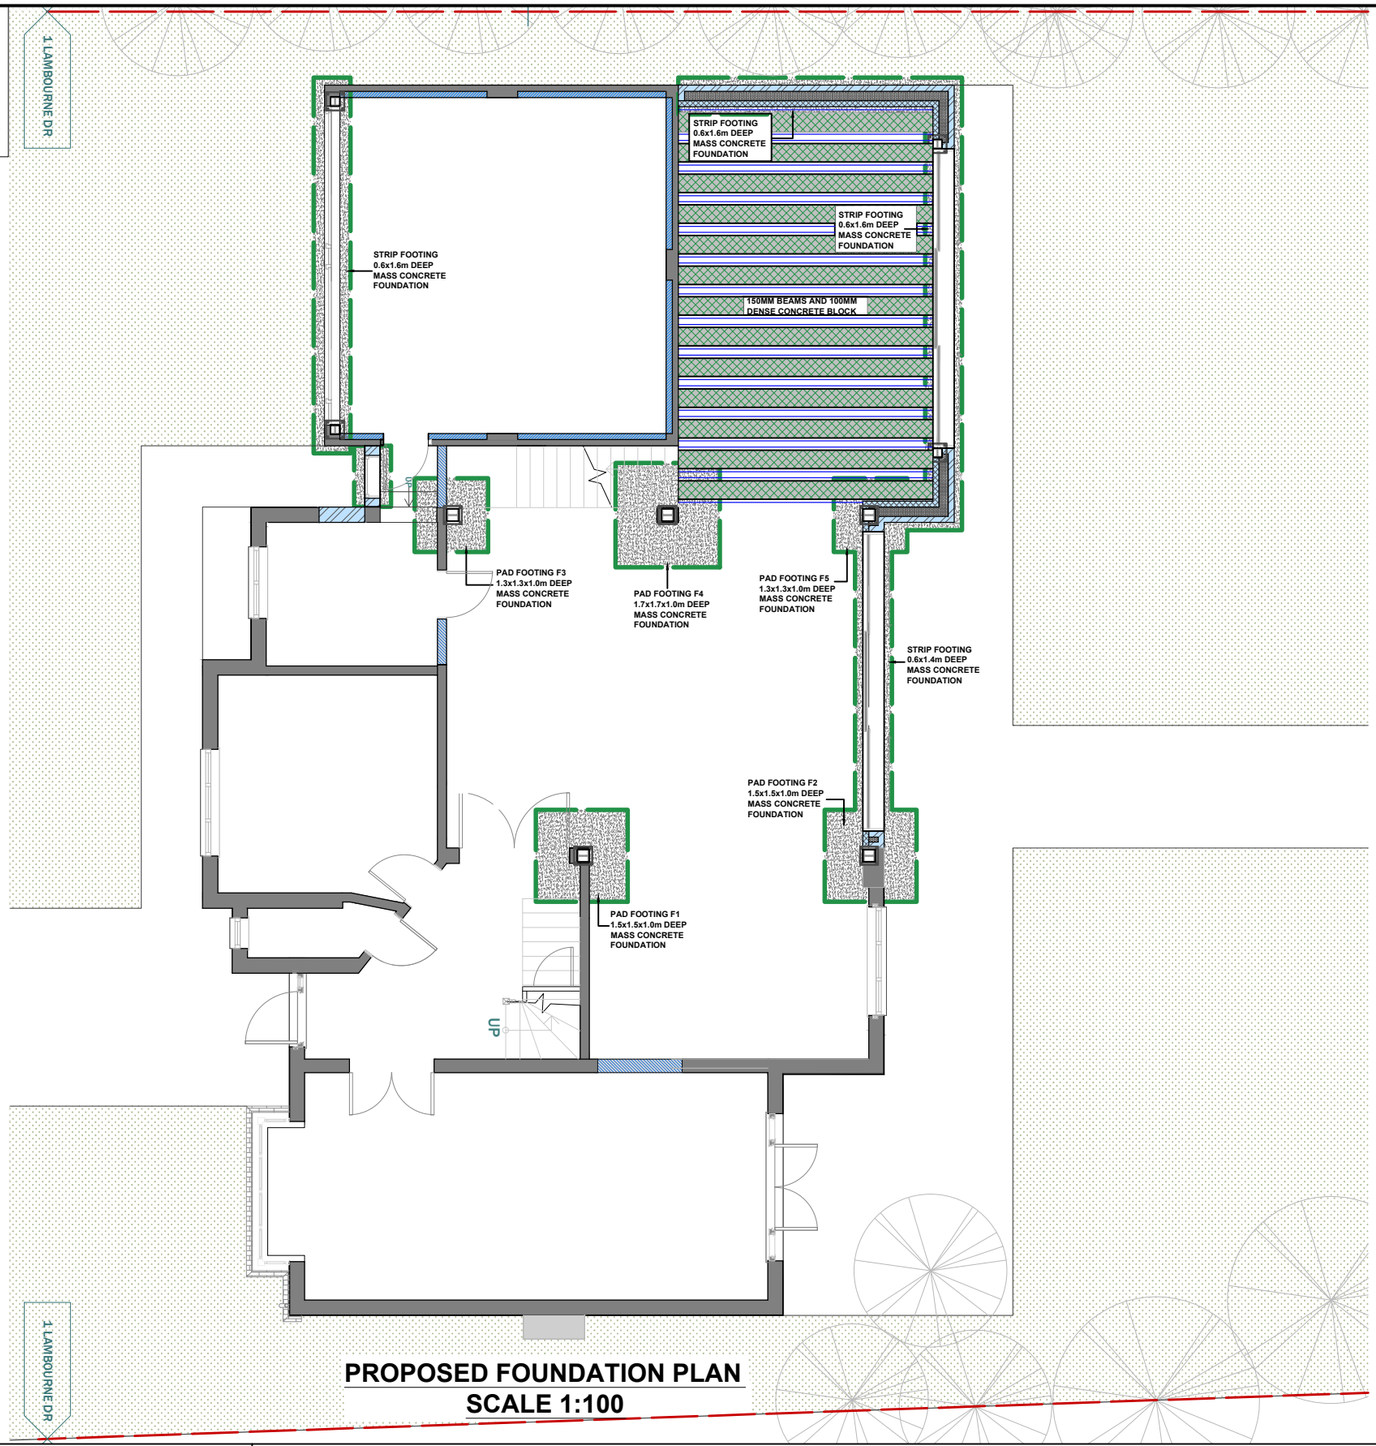

PROPOSED FOUNDATION PLAN
SCALE 1:100

THE CONTRACTOR IS TO BE RESPONSIBLE FOR ALL TEMPORARY SUPPORT DURING THE EXECUTION OF THE WORKS, AND TO SUBMIT HIS OWN METHOD STATEMENT FOR THE TEMPORARY AND PERMANENT CONSTRUCTION.

GENERAL NOTES:

1. ALL STEEL DIMENSIONS CHECKED ON SITE PRIOR TO FABRICATION.
2. SUPPLY AND INSTALL ALL STRUCTURAL ELEMENTS SUCH AS BEAMS, ROOF STRUCTURE, FLOOR STRUCTURE, BEARINGS, AND PADSTONES IN ACCORDANCE WITH THE STRUCTURAL ENGINEER'S CALCULATIONS AND DETAILS.
3. NEW STEEL BEAMS TO BE ENCASED IN 12.5MM GYPROC FIRELINE BOARD WITH STAGGERED JOINTS, GYPROC FIRECASE OR PAINTED IN NULLIFIRE S OR SIMILAR INTUMESCENT PAINT TO PROVIDE 1/2 HOUR FIRE RESISTANCE AS AGREED WITH BUILDING CONTROL. ALL FIRE PROTECTION TO BE INSTALLED AS DETAILED BY SPECIALIST MANUFACTURER.
4. DOUBLE JOISTS/RAFTERS, TRIPLE JOISTS & TIMBER BEAMS (TB) BOLTED TOGETHER WITH M10 (8.8) BOLTS @ 400 STAGGERED CTRS. + 50Ø DOUBLE SIDED TOOTH CONNECTORS +50X50X5 WASHERS EACH SIDE.
5. INSERT DOUBLE-UP JOISTS UNDER BATHROOMS.
6. STEEL GRADE - S355
7. TIMBER GRADE - (C24)

STRAPPINNG NOTES:


1. STRAPPING OF FLOORS PROVIDE LATERAL RESTRAINT WHERE JOISTS RUN PARALLEL TO WALLS, FLOORS ARE TO BE STRAPPED TO WALLS WITH 1000MM X 30MM X 5MM GALVANISED MILD STEEL STRAPS OR OTHER APPROVED IN COMPLIANCE WITH BS EN 845-1 AT MAX 2.0M CENTRES, STRAPS TO BE TAKEN ACROSS MINIMUM OF 3 JOISTS. STRAPS TO BE BUILT INTO WALLS.
2. PROVIDE 38MM WIDE X ¾ DEPTH SOLID NOGGINS BETWEEN JOISTS AT STRAP POSITIONS. WHERE THE JOISTS SPAN OVER 2.5M, PROVIDE ONE ROW OF STRUTTING AT MID SPAN TO PREVENT JOISTS TWISTING + AT EACH END SUPPORTS.
3. STRAPPING FOR PITCHED ROOF ALL EXTERNAL WALLS SUPPORTING THE ROOF RAFTERS TO BE RESTRAINED AT ROOF LEVEL USING 1000MM X 30MM X 5MM GALVANISED MILD STEEL HORIZONTAL STRAPS (OR OTHER APPROVED TO BSEN 845-1) BUILT INTO WALLS AT MAX 2000MM CENTRES AND SCREW FIXED TO THE RAFTERS.
4. ALL WALL PLATES TO BE 100 X 50MM FIXED TO INNER SKIN OF CAVITY WALL USING 30MM X 5MM X 1000MM GALVANIZED METAL STRAPS OR OTHER APPROVED TO BSEN 845-1 AT MAXIMUM 1.5 CENTRES.
5. PROVIDE 30X5X1000MM GALVANISED MILD STEEL STRAPS FIXED OVER RIDGE BEAM TO RAFTERS AND JOISTS @ MAX. 0.8M CRS.

extension architecture

EXTENSION ARCHITECTURE & INTERIORS LTD
231 COBDEN HOUSE,
ROEHAMPTON LANE,
LONDON, SW15 4LB
TEL (0208) 288 8950
FAX (0871) 918 2798
www.extensionarchitecture.co.uk

THESE STRUCTURAL DRAWINGS HAVE BEEN PREPARED BY EXTENSION ARCHITECTURE WITH THE SOLE PURPOSE OF PROVIDING STRUCTURAL ENGINEERING SOLUTIONS. ANY QUESTIONS ABOUT STRUCTURAL COMPLIANCE SHOULD BE DIRECTED TO EXTENSION ARCHITECTURE OR THE LOCAL BUILDING CONTROL AUTHORITY. COLLABORATION WITH THE BUILDING CONTROL AUTHORITY FOR NECESSARY SITE INSPECTIONS AND APPROVALS IS COMPULSORY. WHILE THESE DRAWINGS ARE INTENDED FOR DISCUSSIONS WITH THE BUILDING CONTROL AUTHORITY, ON-SITE VERIFICATION BY THE BUILDER OR CONTRACTOR IS ESSENTIAL BEFORE CONSTRUCTION. THE BUILDER OR CONTRACTOR IS RESPONSIBLE FOR MAINTAINING RECORDS OF ANY DISCREPANCIES FOUND OR ON-SITE CHANGES THROUGHOUT CONSTRUCTION. CHARGES APPLY FOR EXTENSION ARCHITECTURE'S ON-SITE SUPERVISION, AND FEES APPLY FOR PROJECT MANAGER SERVICES IN CASE OF BUILDER ERRORS OR ISSUES. THE COPYRIGHT OF THE DRAWINGS AND DESIGNS REMAINS WITH EXTENSION ARCHITECTURE, REQUIRING EXPRESS WRITTEN PERMISSION FOR USAGE BEYOND THE APPLICATION.

DRAWN	CLIENT NAME: VIK BARODIA	DRAWING No.: A01
CHECKED	PROJECT NAME: 1 LAMBOURNE DRIVE	SCALE: 1:100 @A3
JOB NO.	TITLE: PROPOSED FOUNDATION PLAN	DATE: 31-07-2024
REVISION: F		

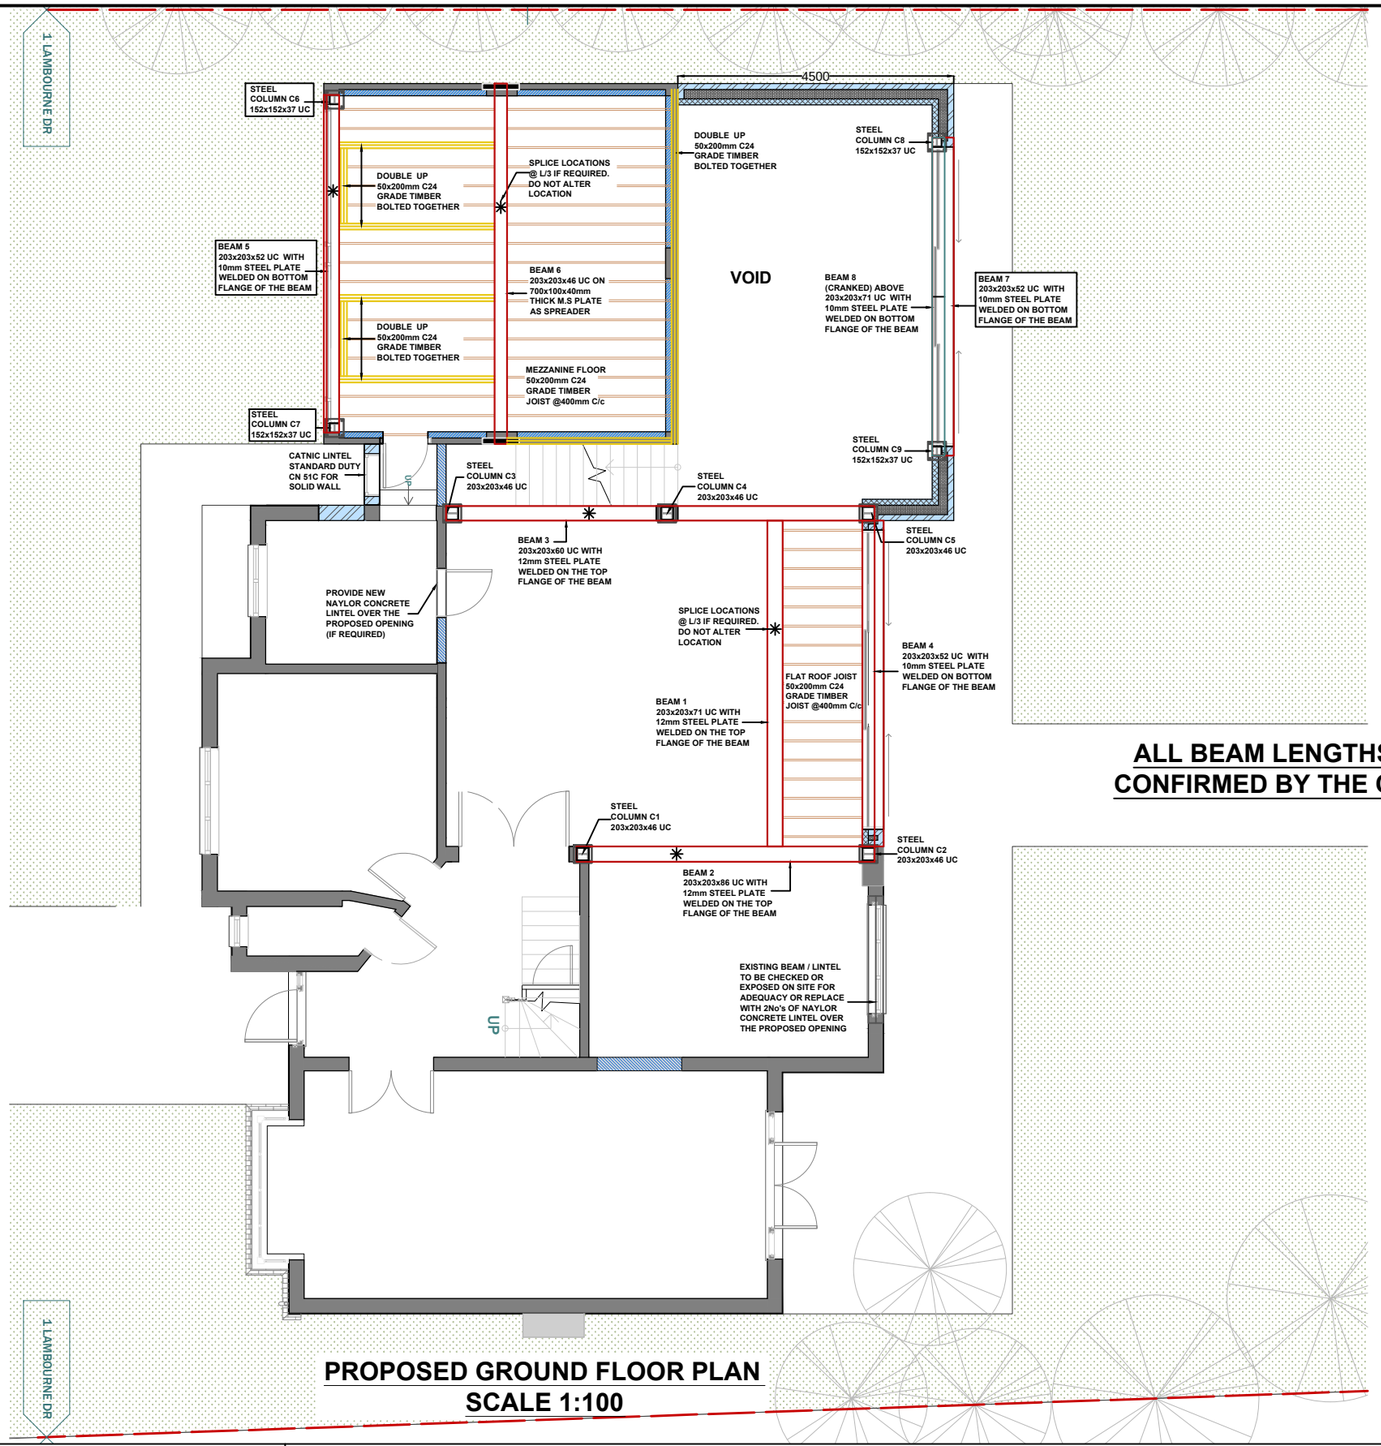

ALL BEAM LENGTHS ARE TO BE CONFIRMED BY THE CONTRACTOR

PROPOSED GROUND FLOOR PLAN
SCALE 1:100

THE CONTRACTOR IS TO BE RESPONSIBLE FOR ALL TEMPORARY SUPPORT DURING THE EXECUTION OF THE WORKS, AND TO SUBMIT HIS OWN METHOD STATEMENT FOR THE TEMPORARY AND PERMANENT CONSTRUCTION.

GENERAL NOTES:

1. ALL STEEL DIMENSIONS CHECKED ON SITE PRIOR TO FABRICATION.
2. SUPPLY AND INSTALL ALL STRUCTURAL ELEMENTS SUCH AS BEAMS, ROOF STRUCTURE, FLOOR STRUCTURE, BEARINGS, AND PADSTONES IN ACCORDANCE WITH THE STRUCTURAL ENGINEER'S CALCULATIONS AND DETAILS.
3. NEW STEEL BEAMS TO BE ENCASED IN 12.5MM GYPROC FIRELINE BOARD WITH STAGGERED JOINTS, GYPROC FIRECASE OR PAINTED IN NULLIFIRE S OR SIMILAR INTUMESCENT PAINT TO PROVIDE 1/2 HOUR FIRE RESISTANCE AS AGREED WITH BUILDING CONTROL. ALL FIRE PROTECTION TO BE INSTALLED AS DETAILED BY SPECIALIST MANUFACTURER.
4. DOUBLE JOISTS/RAFTERS, TRIPLE JOISTS & TIMBER BEAMS (TB) BOLTED TOGETHER WITH M10 (8.8) BOLTS @ 400 STAGGERED CTRS. + 50Ø DOUBLE SIDED TOOTH CONNECTORS +50X50X5 WASHERS EACH SIDE.
5. INSERT DOUBLE-UP JOISTS UNDER BATHROOMS.
6. STEEL GRADE - S355
7. TIMBER GRADE - (C24)

STRAPPINNG NOTES:


1. STRAPPING OF FLOORS PROVIDE LATERAL RESTRAINT WHERE JOISTS RUN PARALLEL TO WALLS, FLOORS ARE TO BE STRAPPED TO WALLS WITH 1000MM X 30MM X 5MM GALVANISED MILD STEEL STRAPS OR OTHER APPROVED IN COMPLIANCE WITH BS EN 845-1 AT MAX 2.0M CENTRES, STRAPS TO BE TAKEN ACROSS MINIMUM OF 3 JOISTS. STRAPS TO BE BUILT INTO WALLS.
2. PROVIDE 38MM WIDE X ¾ DEPTH SOLID NOGGINS BETWEEN JOISTS AT STRAP POSITIONS. WHERE THE JOISTS SPAN OVER 2.5M, PROVIDE ONE ROW OF STRUTTING AT MID SPAN TO PREVENT JOISTS TWISTING + AT EACH END SUPPORTS.
3. STRAPPING FOR PITCHED ROOF ALL EXTERNAL WALLS SUPPORTING THE ROOF RAFTERS TO BE RESTRAINED AT ROOF LEVEL USING 1000MM X 30MM X 5MM GALVANISED MILD STEEL HORIZONTAL STRAPS (OR OTHER APPROVED TO BSEN 845-1) BUILT INTO WALLS AT MAX 2000MM CENTRES AND SCREW FIXED TO THE RAFTERS.
4. ALL WALL PLATES TO BE 100 X 50MM FIXED TO INNER SKIN OF CAVITY WALL USING 30MM X 5MM X 1000MM GALVANIZED METAL STRAPS OR OTHER APPROVED TO BSEN 845-1 AT MAXIMUM 1.5 CENTRES.
5. PROVIDE 30X5X1000MM GALVANISED MILD STEEL STRAPS FIXED OVER RIDGE BEAM TO RAFTERS AND JOISTS @ MAX. 0.8M CRS.

extension architecture

EXTENSION ARCHITECTURE & INTERIORS LTD
231 COBDEN HOUSE,
ROEHAMPTON LANE,
LONDON, SW15 4LB
TEL (0208) 288 8950
FAX (0871) 918 2798
www.extensionarchitecture.co.uk

THESE STRUCTURAL DRAWINGS HAVE BEEN PREPARED BY EXTENSION ARCHITECTURE WITH THE SOLE PURPOSE OF PROVIDING STRUCTURAL ENGINEERING SOLUTIONS. ANY QUESTIONS ABOUT STRUCTURAL COMPLIANCE SHOULD BE DIRECTED TO EXTENSION ARCHITECTURE OR THE LOCAL BUILDING CONTROL AUTHORITY. COLLABORATION WITH THE BUILDING CONTROL AUTHORITY FOR NECESSARY SITE INSPECTIONS AND APPROVALS IS COMPULSORY. WHILE THESE DRAWINGS ARE INTENDED FOR DISCUSSIONS WITH THE BUILDING CONTROL AUTHORITY, ON-SITE VERIFICATION BY THE BUILDER OR CONTRACTOR IS ESSENTIAL BEFORE CONSTRUCTION. THE BUILDER OR CONTRACTOR IS RESPONSIBLE FOR MAINTAINING RECORDS OF ANY DISCREPANCIES FOUND OR ON-SITE CHANGES THROUGHOUT CONSTRUCTION. CHARGES APPLY FOR EXTENSION ARCHITECTURE'S ON-SITE SUPERVISION, AND FEES APPLY FOR PROJECT MANAGER SERVICES IN CASE OF BUILDER ERRORS OR ISSUES. THE COPYRIGHT OF THE DRAWINGS AND DESIGNS REMAINS WITH EXTENSION ARCHITECTURE, REQUIRING EXPRESS WRITTEN PERMISSION FOR USAGE BEYOND THE APPLICATION.

DRAWN	CLIENT NAME: VIK BARODIA	DRAWING No.: A02
CHECKED	PROJECT NAME: 1 LAMBOURNE DRIVE	SCALE: 1:100 @A3
JOB NO.	TITLE: PROPOSED GROUND FLOOR PLAN	DATE: 31-07-2024
REVISION: F		

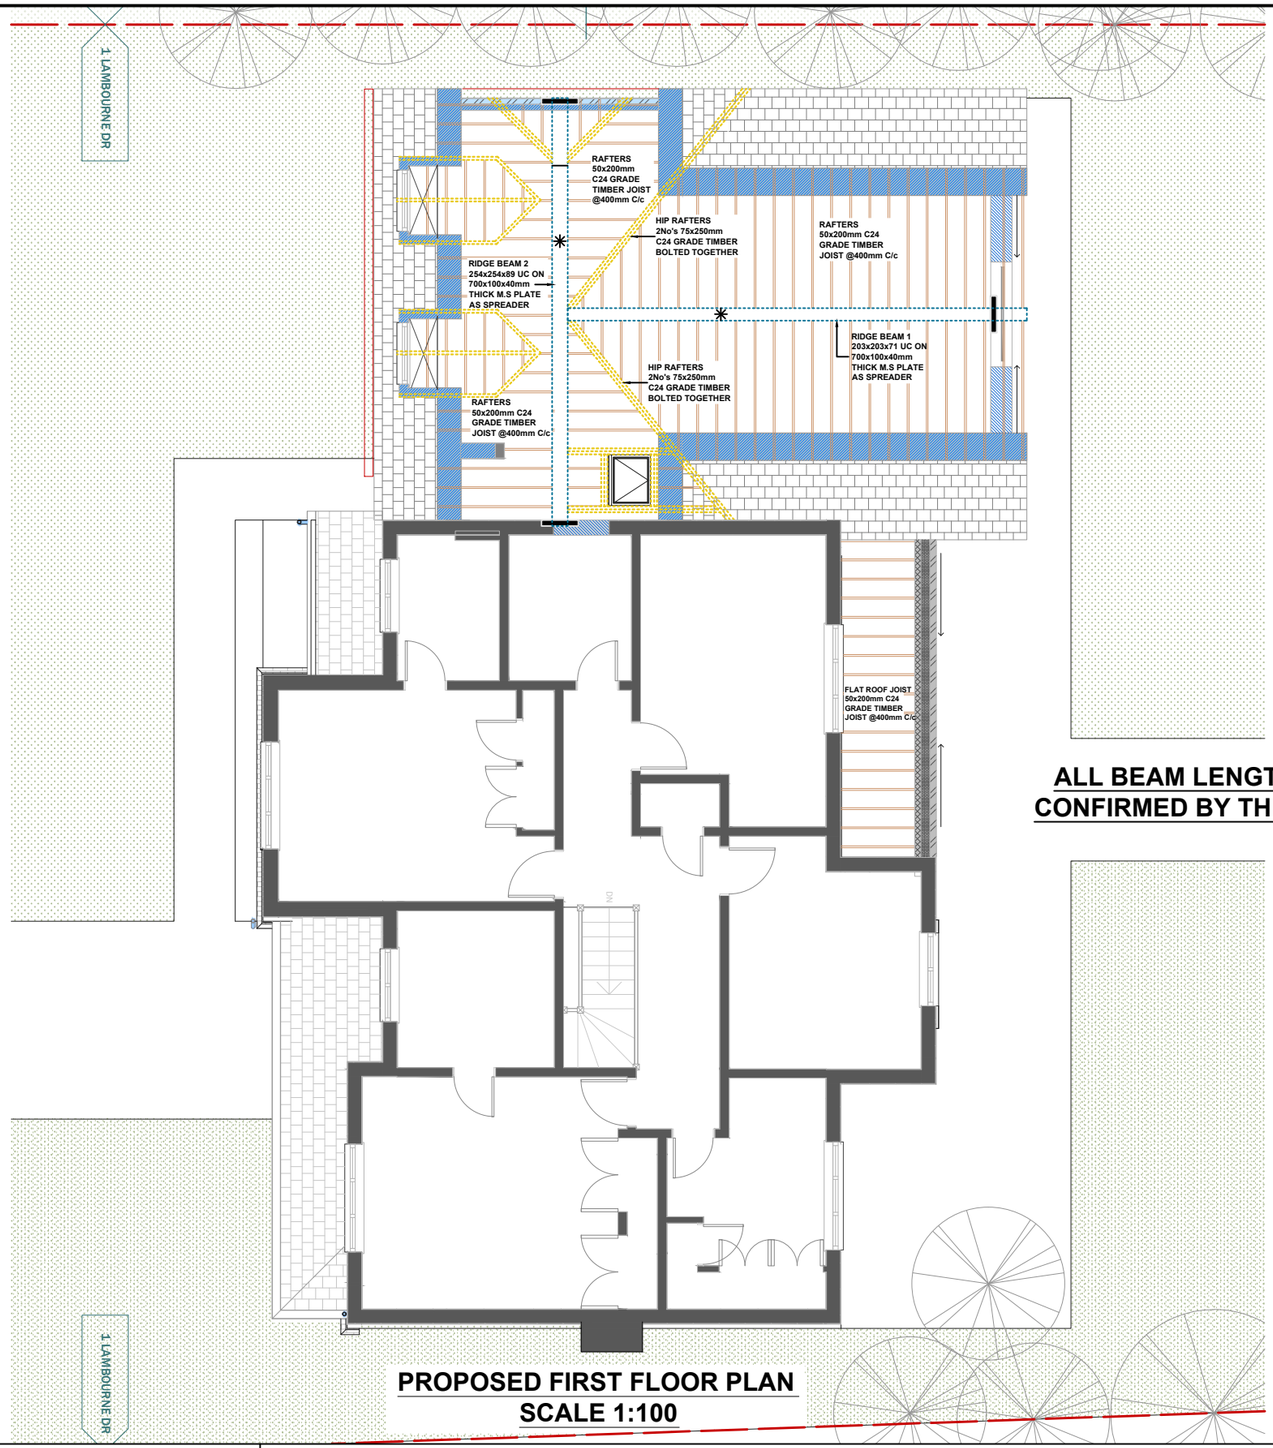

ALL BEAM LENGTHS ARE TO BE CONFIRMED BY THE CONTRACTOR

PROPOSED FIRST FLOOR PLAN
SCALE 1:100

THE CONTRACTOR IS TO BE RESPONSIBLE FOR ALL TEMPORARY SUPPORT DURING THE EXECUTION OF THE WORKS, AND TO SUBMIT HIS OWN METHOD STATEMENT FOR THE TEMPORARY AND PERMANENT CONSTRUCTION.

GENERAL NOTES:

1. ALL STEEL DIMENSIONS CHECKED ON SITE PRIOR TO FABRICATION.
2. SUPPLY AND INSTALL ALL STRUCTURAL ELEMENTS SUCH AS BEAMS, ROOF STRUCTURE, FLOOR STRUCTURE, BEARINGS, AND PADSTONES IN ACCORDANCE WITH THE STRUCTURAL ENGINEER'S CALCULATIONS AND DETAILS.
3. NEW STEEL BEAMS TO BE ENCASED IN 12.5MM GYPROC FIRELINE BOARD WITH STAGGERED JOINTS, GYPROC FIRECASE OR PAINTED IN NULLIFIRE S OR SIMILAR INTUMESCENT PAINT TO PROVIDE 1/2 HOUR FIRE RESISTANCE AS AGREED WITH BUILDING CONTROL. ALL FIRE PROTECTION TO BE INSTALLED AS DETAILED BY SPECIALIST MANUFACTURER.
4. DOUBLE JOISTS/RAFTERS, TRIPLE JOISTS & TIMBER BEAMS (TB) BOLTED TOGETHER WITH M10 (8.8) BOLTS @ 400 STAGGERED CTRS. + 50Ø DOUBLE SIDED TOOTH CONNECTORS +50X50X5 WASHERS EACH SIDE.
5. INSERT DOUBLE-UP JOISTS UNDER BATHROOMS.
6. STEEL GRADE - S355
7. TIMBER GRADE - (C24)

STRAPPINNG NOTES:


1. STRAPPING OF FLOORS PROVIDE LATERAL RESTRAINT WHERE JOISTS RUN PARALLEL TO WALLS, FLOORS ARE TO BE STRAPPED TO WALLS WITH 1000MM X 30MM X 5MM GALVANISED MILD STEEL STRAPS OR OTHER APPROVED IN COMPLIANCE WITH BS EN 845-1 AT MAX 2.0M CENTRES, STRAPS TO BE TAKEN ACROSS MINIMUM OF 3 JOISTS. STRAPS TO BE BUILT INTO WALLS.
2. PROVIDE 38MM WIDE X ¾ DEPTH SOLID NOGGINS BETWEEN JOISTS AT STRAP POSITIONS. WHERE THE JOISTS SPAN OVER 2.5M, PROVIDE ONE ROW OF STRUTTING AT MID SPAN TO PREVENT JOISTS TWISTING + AT EACH END SUPPORTS.
3. STRAPPING FOR PITCHED ROOF ALL EXTERNAL WALLS SUPPORTING THE ROOF RAFTERS TO BE RESTRAINED AT ROOF LEVEL USING 1000MM X 30MM X 5MM GALVANISED MILD STEEL HORIZONTAL STRAPS (OR OTHER APPROVED TO BSEN 845-1) BUILT INTO WALLS AT MAX 2000MM CENTRES AND SCREW FIXED TO THE RAFTERS.
4. ALL WALL PLATES TO BE 100 X 50MM FIXED TO INNER SKIN OF CAVITY WALL USING 30MM X 5MM X 1000MM GALVANIZED METAL STRAPS OR OTHER APPROVED TO BSEN 845-1 AT MAXIMUM 1.5 CENTRES.
5. PROVIDE 30X5X1000MM GALVANISED MILD STEEL STRAPS FIXED OVER RIDGE BEAM TO RAFTERS AND JOISTS @ MAX. 0.8M CRS.

extension architecture

EXTENSION ARCHITECTURE & INTERIORS LTD
231 COBDEN HOUSE,
ROEHAMPTON LANE,
LONDON, SW15 4LB
TEL (0208) 288 8950
FAX (0871) 918 2798
www.extensionarchitecture.co.uk

THESE STRUCTURAL DRAWINGS HAVE BEEN PREPARED BY EXTENSION ARCHITECTURE WITH THE SOLE PURPOSE OF PROVIDING STRUCTURAL ENGINEERING SOLUTIONS. ANY QUESTIONS ABOUT STRUCTURAL COMPLIANCE SHOULD BE DIRECTED TO EXTENSION ARCHITECTURE OR THE LOCAL BUILDING CONTROL AUTHORITY. COLLABORATION WITH THE BUILDING CONTROL AUTHORITY FOR NECESSARY SITE INSPECTIONS AND APPROVALS IS COMPULSORY. WHILE THESE DRAWINGS ARE INTENDED FOR DISCUSSIONS WITH THE BUILDING CONTROL AUTHORITY, ON-SITE VERIFICATION BY THE BUILDER OR CONTRACTOR IS ESSENTIAL BEFORE CONSTRUCTION. THE BUILDER OR CONTRACTOR IS RESPONSIBLE FOR MAINTAINING RECORDS OF ANY DISCREPANCIES FOUND OR ON-SITE CHANGES THROUGHOUT CONSTRUCTION. CHARGES APPLY FOR EXTENSION ARCHITECTURE'S ON-SITE SUPERVISION, AND FEES APPLY FOR PROJECT MANAGER SERVICES IN CASE OF BUILDER ERRORS OR ISSUES. THE COPYRIGHT OF THE DRAWINGS AND DESIGNS REMAINS WITH EXTENSION ARCHITECTURE, REQUIRING EXPRESS WRITTEN PERMISSION FOR USAGE BEYOND THE APPLICATION.

DRAWN	CLIENT NAME: VIK BARODIA	DRAWING No.: A03
CHECKED	PROJECT NAME: 1 LAMBOURNE DRIVE	SCALE: 1:100 @A3
JOB NO.	TITLE: PROPOSED FIRST FLOOR PLAN	DATE: 31-07-2024
REVISION: F		

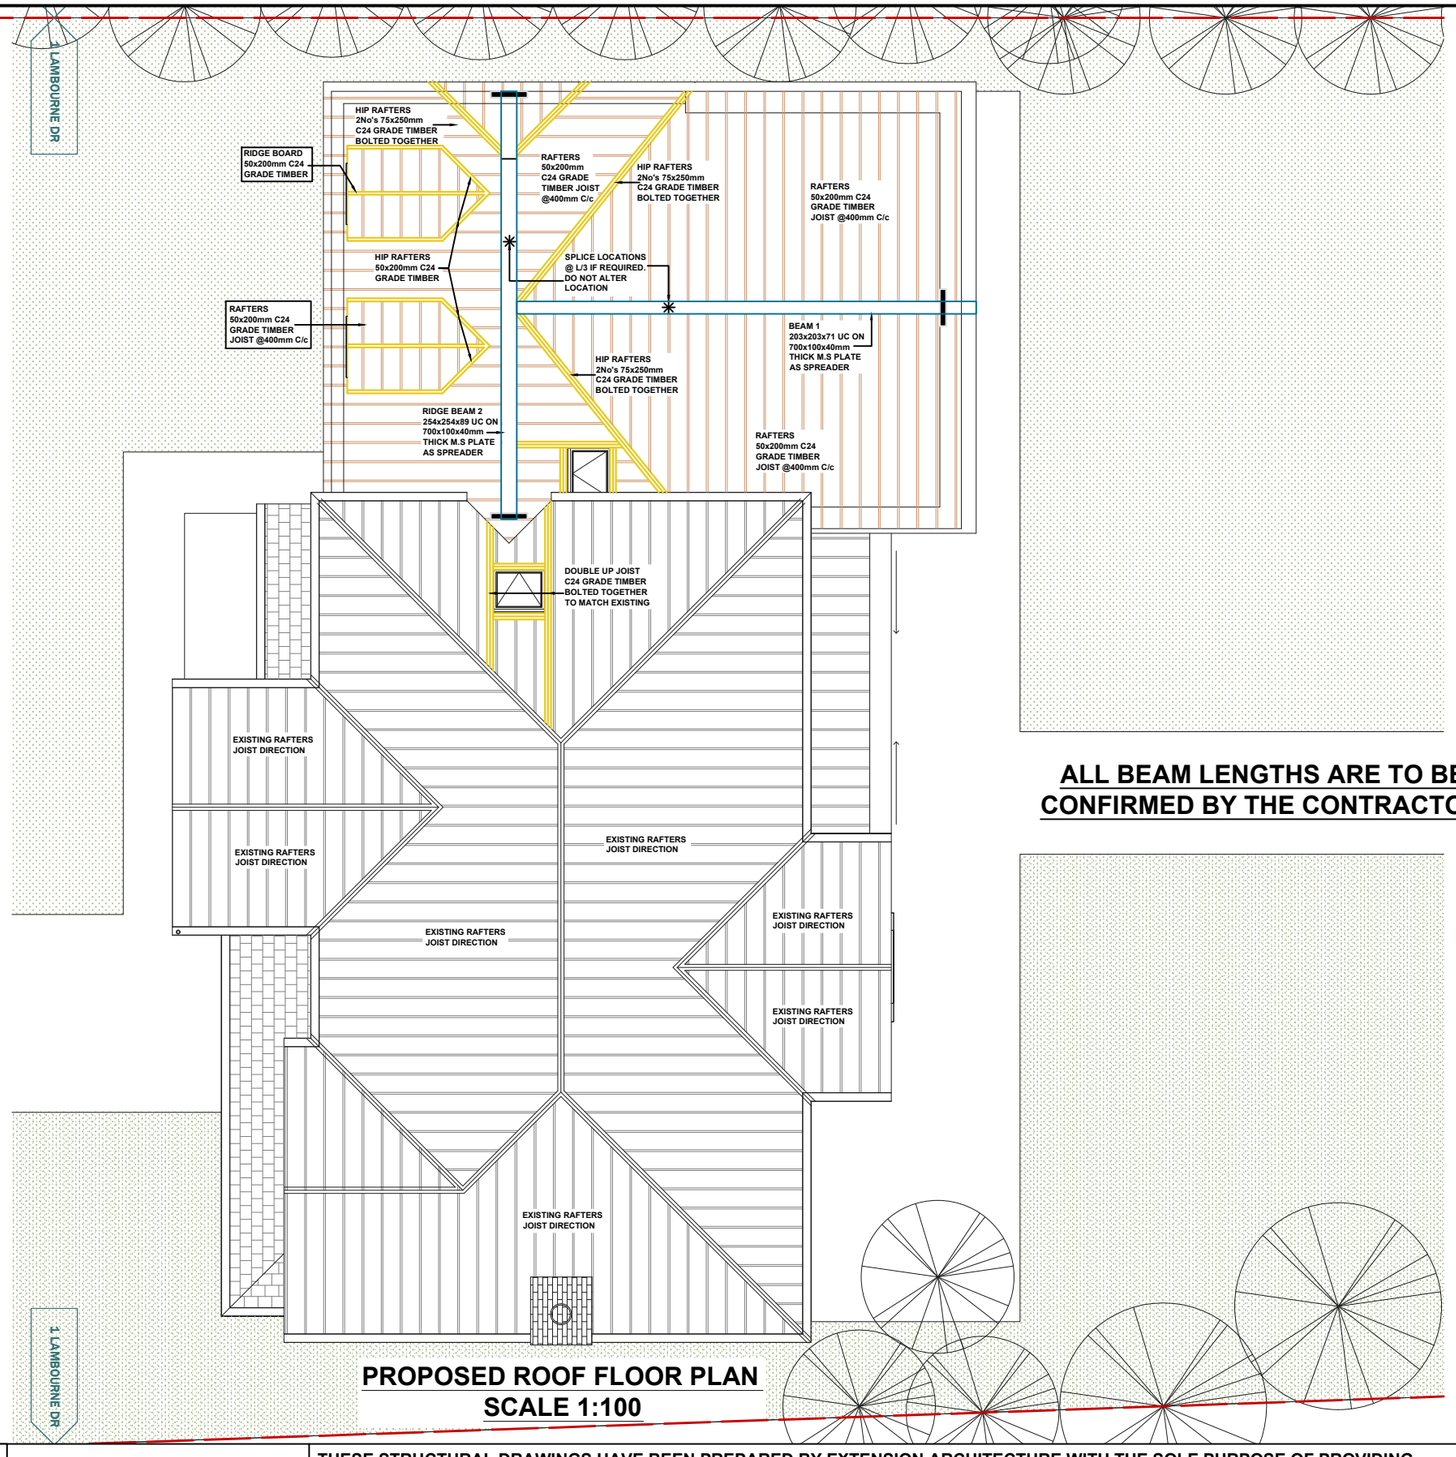

PROPOSED ROOF FLOOR PLAN
SCALE 1:100

ALL BEAM LENGTHS ARE TO BE CONFIRMED BY THE CONTRACTOR

THE CONTRACTOR IS TO BE RESPONSIBLE FOR ALL TEMPORARY SUPPORT DURING THE EXECUTION OF THE WORKS, AND TO SUBMIT HIS OWN METHOD STATEMENT FOR THE TEMPORARY AND PERMANENT CONSTRUCTION.

GENERAL NOTES:

1. ALL STEEL DIMENSIONS CHECKED ON SITE PRIOR TO FABRICATION.
2. SUPPLY AND INSTALL ALL STRUCTURAL ELEMENTS SUCH AS BEAMS, ROOF STRUCTURE, FLOOR STRUCTURE, BEARINGS, AND PADSTONES IN ACCORDANCE WITH THE STRUCTURAL ENGINEER'S CALCULATIONS AND DETAILS.
3. NEW STEEL BEAMS TO BE ENCASED IN 12.5MM GYPROC FIRELINE BOARD WITH STAGGERED JOINTS, GYPROC FIRECASE OR PAINTED IN NULLIFIRE S OR SIMILAR INTUMESCENT PAINT TO PROVIDE 1/2 HOUR FIRE RESISTANCE AS AGREED WITH BUILDING CONTROL. ALL FIRE PROTECTION TO BE INSTALLED AS DETAILED BY SPECIALIST MANUFACTURER.
4. DOUBLE JOISTS/RAFTERS, TRIPLE JOISTS & TIMBER BEAMS (TB) BOLTED TOGETHER WITH M10 (8.8) BOLTS @ 400 STAGGERED CTRS. + 50Ø DOUBLE SIDED TOOTH CONNECTORS +50X50X5 WASHERS EACH SIDE.
5. INSERT DOUBLE-UP JOISTS UNDER BATHROOMS.
6. STEEL GRADE - S355
7. TIMBER GRADE - (C24)

STRAPPINNG NOTES:


1. STRAPPING OF FLOORS PROVIDE LATERAL RESTRAINT WHERE JOISTS RUN PARALLEL TO WALLS, FLOORS ARE TO BE STRAPPED TO WALLS WITH 1000MM X 30MM X 5MM GALVANISED MILD STEEL STRAPS OR OTHER APPROVED IN COMPLIANCE WITH BS EN 845-1 AT MAX 2.0M CENTRES, STRAPS TO BE TAKEN ACROSS MINIMUM OF 3 JOISTS. STRAPS TO BE BUILT INTO WALLS.
2. PROVIDE 38MM WIDE X ¾ DEPTH SOLID NOGGINS BETWEEN JOISTS AT STRAP POSITIONS. WHERE THE JOISTS SPAN OVER 2.5M, PROVIDE ONE ROW OF STRUTTING AT MID SPAN TO PREVENT JOISTS TWISTING + AT EACH END SUPPORTS.
3. STRAPPING FOR PITCHED ROOF ALL EXTERNAL WALLS SUPPORTING THE ROOF RAFTERS TO BE RESTRAINED AT ROOF LEVEL USING 1000MM X 30MM X 5MM GALVANISED MILD STEEL HORIZONTAL STRAPS (OR OTHER APPROVED TO BSEN 845-1) BUILT INTO WALLS AT MAX 2000MM CENTRES AND SCREW FIXED TO THE RAFTERS.
4. ALL WALL PLATES TO BE 100 X 50MM FIXED TO INNER SKIN OF CAVITY WALL USING 30MM X 5MM X 1000MM GALVANIZED METAL STRAPS OR OTHER APPROVED TO BSEN 845-1 AT MAXIMUM 1.5 CENTRES.
5. PROVIDE 30X5X1000MM GALVANISED MILD STEEL STRAPS FIXED OVER RIDGE BEAM TO RAFTERS AND JOISTS @ MAX. 0.8M CRS.

extension architecture

EXTENSION ARCHITECTURE & INTERIORS LTD
231 COBDEN HOUSE,
ROEHAMPTON LANE,
LONDON, SW15 4LB
TEL (0208) 288 8950
FAX (0871) 918 2798
www.extensionarchitecture.co.uk

THESE STRUCTURAL DRAWINGS HAVE BEEN PREPARED BY EXTENSION ARCHITECTURE WITH THE SOLE PURPOSE OF PROVIDING STRUCTURAL ENGINEERING SOLUTIONS. ANY QUESTIONS ABOUT STRUCTURAL COMPLIANCE SHOULD BE DIRECTED TO EXTENSION ARCHITECTURE OR THE LOCAL BUILDING CONTROL AUTHORITY. COLLABORATION WITH THE BUILDING CONTROL AUTHORITY FOR NECESSARY SITE INSPECTIONS AND APPROVALS IS COMPULSORY. WHILE THESE DRAWINGS ARE INTENDED FOR DISCUSSIONS WITH THE BUILDING CONTROL AUTHORITY, ON-SITE VERIFICATION BY THE BUILDER OR CONTRACTOR IS ESSENTIAL BEFORE CONSTRUCTION. THE BUILDER OR CONTRACTOR IS RESPONSIBLE FOR MAINTAINING RECORDS OF ANY DISCREPANCIES FOUND OR ON-SITE CHANGES THROUGHOUT CONSTRUCTION. CHARGES APPLY FOR EXTENSION ARCHITECTURE'S ON-SITE SUPERVISION, AND FEES APPLY FOR PROJECT MANAGER SERVICES IN CASE OF BUILDER ERRORS OR ISSUES. THE COPYRIGHT OF THE DRAWINGS AND DESIGNS REMAINS WITH EXTENSION ARCHITECTURE, REQUIRING EXPRESS WRITTEN PERMISSION FOR USAGE BEYOND THE APPLICATION.

DRAWN	CLIENT NAME: VIK BARODIA	DRAWING No.: A04
CHECKED	PROJECT NAME: 1 LAMBOURNE DRIVE	SCALE: 1:100 @A3
JOB NO.	TITLE: PROPOSED ROOF PLAN	DATE: 31-07-2024
REVISION: F		

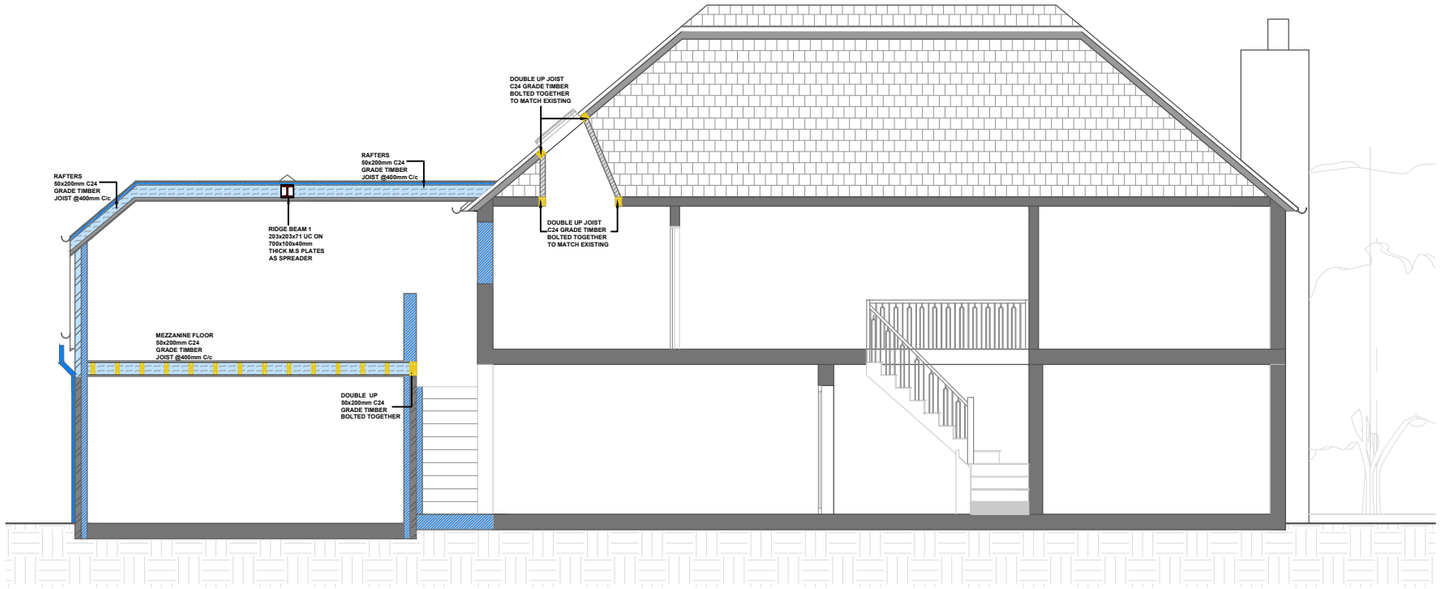

PROPOSED SECTION AA
SCALE 1:100

THE CONTRACTOR IS TO BE RESPONSIBLE FOR ALL TEMPORARY SUPPORT DURING THE EXECUTION OF THE WORKS, AND TO SUBMIT HIS OWN METHOD STATEMENT FOR THE TEMPORARY AND PERMANENT CONSTRUCTION.

GENERAL NOTES:

1. ALL STEEL DIMENSIONS CHECKED ON SITE PRIOR TO FABRICATION.
2. SUPPLY AND INSTALL ALL STRUCTURAL ELEMENTS SUCH AS BEAMS, ROOF STRUCTURE, FLOOR STRUCTURE, BEARINGS, AND PADSTONES IN ACCORDANCE WITH THE STRUCTURAL ENGINEER'S CALCULATIONS AND DETAILS.
3. NEW STEEL BEAMS TO BE ENCASED IN 12.5MM GYPROC FIRELINE BOARD WITH STAGGERED JOINTS, GYPROC FIRECASE OR PAINTED IN NULLIFIRE S OR SIMILAR INTUMESCENT PAINT TO PROVIDE 1/2 HOUR FIRE RESISTANCE AS AGREED WITH BUILDING CONTROL. ALL FIRE PROTECTION TO BE INSTALLED AS DETAILED BY SPECIALIST MANUFACTURER.
4. DOUBLE JOISTS/RAFTERS, TRIPLE JOISTS & TIMBER BEAMS (TB) BOLTED TOGETHER WITH M10 (8.8) BOLTS @ 400 STAGGERED CTRS. + 50Ø DOUBLE SIDED TOOTH CONNECTORS +50X50X5 WASHERS EACH SIDE.
5. INSERT DOUBLE-UP JOISTS UNDER BATHROOMS.
6. STEEL GRADE - S355
7. TIMBER GRADE - (C24)

STRAPPINNG NOTES:


1. STRAPPING OF FLOORS PROVIDE LATERAL RESTRAINT WHERE JOISTS RUN PARALLEL TO WALLS, FLOORS ARE TO BE STRAPPED TO WALLS WITH 1000MM X 30MM X 5MM GALVANISED MILD STEEL STRAPS OR OTHER APPROVED IN COMPLIANCE WITH BS EN 845-1 AT MAX 2.0M CENTRES, STRAPS TO BE TAKEN ACROSS MINIMUM OF 3 JOISTS. STRAPS TO BE BUILT INTO WALLS.
2. PROVIDE 38MM WIDE X ¾ DEPTH SOLID NOGGINS BETWEEN JOISTS AT STRAP POSITIONS. WHERE THE JOISTS SPAN OVER 2.5M, PROVIDE ONE ROW OF STRUTTING AT MID SPAN TO PREVENT JOISTS TWISTING + AT EACH END SUPPORTS.
3. STRAPPING FOR PITCHED ROOF ALL EXTERNAL WALLS SUPPORTING THE ROOF RAFTERS TO BE RESTRAINED AT ROOF LEVEL USING 1000MM X 30MM X 5MM GALVANISED MILD STEEL HORIZONTAL STRAPS (OR OTHER APPROVED TO BSEN 845-1) BUILT INTO WALLS AT MAX 2000MM CENTRES AND SCREW FIXED TO THE RAFTERS.
4. ALL WALL PLATES TO BE 100 X 50MM FIXED TO INNER SKIN OF CAVITY WALL USING 30MM X 5MM X 1000MM GALVANIZED METAL STRAPS OR OTHER APPROVED TO BSEN 845-1 AT MAXIMUM 1.5 CENTRES.
5. PROVIDE 30X5X1000MM GALVANISED MILD STEEL STRAPS FIXED OVER RIDGE BEAM TO RAFTERS AND JOISTS @ MAX. 0.8M CRS.

extension architecture

EXTENSION ARCHITECTURE & INTERIORS LTD
231 COBDEN HOUSE,
ROEHAMPTON LANE,
LONDON, SW15 4LB
TEL (0208) 288 8950
FAX (0871) 918 2798
www.extensionarchitecture.co.uk

THESE STRUCTURAL DRAWINGS HAVE BEEN PREPARED BY EXTENSION ARCHITECTURE WITH THE SOLE PURPOSE OF PROVIDING STRUCTURAL ENGINEERING SOLUTIONS. ANY QUESTIONS ABOUT STRUCTURAL COMPLIANCE SHOULD BE DIRECTED TO EXTENSION ARCHITECTURE OR THE LOCAL BUILDING CONTROL AUTHORITY. COLLABORATION WITH THE BUILDING CONTROL AUTHORITY FOR NECESSARY SITE INSPECTIONS AND APPROVALS IS COMPULSORY. WHILE THESE DRAWINGS ARE INTENDED FOR DISCUSSIONS WITH THE BUILDING CONTROL AUTHORITY, ON-SITE VERIFICATION BY THE BUILDER OR CONTRACTOR IS ESSENTIAL BEFORE CONSTRUCTION. THE BUILDER OR CONTRACTOR IS RESPONSIBLE FOR MAINTAINING RECORDS OF ANY DISCREPANCIES FOUND OR ON-SITE CHANGES THROUGHOUT CONSTRUCTION. CHARGES APPLY FOR EXTENSION ARCHITECTURE'S ON-SITE SUPERVISION, AND FEES APPLY FOR PROJECT MANAGER SERVICES IN CASE OF BUILDER ERRORS OR ISSUES. THE COPYRIGHT OF THE DRAWINGS AND DESIGNS REMAINS WITH EXTENSION ARCHITECTURE, REQUIRING EXPRESS WRITTEN PERMISSION FOR USAGE BEYOND THE APPLICATION.

DRAWN	CLIENT NAME: VIK BARODIA	DRAWING No.: A05	
CHECKED	PROJECT NAME: 1 LAMBOURNE DRIVE	SCALE: 1:100 @A3	
JOB NO.			
REVISION: F	TITLE: PROPOSED SECTION AA	DATE: 31-07-2024	

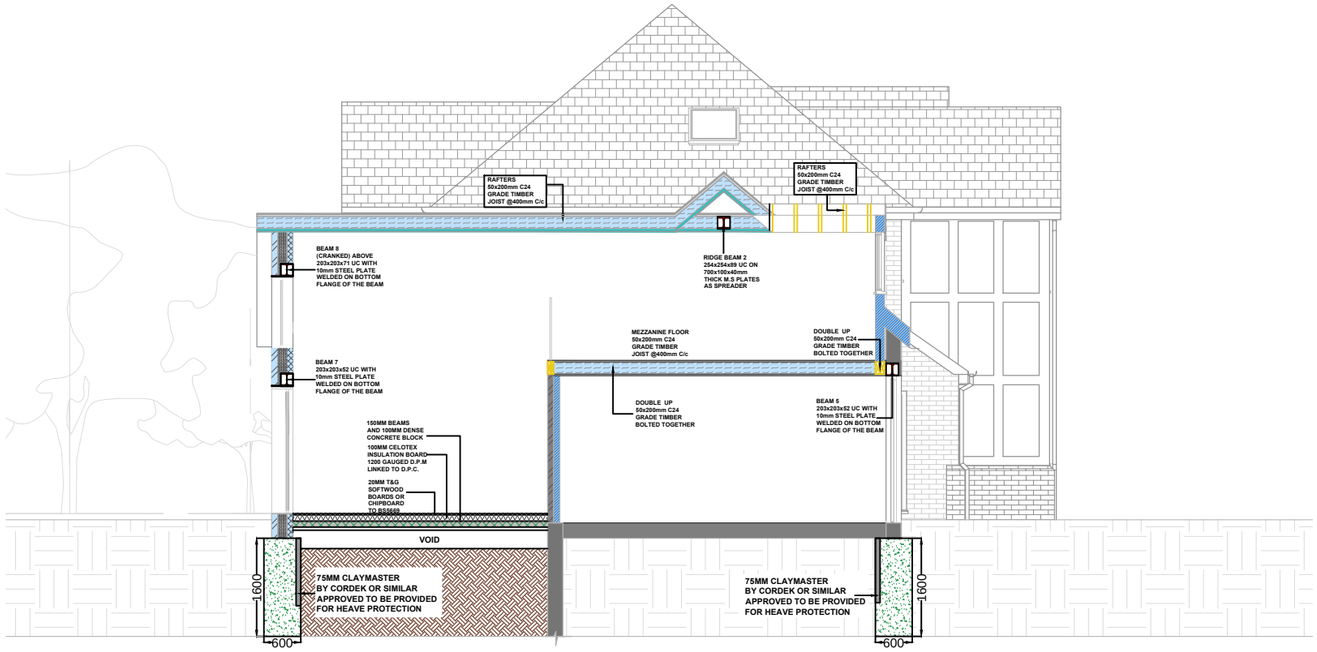

PROPOSED SECTION BB
SCALE 1:100

THE CONTRACTOR IS TO BE RESPONSIBLE FOR ALL TEMPORARY SUPPORT DURING THE EXECUTION OF THE WORKS, AND TO SUBMIT HIS OWN METHOD STATEMENT FOR THE TEMPORARY AND PERMANENT CONSTRUCTION.

GENERAL NOTES:

1. ALL STEEL DIMENSIONS CHECKED ON SITE PRIOR TO FABRICATION.
2. SUPPLY AND INSTALL ALL STRUCTURAL ELEMENTS SUCH AS BEAMS, ROOF STRUCTURE, FLOOR STRUCTURE, BEARINGS, AND PADSTONES IN ACCORDANCE WITH THE STRUCTURAL ENGINEER'S CALCULATIONS AND DETAILS.
3. NEW STEEL BEAMS TO BE ENCASED IN 12.5MM GYPROC FIRELINE BOARD WITH STAGGERED JOINTS, GYPROC FIRECASE OR PAINTED IN NULLIFIRE S OR SIMILAR INTUMESCENT PAINT TO PROVIDE 1/2 HOUR FIRE RESISTANCE AS AGREED WITH BUILDING CONTROL. ALL FIRE PROTECTION TO BE INSTALLED AS DETAILED BY SPECIALIST MANUFACTURER.
4. DOUBLE JOISTS/RAFTERS, TRIPLE JOISTS & TIMBER BEAMS (TB) BOLTED TOGETHER WITH M10 (8.8) BOLTS @ 400 STAGGERED CTRS. + 50Ø DOUBLE SIDED TOOTH CONNECTORS +50X50X5 WASHERS EACH SIDE.
5. INSERT DOUBLE-UP JOISTS UNDER BATHROOMS.
6. STEEL GRADE - S355
7. TIMBER GRADE - (C24)

STRAPPINNG NOTES:


1. STRAPPING OF FLOORS PROVIDE LATERAL RESTRAINT WHERE JOISTS RUN PARALLEL TO WALLS, FLOORS ARE TO BE STRAPPED TO WALLS WITH 1000MM X 30MM X 5MM GALVANISED MILD STEEL STRAPS OR OTHER APPROVED IN COMPLIANCE WITH BS EN 845-1 AT MAX 2.0M CENTRES, STRAPS TO BE TAKEN ACROSS MINIMUM OF 3 JOISTS. STRAPS TO BE BUILT INTO WALLS.
2. PROVIDE 38MM WIDE X ¾ DEPTH SOLID NOGGINS BETWEEN JOISTS AT STRAP POSITIONS. WHERE THE JOISTS SPAN OVER 2.5M, PROVIDE ONE ROW OF STRUTTING AT MID SPAN TO PREVENT JOISTS TWISTING + AT EACH END SUPPORTS.
3. STRAPPING FOR PITCHED ROOF ALL EXTERNAL WALLS SUPPORTING THE ROOF RAFTERS TO BE RESTRAINED AT ROOF LEVEL USING 1000MM X 30MM X 5MM GALVANISED MILD STEEL HORIZONTAL STRAPS (OR OTHER APPROVED TO BSEN 845-1) BUILT INTO WALLS AT MAX 2000MM CENTRES AND SCREW FIXED TO THE RAFTERS.
4. ALL WALL PLATES TO BE 100 X 50MM FIXED TO INNER SKIN OF CAVITY WALL USING 30MM X 5MM X 1000MM GALVANIZED METAL STRAPS OR OTHER APPROVED TO BSEN 845-1 AT MAXIMUM 1.5 CENTRES.
5. PROVIDE 30X5X1000MM GALVANISED MILD STEEL STRAPS FIXED OVER RIDGE BEAM TO RAFTERS AND JOISTS @ MAX. 0.8M CRS.

extension architecture


EXTENSION ARCHITECTURE & INTERIORS LTD
231 COBDEN HOUSE,
ROEHAMPTON LANE,
LONDON, SW15 4LB
TEL (0208) 288 8950
FAX (0871) 918 2798
www.extensionarchitecture.co.uk

THESE STRUCTURAL DRAWINGS HAVE BEEN PREPARED BY EXTENSION ARCHITECTURE WITH THE SOLE PURPOSE OF PROVIDING STRUCTURAL ENGINEERING SOLUTIONS. ANY QUESTIONS ABOUT STRUCTURAL COMPLIANCE SHOULD BE DIRECTED TO EXTENSION ARCHITECTURE OR THE LOCAL BUILDING CONTROL AUTHORITY. COLLABORATION WITH THE BUILDING CONTROL AUTHORITY FOR NECESSARY SITE INSPECTIONS AND APPROVALS IS COMPULSORY. WHILE THESE DRAWINGS ARE INTENDED FOR DISCUSSIONS WITH THE BUILDING CONTROL AUTHORITY, ON-SITE VERIFICATION BY THE BUILDER OR CONTRACTOR IS ESSENTIAL BEFORE CONSTRUCTION. THE BUILDER OR CONTRACTOR IS RESPONSIBLE FOR MAINTAINING RECORDS OF ANY DISCREPANCIES FOUND OR ON-SITE CHANGES THROUGHOUT CONSTRUCTION. CHARGES APPLY FOR EXTENSION ARCHITECTURE'S ON-SITE SUPERVISION, AND FEES APPLY FOR PROJECT MANAGER SERVICES IN CASE OF BUILDER ERRORS OR ISSUES. THE COPYRIGHT OF THE DRAWINGS AND DESIGNS REMAINS WITH EXTENSION ARCHITECTURE, REQUIRING EXPRESS WRITTEN PERMISSION FOR USAGE BEYOND THE APPLICATION.


DRAWN	CLIENT NAME: VIK BARODIA	DRAWING No.: A06
CHECKED	PROJECT NAME: 1 LAMBOURNE DRIVE	SCALE: 1:100 @A3
JOB NO.	TITLE: PROPOSED SECTION BB	DATE: 31-07-2024
REVISION: F		

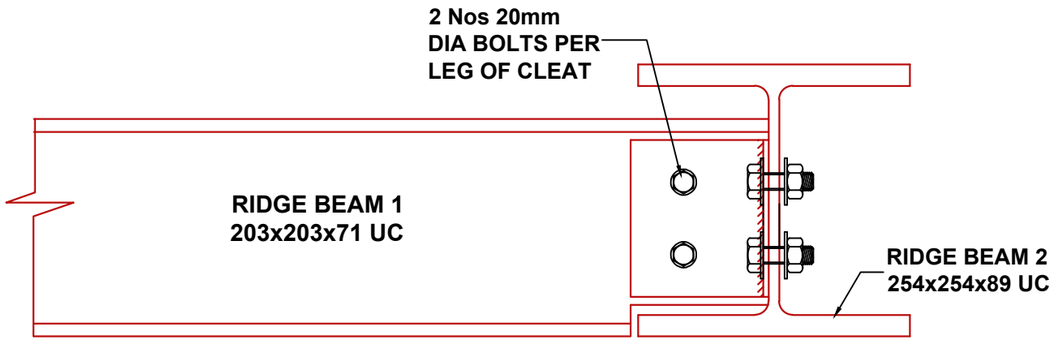


BEAM / BEAM CONNECTION

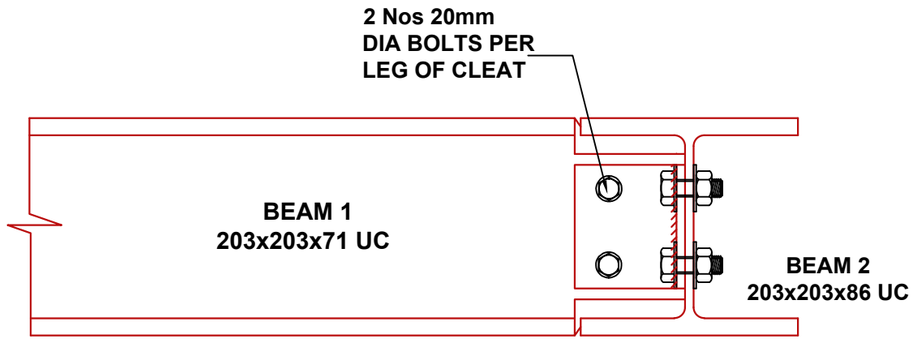

BEAM / BEAM CONNECTION

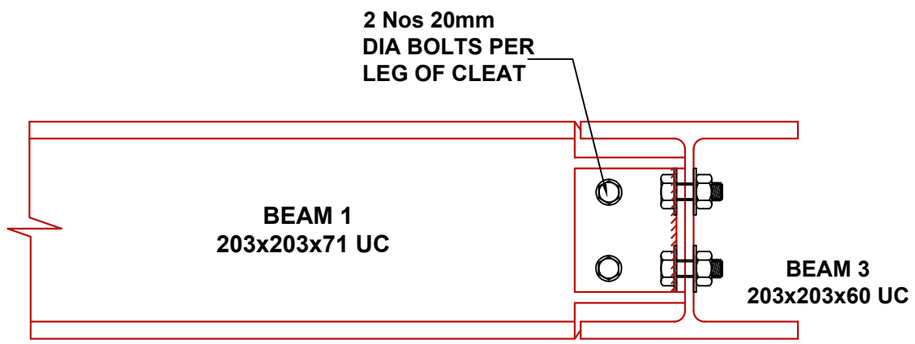

BEAM / BEAM CONNECTION

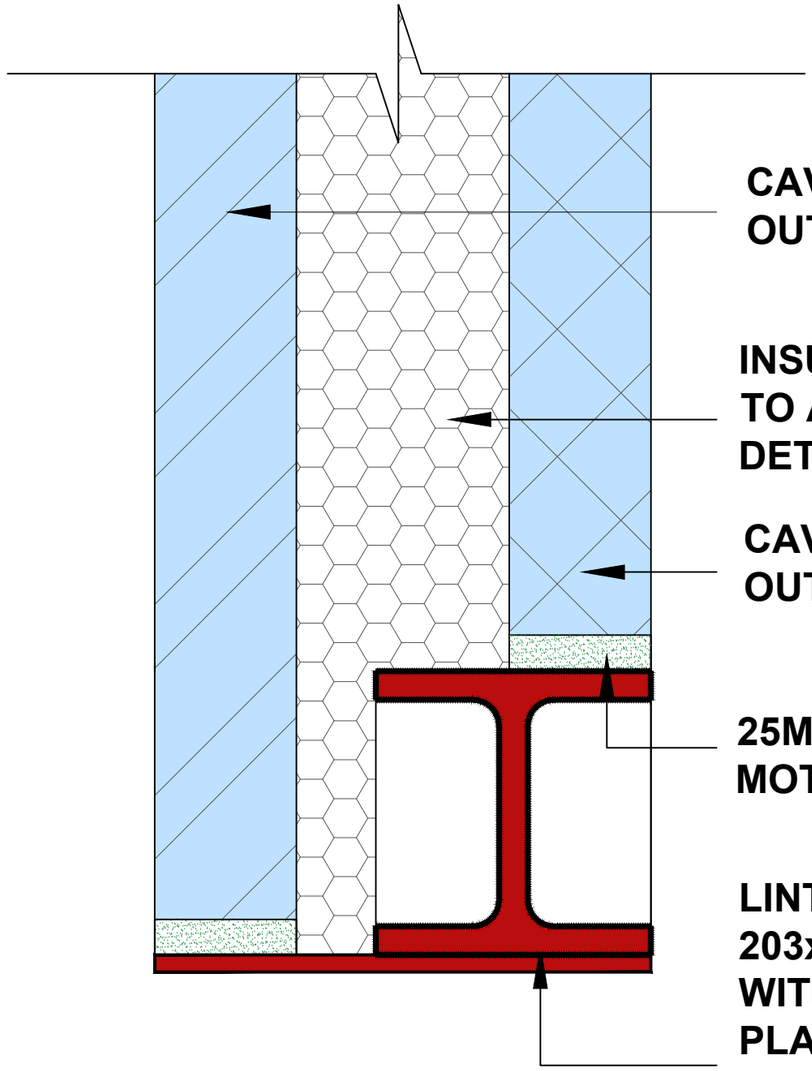


LINTEL BEAM DETAILS

extension architecture

EXTENSION ARCHITECTURE & INTERIORS LTD
231 COBDEN HOUSE,
ROEHAMPTON LANE,
LONDON, SW15 4LB
TEL (0208) 288 8950
FAX (0871) 918 2798
www.extensionarchitecture.co.uk

THESE STRUCTURAL DRAWINGS HAVE BEEN PREPARED BY EXTENSION ARCHITECTURE WITH THE SOLE PURPOSE OF PROVIDING STRUCTURAL ENGINEERING SOLUTIONS. ANY QUESTIONS ABOUT STRUCTURAL COMPLIANCE SHOULD BE DIRECTED TO EXTENSION ARCHITECTURE OR THE LOCAL BUILDING CONTROL AUTHORITY. COLLABORATION WITH THE BUILDING CONTROL AUTHORITY FOR NECESSARY SITE INSPECTIONS AND APPROVALS IS COMPULSORY. WHILE THESE DRAWINGS ARE INTENDED FOR DISCUSSIONS WITH THE BUILDING CONTROL AUTHORITY, ON-SITE VERIFICATION BY THE BUILDER OR CONTRACTOR IS ESSENTIAL BEFORE CONSTRUCTION. THE BUILDER OR CONTRACTOR IS RESPONSIBLE FOR MAINTAINING RECORDS OF ANY DISCREPANCIES FOUND OR ON-SITE CHANGES THROUGHOUT CONSTRUCTION. CHARGES APPLY FOR EXTENSION ARCHITECTURE'S ON-SITE SUPERVISION, AND FEES APPLY FOR PROJECT MANAGER SERVICES IN CASE OF BUILDER ERRORS OR ISSUES. THE COPYRIGHT OF THE DRAWINGS AND DESIGNS REMAINS WITH EXTENSION ARCHITECTURE, REQUIRING EXPRESS WRITTEN PERMISSION FOR USAGE BEYOND THE APPLICATION.

DRAWN	CLIENT NAME: VIK BARODIA	DRAWING No.: A07
CHECKED	PROJECT NAME: 1 LAMBOURNE DRIVE	SCALE: NTS @A3
JOB NO.	TITLE: CONNECTIONS DETAILS	DATE: 31-07-2024
REVISION: F		

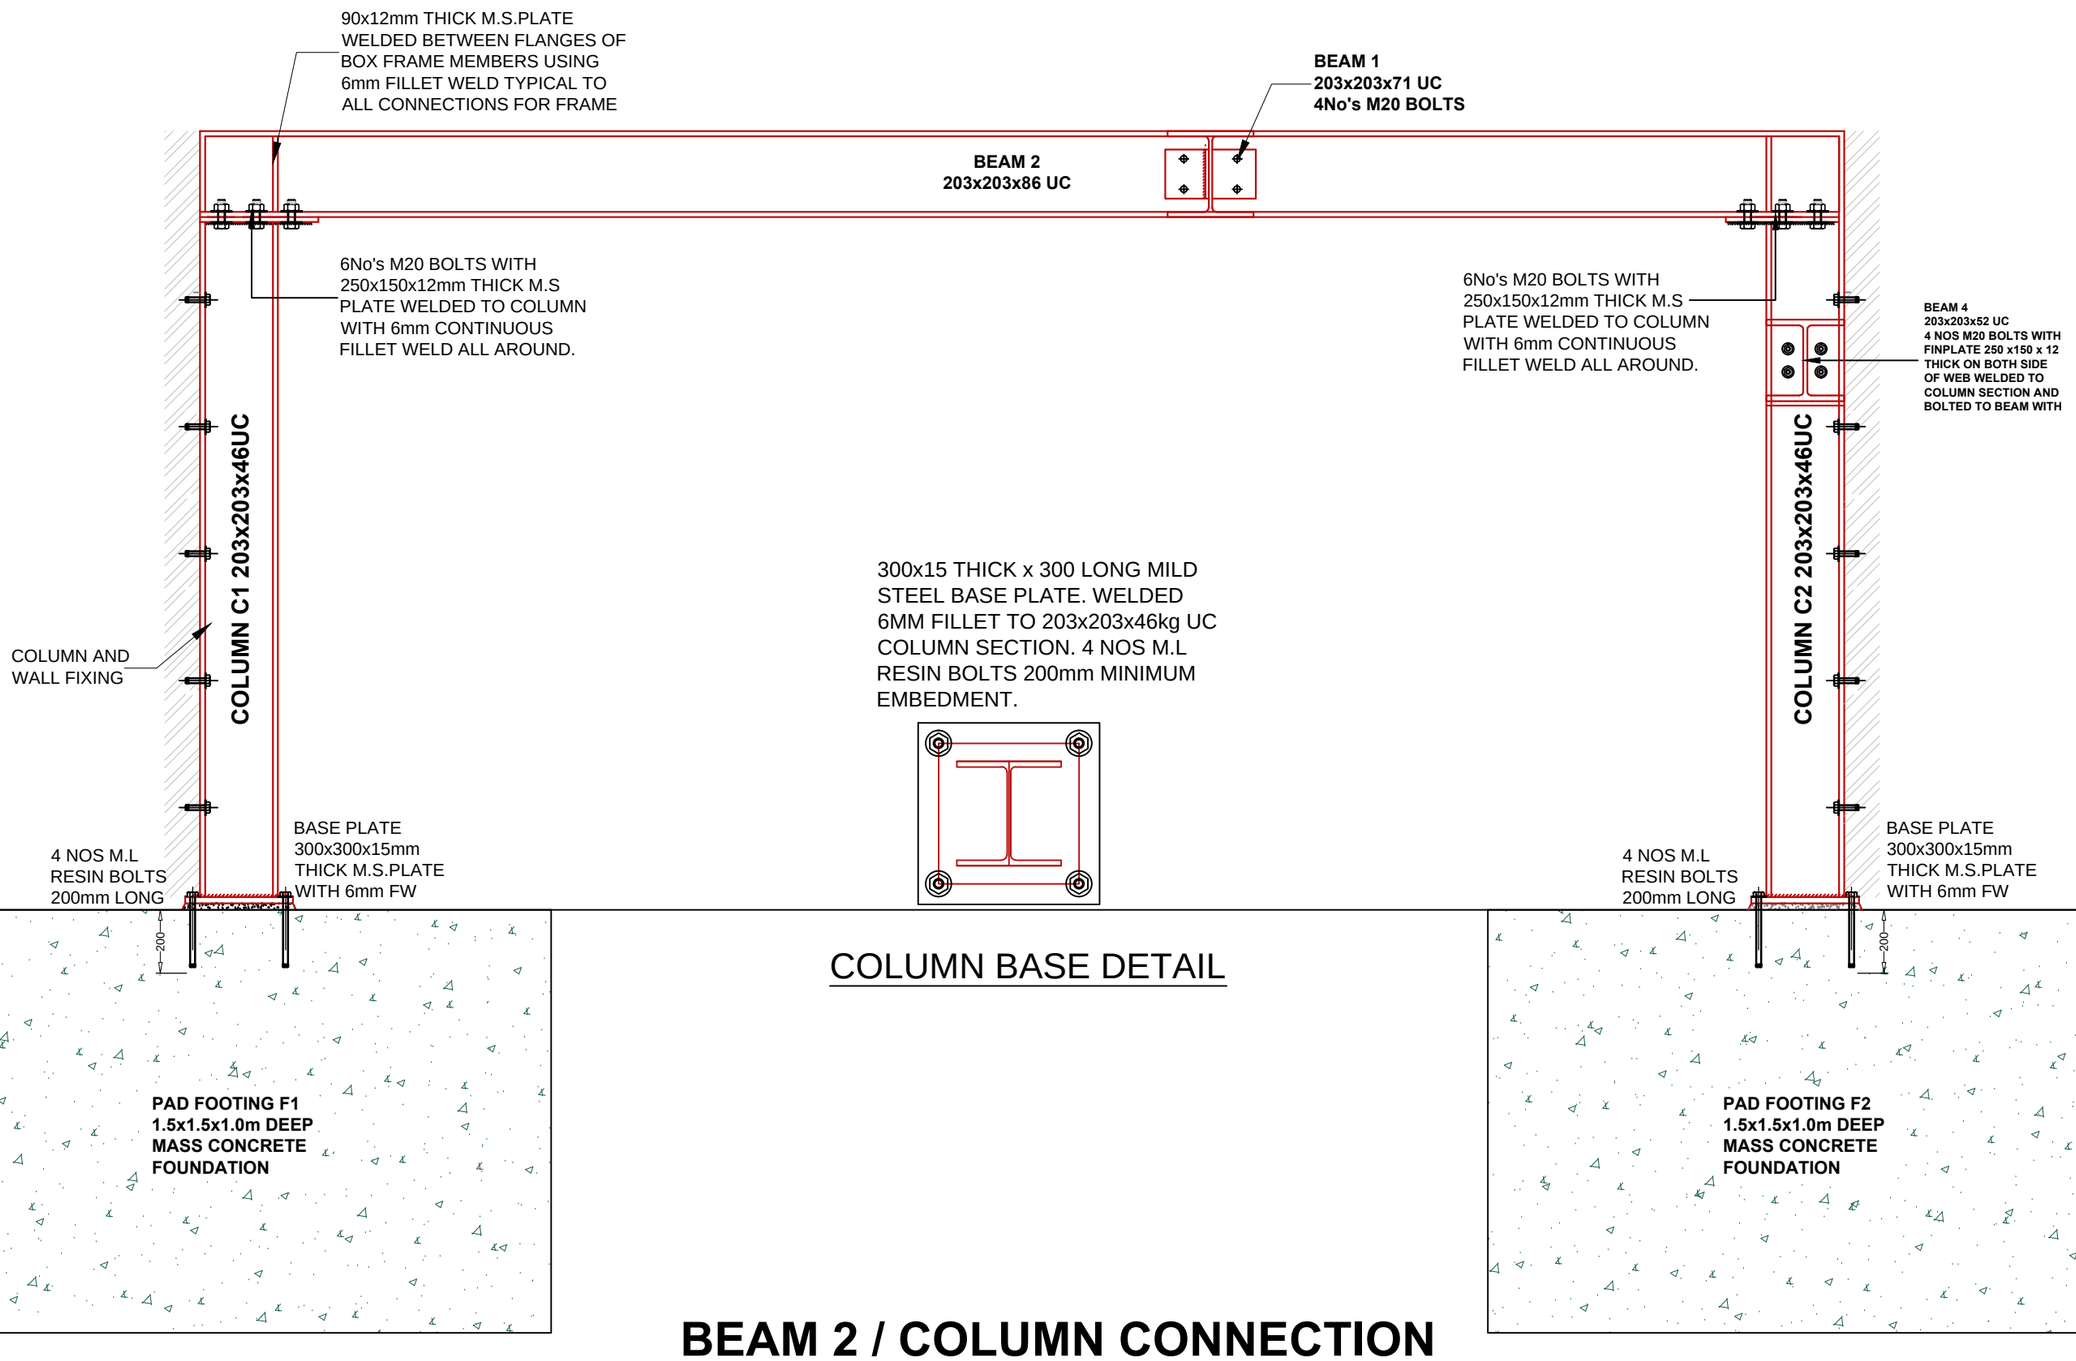

COLUMN BASE DETAIL


BEAM 2 / COLUMN CONNECTION


extension architecture

EXTENSION ARCHITECTURE & INTERIORS LTD
231 COBDEN HOUSE,
ROEHAMPTON LANE,
LONDON, SW15 4LB
TEL (0208) 288 8950
FAX (0871) 918 2798
www.extensionarchitecture.co.uk

THESE STRUCTURAL DRAWINGS HAVE BEEN PREPARED BY EXTENSION ARCHITECTURE WITH THE SOLE PURPOSE OF PROVIDING STRUCTURAL ENGINEERING SOLUTIONS. ANY QUESTIONS ABOUT STRUCTURAL COMPLIANCE SHOULD BE DIRECTED TO EXTENSION ARCHITECTURE OR THE LOCAL BUILDING CONTROL AUTHORITY. COLLABORATION WITH THE BUILDING CONTROL AUTHORITY FOR NECESSARY SITE INSPECTIONS AND APPROVALS IS COMPULSORY. WHILE THESE DRAWINGS ARE INTENDED FOR DISCUSSIONS WITH THE BUILDING CONTROL AUTHORITY, ON-SITE VERIFICATION BY THE BUILDER OR CONTRACTOR IS ESSENTIAL BEFORE CONSTRUCTION. THE BUILDER OR CONTRACTOR IS RESPONSIBLE FOR MAINTAINING RECORDS OF ANY DISCREPANCIES FOUND OR ON-SITE CHANGES THROUGHOUT CONSTRUCTION. CHARGES APPLY FOR EXTENSION ARCHITECTURE'S ON-SITE SUPERVISION, AND FEES APPLY FOR PROJECT MANAGER SERVICES IN CASE OF BUILDER ERRORS OR ISSUES. THE COPYRIGHT OF THE DRAWINGS AND DESIGNS REMAINS WITH EXTENSION ARCHITECTURE, REQUIRING EXPRESS WRITTEN PERMISSION FOR USAGE BEYOND THE APPLICATION.


DRAWN	CLIENT NAME: VIK BARODIA		DRAWING No.: A08
CHECKED	PROJECT NAME: 1 LAMBOURNE DRIVE		SCALE: NTS @A3
JOB NO.	TITLE: CONNECTIONS DETAILS		DATE: 31-07-2024
REVISION: F			

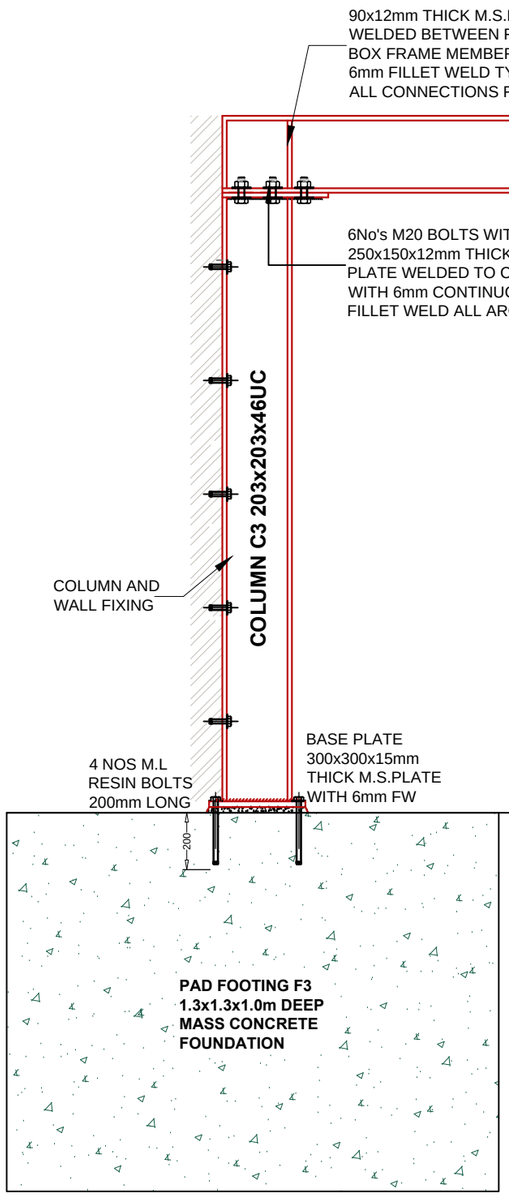


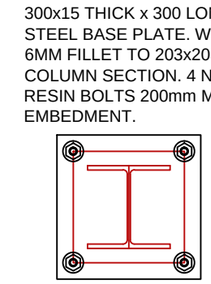

COLUMN BASE DETAIL


300x15 THICK x 300 LONG MILD STEEL BASE PLATE. WELDED 6MM FILLET TO 203x203x46kg UC COLUMN SECTION. 4 NOS M.L RESIN BOLTS 200mm MINIMUM EMBEDMENT.

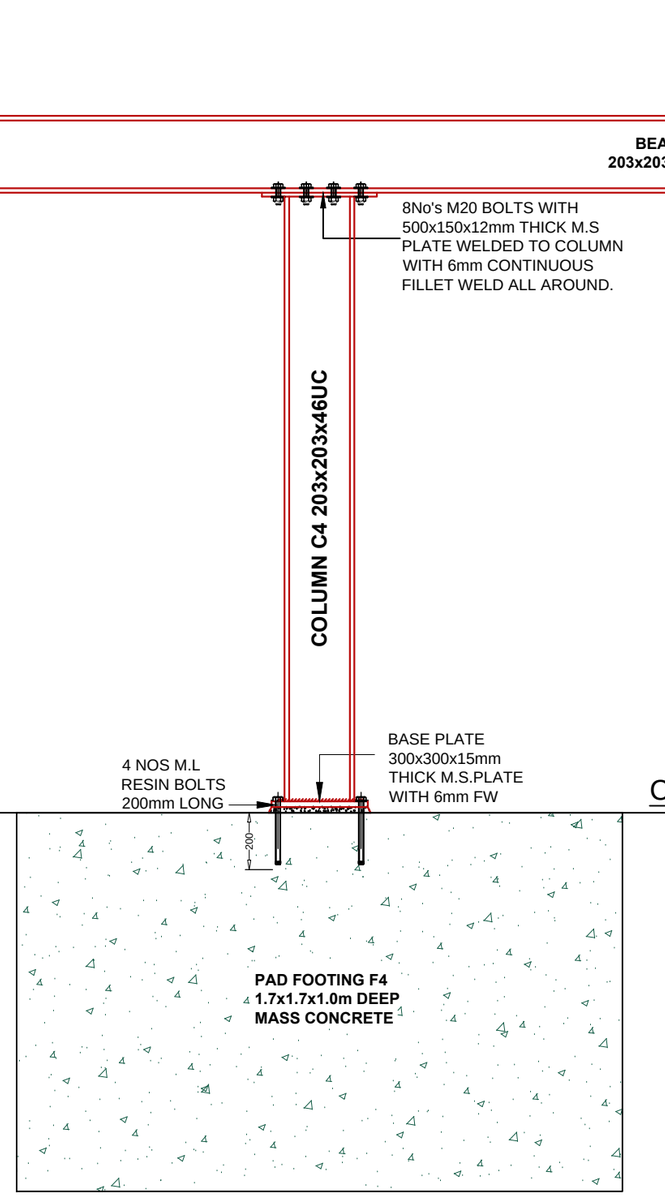

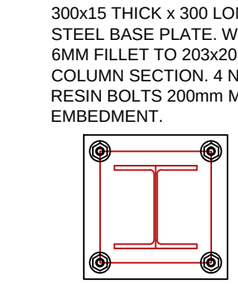

COLUMN BASE DETAIL

300x15 THICK x 300 LONG MILD STEEL BASE PLATE. WELDED 6MM FILLET TO 203x203x46kg UC COLUMN SECTION. 4 NOS M.L RESIN BOLTS 200mm MINIMUM EMBEDMENT.

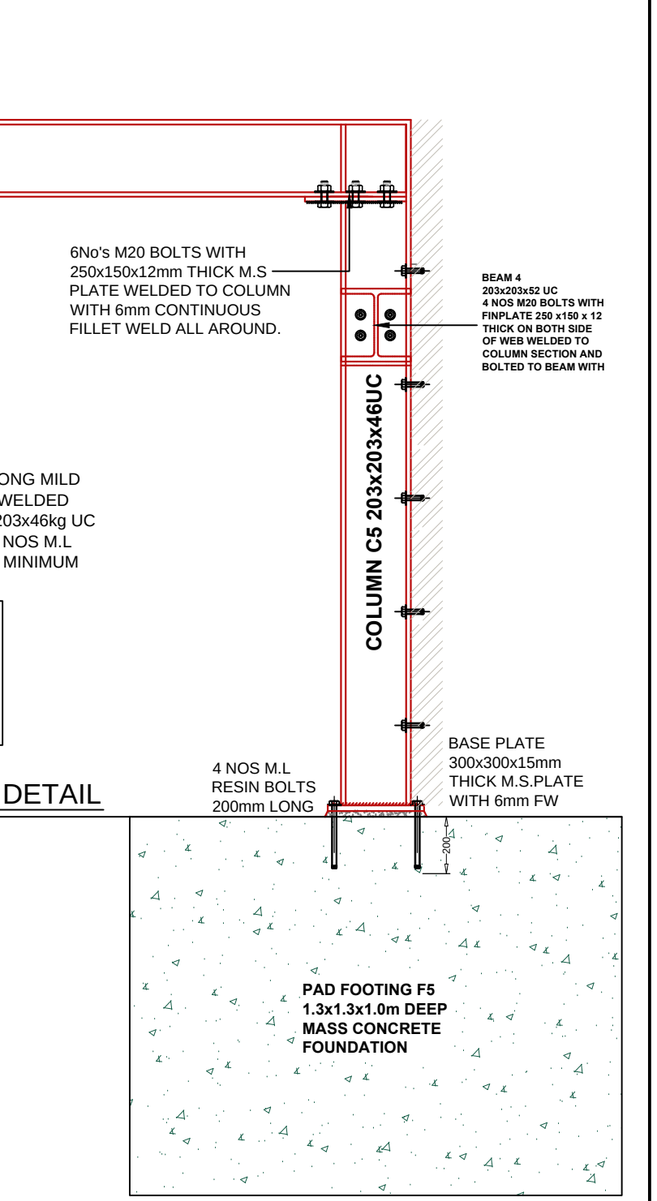


BEAM 3 / COLUMN CONNECTION

extension architecture

EXTENSION ARCHITECTURE & INTERIORS LTD
231 COBDEN HOUSE,
ROEHAMPTON LANE,
LONDON, SW15 4LB
TEL (0208) 288 8950
FAX (0871) 918 2798
www.extensionarchitecture.co.uk

THESE STRUCTURAL DRAWINGS HAVE BEEN PREPARED BY EXTENSION ARCHITECTURE WITH THE SOLE PURPOSE OF PROVIDING STRUCTURAL ENGINEERING SOLUTIONS. ANY QUESTIONS ABOUT STRUCTURAL COMPLIANCE SHOULD BE DIRECTED TO EXTENSION ARCHITECTURE OR THE LOCAL BUILDING CONTROL AUTHORITY. COLLABORATION WITH THE BUILDING CONTROL AUTHORITY FOR NECESSARY SITE INSPECTIONS AND APPROVALS IS COMPULSORY. WHILE THESE DRAWINGS ARE INTENDED FOR DISCUSSIONS WITH THE BUILDING CONTROL AUTHORITY, ON-SITE VERIFICATION BY THE BUILDER OR CONTRACTOR IS ESSENTIAL BEFORE CONSTRUCTION. THE BUILDER OR CONTRACTOR IS RESPONSIBLE FOR MAINTAINING RECORDS OF ANY DISCREPANCIES FOUND OR ON-SITE CHANGES THROUGHOUT CONSTRUCTION. CHARGES APPLY FOR EXTENSION ARCHITECTURE'S ON-SITE SUPERVISION, AND FEES APPLY FOR PROJECT MANAGER SERVICES IN CASE OF BUILDER ERRORS OR ISSUES. THE COPYRIGHT OF THE DRAWINGS AND DESIGNS REMAINS WITH EXTENSION ARCHITECTURE, REQUIRING EXPRESS WRITTEN PERMISSION FOR USAGE BEYOND THE APPLICATION.

DRAWN	CLIENT NAME: VIK BARODIA	DRAWING No.: A09
CHECKED	PROJECT NAME: 1 LAMBOURNE DRIVE	SCALE: NTS @A3
JOB NO.	TITLE: CONNECTIONS DETAILS	DATE: 31-07-2024
REVISION: F		

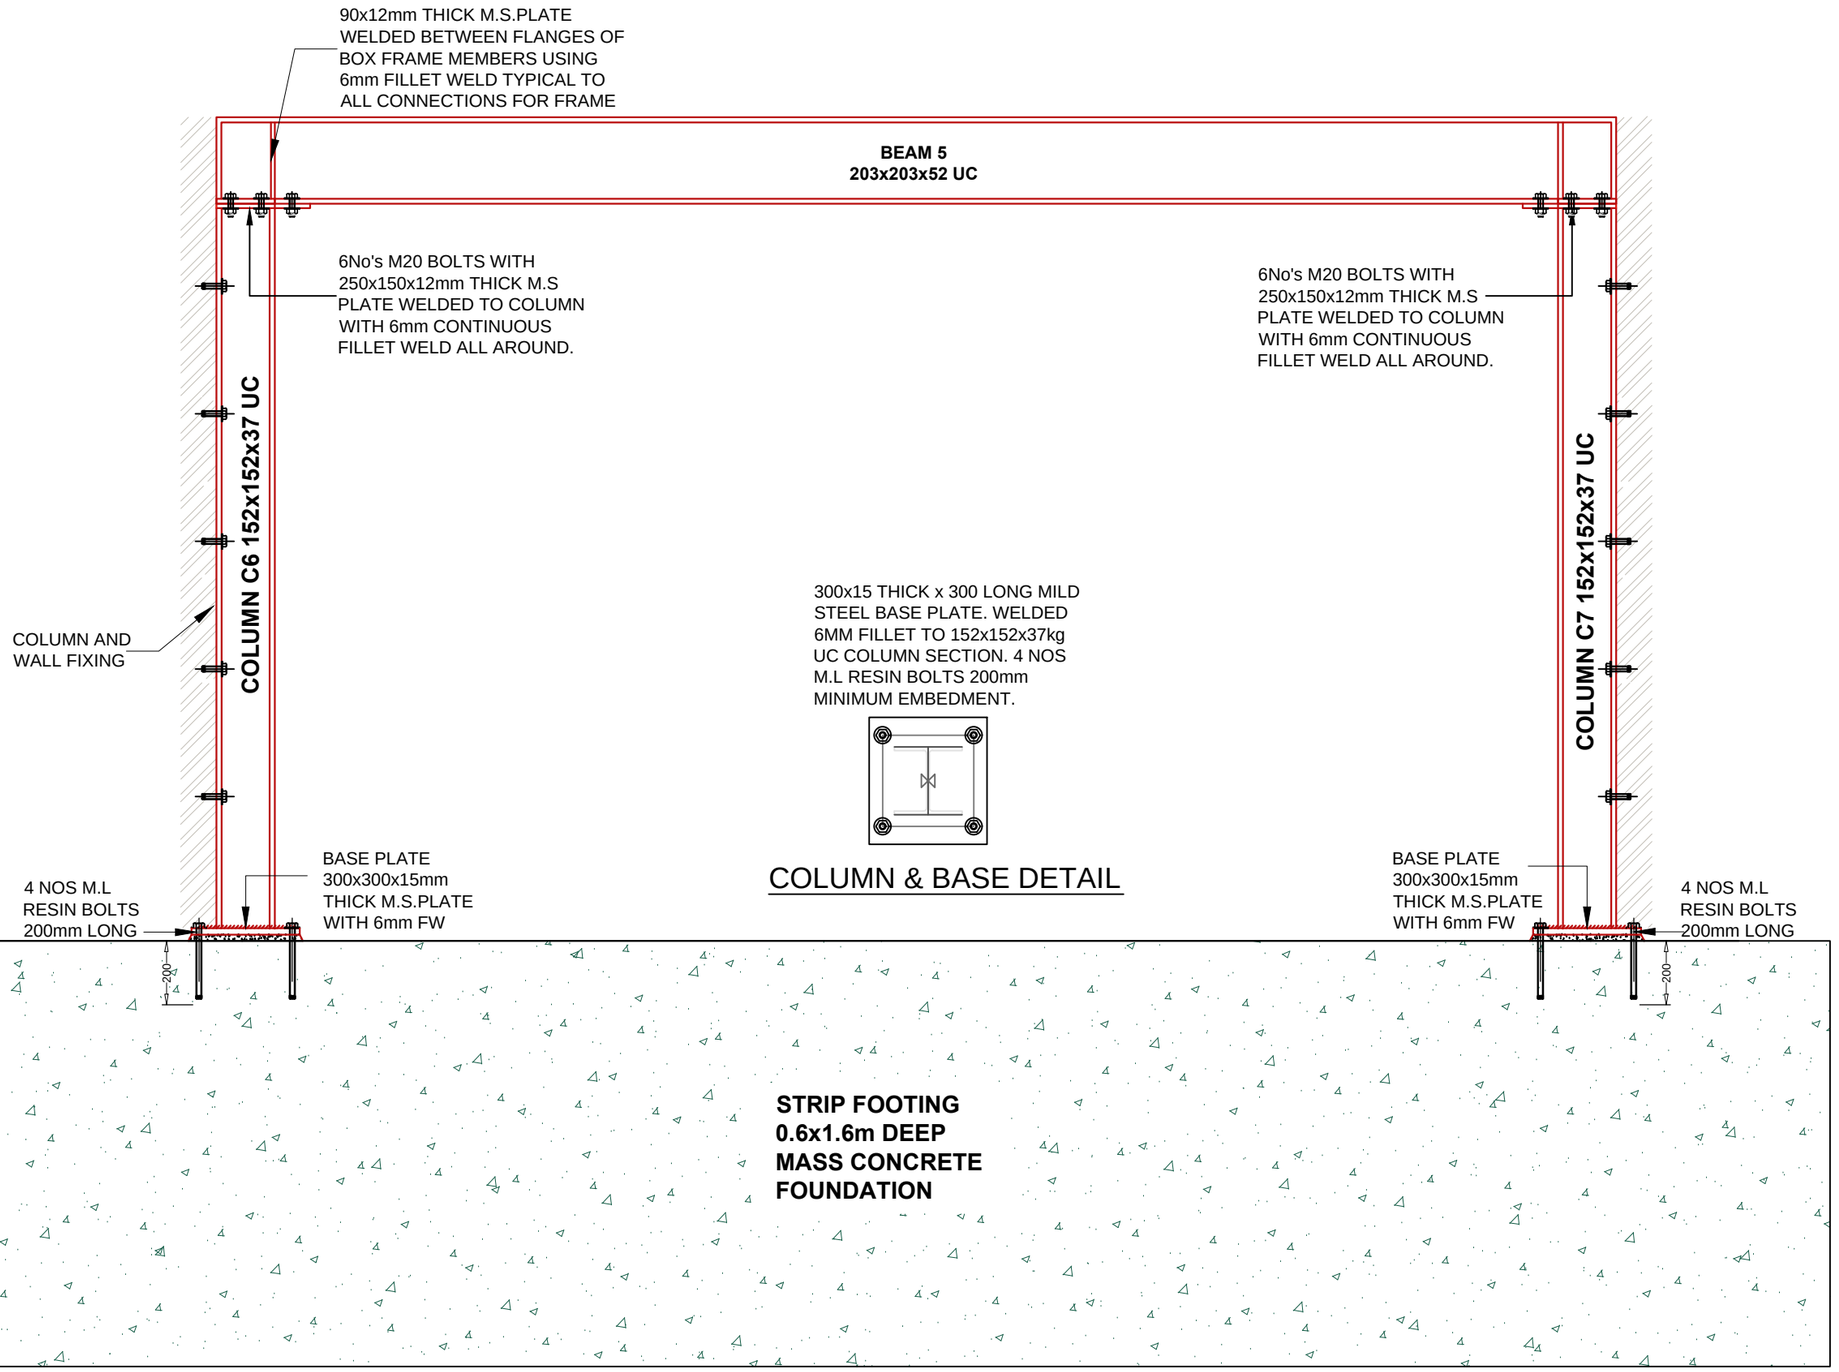

COLUMN & BASE DETAIL


BEAM 5 / COLUMN CONNECTION

extension architecture


EXTENSION ARCHITECTURE & INTERIORS LTD
231 COBDEN HOUSE,
ROEHAMPTON LANE,
LONDON, SW15 4LB
TEL (0208) 288 8950
FAX (0871) 918 2798
www.extensionarchitecture.co.uk

THESE STRUCTURAL DRAWINGS HAVE BEEN PREPARED BY EXTENSION ARCHITECTURE WITH THE SOLE PURPOSE OF PROVIDING STRUCTURAL ENGINEERING SOLUTIONS. ANY QUESTIONS ABOUT STRUCTURAL COMPLIANCE SHOULD BE DIRECTED TO EXTENSION ARCHITECTURE OR THE LOCAL BUILDING CONTROL AUTHORITY. COLLABORATION WITH THE BUILDING CONTROL AUTHORITY FOR NECESSARY SITE INSPECTIONS AND APPROVALS IS COMPULSORY. WHILE THESE DRAWINGS ARE INTENDED FOR DISCUSSIONS WITH THE BUILDING CONTROL AUTHORITY, ON-SITE VERIFICATION BY THE BUILDER OR CONTRACTOR IS ESSENTIAL BEFORE CONSTRUCTION. THE BUILDER OR CONTRACTOR IS RESPONSIBLE FOR MAINTAINING RECORDS OF any DISCREPANCIES FOUND OR ON-SITE CHANGES THROUGHOUT CONSTRUCTION. CHARGES APPLY FOR EXTENSION ARCHITECTURE'S ON-SITE SUPERVISION, AND FEES APPLY FOR PROJECT MANAGER SERVICES IN CASE OF BUILDER ERRORS OR ISSUES. THE COPYRIGHT OF THE DRAWINGS AND DESIGNS REMAINS WITH EXTENSION ARCHITECTURE, REQUIRING EXPRESS WRITTEN PERMISSION FOR USAGE BEYOND THE APPLICATION.

DRAWN	CLIENT NAME: VIK BARODIA	DRAWING No.: A10
CHECKED	PROJECT NAME: 1 LAMBOURNE DRIVE	SCALE: NTS @A3
JOB NO.	TITLE: CONNECTIONS DETAILS	DATE: 31-07-2024
REVISION: F		

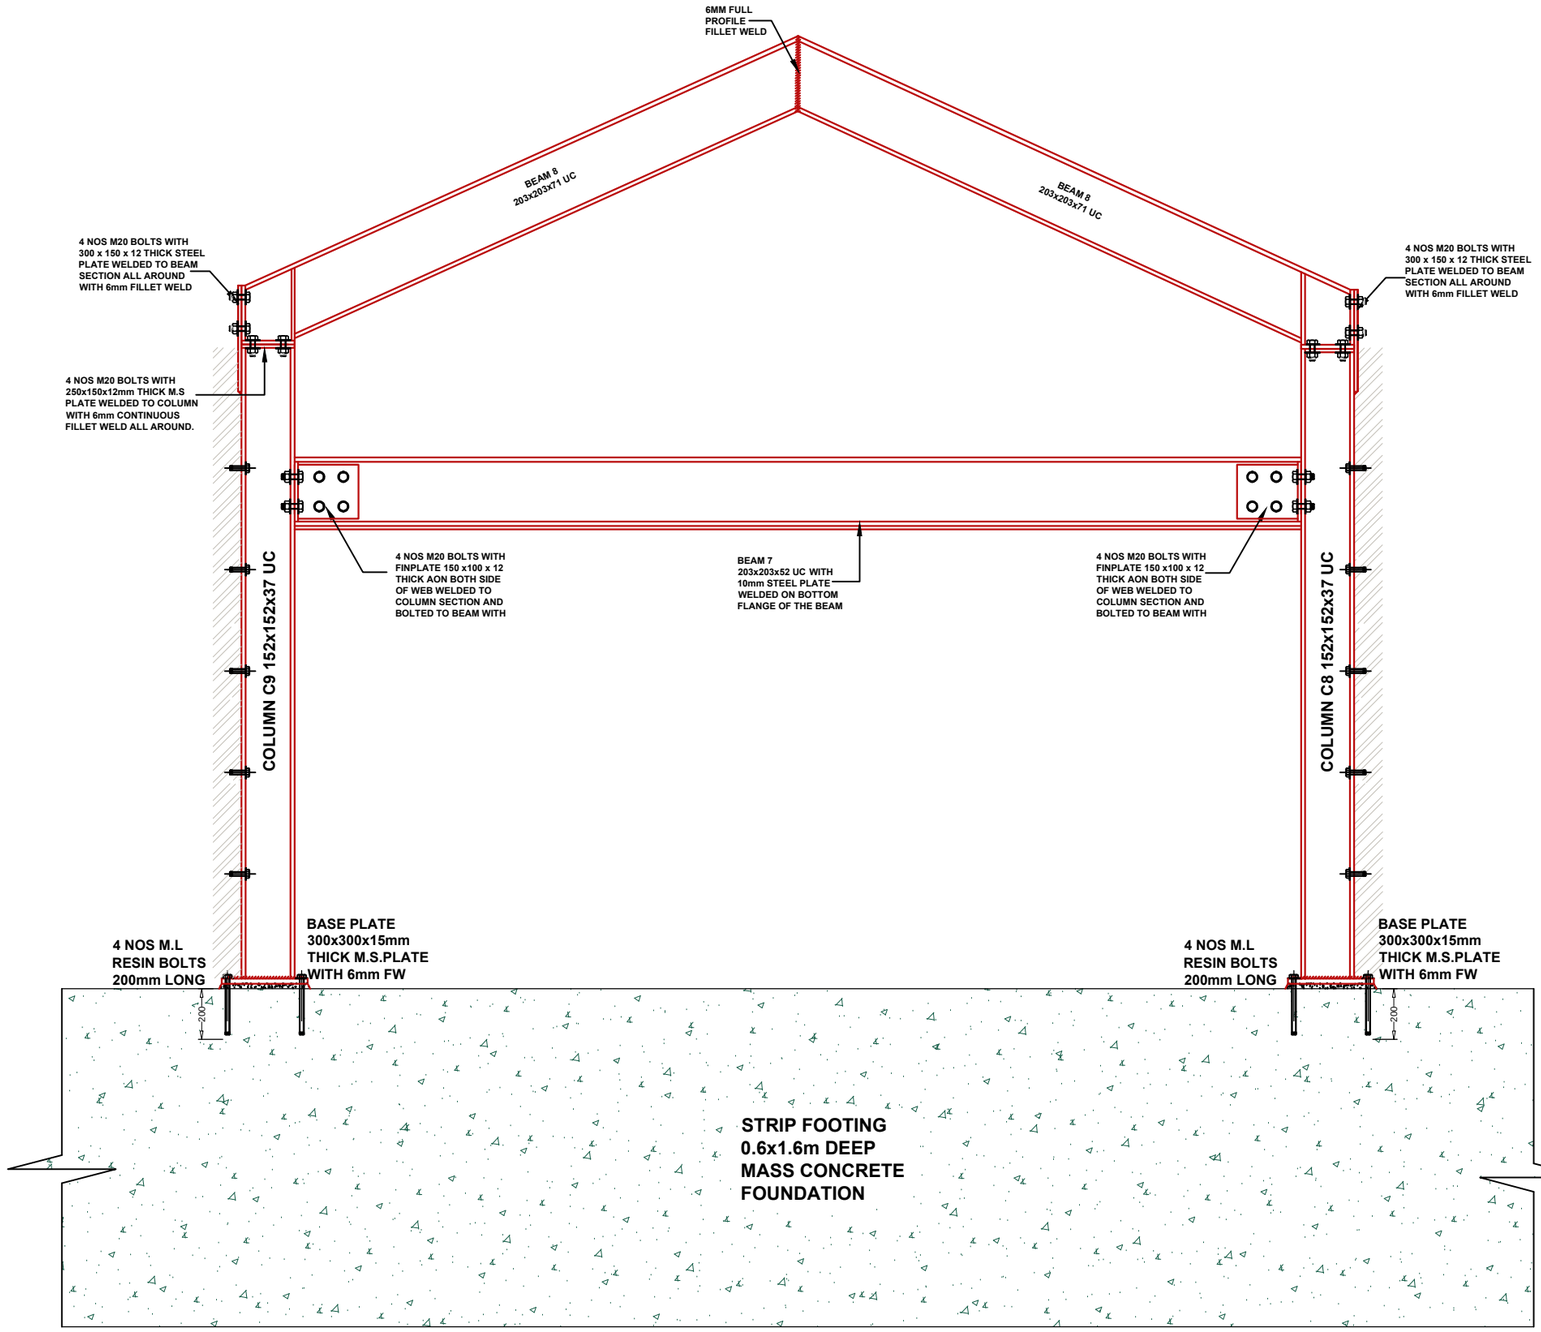

300x15 THICK x 300 LONG MILD STEEL BASE PLATE. WELDED 6MM FILLET TO 152x152x37kg UC COLUMN SECTION. 4 NOS M.L RESIN BOLTS 200mm MINIMUM EMBEDMENT.

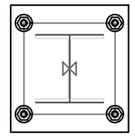

COLUMN & BASE DETAIL


CRANKED BEAM TO COLUMN CONNECTIONS

extension architecture

EXTENSION ARCHITECTURE & INTERIORS LTD
231 COBDEN HOUSE,
ROEHAMPTON LANE,
LONDON, SW15 4LB
TEL (0208) 288 8950
FAX (0871) 918 2798
www.extensionarchitecture.co.uk

THESE STRUCTURAL DRAWINGS HAVE BEEN PREPARED BY EXTENSION ARCHITECTURE WITH THE SOLE PURPOSE OF PROVIDING STRUCTURAL ENGINEERING SOLUTIONS. ANY QUESTIONS ABOUT STRUCTURAL COMPLIANCE SHOULD BE DIRECTED TO EXTENSION ARCHITECTURE OR THE LOCAL BUILDING CONTROL AUTHORITY. COLLABORATION WITH THE BUILDING CONTROL AUTHORITY FOR NECESSARY SITE INSPECTIONS AND APPROVALS IS COMPULSORY. WHILE THESE DRAWINGS ARE INTENDED FOR DISCUSSIONS WITH THE BUILDING CONTROL AUTHORITY, ON-SITE VERIFICATION BY THE BUILDER OR CONTRACTOR IS ESSENTIAL BEFORE CONSTRUCTION. THE BUILDER OR CONTRACTOR IS RESPONSIBLE FOR MAINTAINING RECORDS OF ANY DISCREPANCIES FOUND OR ON-SITE CHANGES THROUGHOUT CONSTRUCTION. CHARGES APPLY FOR EXTENSION ARCHITECTURE'S ON-SITE SUPERVISION, AND FEES APPLY FOR PROJECT MANAGER SERVICES IN CASE OF BUILDER ERRORS OR ISSUES. THE COPYRIGHT OF THE DRAWINGS AND DESIGNS REMAINS WITH EXTENSION ARCHITECTURE, REQUIRING EXPRESS WRITTEN PERMISSION FOR USAGE BEYOND THE APPLICATION.

DRAWN	CLIENT NAME: VIK BARODIA	DRAWING No.: A11
CHECKED	PROJECT NAME: 1 LAMBOURNE DRIVE	SCALE: NTS @A3
JOB NO.	TITLE: CONNECTIONS DETAILS	DATE: 31-07-2024
REVISION: F		

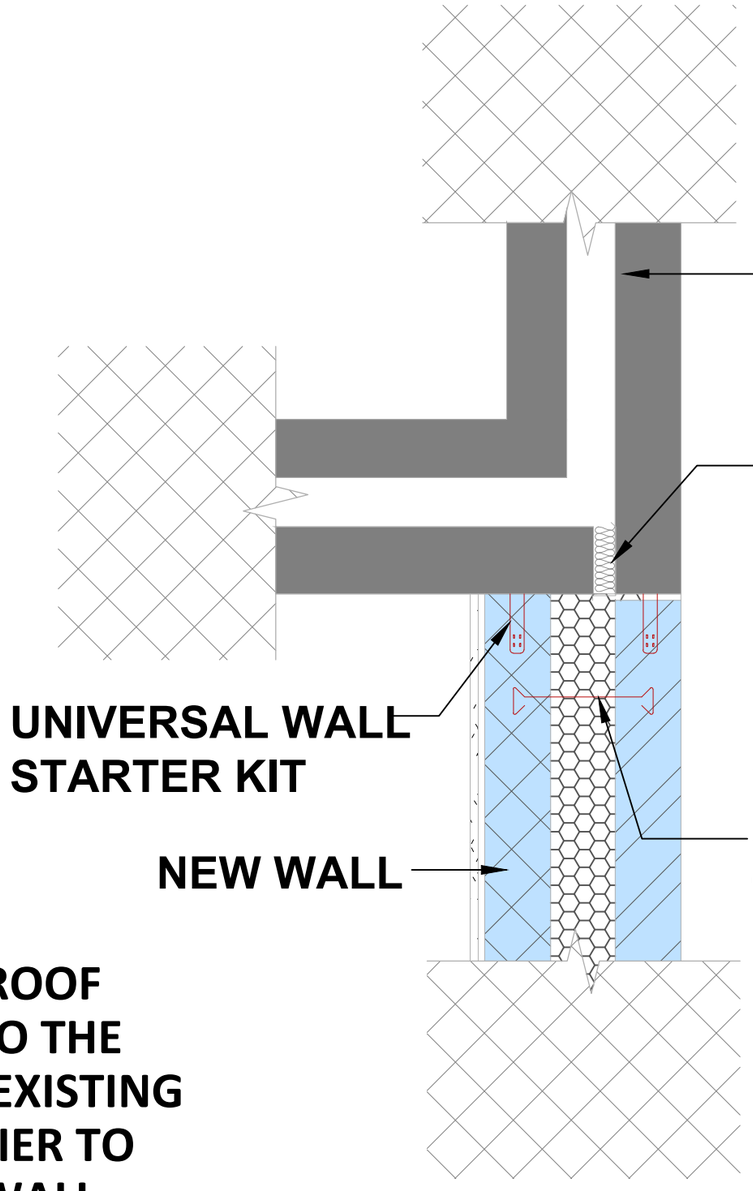

PREFORMED VERTICAL DAMP PROOF COURSE (DPC) FOR INSERTION INTO THE EXTERNAL MASONRY LEAF OF AN EXISTING CAVITY WALL TO PROVIDE A BARRIER TO MOISTURE WHERE THE EXISTING WALL BECOMES AN INTERNAL WALL.


METHOD OF BONDING TO STRUCTURAL ENGINEERS DESIGN

extension architecture


EXTENSION ARCHITECTURE & INTERIORS LTD
231 COBDEN HOUSE,
ROEHAMPTON LANE,
LONDON, SW15 4LB
TEL (0208) 288 8950
FAX (0871) 918 2798
www.extensionarchitecture.co.uk

THESE STRUCTURAL DRAWINGS HAVE BEEN PREPARED BY EXTENSION ARCHITECTURE WITH THE SOLE PURPOSE OF PROVIDING STRUCTURAL ENGINEERING SOLUTIONS. ANY QUESTIONS ABOUT STRUCTURAL COMPLIANCE SHOULD BE DIRECTED TO EXTENSION ARCHITECTURE OR THE LOCAL BUILDING CONTROL AUTHORITY. COLLABORATION WITH THE BUILDING CONTROL AUTHORITY FOR NECESSARY SITE INSPECTIONS AND APPROVALS IS COMPULSORY. WHILE THESE DRAWINGS ARE INTENDED FOR DISCUSSIONS WITH THE BUILDING CONTROL AUTHORITY, ON-SITE VERIFICATION BY THE BUILDER OR CONTRACTOR IS ESSENTIAL BEFORE CONSTRUCTION. THE BUILDER OR CONTRACTOR IS RESPONSIBLE FOR MAINTAINING RECORDS OF ANY DISCREPANCIES FOUND OR ON-SITE CHANGES THROUGHOUT CONSTRUCTION. CHARGES APPLY FOR EXTENSION ARCHITECTURE'S ON-SITE SUPERVISION, AND FEES APPLY FOR PROJECT MANAGER SERVICES IN CASE OF BUILDER ERRORS OR ISSUES. THE COPYRIGHT OF THE DRAWINGS AND DESIGNS REMAINS WITH EXTENSION ARCHITECTURE, REQUIRING EXPRESS WRITTEN PERMISSION FOR USAGE BEYOND THE APPLICATION.


DRAWN	CLIENT NAME: VIK BARODIA	DRAWING No.: A12
CHECKED	PROJECT NAME: 1 LAMBOURNE DRIVE	SCALE: NTS @A3
JOB NO.	TITLE: STRAPPING DETAILS	DATE: 31-07-2024
REVISION: F		

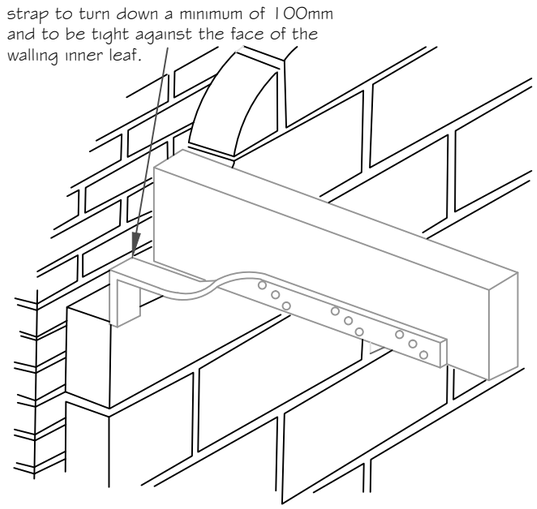


TYING OF TIMBER FLOOR BEARING ON TO WALL

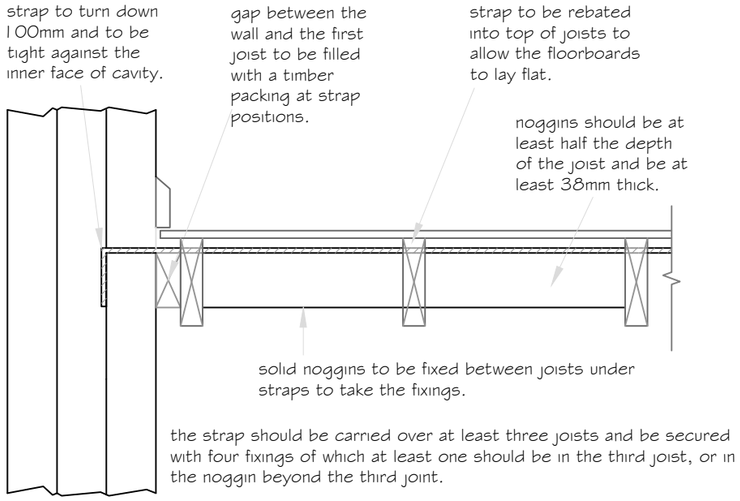


WALL RESTRAINT DETAIL WITH TIMBER FLOOR SPANNING PARALLEL

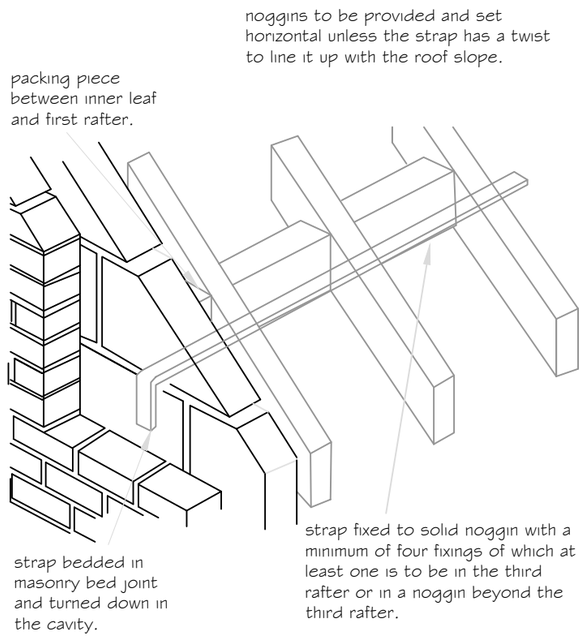


TYING OF PITCHED ROOFS TO GABLE WALLS

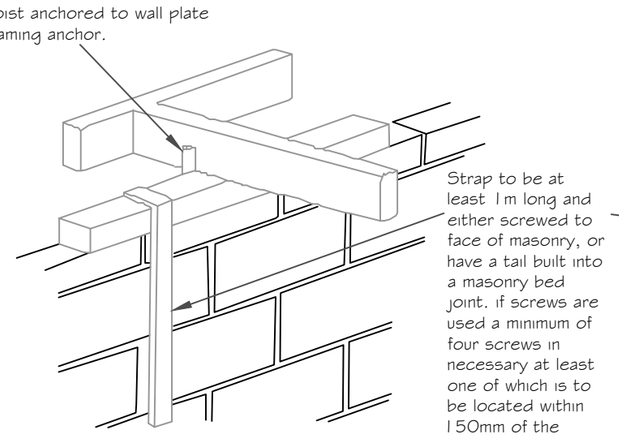

TYING OF TIMBER FLOOR BEARING ON TO WALL

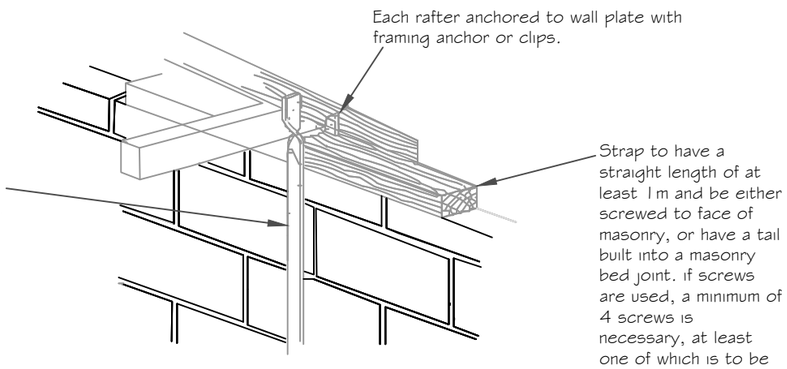

WALL RESTRAINT DETAIL WITH TIMBER FLOOR SPANNING PARALLEL

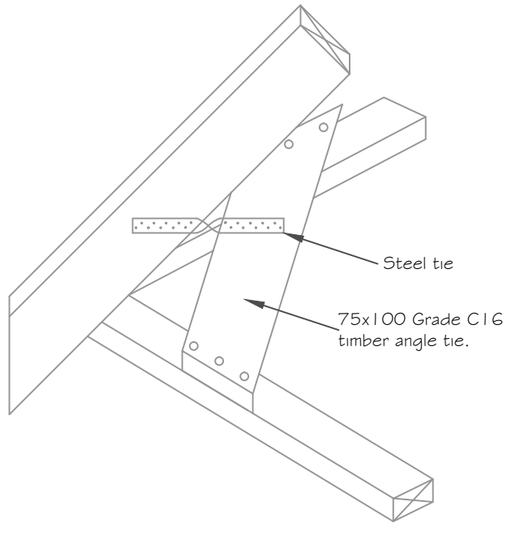

HIP RAFTER DRAGON TIE DETAIL

extension architecture

EXTENSION ARCHITECTURE & INTERIORS LTD
231 COBDEN HOUSE,
ROEHAMPTON LANE,
LONDON, SW15 4LB
TEL (0208) 288 8950
FAX (0871) 918 2798
www.extensionarchitecture.co.uk

THESE STRUCTURAL DRAWINGS HAVE BEEN PREPARED BY EXTENSION ARCHITECTURE WITH THE SOLE PURPOSE OF PROVIDING STRUCTURAL ENGINEERING SOLUTIONS. ANY QUESTIONS ABOUT STRUCTURAL COMPLIANCE SHOULD BE DIRECTED TO EXTENSION ARCHITECTURE OR THE LOCAL BUILDING CONTROL AUTHORITY. COLLABORATION WITH THE BUILDING CONTROL AUTHORITY FOR NECESSARY SITE INSPECTIONS AND APPROVALS IS COMPULSORY. WHILE THESE DRAWINGS ARE INTENDED FOR DISCUSSIONS WITH THE BUILDING CONTROL AUTHORITY, ON-SITE VERIFICATION BY THE BUILDER OR CONTRACTOR IS ESSENTIAL BEFORE CONSTRUCTION. THE BUILDER OR CONTRACTOR IS RESPONSIBLE FOR MAINTAINING RECORDS OF ANY DISCREPANCIES FOUND OR ON-SITE CHANGES THROUGHOUT CONSTRUCTION. CHARGES APPLY FOR EXTENSION ARCHITECTURE'S ON-SITE SUPERVISION, AND FEES APPLY FOR PROJECT MANAGER SERVICES IN CASE OF BUILDER ERRORS OR ISSUES. THE COPYRIGHT OF THE DRAWINGS AND DESIGNS REMAINS WITH EXTENSION ARCHITECTURE, REQUIRING EXPRESS WRITTEN PERMISSION FOR USAGE BEYOND THE APPLICATION.

DRAWN	CLIENT NAME: VIK BARODIA	DRAWING No.: A13
CHECKED	PROJECT NAME: 1 LAMBOURNE DRIVE	SCALE: NTS @A3
JOB NO.	TITLE: STRAPPING DETAILS	DATE: 31-07-2024
REVISION: F		